

LA PROPIEDAD COMPLETA, EN UNA MISMA VERSION

Plantas, fachadas, cortes y detalles extraidos del archivo Blender indicado en cada cartela. Las anotaciones distinguen fuente dimensional, geometria medida y propuestas pendientes.

Hoja	Contenido	Escala
A01	Implantacion, paisaje y perimetro	1:100 / 1:50
A02	Planta baja y vanos	1:50
A03	Planta alta, estudio y vivienda	1:50
A04	Cubiertas y coordinacion pluvial	1:50 / esquema
A05a / A05b	Cuatro fachadas	1:50
A06	Cortes generales A-A y B-B	1:50
A07	Escalera, descanso y acceso	1:20 / 1:5
A08	Pileta y bordes	1:25
A09	Banos: plantas y elevaciones	1:20
A10	Quincho y cocinas	1:25
A11	Estudio y tratamiento acustico	1:25 / 1:50
A12	Carpinterias y herreria	Cuadros / 1:25
A13 / A13b	Encuentros de envolvente	1:5 / 1:10
A14	Estructura conceptual	1:50 / 1:10
A15	Instalaciones coordinadas	1:100 / esquemas
A16	Superficies, decisiones y trazabilidad	Cuadros



COMO LEER ESTE JUEGO

- F - Fuente: cotas expresas del HTML original y decisiones del propietario.
- G - Geometria: medida derivada de la version Blender identificada por SHA256. No equivale a un relevamiento de obra.
- P - Propuesta: coordinacion o solucion grafica inferida. Validar antes de construir.
- Niveles referidos al cero del modelo. No hay relevamiento altimetrico ni mensura catastral.
- Ubicacion declarada: Virrey del Pino, Buenos Aires. Norte orientativo segun propietario: con la calle arriba, abajo a la izquierda.
- Servicios de red disponibles segun propietario. Posiciones, cotas y condiciones exactas de acometida pendientes.
- Escalas fisicas para impresion al 100 %. DXF en metros; cada vista se separa horizontalmente en espacio modelo.

JERARQUIA GRAFICA

- 0,50 mm: contorno de piezas cortadas. Relleno gris: material seccionado.
- 0,18 / 0,13 mm: proyecciones, mobiliario y contexto.
- Azul: cotas, niveles, referencias y criterios de coordinacion.
- No constituye proyecto ejecutivo ni calculo estructural, sanitario, electrico o acustico.


01 Implantacion general | 1:100

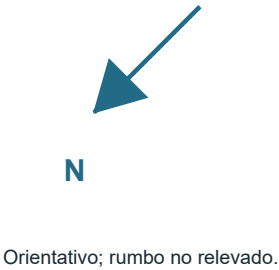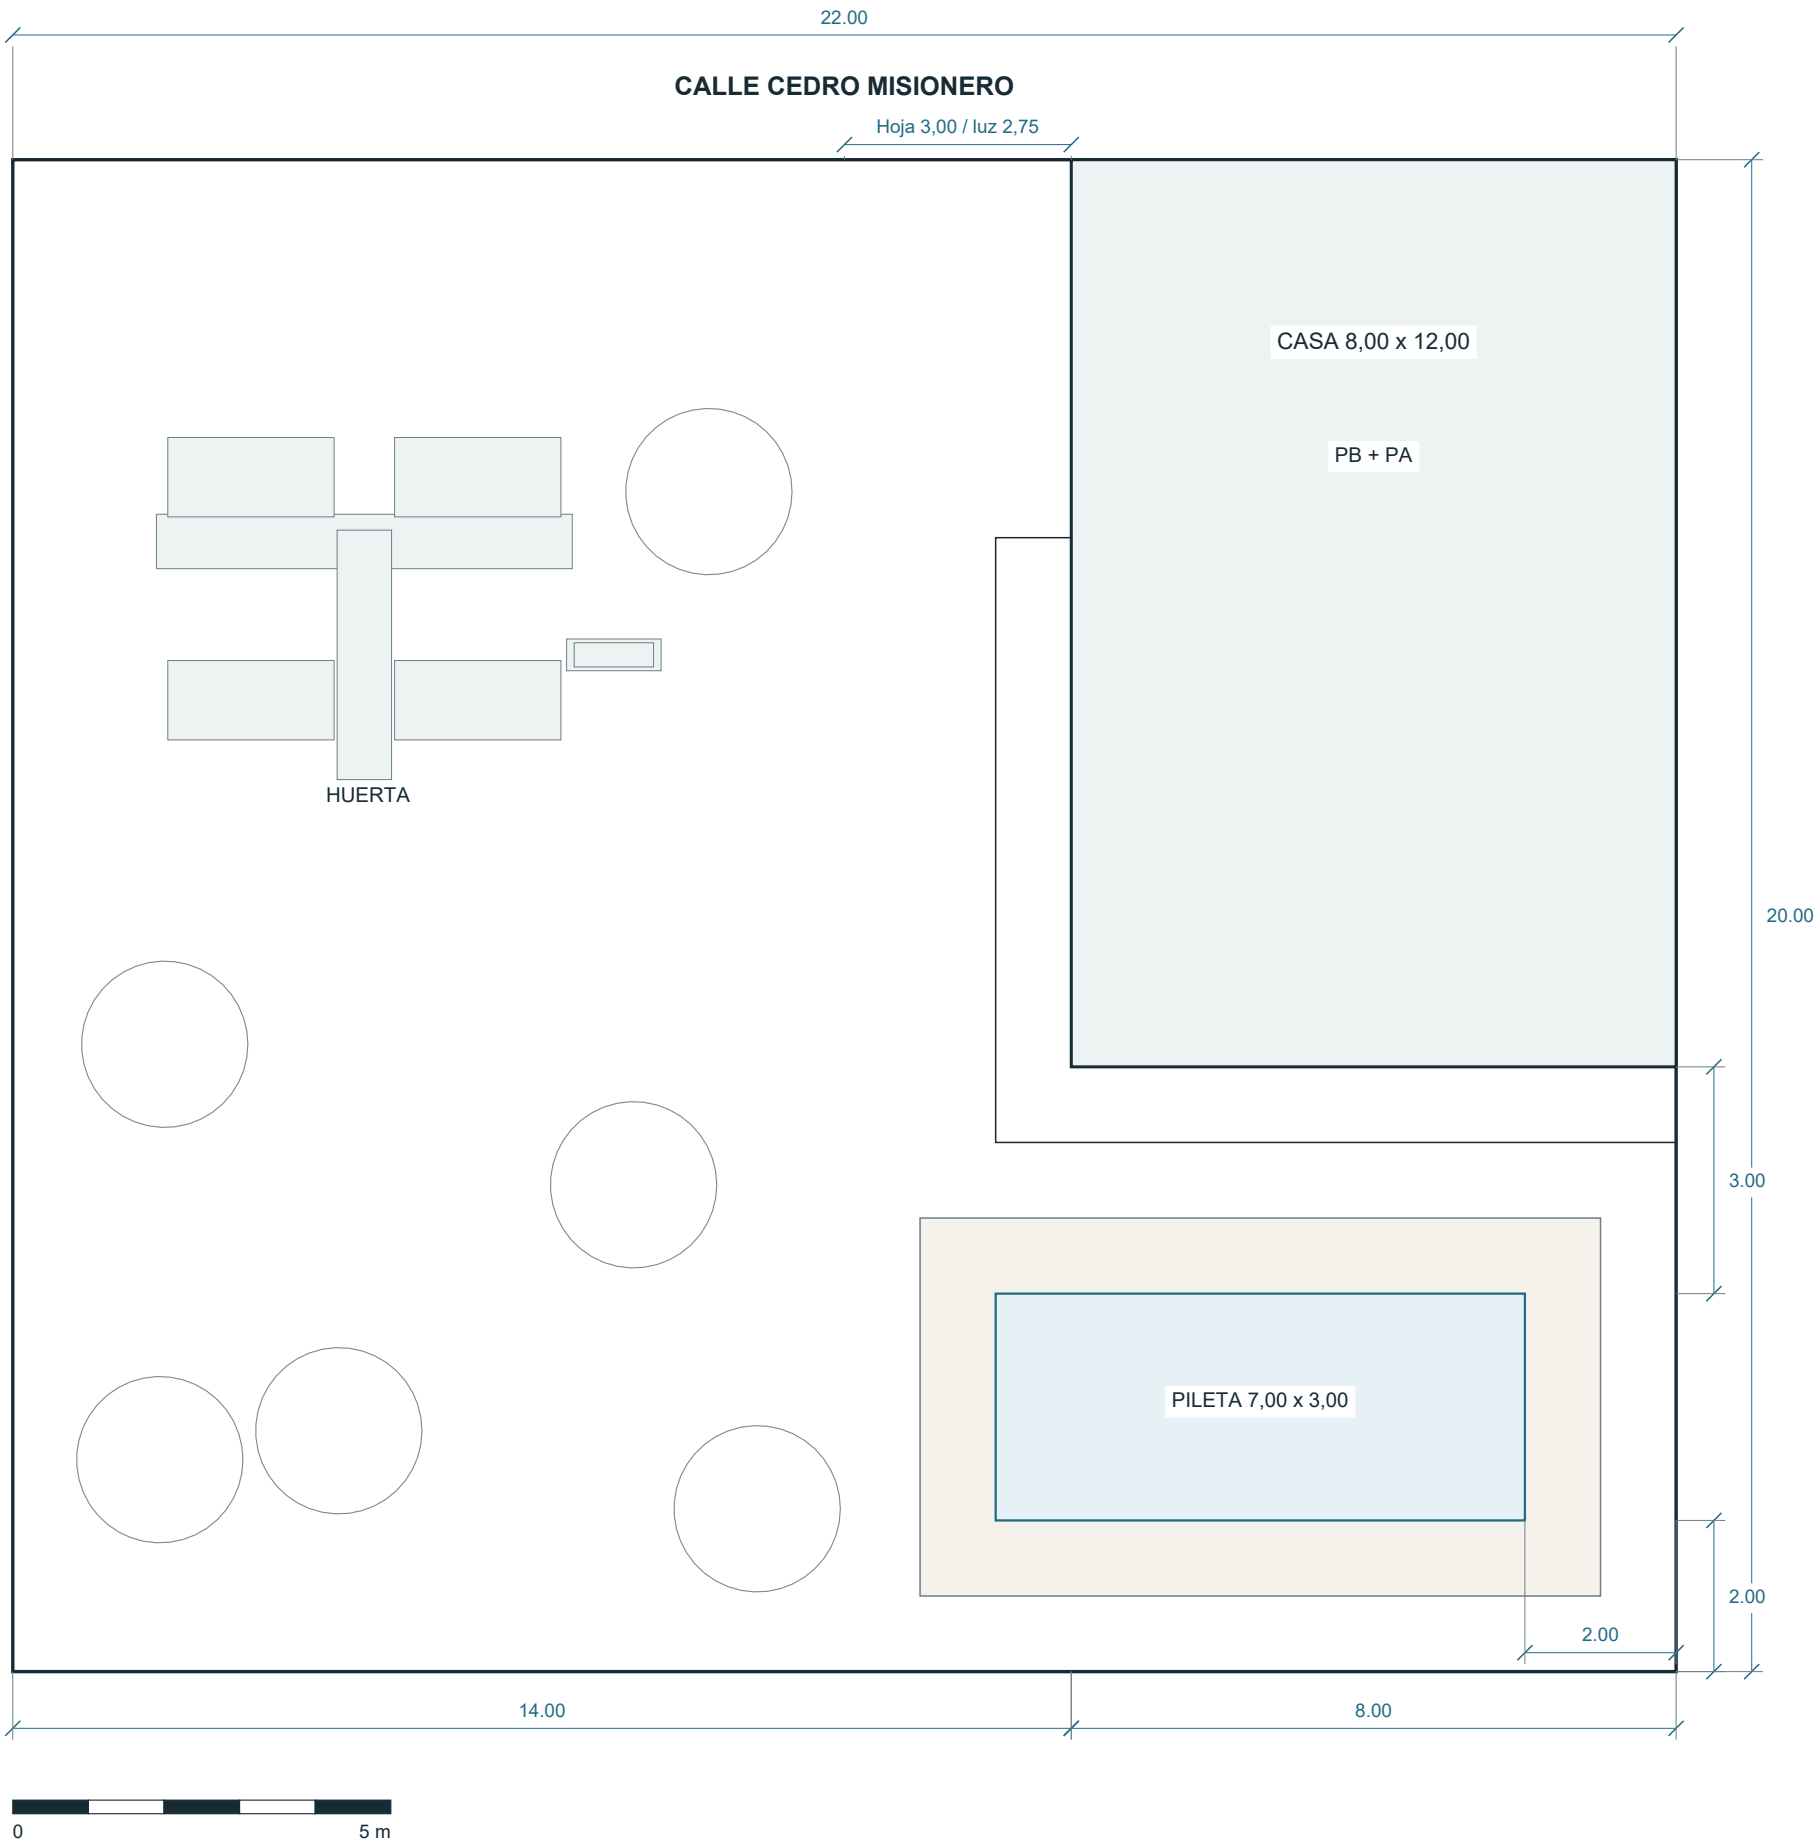

IMPLANTACION CONSERVADA


- F: lote nominal 22,00 x 20,00 m. Casa X=14,00; Z=0,00. Dos modulos de 6,00 m.
- F: pileta X=13,00; Z=15,00. Distancias nominales del vaso: 2,00 m al fondo y 2,00 m al lateral derecho.
- F: borde pavimentado de 1,00 m; huerta y centros de los seis arboles de fuente conservados.
- G: cotas de pavimentos se detallan en A02, A07 y A08. Rasante general del terreno por relevar.
- G: porton de hoja 3,00 m, luz entre pilares 2,75 m y carrera 3,05 m. No confundir hoja con paso libre.

02 Huerta y caminos | 1:50

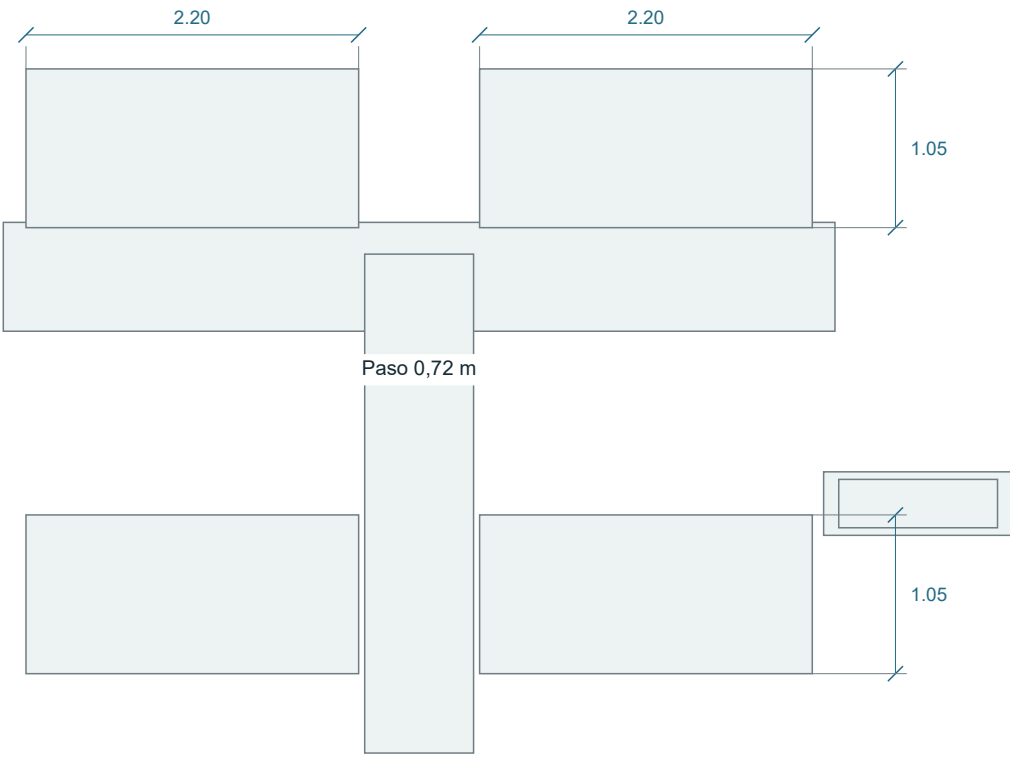

Perimetro y desniveles: confirmar mensura, cotas de terreno y drenajes exteriores. El norte grafico refleja la referencia del propietario y no un azimut topografico.

01 Planta baja amoblada | 1:50

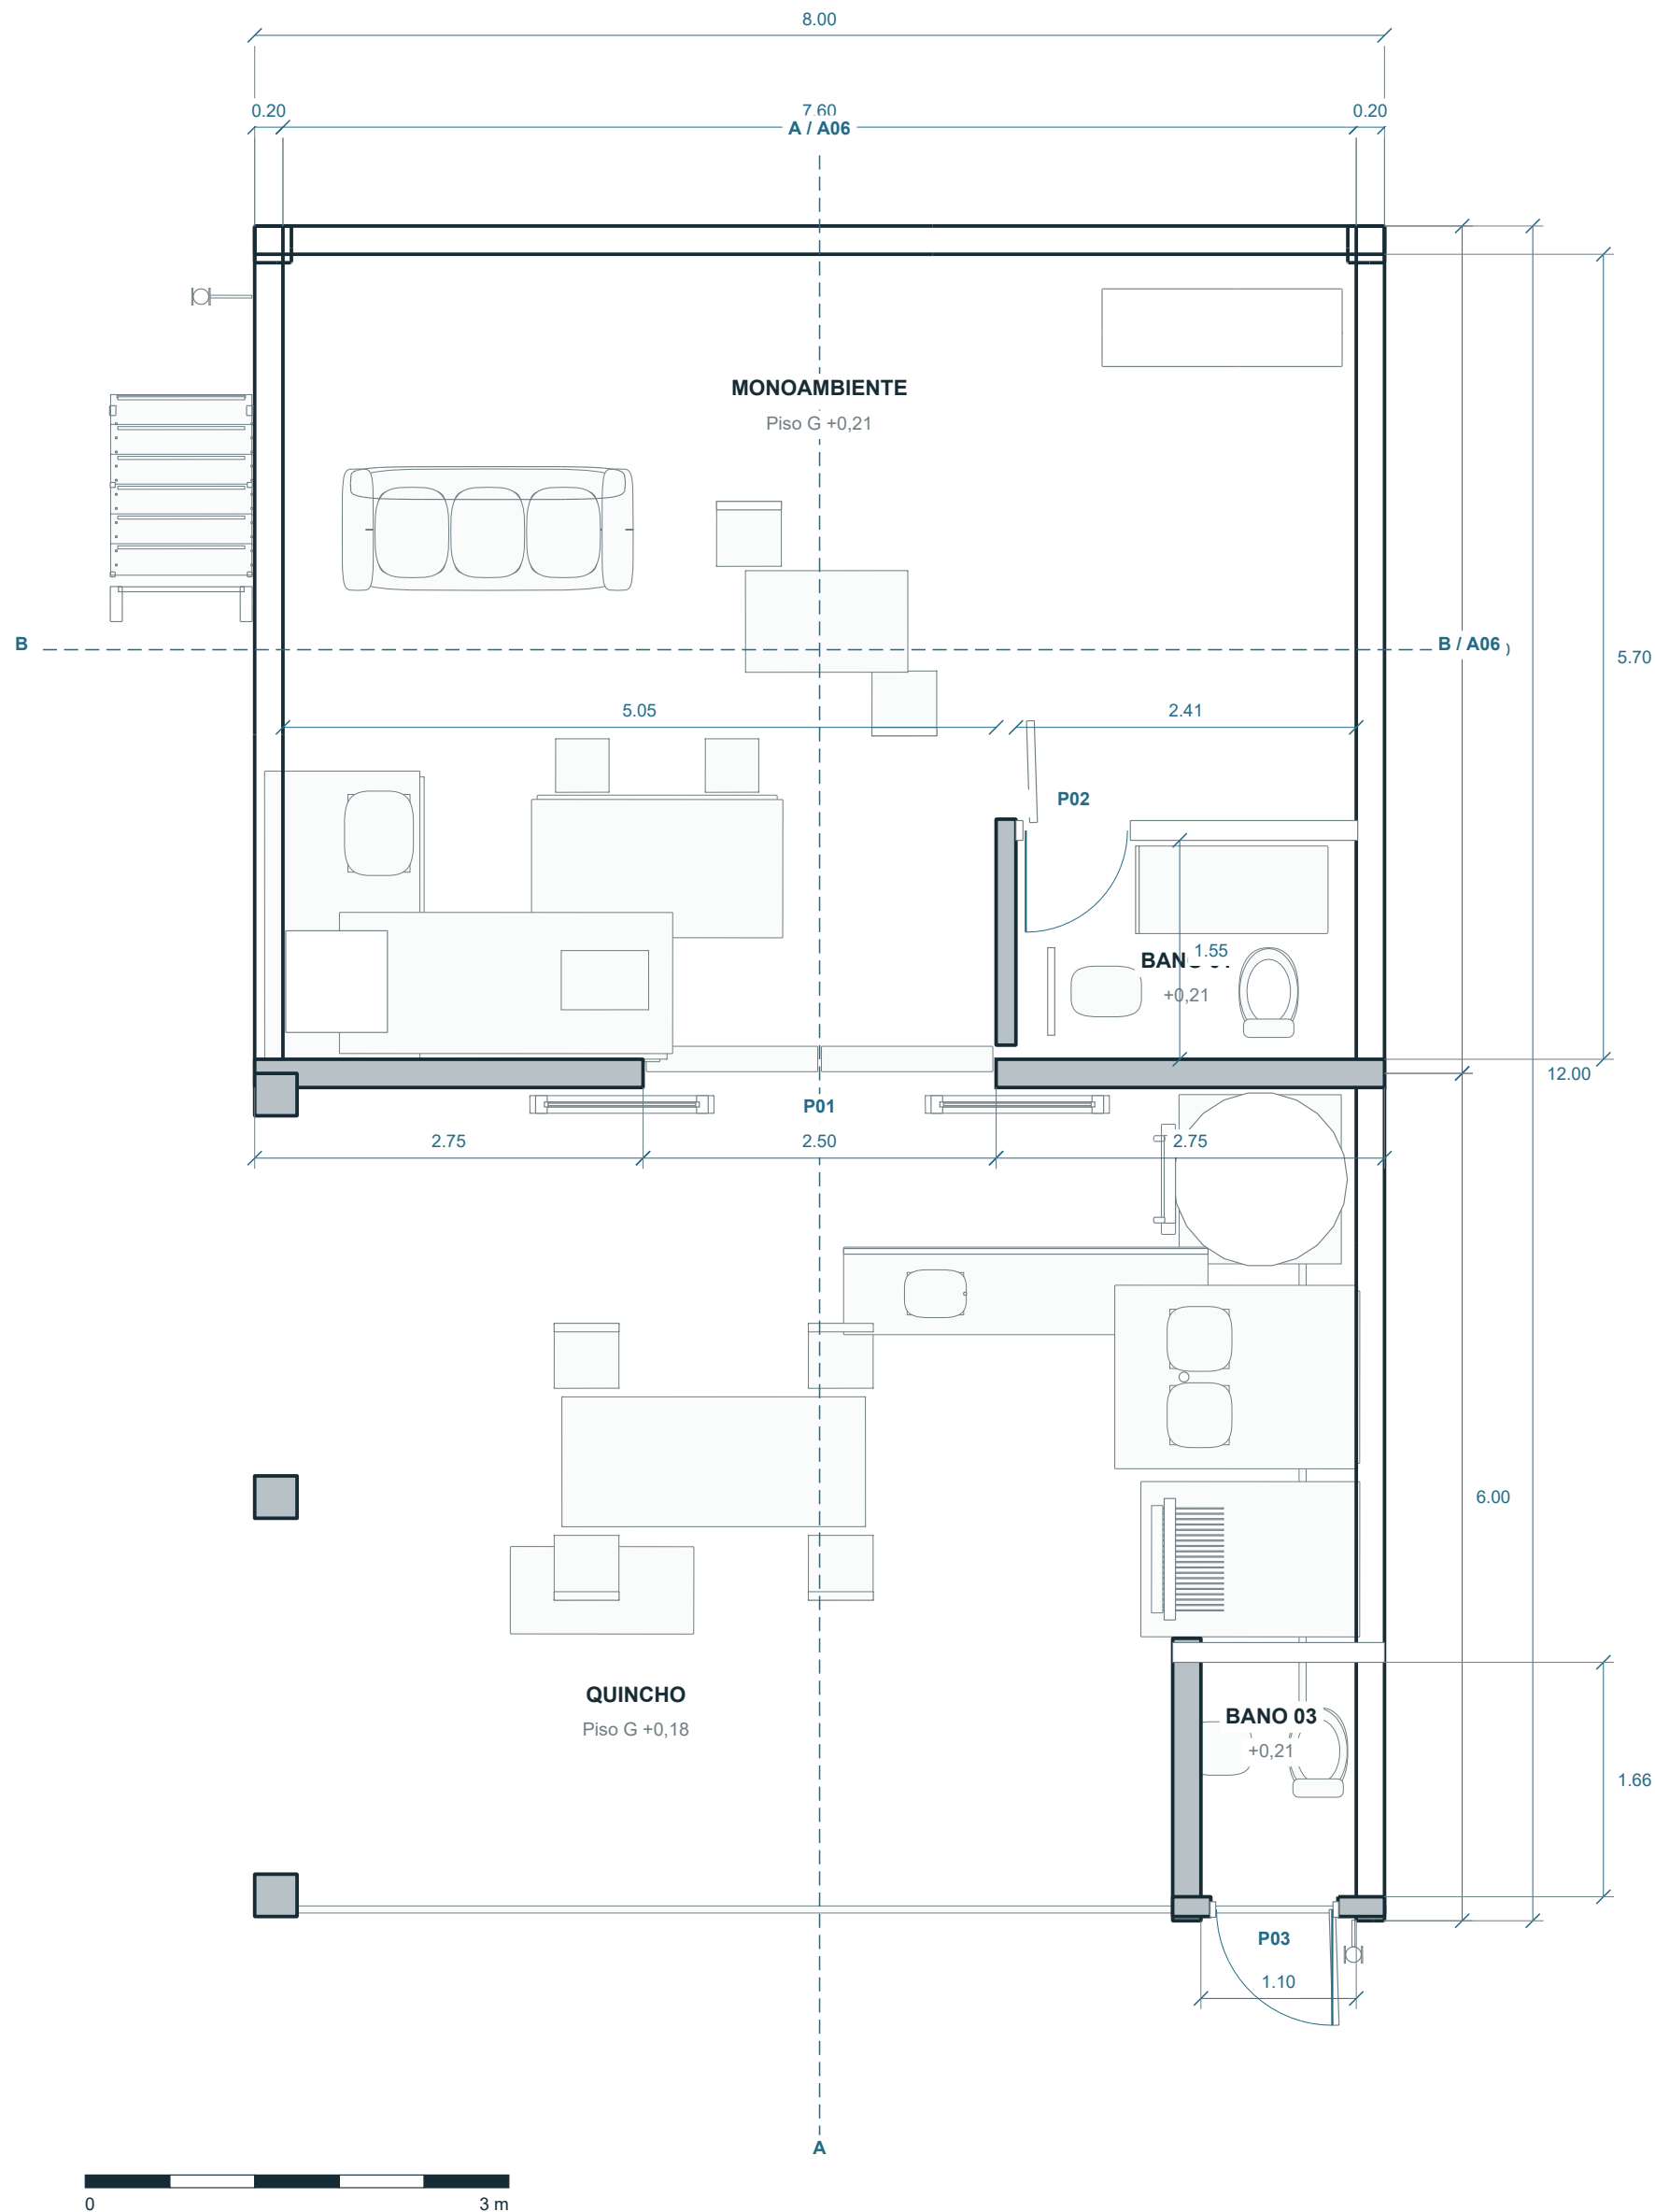

DIMENSIONES Y NIVELES


- F: envoltente nominal 8,00 x 12,00 m; espesor exterior 0,20 m. La geometría de piezas puede incluir juntas y salientes.
- G: piso monoambiente +0,21; quincho +0,18; ambos banos PB +0,21. Saltos entre acabados visibles: no se omiten.
- G: vano doble monoambiente 2,50 m entre jambas. Las hojas y rieles se describen en A12.
- G: tabique bano mono 0,14 m. Ancho interior entre pared lateral y medianera aprox. 2,41 m; verificar acabados.
- G: bano de pileta exterior con acceso desde jardin. Detalle acotado en A09.
- Barridos azules: pose de apertura esquematica de hojas; la ausencia de colision se audita en el modelo y no se presume por este simbolo.

LECTURA DE LOS EQUIPOS

- Cocina en L e isla del monoambiente: plantas y alturas de mesada en A10.
- Quincho: horno, bacha y parrilla mantienen la linea de fuente; extracciones independientes hacia patinillo. Ver A10 y A15.
- La circulacion y los usos se muestran con el mobiliario actual. No se certifican accesibilidad ni condiciones reglamentarias locales.

Ref.	Ambito	Consultar
P01	Corredera PB	A12 carpinterias
P02 / P03	Banos PB / pileta	A09 locales
A-A / B-B	Secciones reales	A06 cortes generales

01 Planta alta amoblada | 1:50

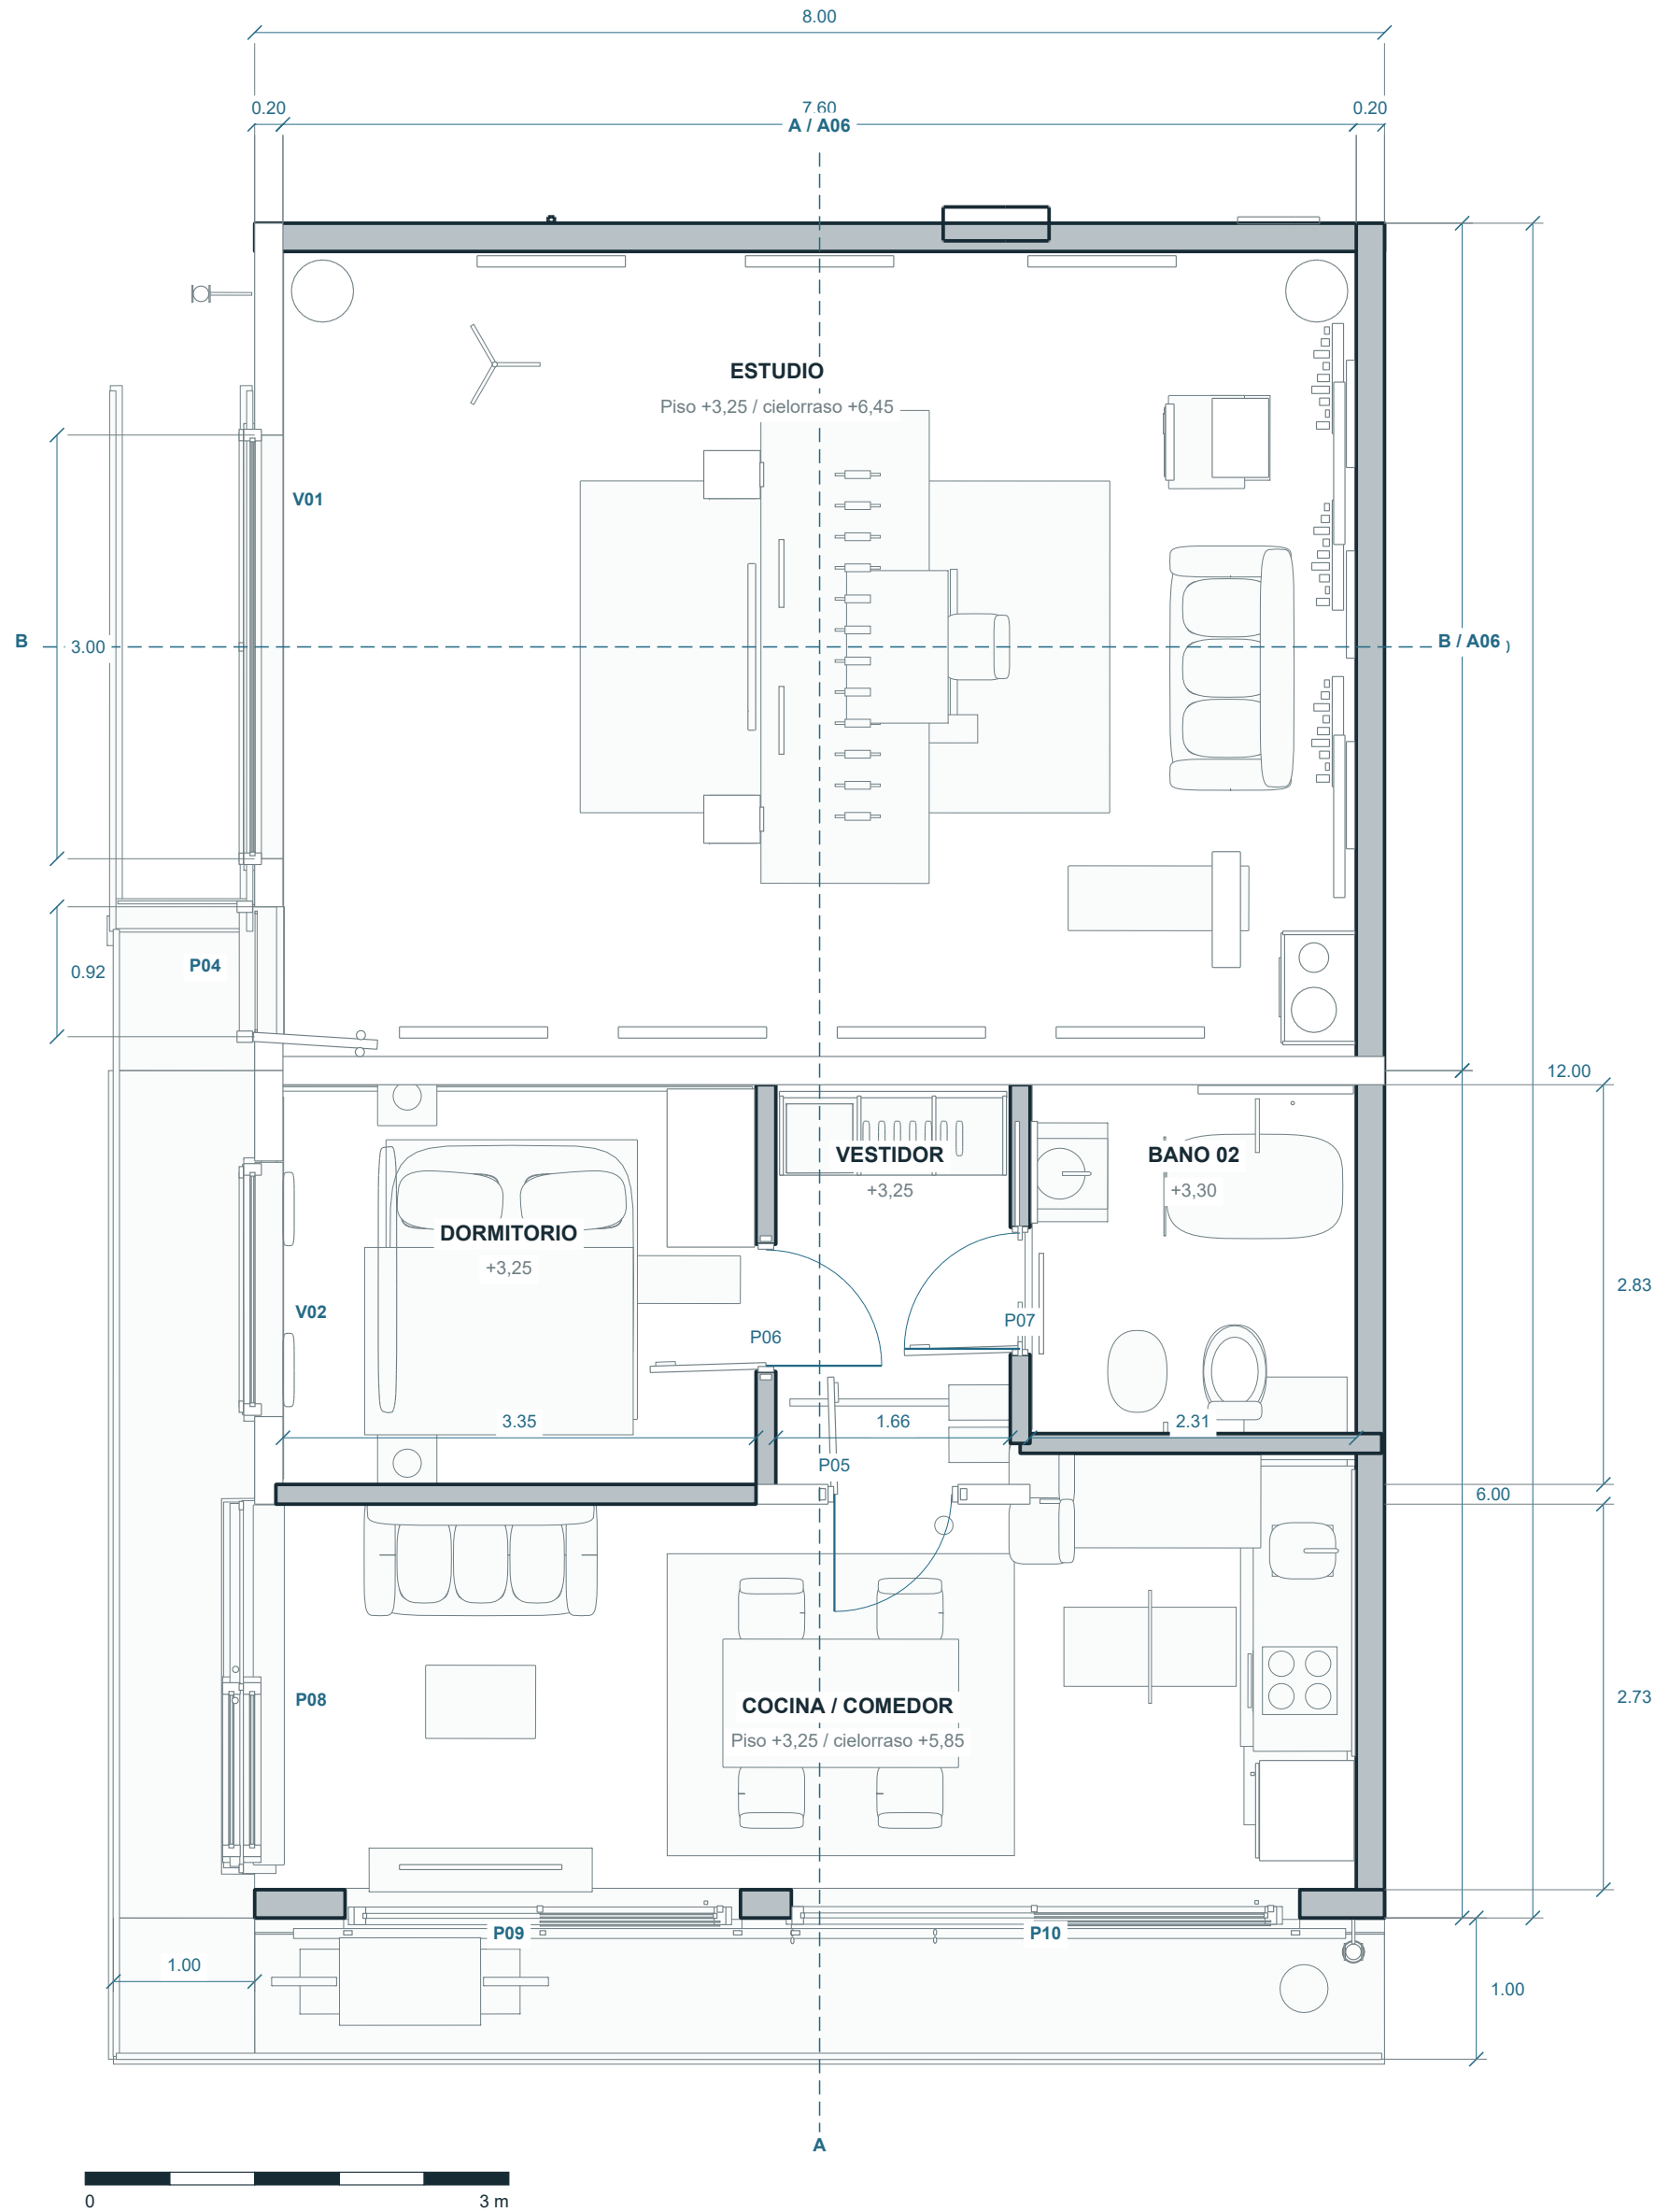

ALTURAS AUTORIZADAS

F/G: piso estudio +3,25; cara inferior del cielorraso +6,45 = 3,20 m libres.

F/G: piso vivienda +3,25; cielorraso general +5,85 = 2,60 m libres.

G: piso bano +3,30; cielorraso bano +5,90 = 2,60 m libres. El escalon local de 50 mm requiere detalle de impermeabilizacion.

G: losa entre plantas +3,00 a +3,20; espesor 0,20 m. Acabado general superior 0,05 m.

F: acceso exterior unico al nivel alto. Escalera y descanso 1,00 m nominal; detalle del umbral en A07.

CERRAMIENTOS Y VANOS


F: ventana del estudio 3,00 m. G: paños DVH y marco segun cuadro A12.

G: dormitorio, vestidor y bano con puertas operables; cadenas interiores miden entre caras de tabiques del modelo.

G: balcon lateral 1,00 m y posterior 1,00 m nominal. Barandas y borde de losa en A12/A13.

La composicion acustica, ventilacion silenciosa, ruido de instalaciones y sellado se coordinan en A11; prestaciones aun no calculadas.

01 Cubiertas y captacion | 1:50

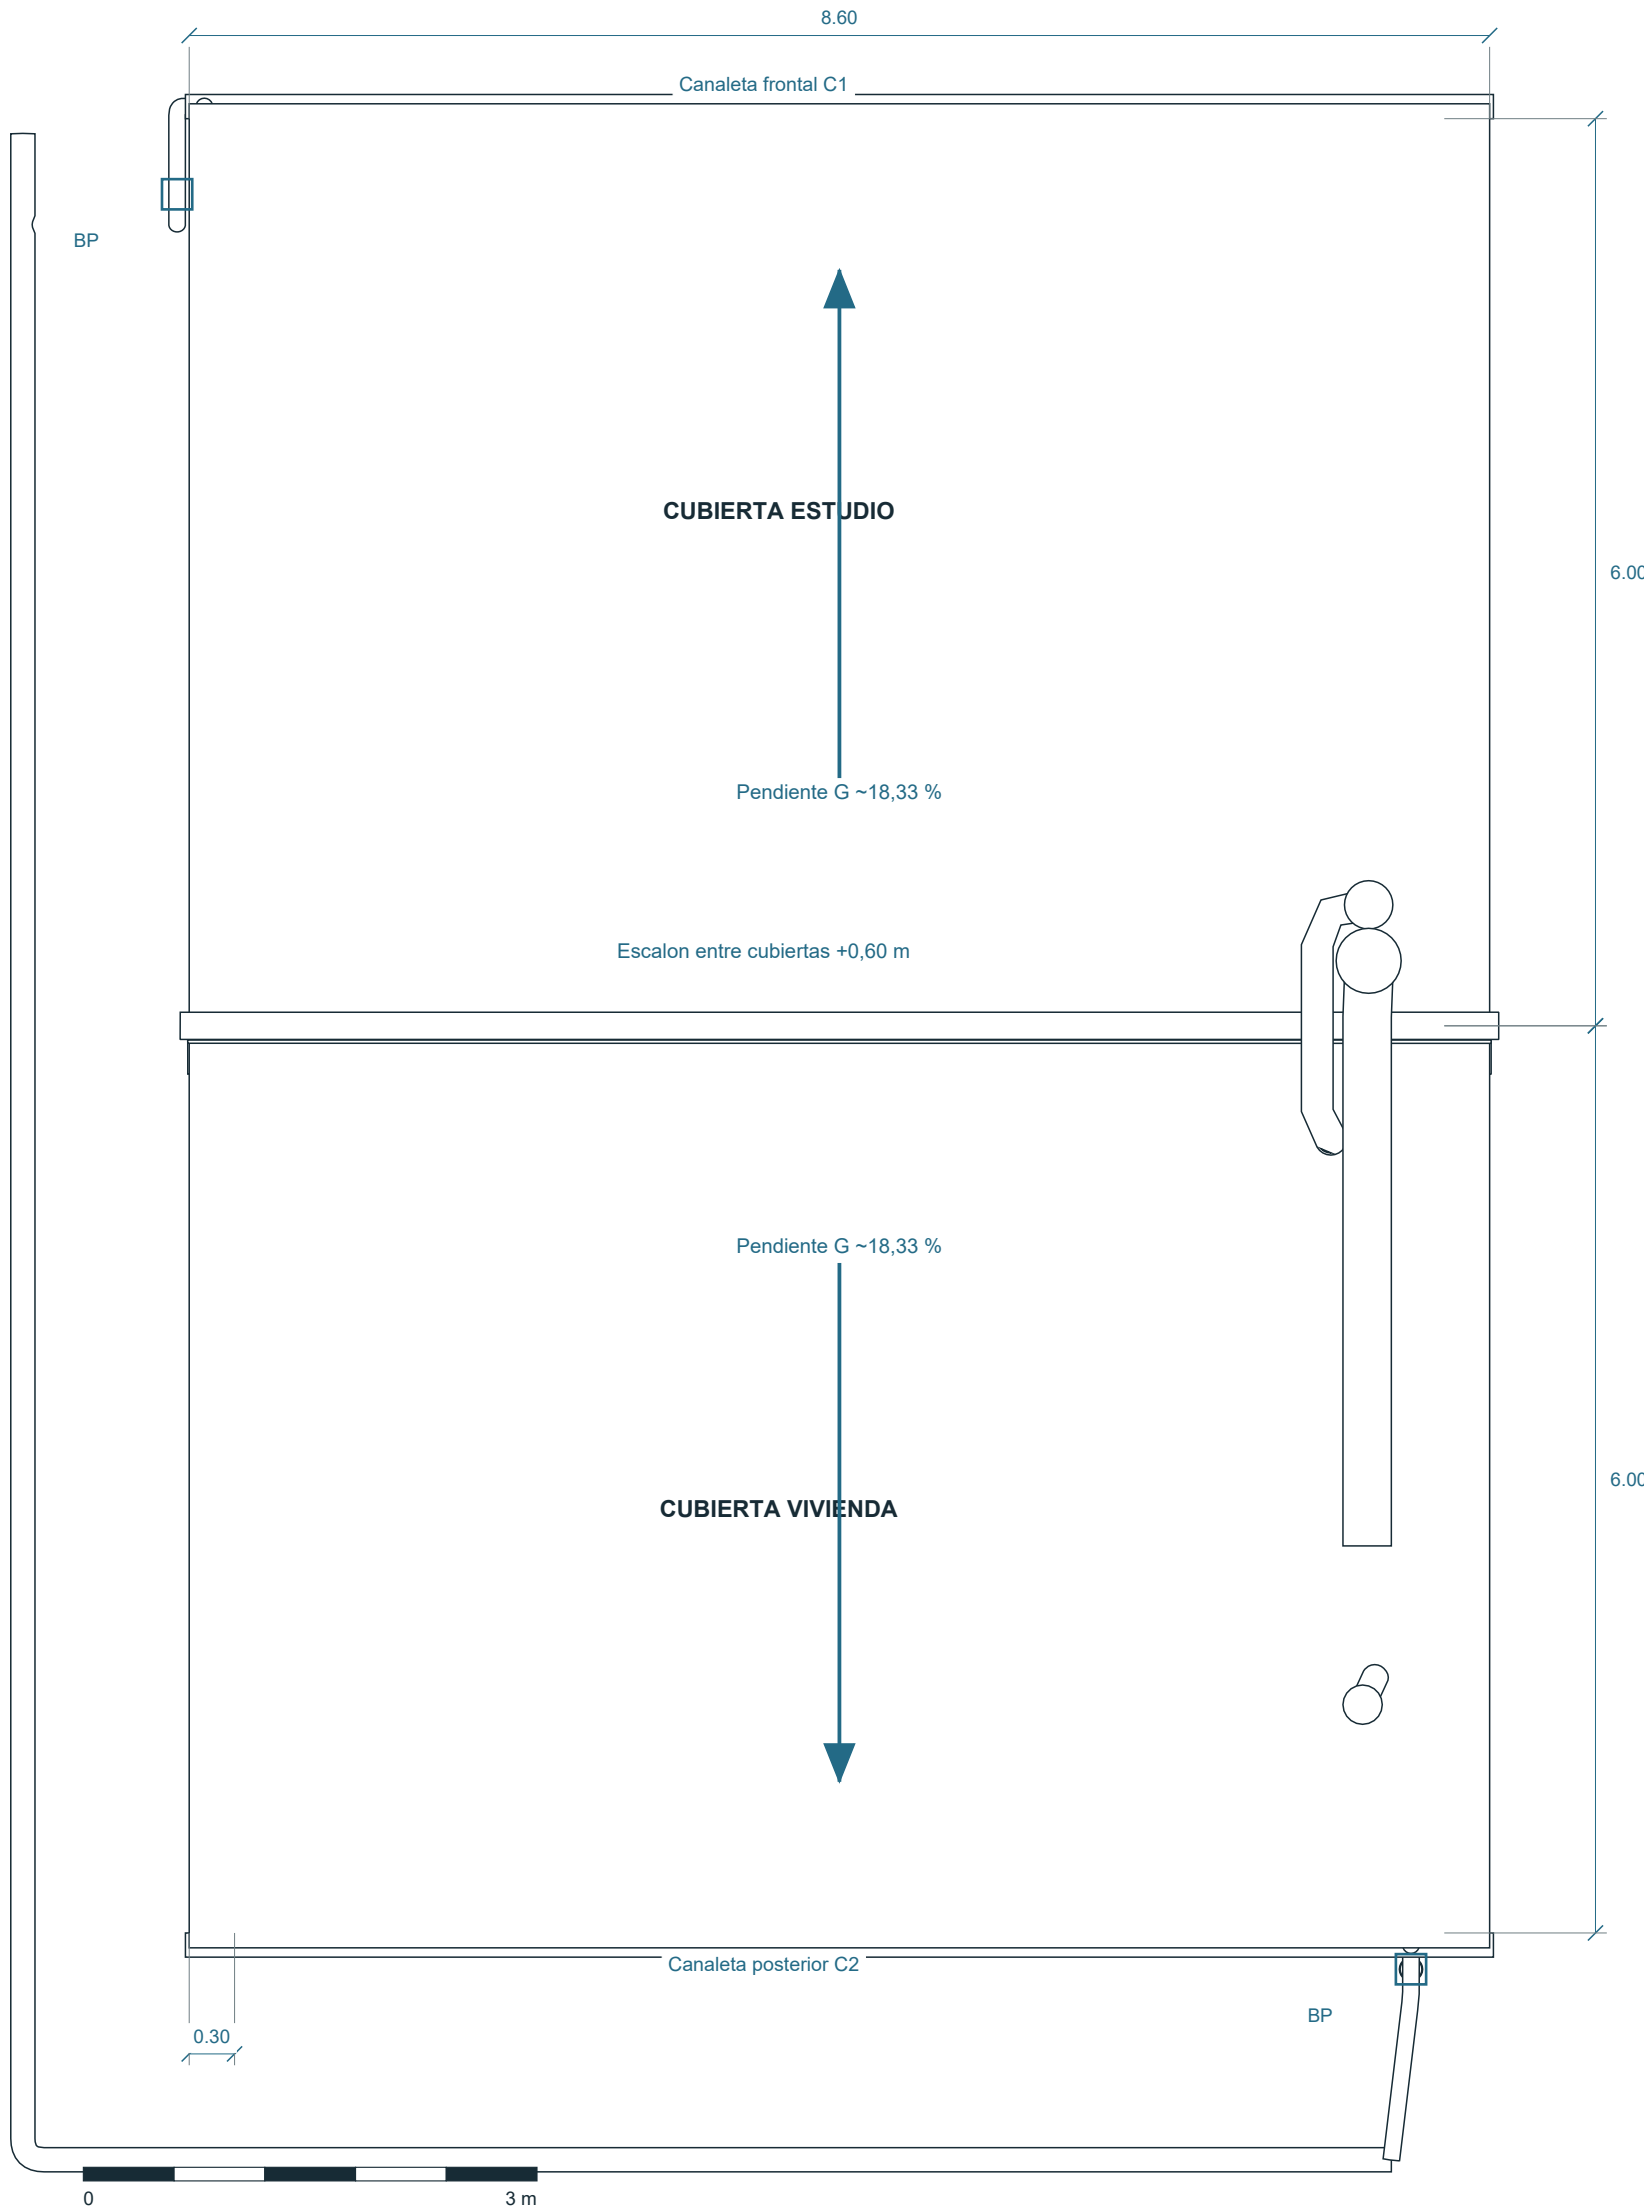

CONTINUIDAD DEL AGUA

G: pendientes principales conservadas, 1,10 m de subida en 6,00 m de desarrollo horizontal nominal (18,33 %). No es una pendiente pluvial de canería.


G: estudio elevado 0,60 m respecto de la cubierta de vivienda. Alero lateral nominal 0,30 m.

Captacion: revisar seccion abierta, embudo, codo y abrazaderas en el modelo de esta emision. El corte de abajo reproduce sus piezas reales.

P: conduccion de descarga hasta punto de red pluvial propuesto. Conexion, cota, caudal y diametros finales pendientes de datos de servicio y calculo.

No se presume que una bajada dibujada llega a una red existente. A15 identifica el limite de coordinacion.

02 Circuito frontal / proyeccion | 1:50

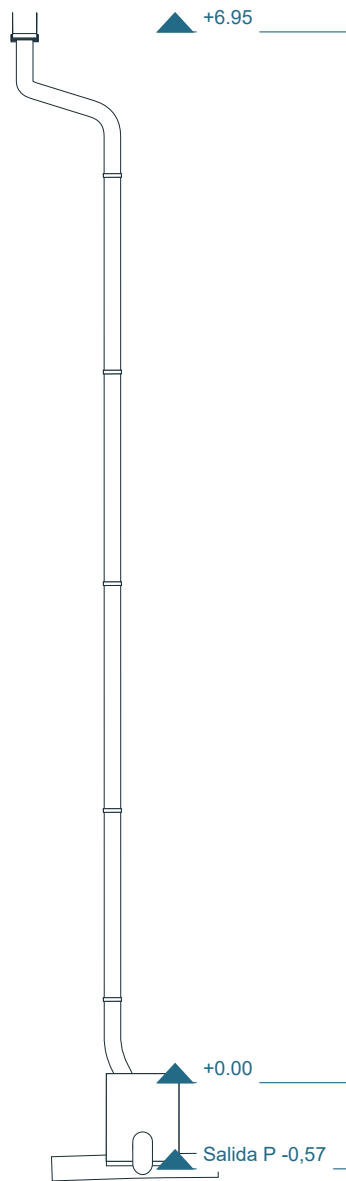


PUNTOS DE CONTROL

1. Cubierta hacia canaleta receptora.
2. Fondo de canaleta hacia salida.
3. Conexion estancia entre piezas.
4. Bajada continua y registrable.
5. Descarga con destino definido.

La continuidad física y la prueba de paso se documentan en la auditoria del modelo.

01 Frente / Cedro Misionero | 1:50

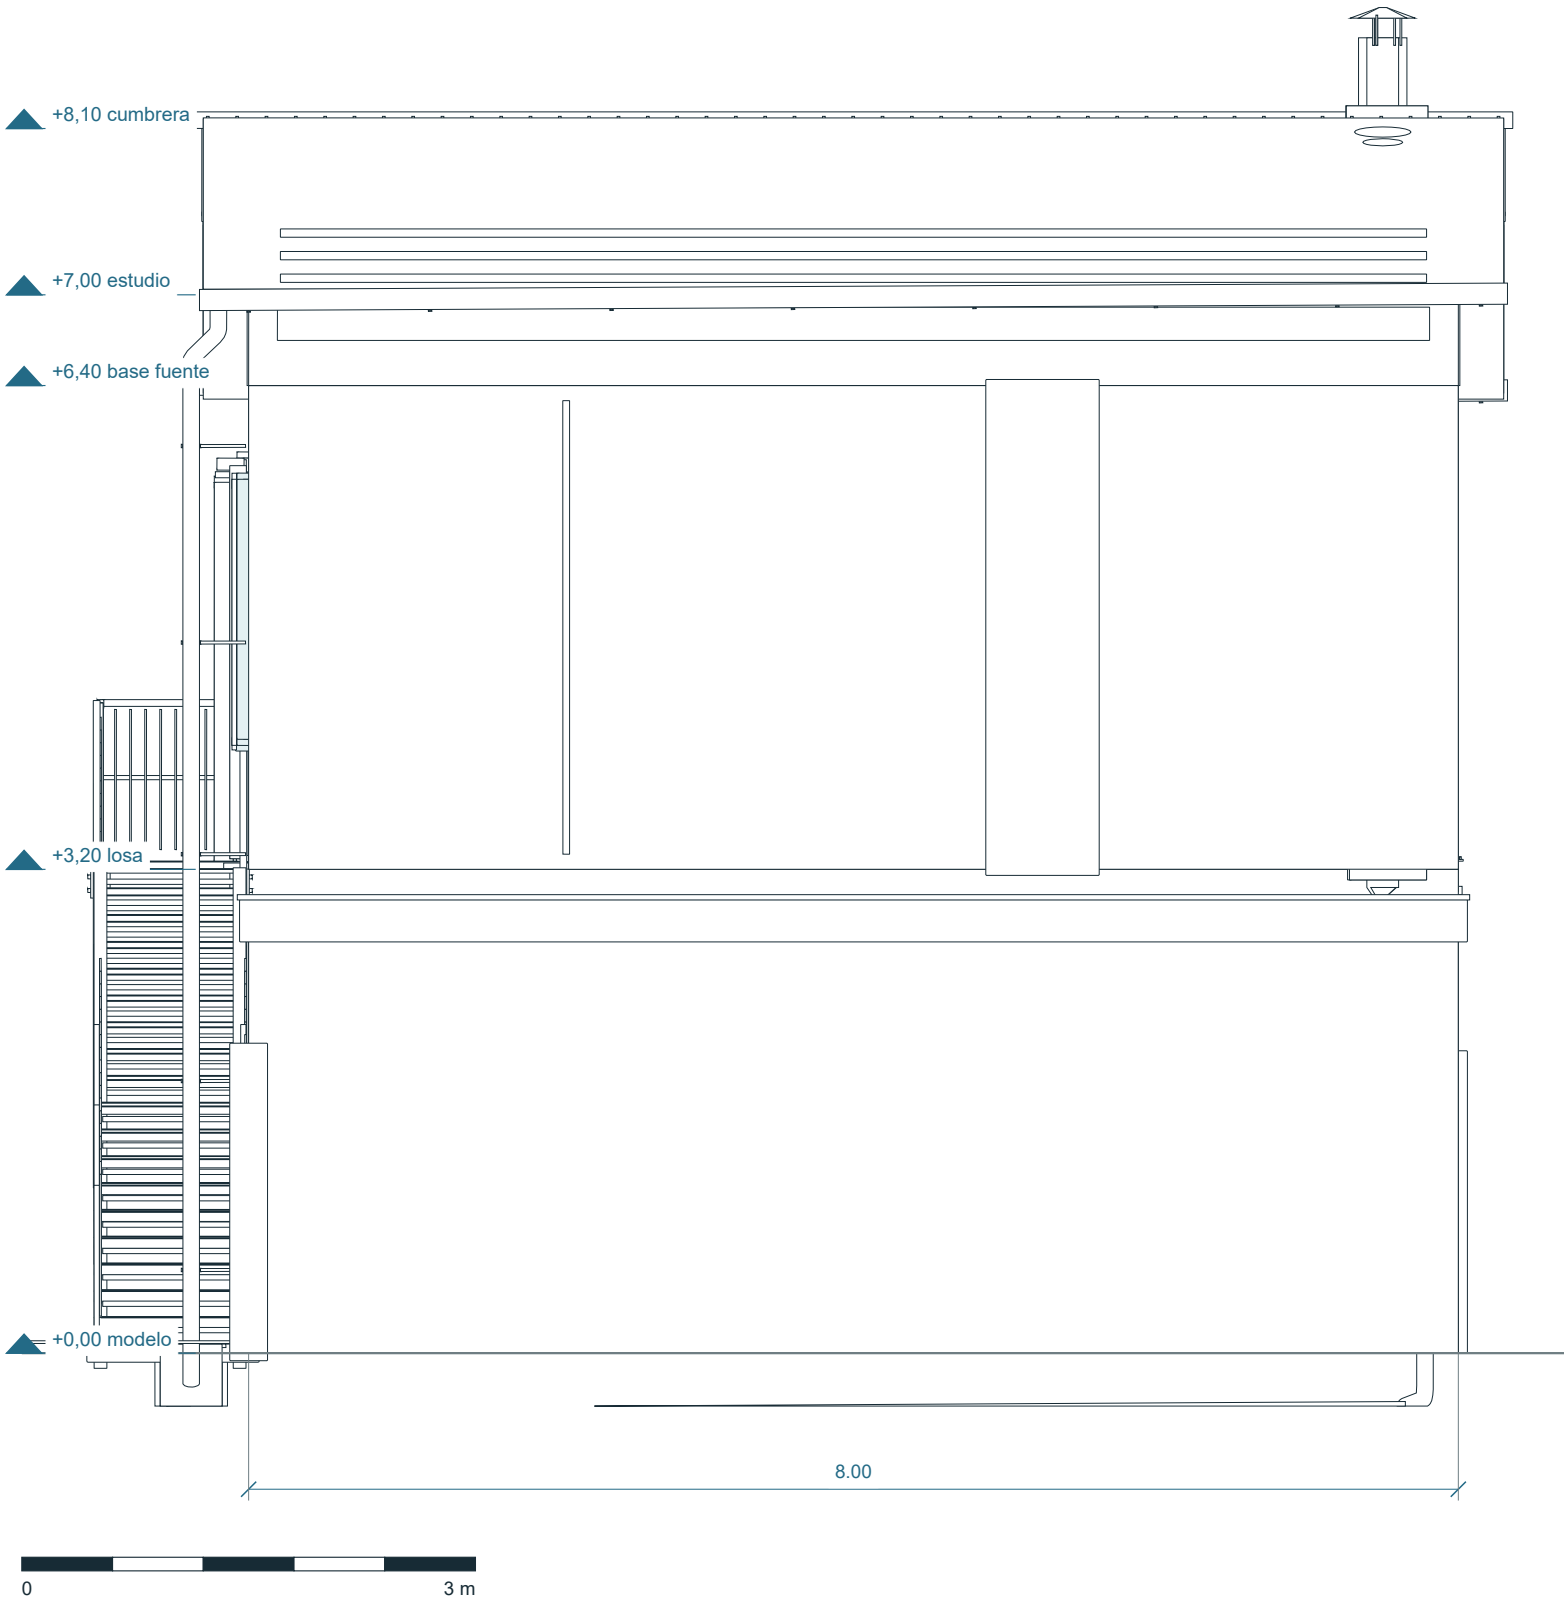

MATERIALIDAD REPRESENTADA


Ladrillo visto en cerramientos; hormigon en losas, pilares y vigas; cubierta metalica con encuentros y remates; DVH en carpinterias; herreria en balcones y escalera.

Los contornos son proyecciones simplificadas de las mallas evaluadas. Los detalles de hojas, capas y fijaciones se leen en A12 y A13; no representan un despiece de fabricacion.

02 Contrafrente / pileta | 1:50



03 Lateral de acceso | 1:50

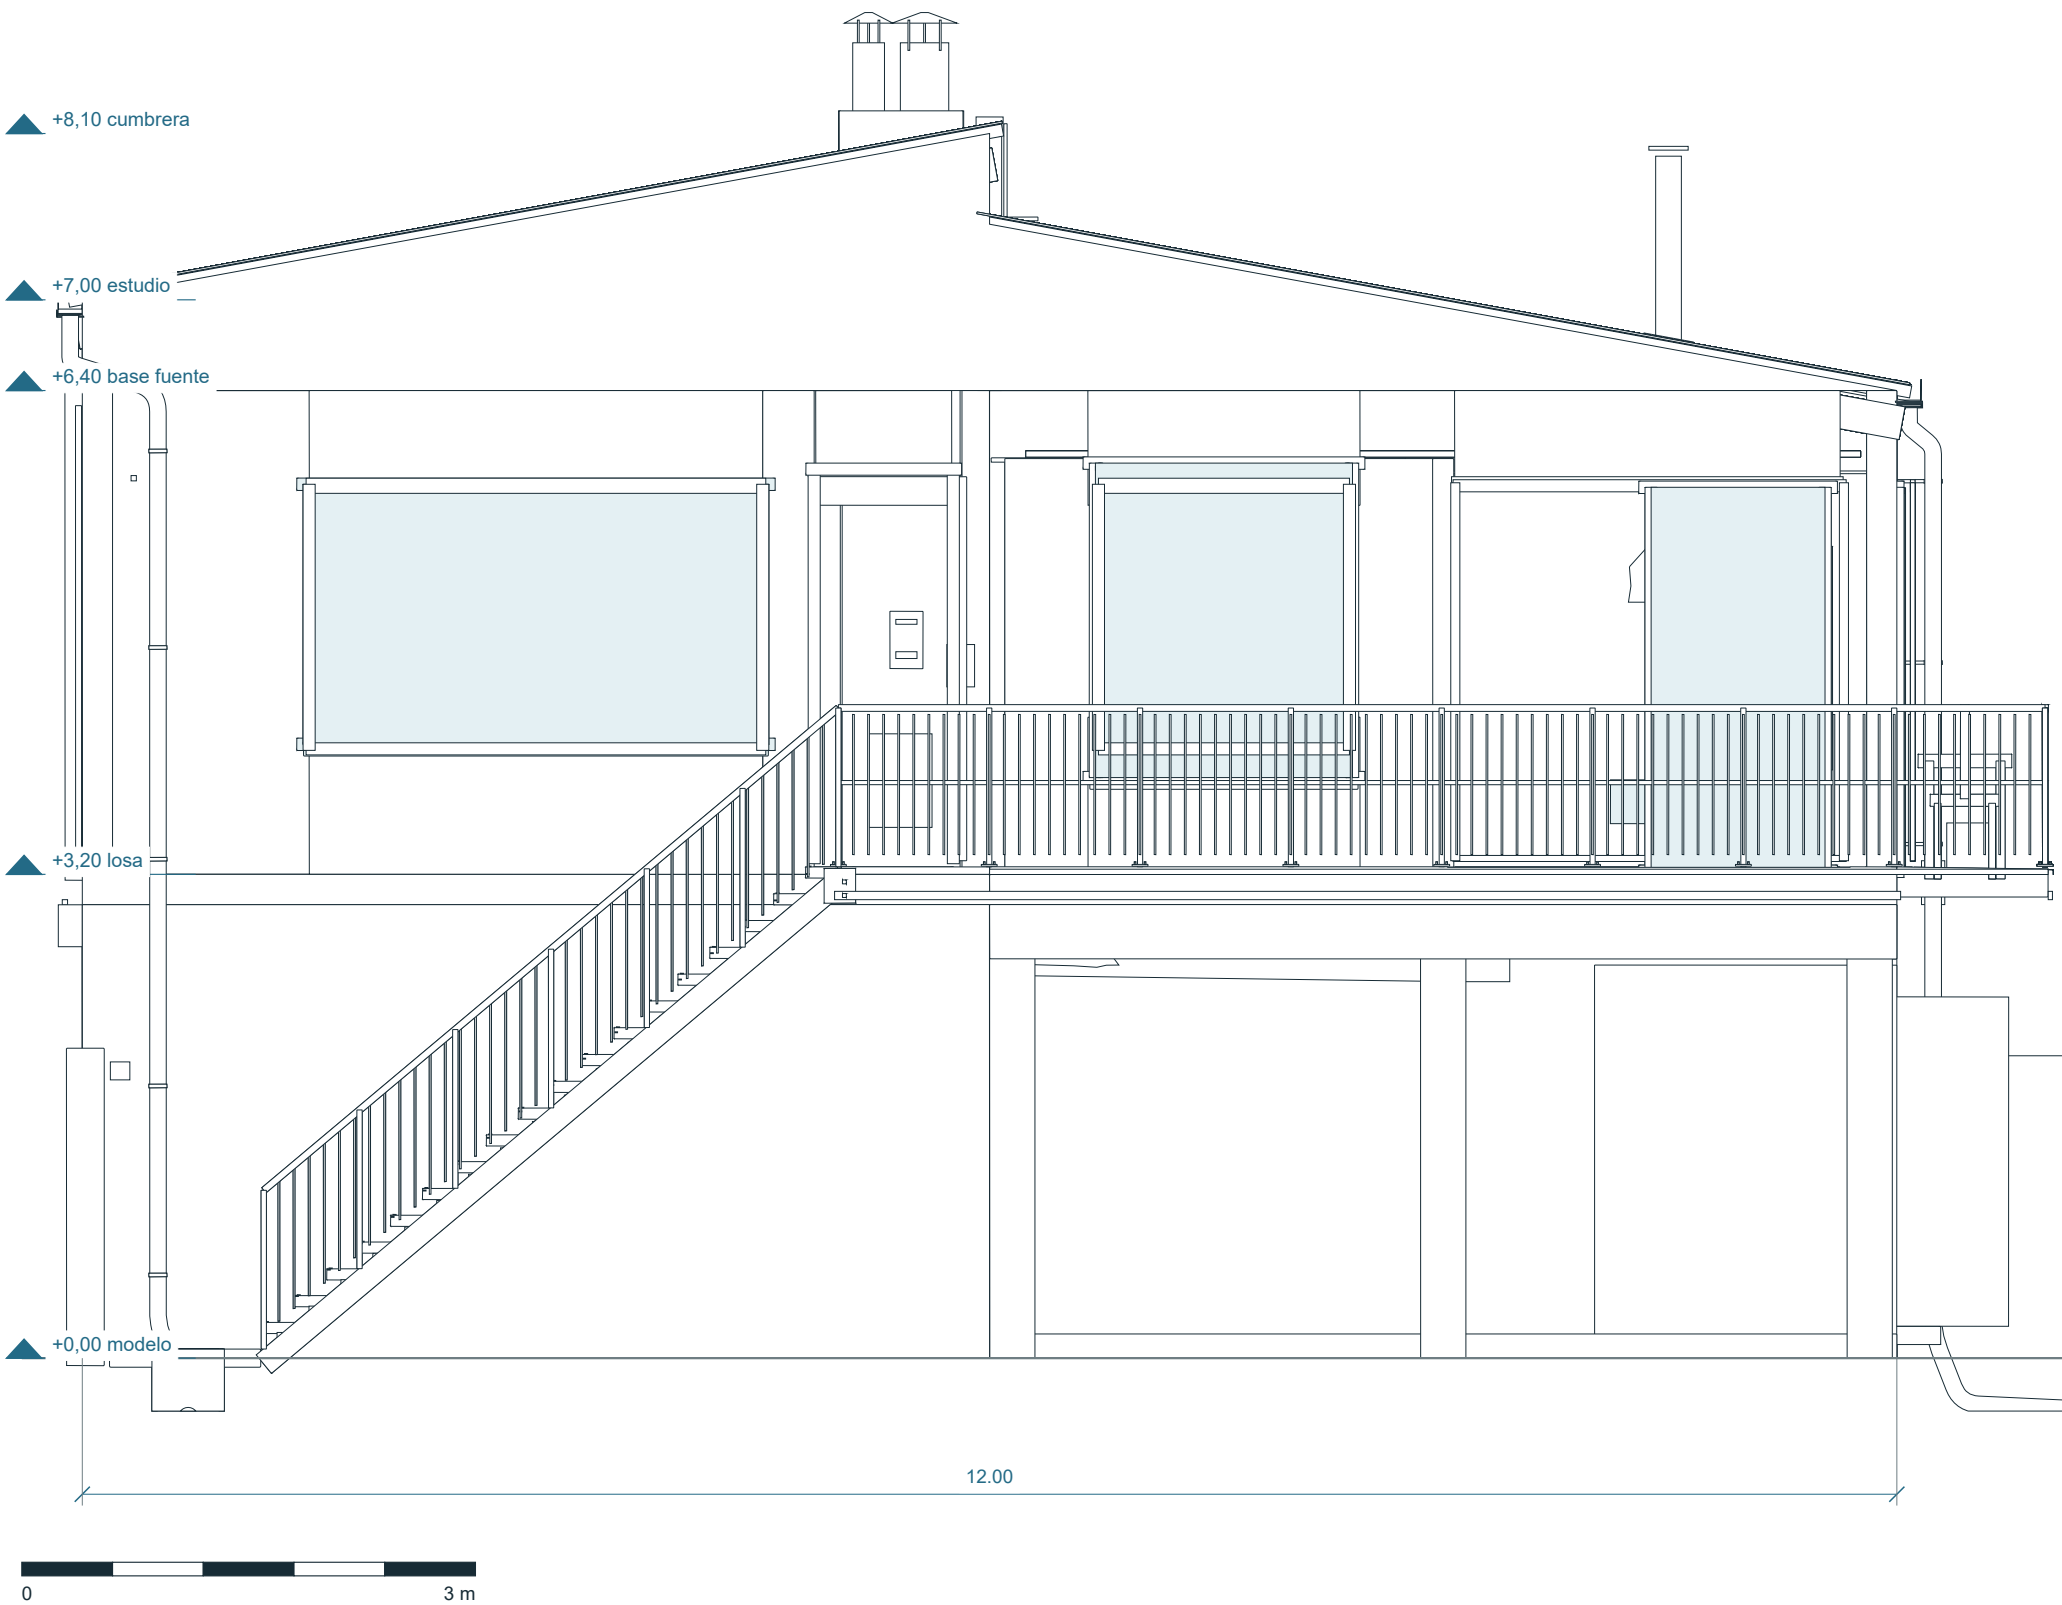


MATERIALIDAD REPRESENTADA


Ladrillo visto en cerramientos; hormigon en losas, pilares y vigas; cubierta metalica con encuentros y remates; DVH en carpinterias; herreria en balcones y escalera.

Los contornos son proyecciones simplificadas de las mallas evaluadas. Los detalles de hojas, capas y fijaciones se leen en A12 y A13; no representan un despiece de fabricacion.


04 Medianera lateral | 1:50

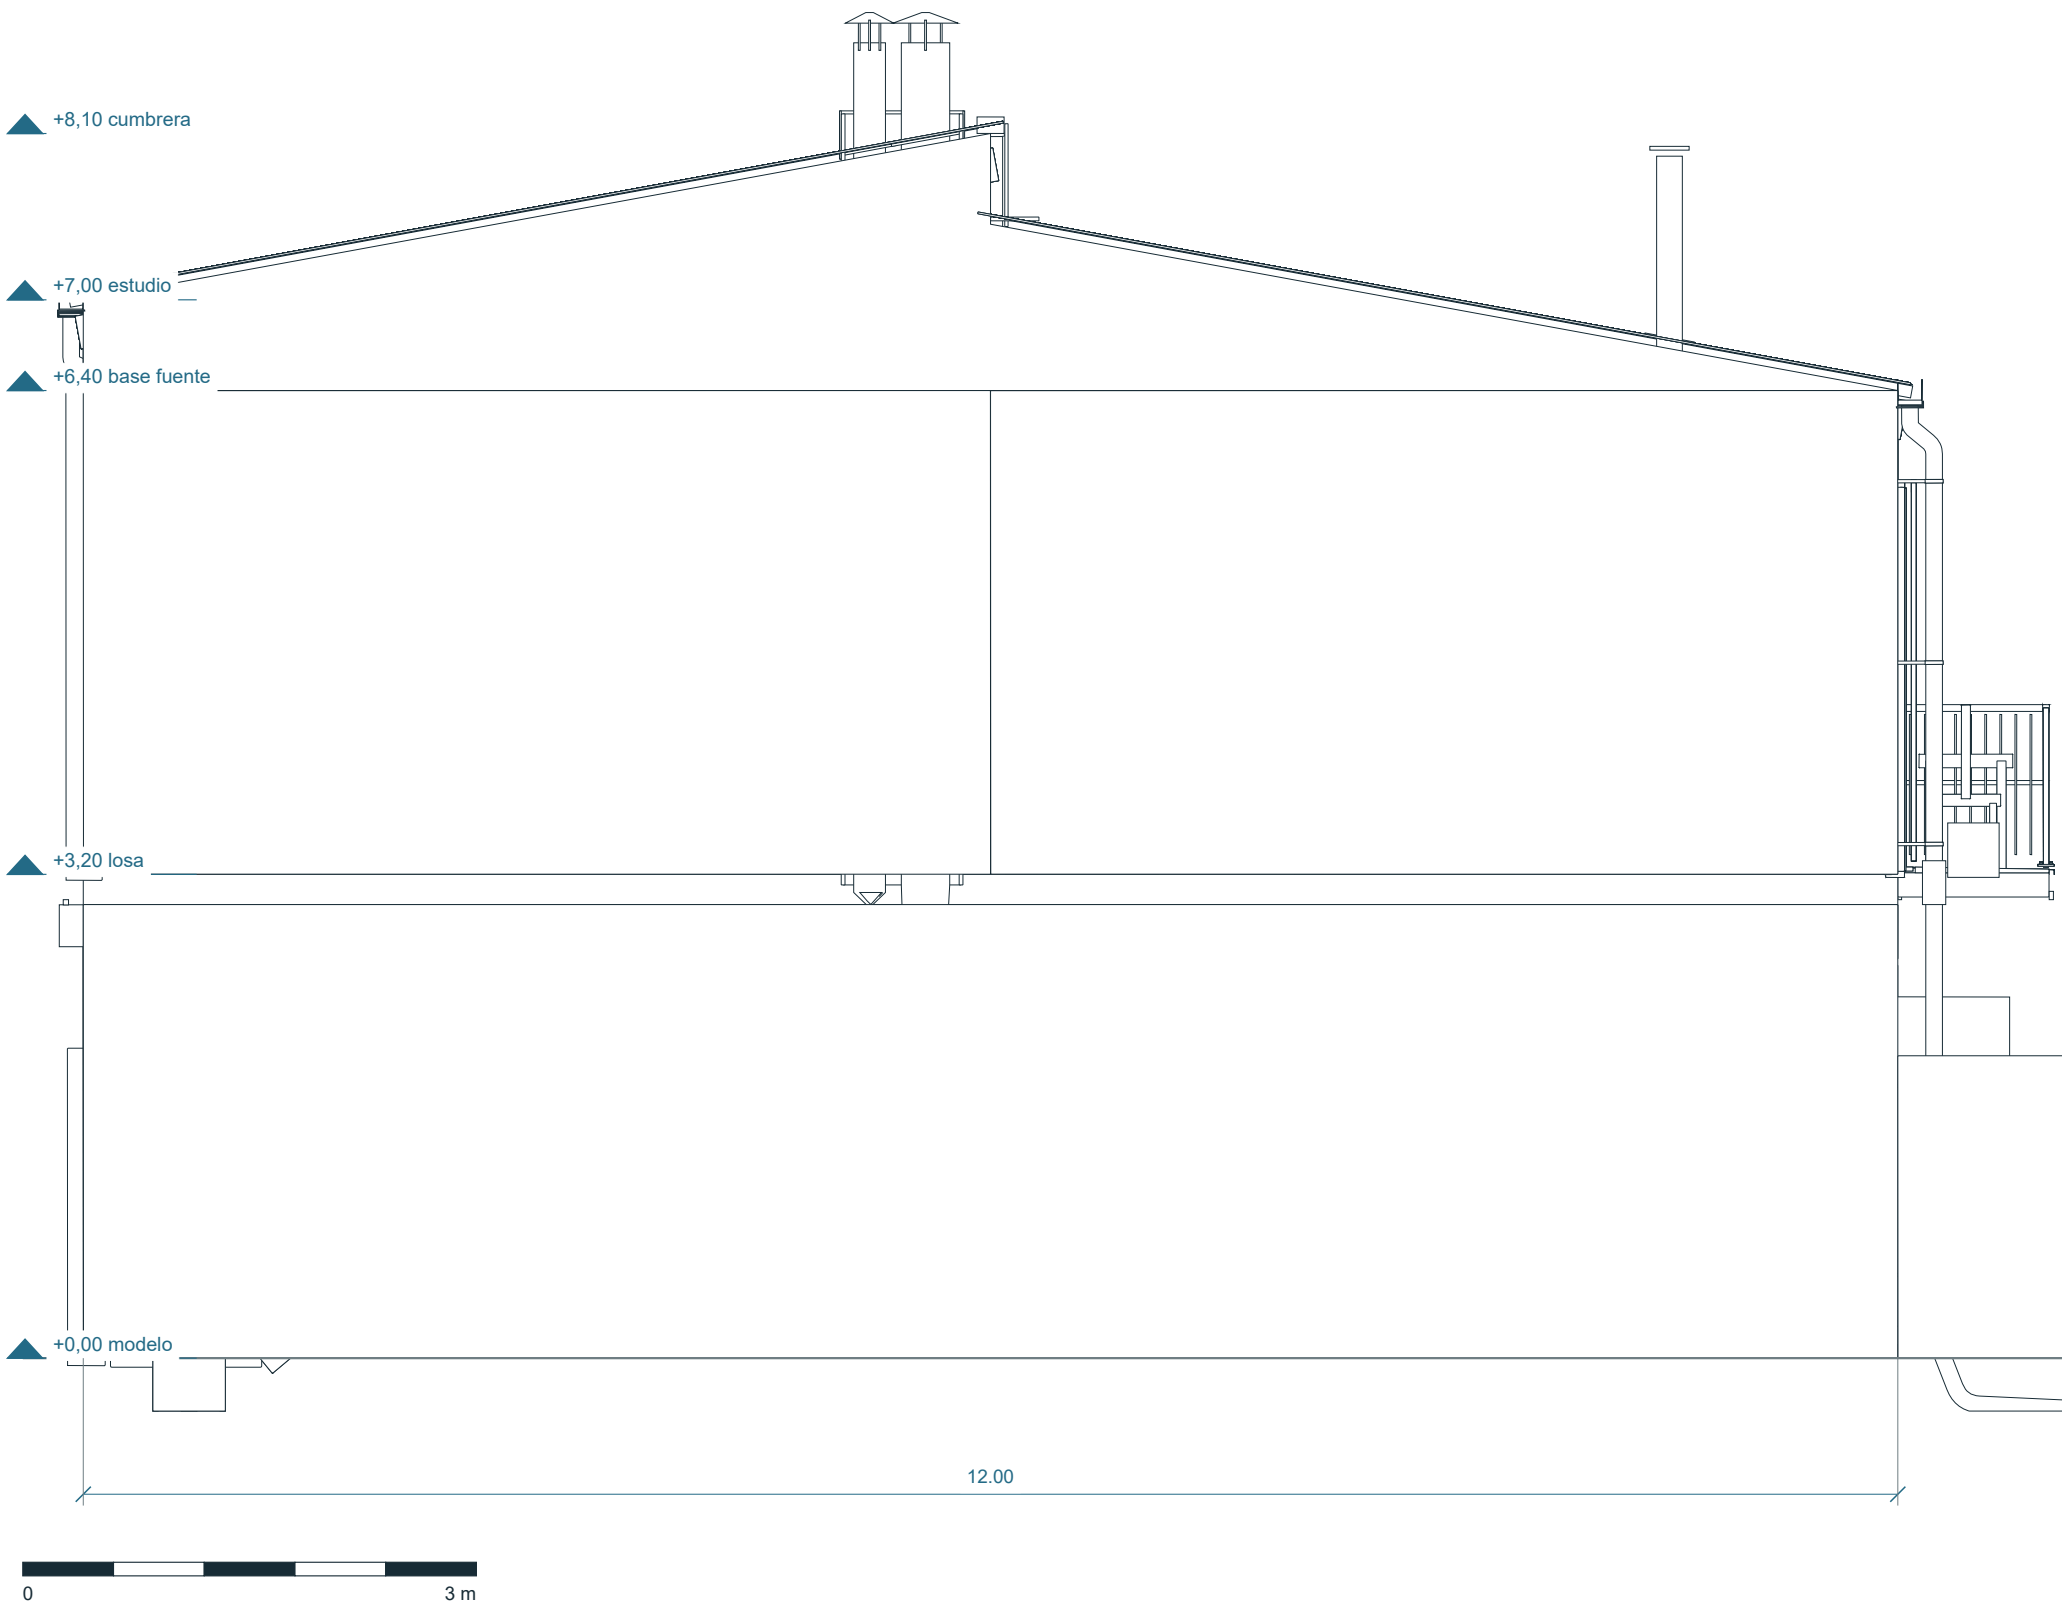

A-A Longitudinal por ambas alturas | 1:50

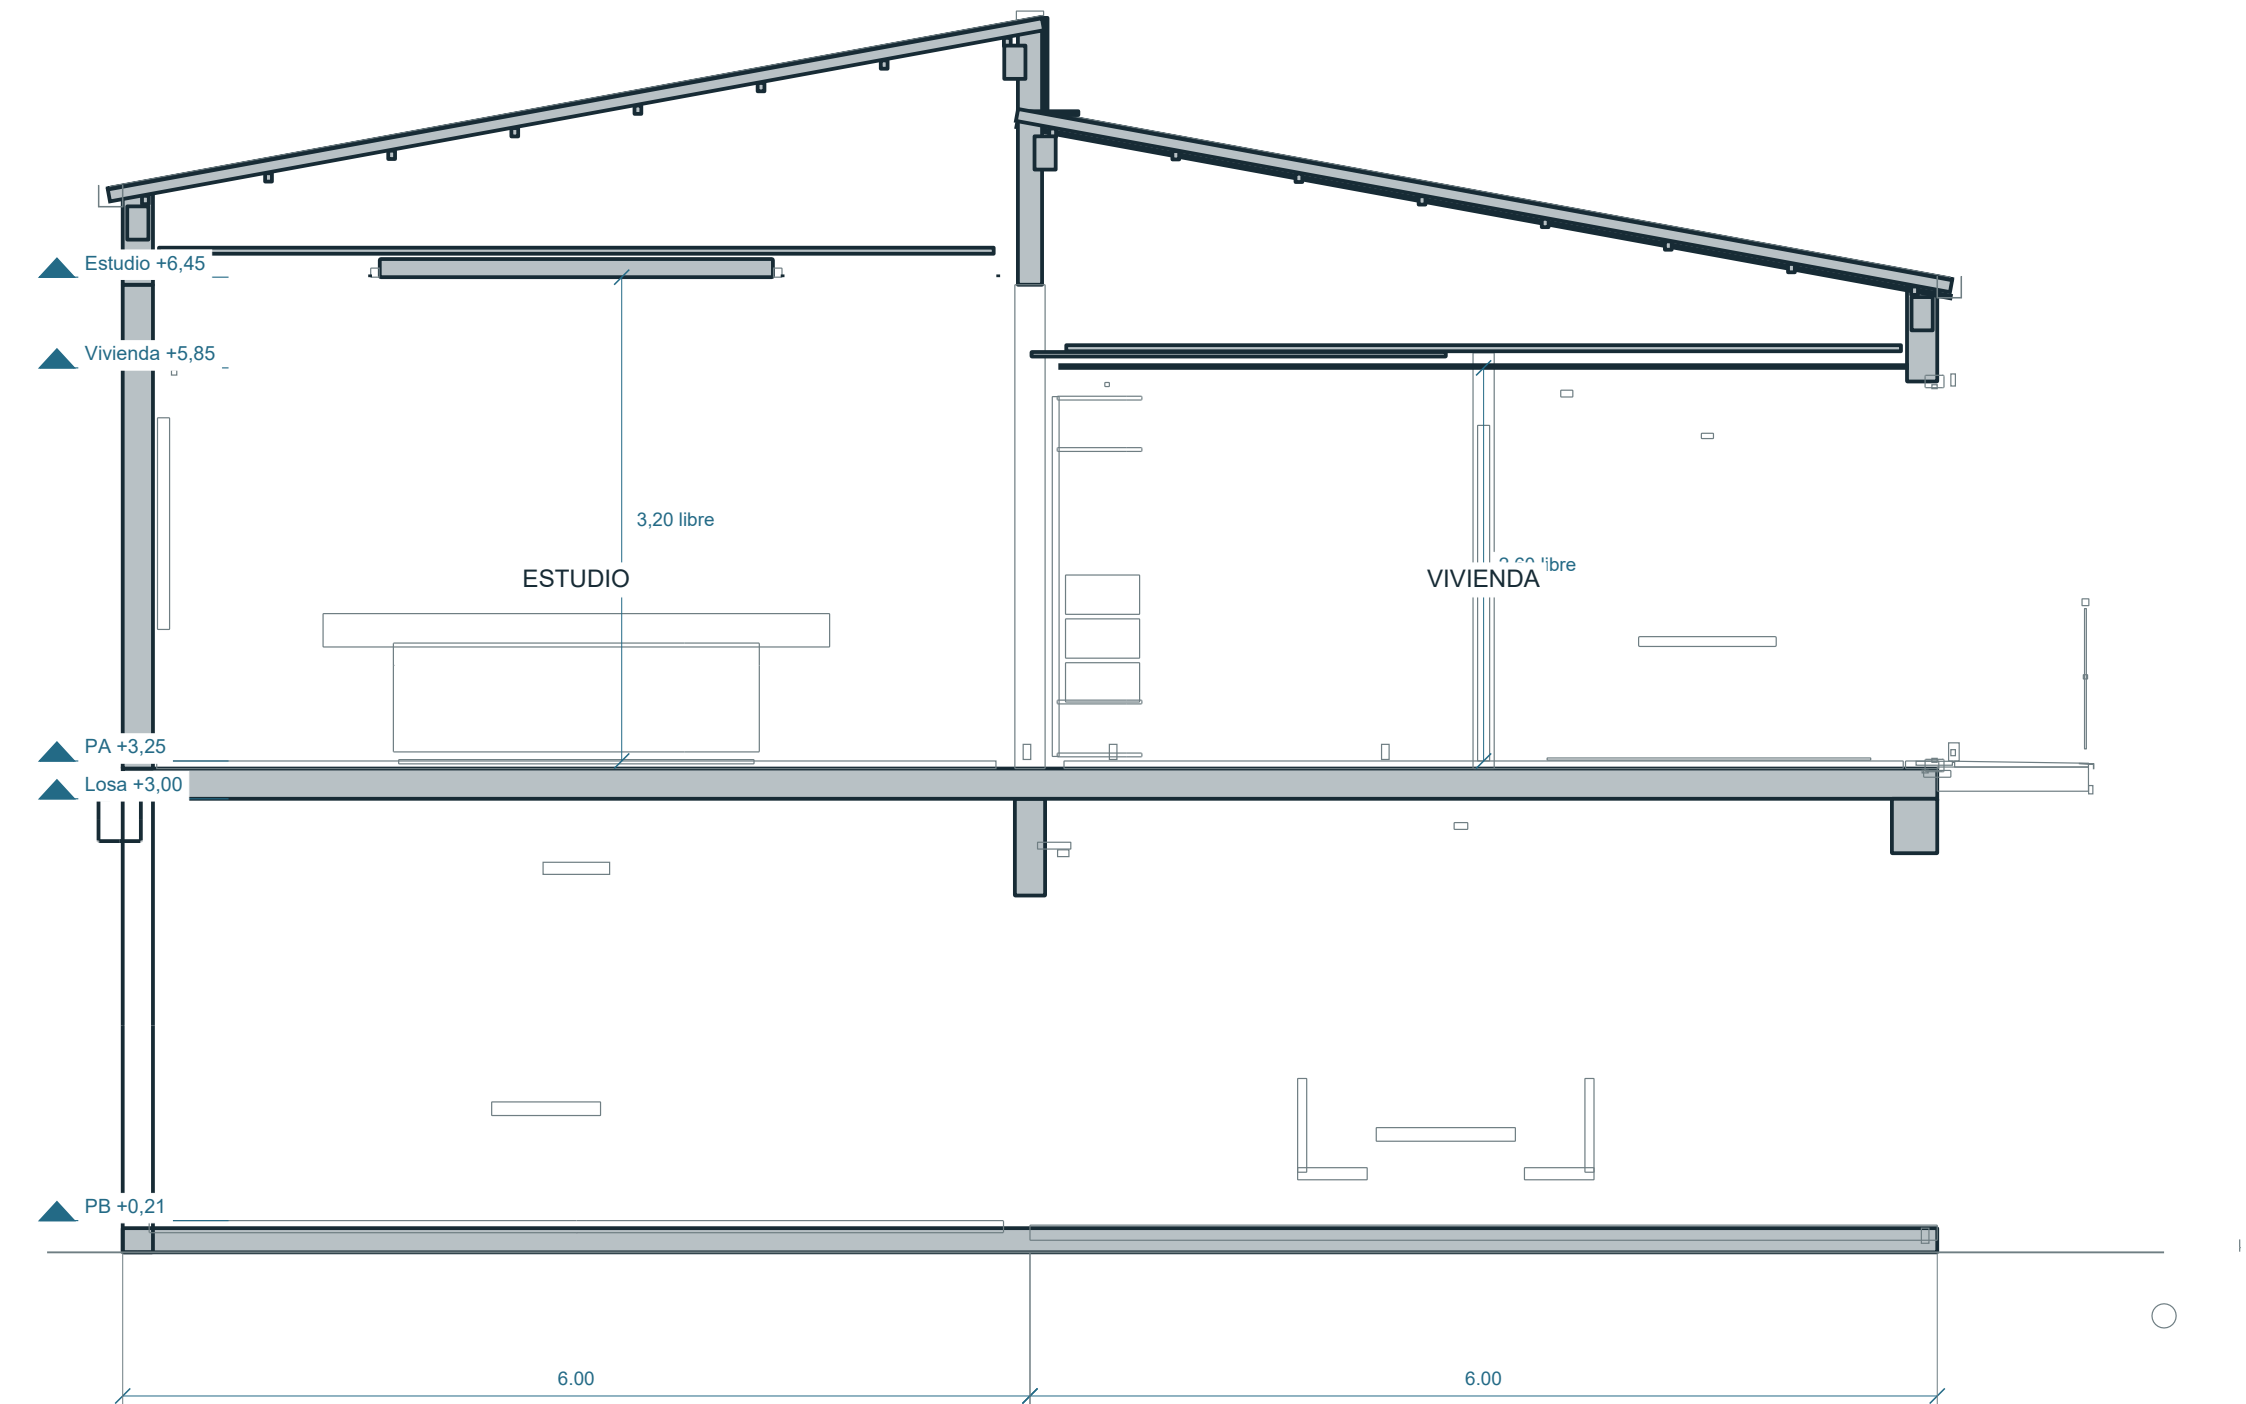

B-B Transversal por estudio | 1:50

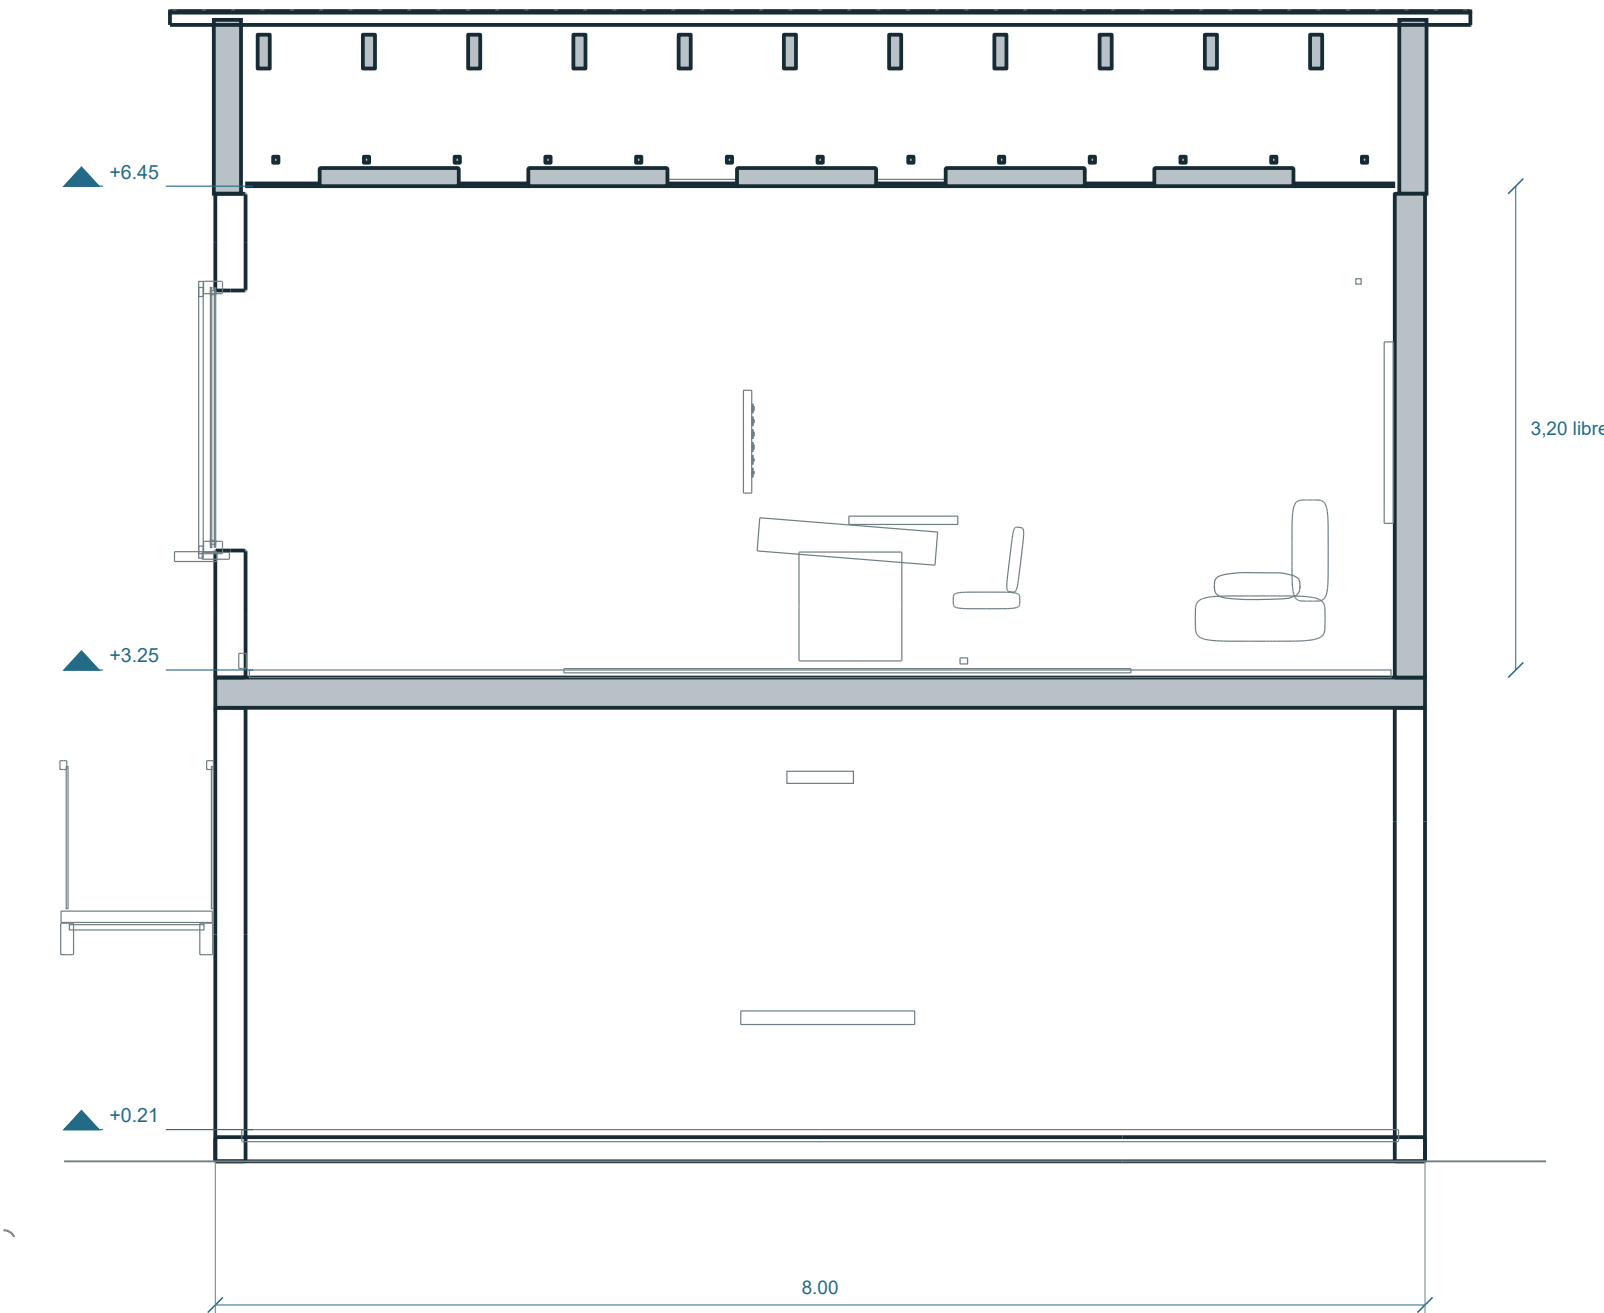


NIVELES Y CONSTRUCCION

G: losa entre plantas 0,20 m; piso general superior 0,05 m; cielorraso estudio +6,45 y vivienda +5,85. Corte A-A comprueba ambos volúmenes y el escalon exterior.


F: alturas libres autorizadas 3,20 / 2,60 m. La diferencia se conserva sin desplazar la implantación ni las huellas de los ambientes.

P: continuidad de cargas, fundaciones y conexiones por dimensionar. No hay estudio geotécnico ni verificación estructural; ver A14.


01 Planta / acceso | 1:20

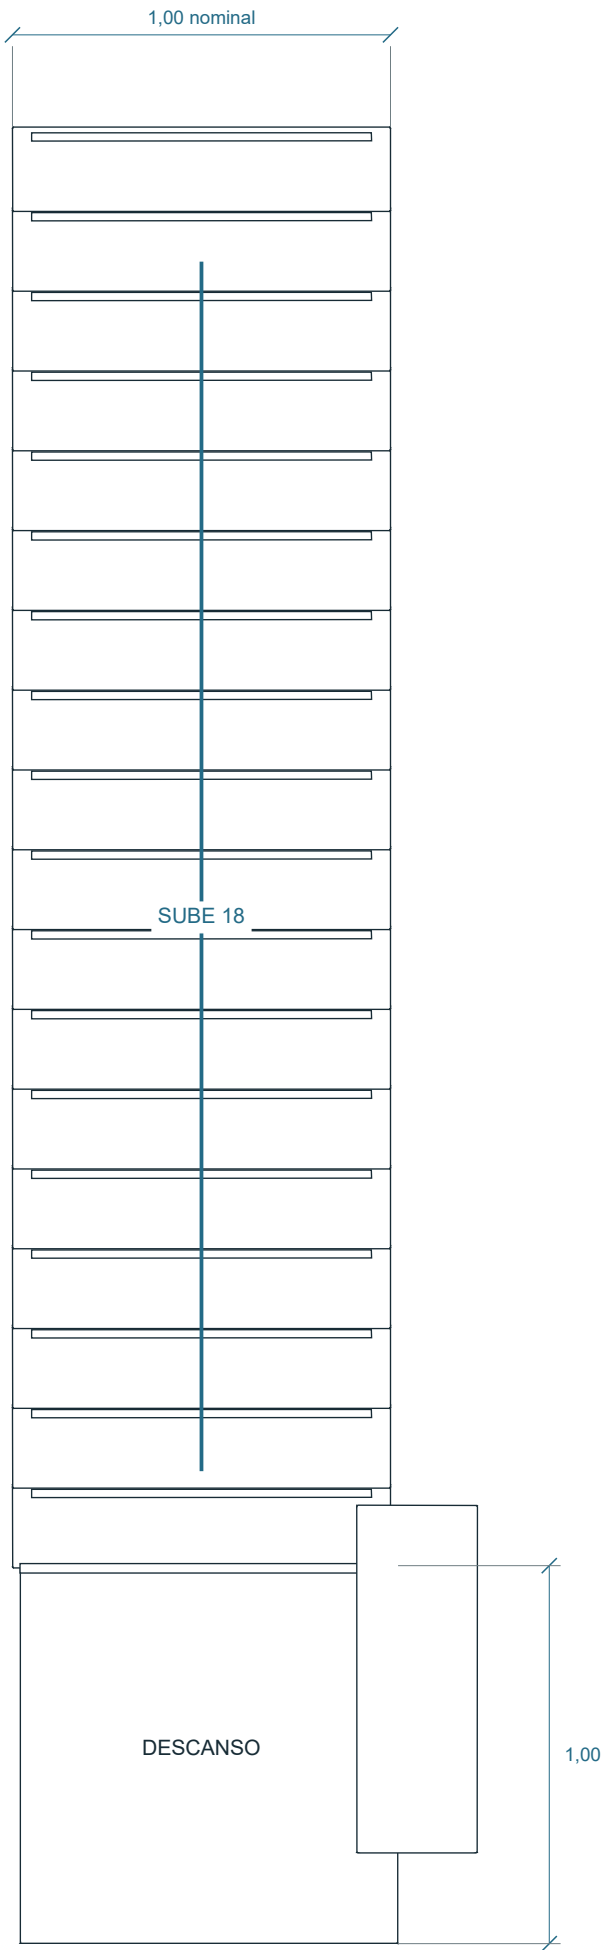

02 Seccion y proyeccion lateral | 1:20

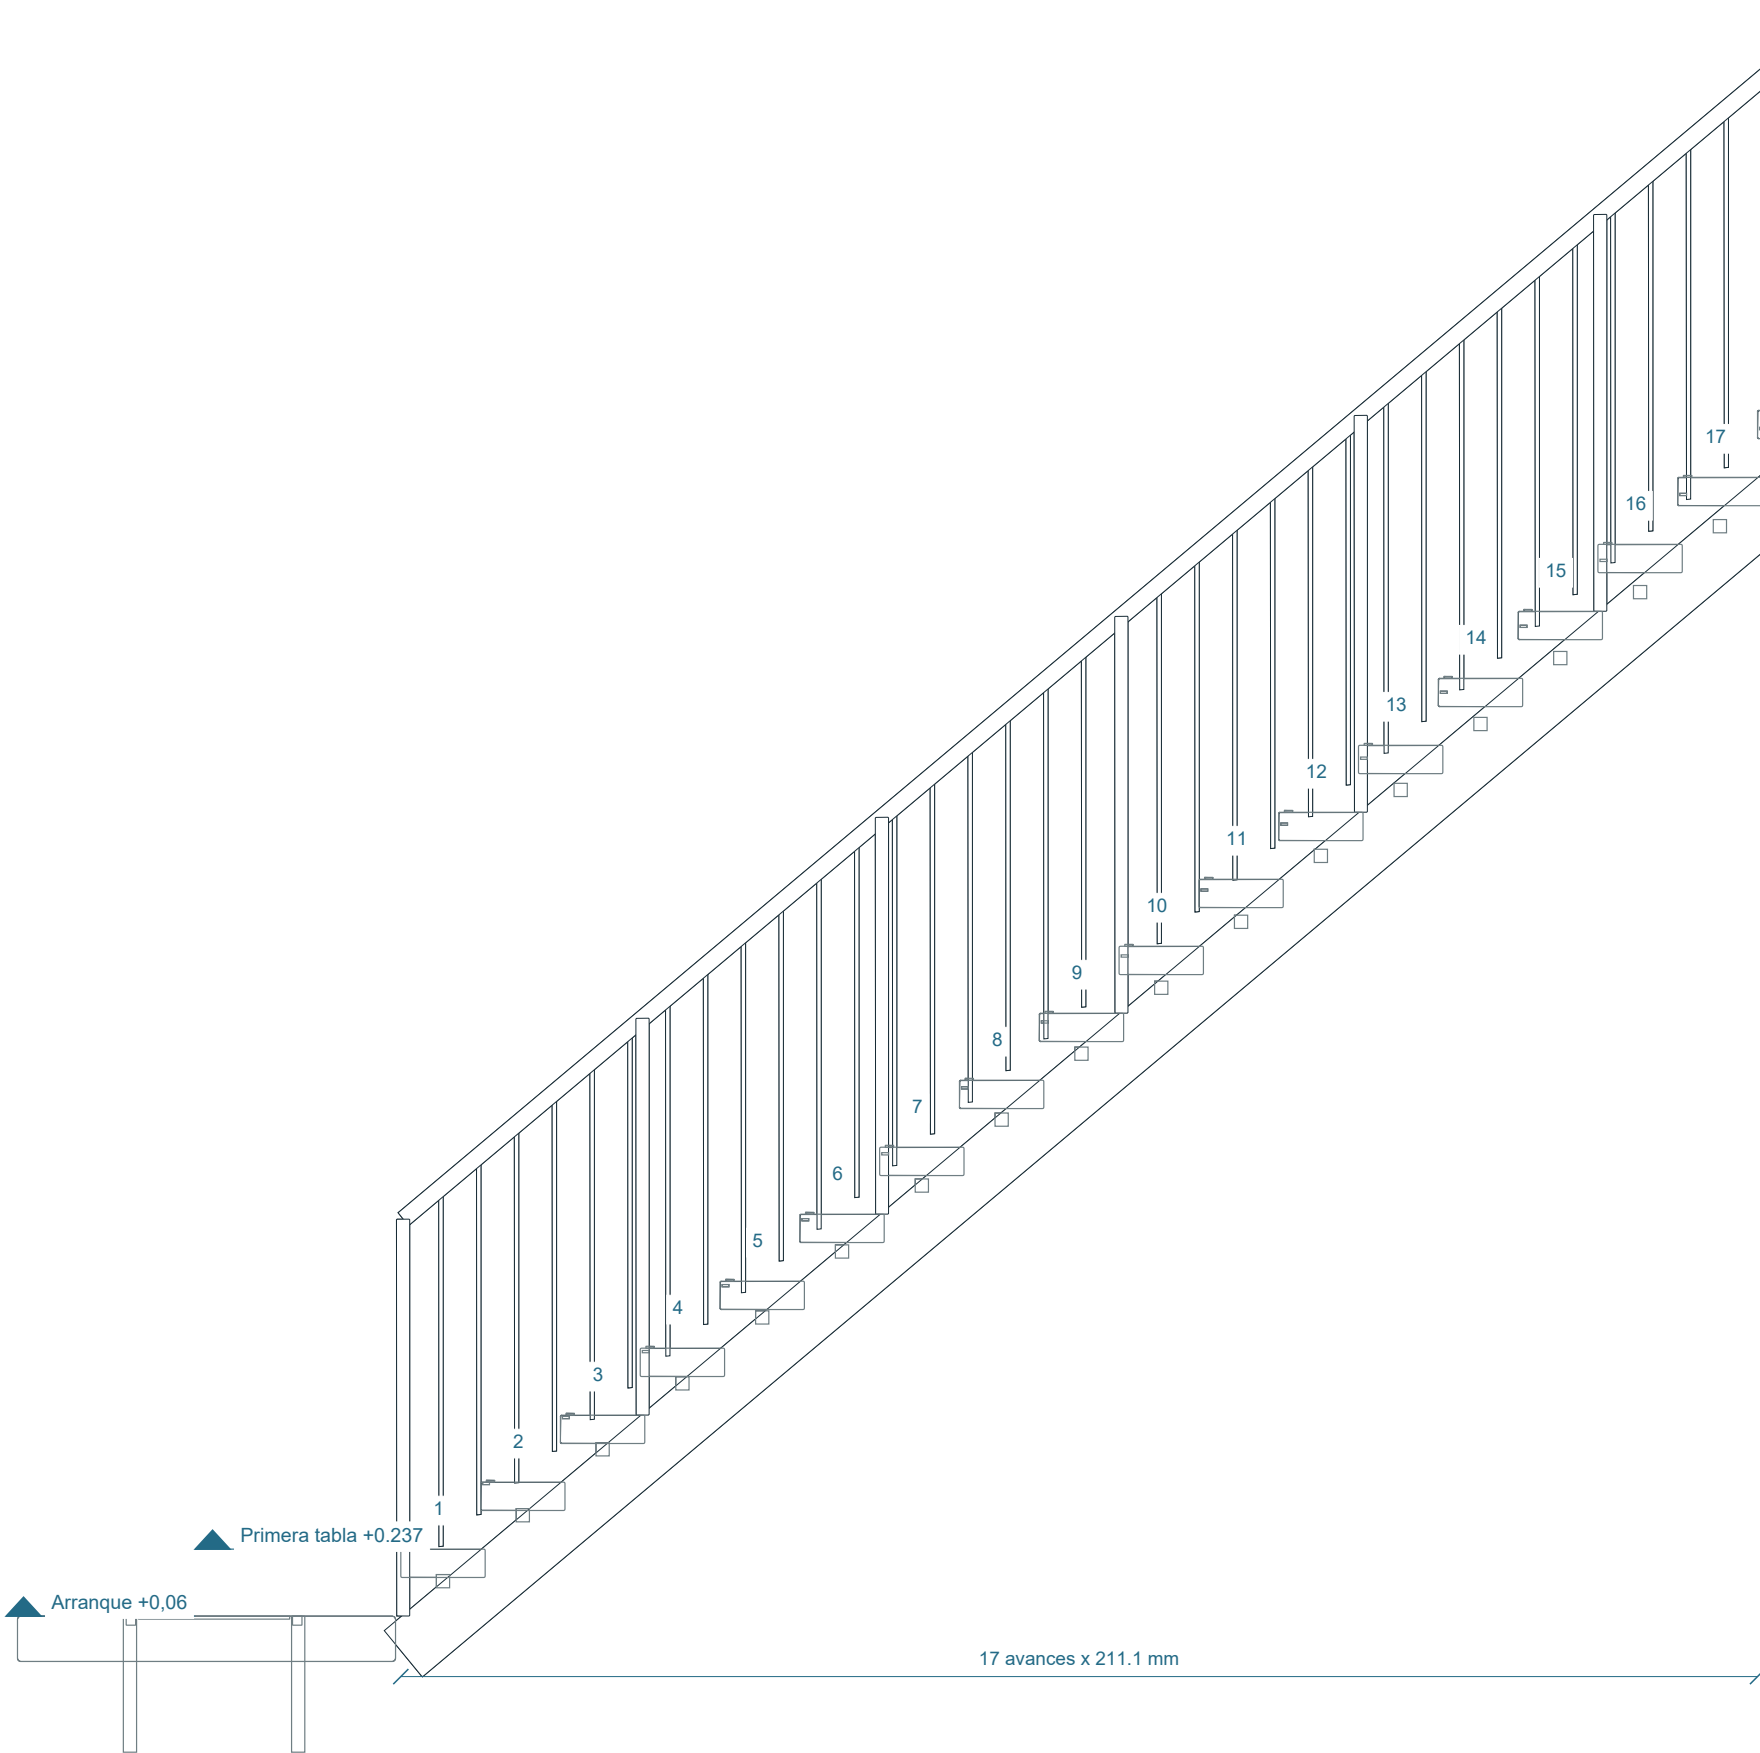

03 Umbral / corte Z=5,30 | 1:5

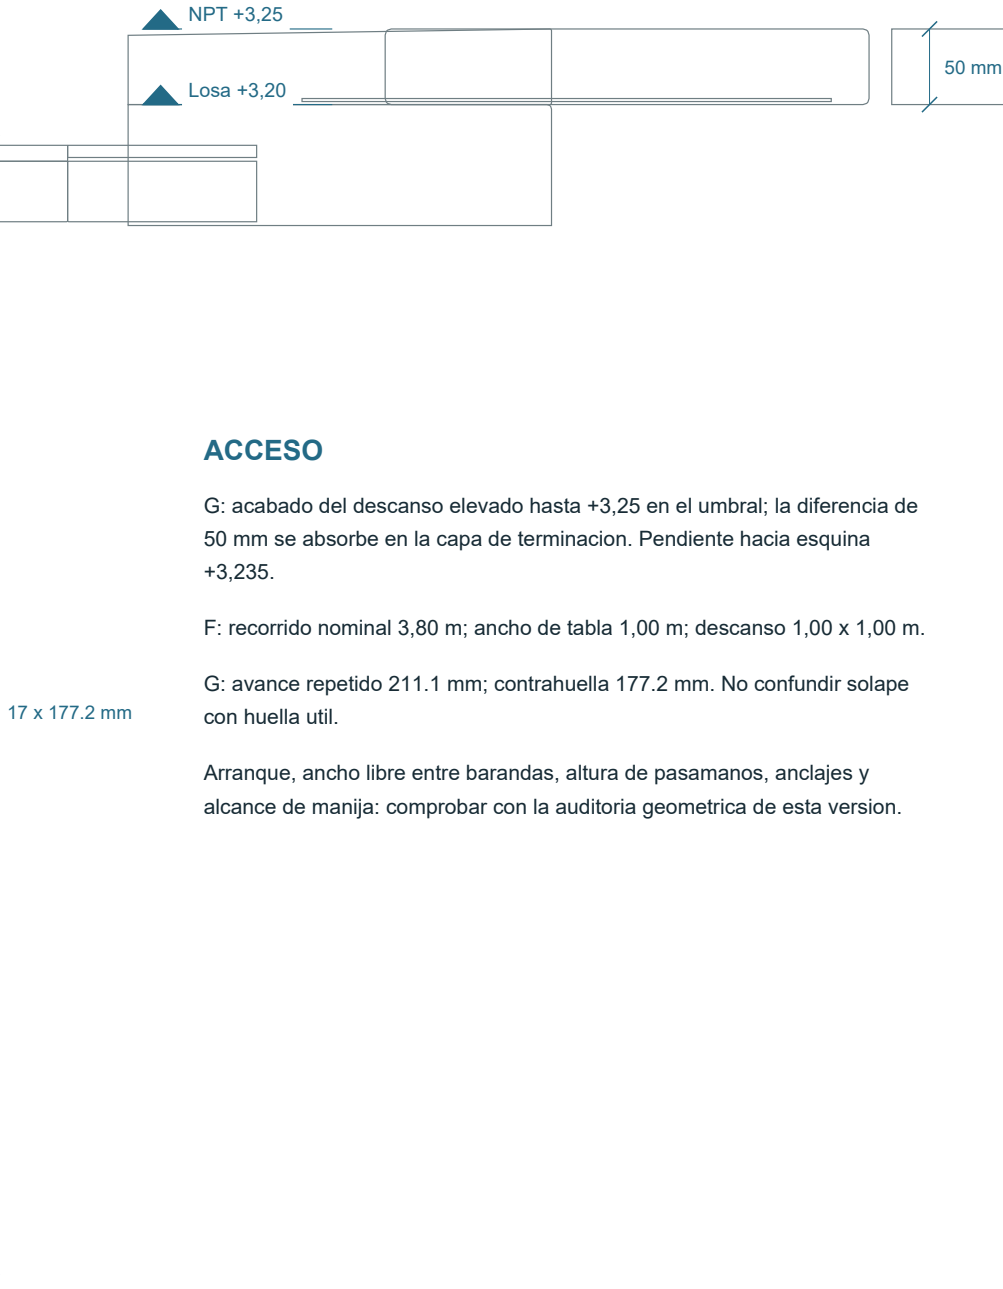

ACCESO

G: acabado del descanso elevado hasta +3,25 en el umbral; la diferencia de 50 mm se absorbe en la capa de terminacion. Pendiente hacia esquina +3,235.

F: recorrido nominal 3,80 m; ancho de tabla 1,00 m; descanso 1,00 x 1,00 m.


G: avance repetido 211.1 mm; contrahuella 177.2 mm. No confundir solape con huella util.

Arranque, ancho libre entre barandas, altura de pasamanos, anclajes y alcance de manija: comprobar con la auditoria geometrica de esta version.

COMPROBACIONES DE USO Y ANCLAJES

En el modelo: comprobar pavimento inicial y primera contrahuella, continuidad de pasamanos, proteccion del descanso y recorrido de apertura de la puerta. Secciones de anclaje en A14. No se modifican las cotas de fuente por ajuste grafico.

01 Planta del vaso y playa humeda | 1:25

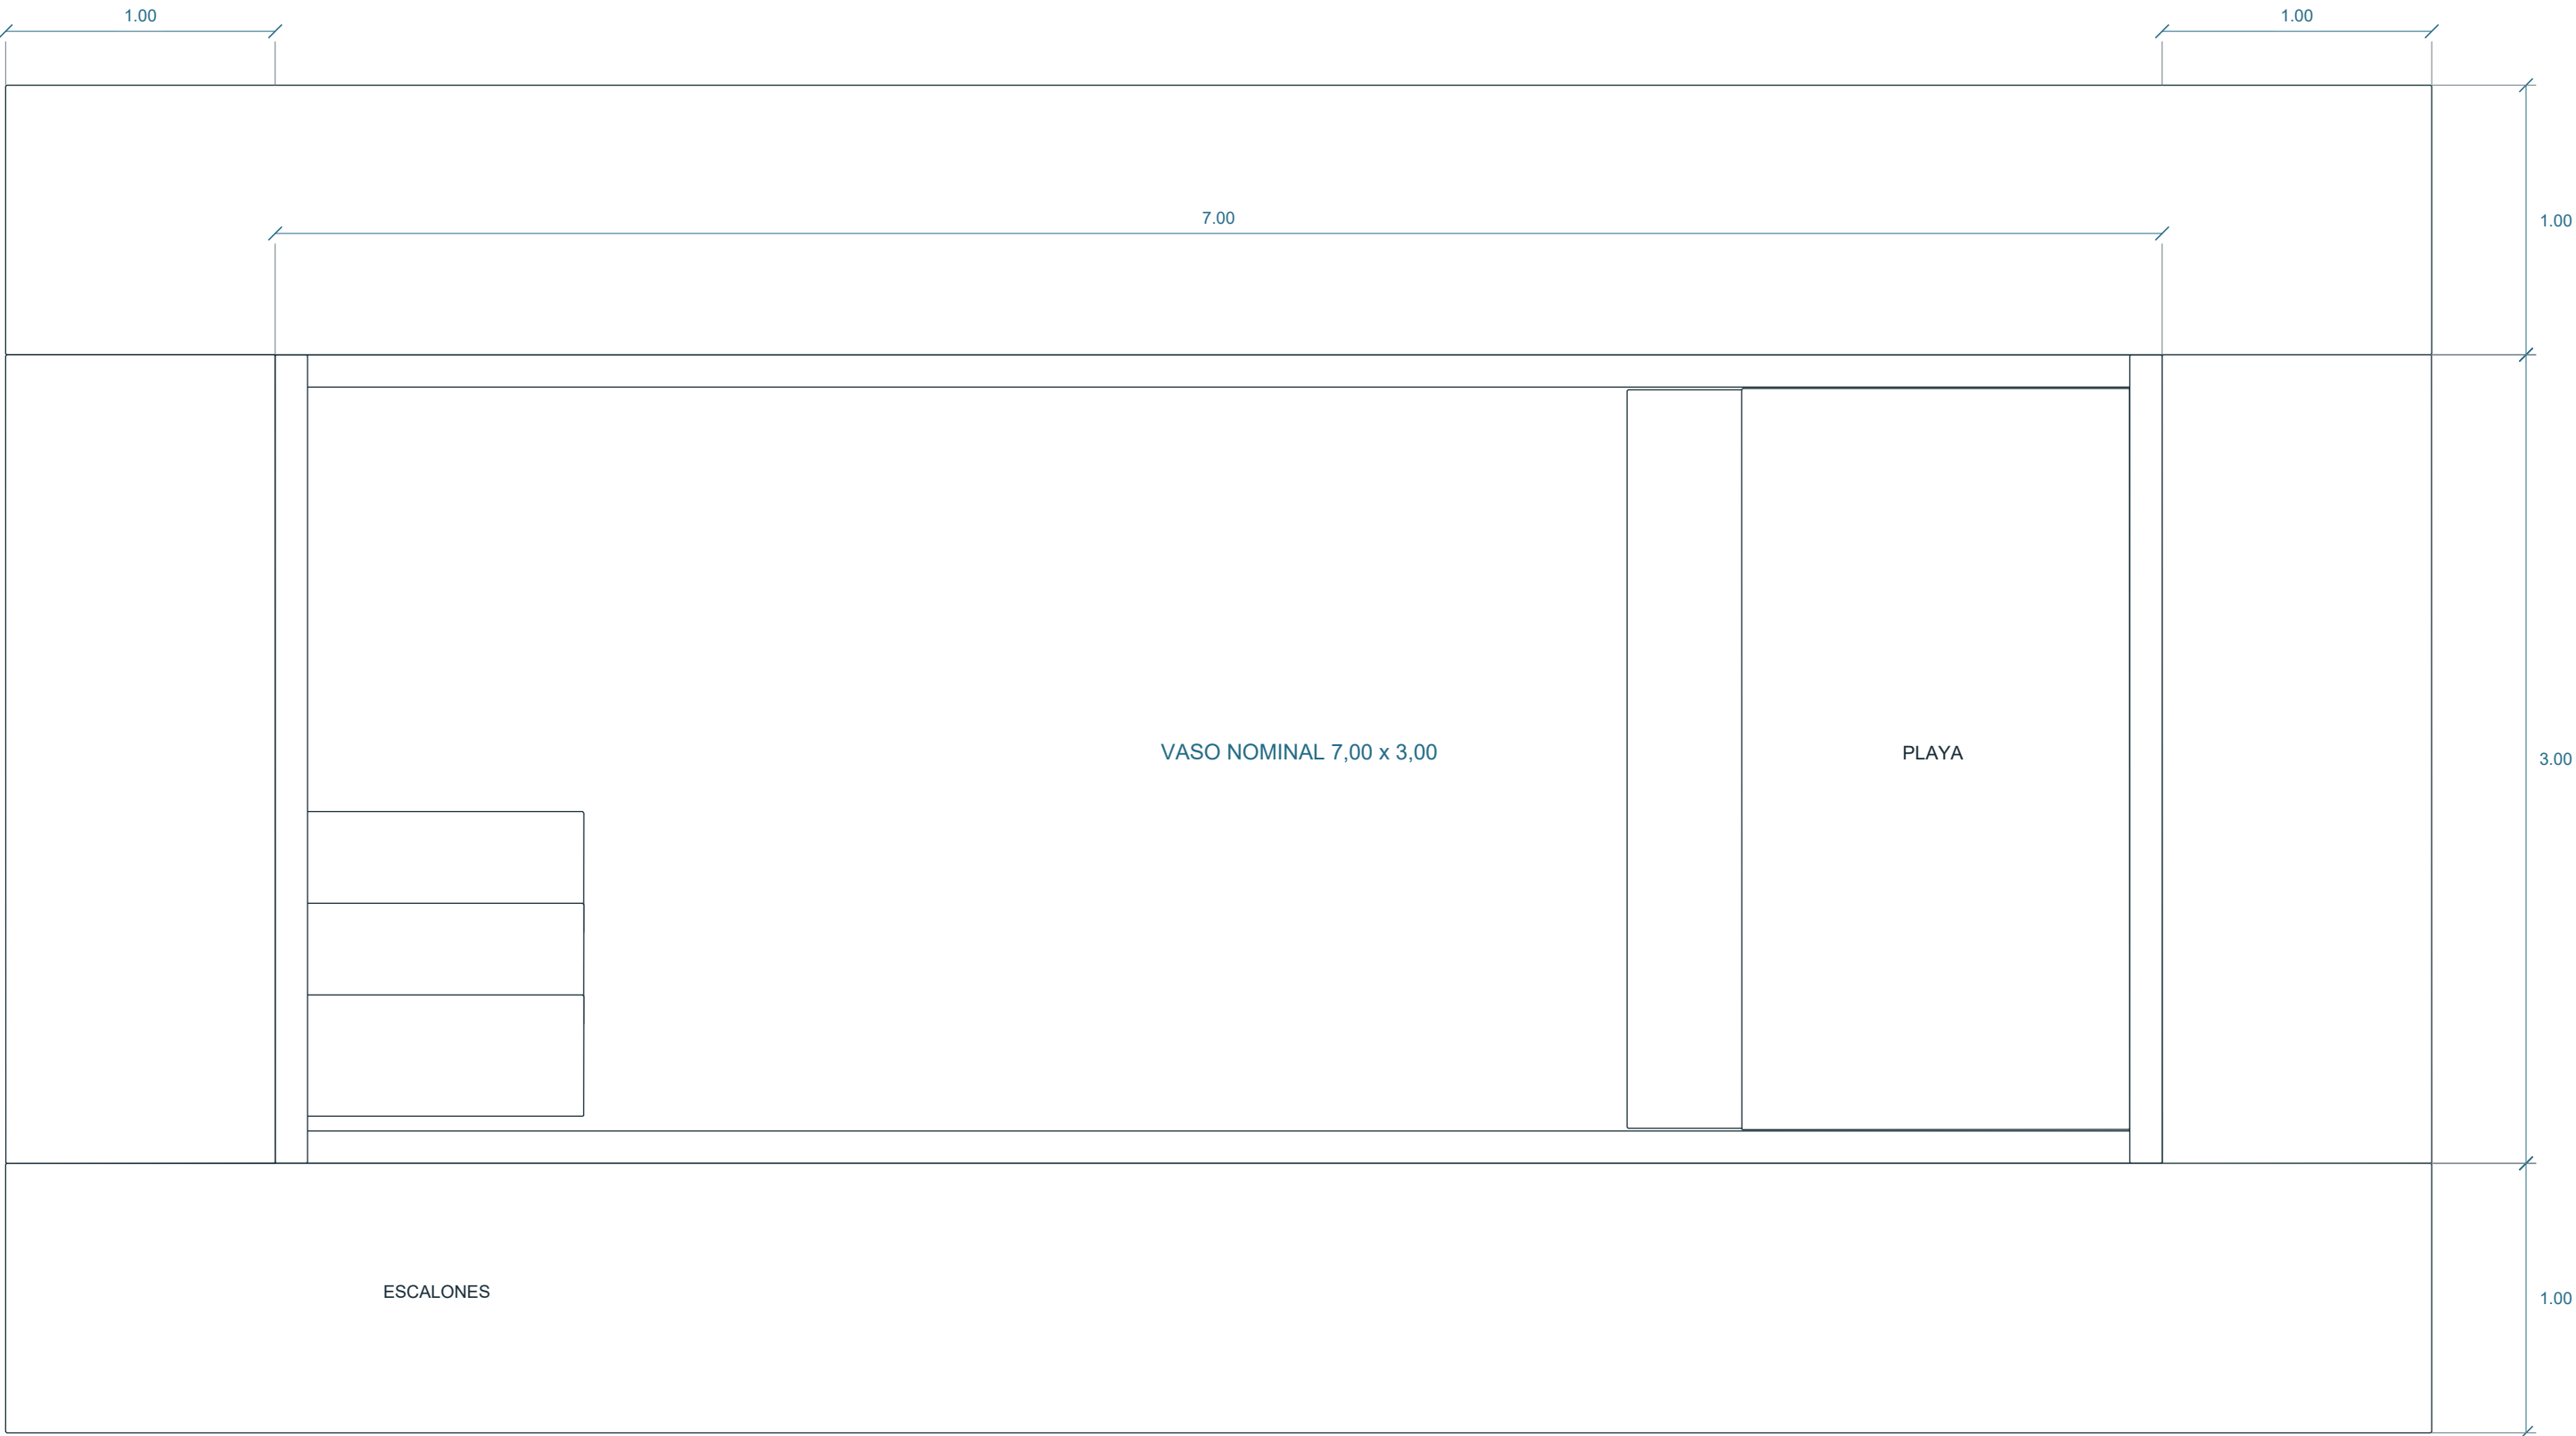

NIVELES DEL MODELO

G: pavimento perimetral +0,09 m; borde vertical del vaso hasta +0,07 m.

G: fondo del vaso entre -1,57 y -1,39 m; espesor representado 0,18 m.


G: tres escalones con caras superiores -0,14 / -0,43 / -0,72 m.




G: playa humeda superior -0,08 m; escalon intermedio -0,31 m.

Agua es un volumen de visualizacion. Nivel operativo, rebalse y resguardo deben definirse en proyecto de pileta.

P: skimmer, retornos, toma de fondo, equipo de filtrado y desague requieren ubicacion, dimensionado y seguridad especifica. Esquema en A15.


02 Corte transversal al largo / Z=16,50 | 1:50

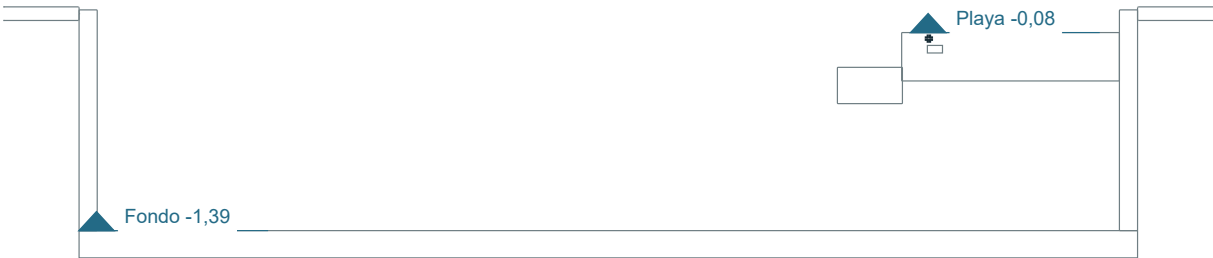

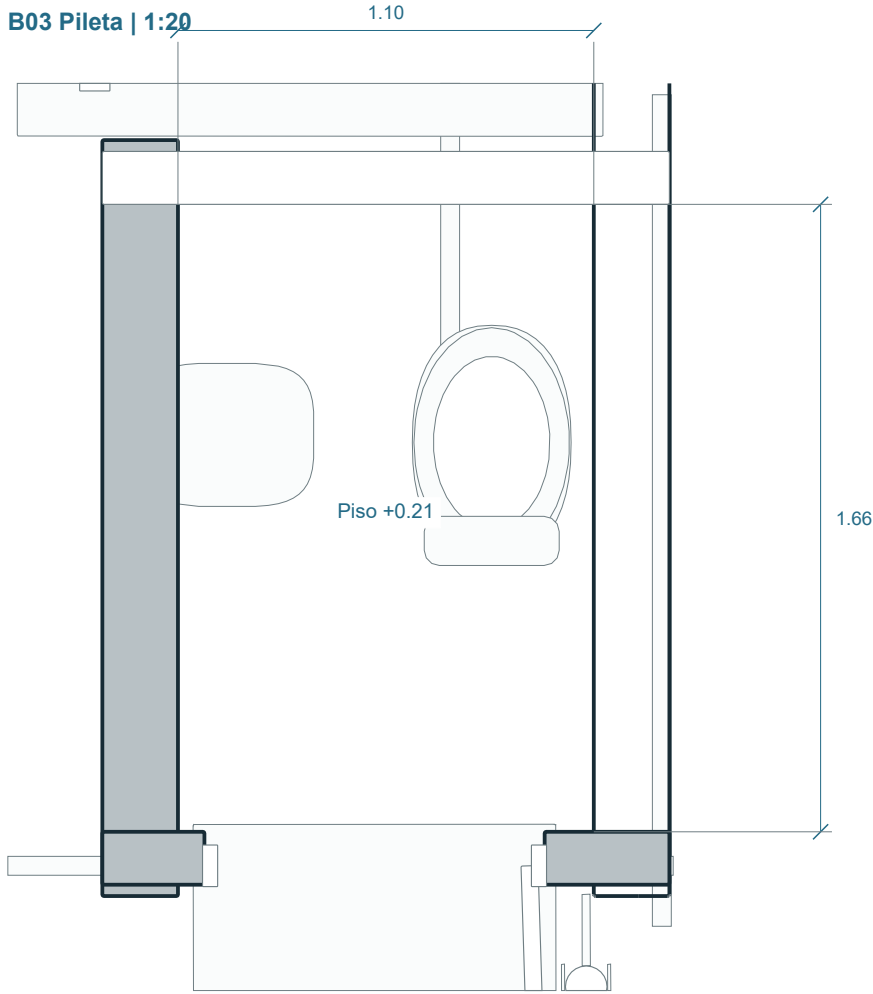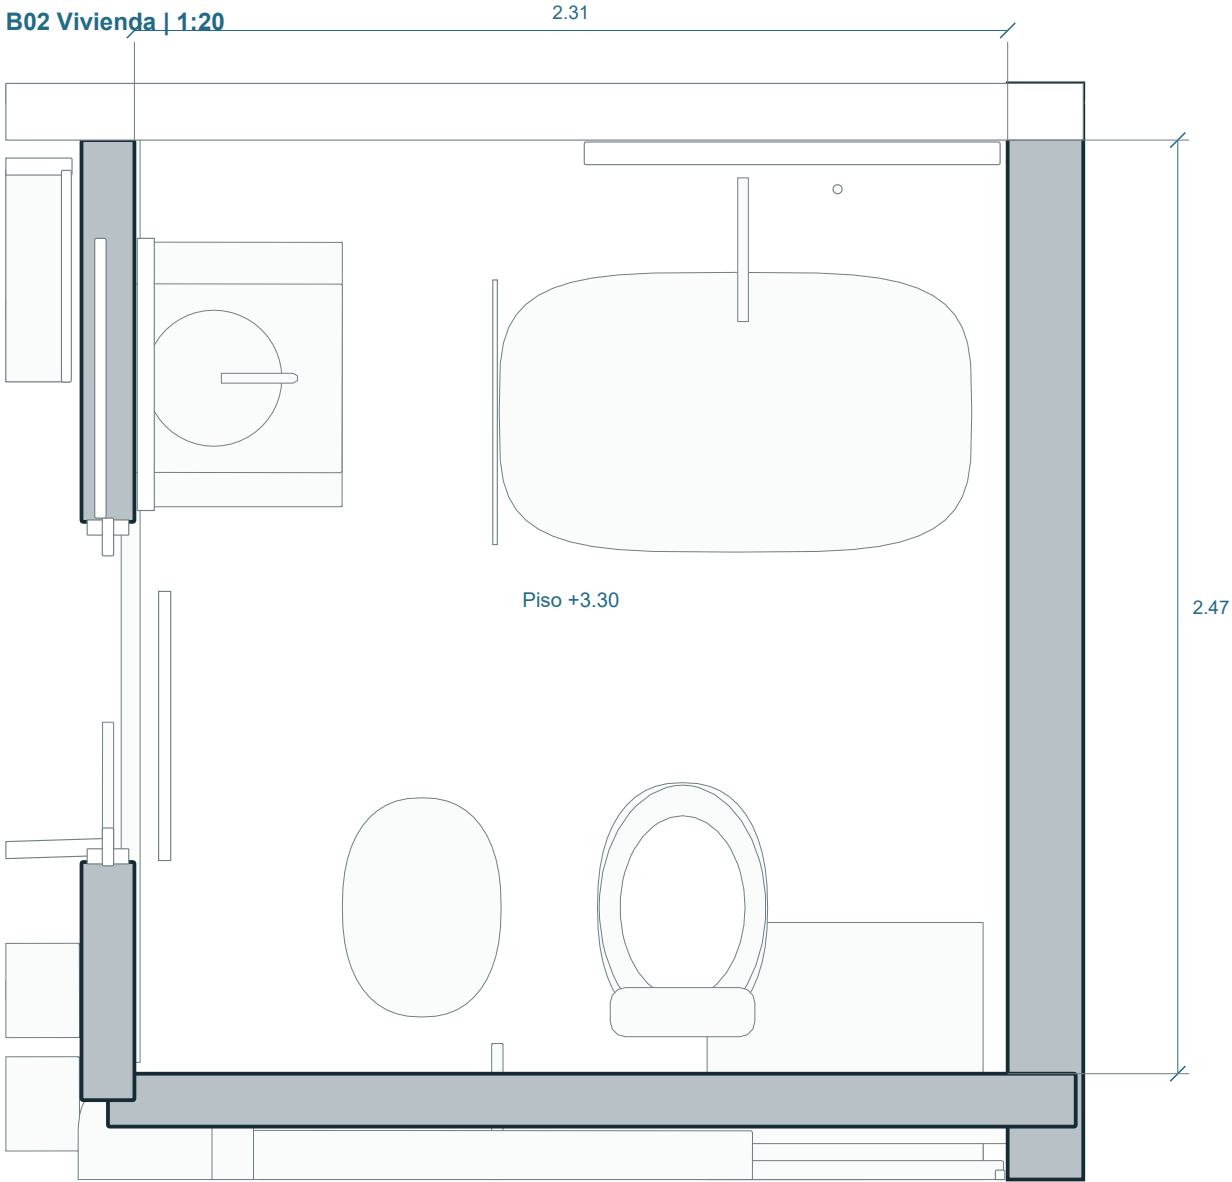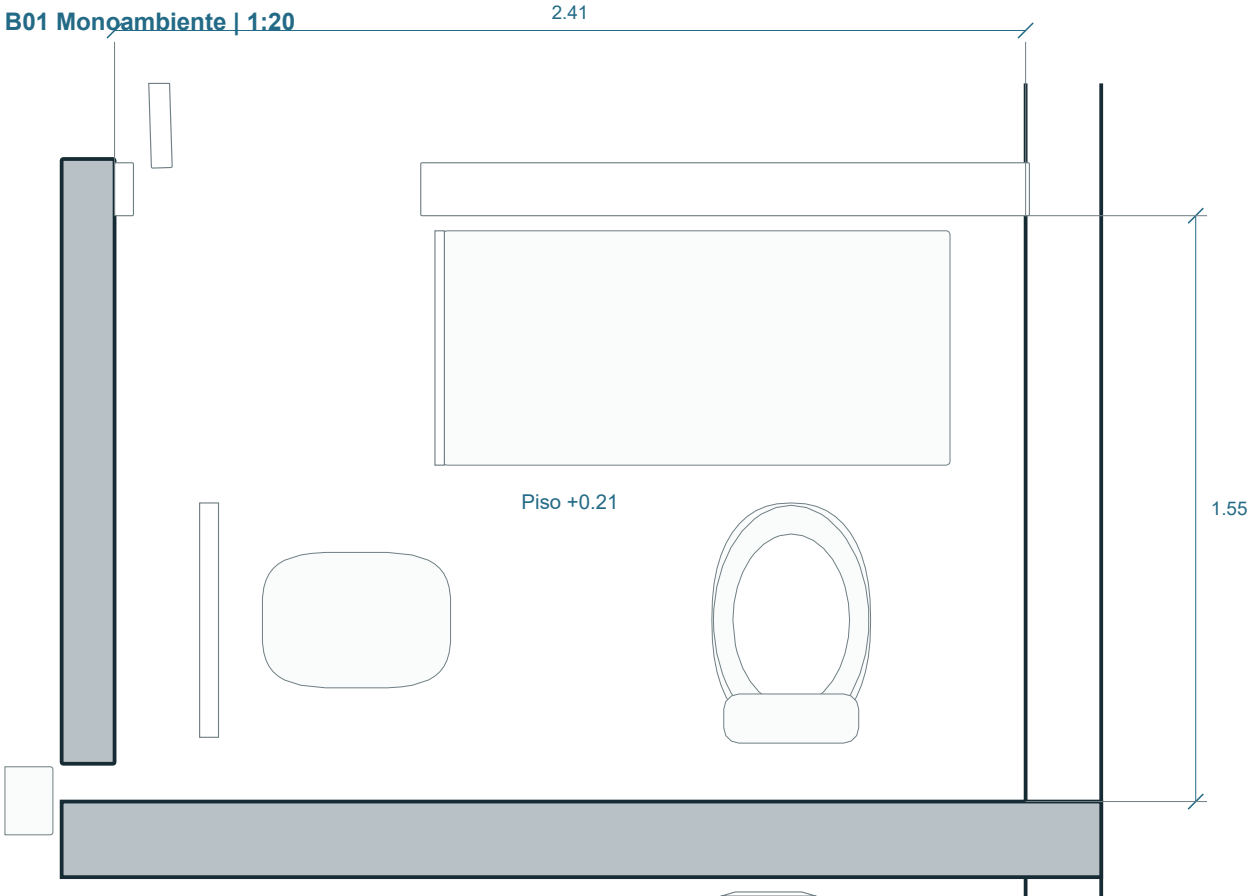


Los artefactos y mamparas se proyectan desde la malla actual. Cotas interiores entre caras del modelo; confirmar terminaciones, pendientes, accesos de mantenimiento y sellos. Las plantas muestran los vanos; el cuadro de hojas esta en A12.


Elevacion interior / artefactos | 1:20

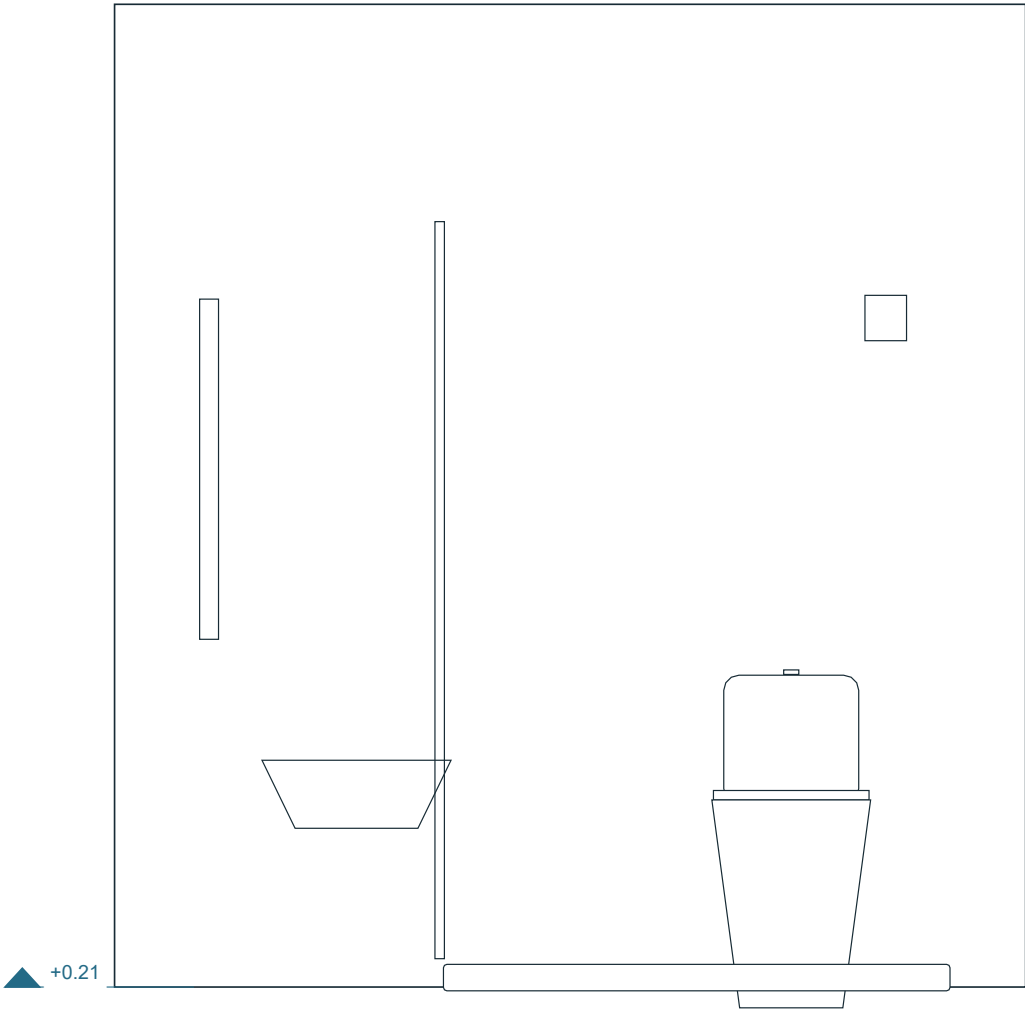


Elevacion interior / artefactos | 1:20

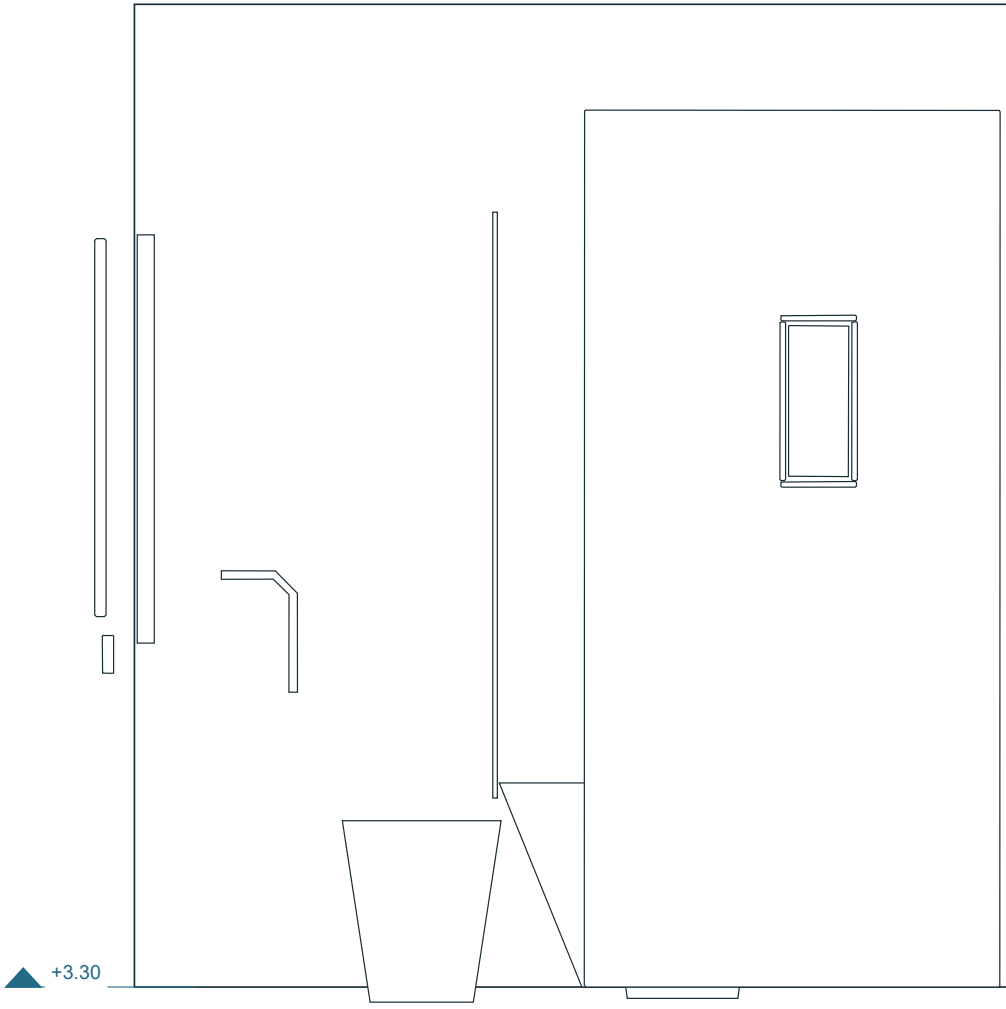

Elevacion interior / artefactos | 1:20

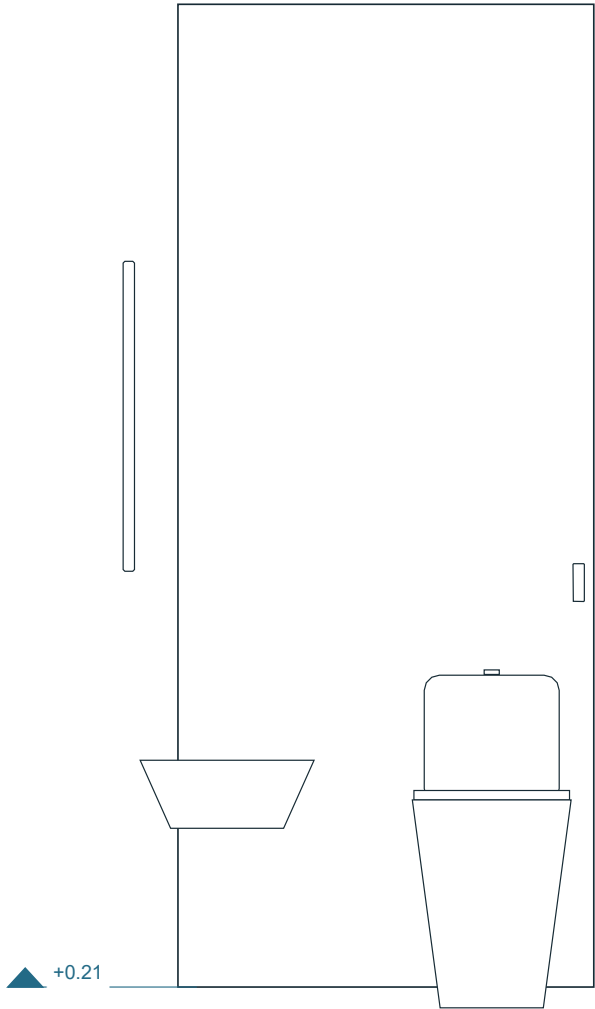

01 Línea del quincho | 1:25

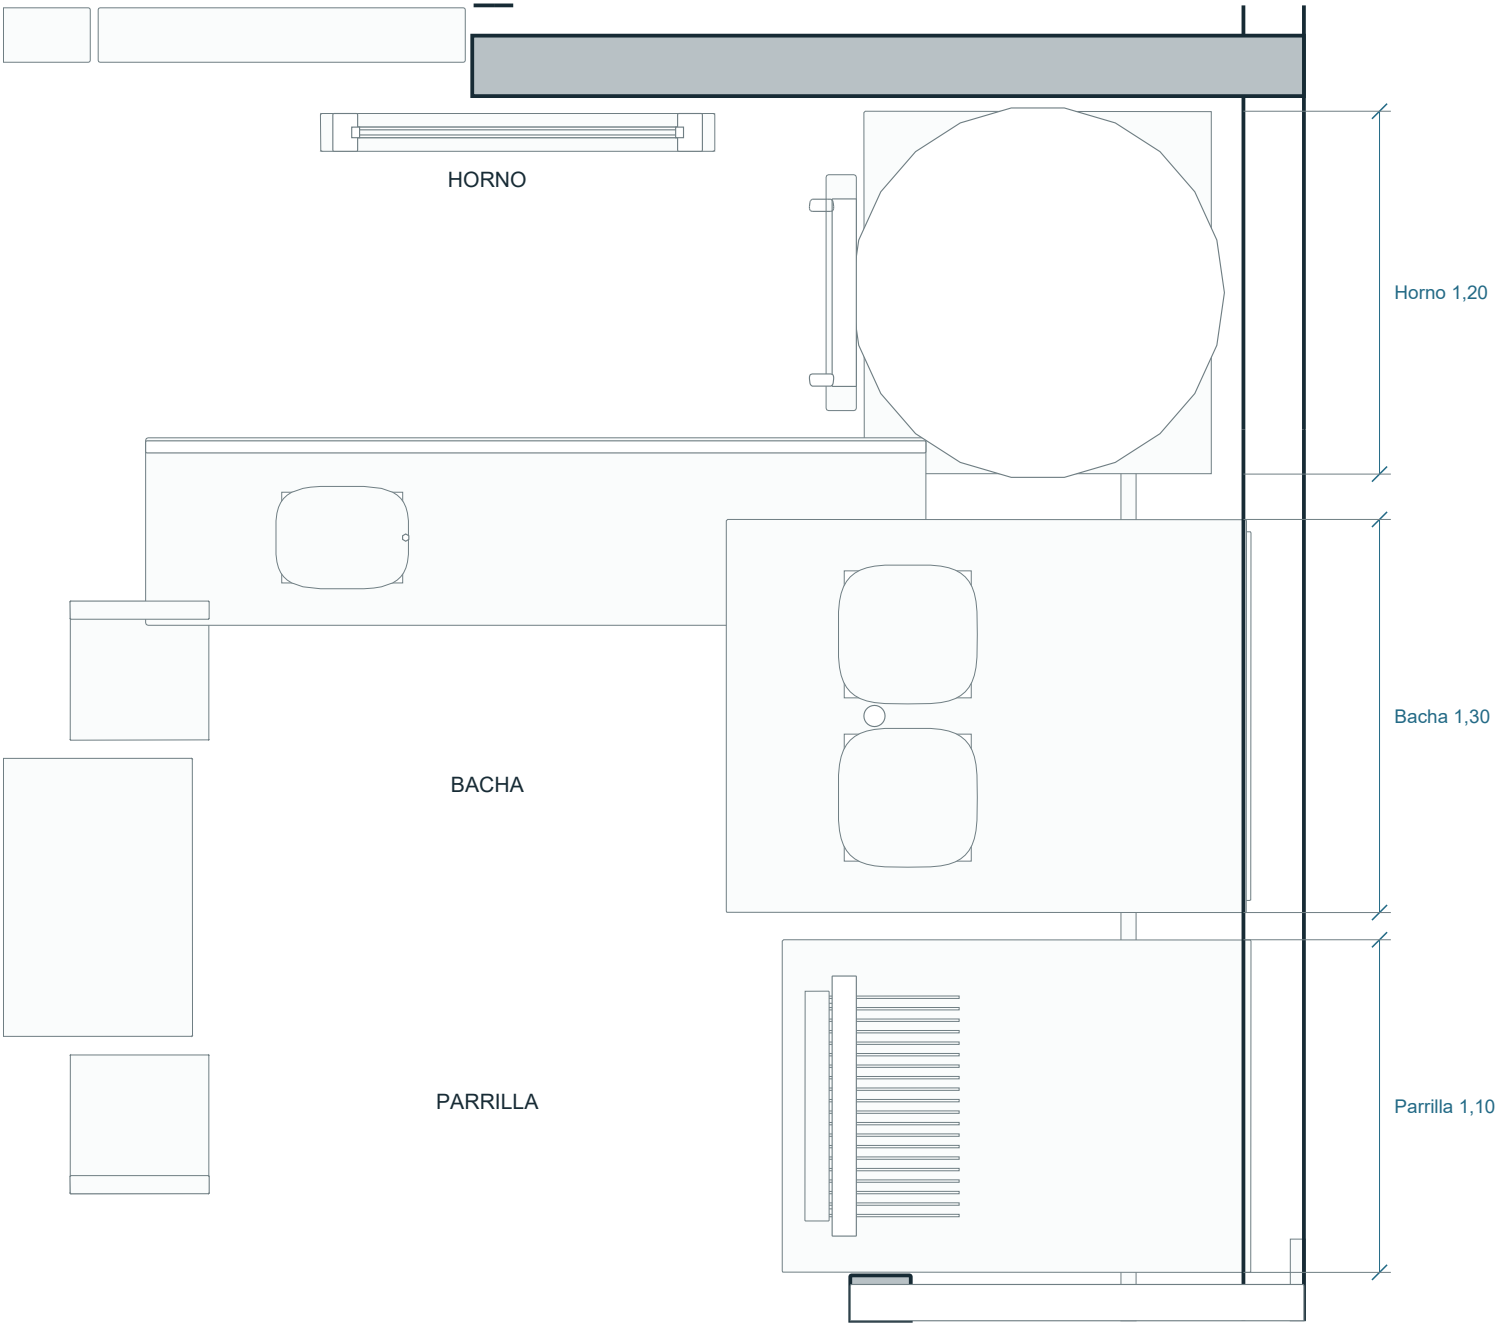


ALTURAS Y RELACION CON LOS LOCALES

G: mesada bacha quincho hasta +1,08 m; mesa quincho +0,825 m; isla mono +1,155 m. Valores medidos sobre el cero del modelo.


Comparar alturas de trabajo descontando el piso terminado de cada ambiente. No se confunden cotas absolutas con altura sobre piso.

La campana, el faldon y la boca de cada equipo se leen en los cortes del modelo. El tiro de combustion no esta certificado.

02 Cocina mono / isla | 1:25

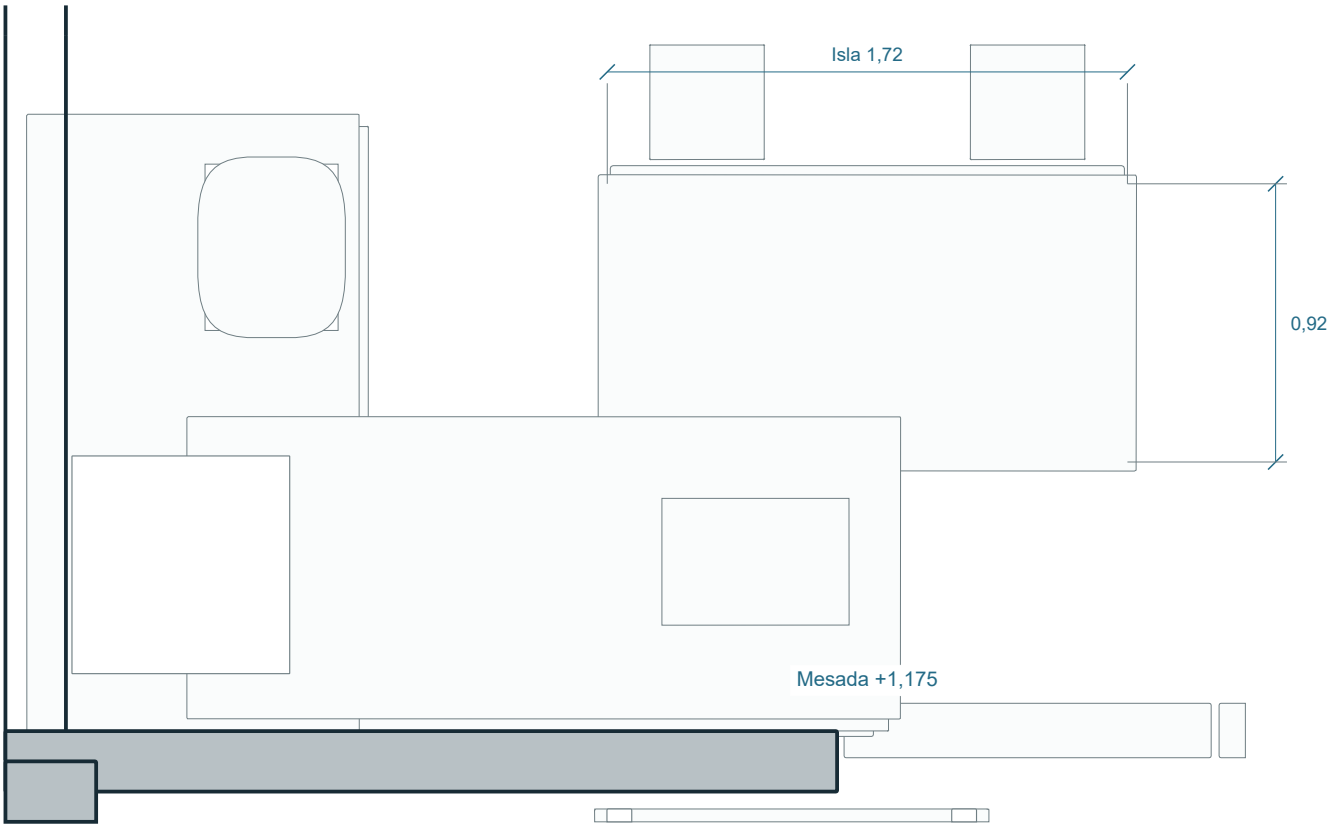

03 Cocina vivienda | 1:25

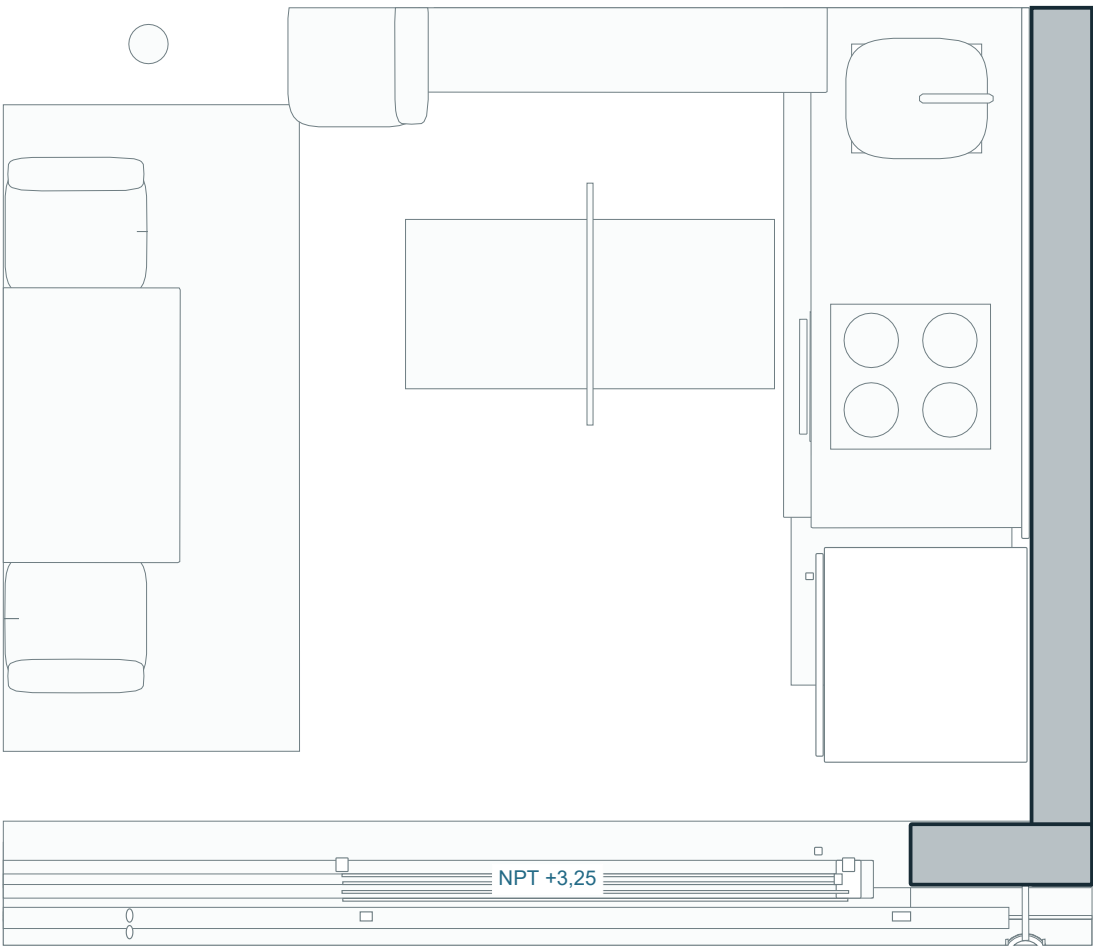

EXTRACCION Y MANTENIMIENTO


G: horno y parrilla con conductos independientes hacia el patinillo junto al estudio; cocina vivienda con salida independiente.

G: diámetros representados de horno / parrilla ~0,21 / 0,32 m; son dimensiones de malla, no resultado de calculo.

P: verificar longitud desarrollada, radios, caudal, reposicion de aire, temperatura, aislamiento, registro y limpieza.

P: conexiones sanitarias de bachas y lavatorios, llaves de corte y sifones requieren detalle de instalacion. A15 ubica los puntos de coordinacion.

El patinillo comparte proximidad con el estudio. A11 identifica control termico, vibratorio y acustico pendiente.

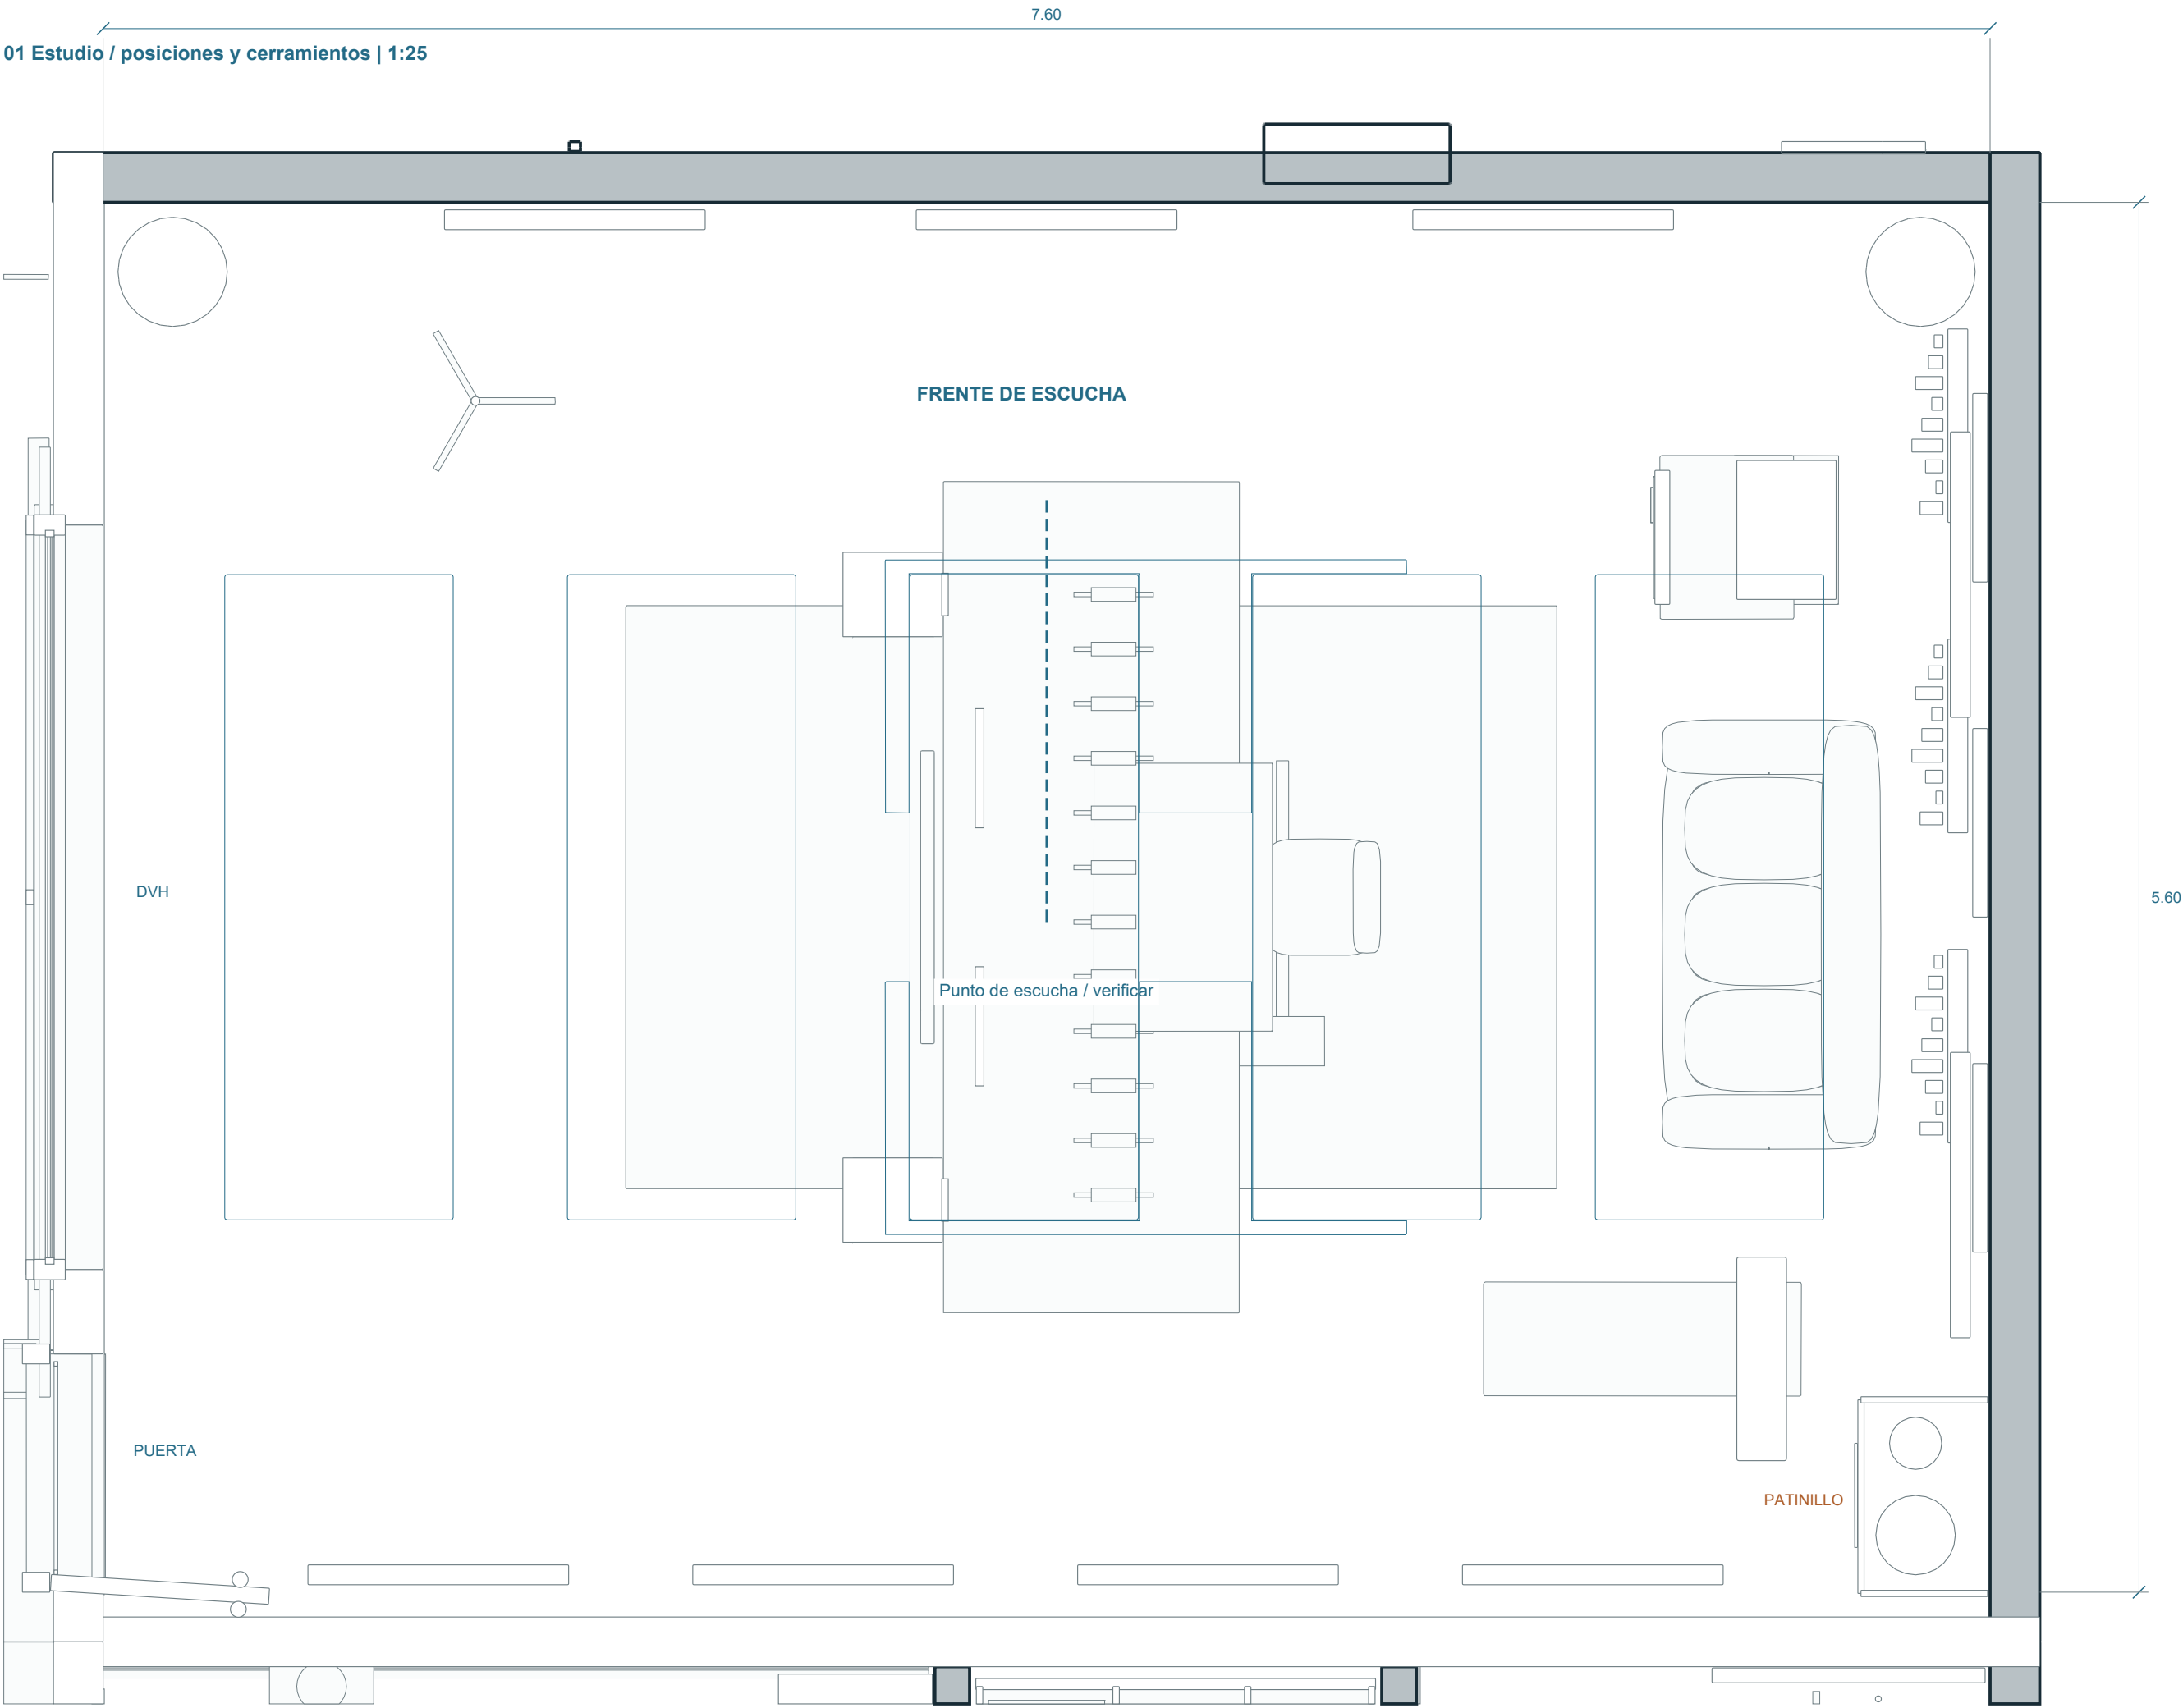

CRITERIO ACUSTICO PROPUESTO

- G: altura libre 3,20 m; cielorraso a +6,45. Paneles y nubes seccionados/coordinados con esa cota.
- P: identificar primeras reflexiones con posicion final de monitores y oidos. El trazado de escucha es una referencia grafica, no un calculo acustico.
- P: definir objetivo de aislamiento, RT60 y ruido de fondo antes de asignar espesores o prestaciones.
- P: sellado perimetral continuo en puerta, DVH y pasos; juntas elasticas y desacople donde el sistema constructivo lo requiera.
- P: ventilacion silenciosa con recorridos atenuados; controlar vibracion y ruido de equipos. No hay sistema de acondicionamiento dimensionado.
- P: patinillo de combustion: definir proteccion termica, separacion, juntas y acceso de limpieza sin comprometer el estudio.

VERIFICACION PENDIENTE

Medicion o simulacion acustica con absorcion real de materiales, volumen util, posiciones definitivas y ruido de instalaciones. No se asignan valores de dB ni tiempos de reverberacion sin evidencia.

Ref.	Pieza medida G	Ancho m	Alto m	Base	Tope
P01i	Corredera PB / vidrio	1.140	2.300	+0.270	+2.570
P01d	Corredera PB / vidrio	1.140	2.300	+0.270	+2.570
P02	Abatible bano mono	0.721	2.150	+0.210	+2.360
P03	Abatible bano piletá	0.821	2.180	+0.210	+2.390
P04	Acceso estudio	0.882	2.540	+3.290	+5.830
P05	Acceso vestidor	0.831	2.180	+3.250	+5.430
P06	Dormitorio	0.821	2.180	+3.250	+5.430
P07	Bano vivienda	0.821	2.180	+3.250	+5.430
V01	DVH estudio / paño	3.000	1.720	+4.060	+5.780
V02	Lateral dormitorio / paño	1.700	2.080	+3.840	+5.920
P08a	Corredera lateral A / vidrio	1.150	2.540	+3.220	+5.760
P08b	Corredera lateral B / vidrio	1.150	2.540	+3.220	+5.760
P09	Corredera posterior A / vidrio	1.275	2.540	+3.220	+5.760
P10	Corredera posterior B / vidrio	1.675	2.540	+3.220	+5.760
H01	Porton / hoja	3.000	2.000	+0.085	+2.085

HERRERIA Y PROTECCION

F: baranda nominal 1,05 m sobre nivel de balcon. G: eje pasamanos lateral +4.30; NPT alto +3.25; diferencia 1.05 m. Medir altura util donde cambie el acabado.

G: postes, barrotes y zancas representados. Separacion de barrotes, resistencia horizontal, soldaduras, placas y anclajes requieren validacion de proyecto.

Escalera: 18 tablas de 1,00 m; avance entre tablas ~211,1 mm. A07 muestra el recorrido y el encuentro de acceso; A14 las piezas de soporte.

Pendiente: cuadro de fabricacion definitivo con materiales, espesores, tratamientos, sellos, drenajes, tolerancias y accesorios del fabricante.

LECTURA DEL CUADRO

Las dimensiones son de hoja o vidrio nombrado. No equivalen automaticamente al vano de obra ni al paso libre.


Los marcos, burletes y herrajes amplian o reducen las dimensiones utiles. Ver cotas entre jambas en plantas.

G: DVH con dos paños de vidrio; espesor y separacion segun modelo. Prestaciones y composicion final por especificar.

P08/P09/P10: correderas vivienda; replantear rieles, solapes, desagues y retenedores a partir del vano real.

Porton: hoja 3,00 m; paso libre 2,75 m; carrera 3,05 m. No modificar pilares silenciosamente.


D01 Alero estudio / X=17,80 | 1:5

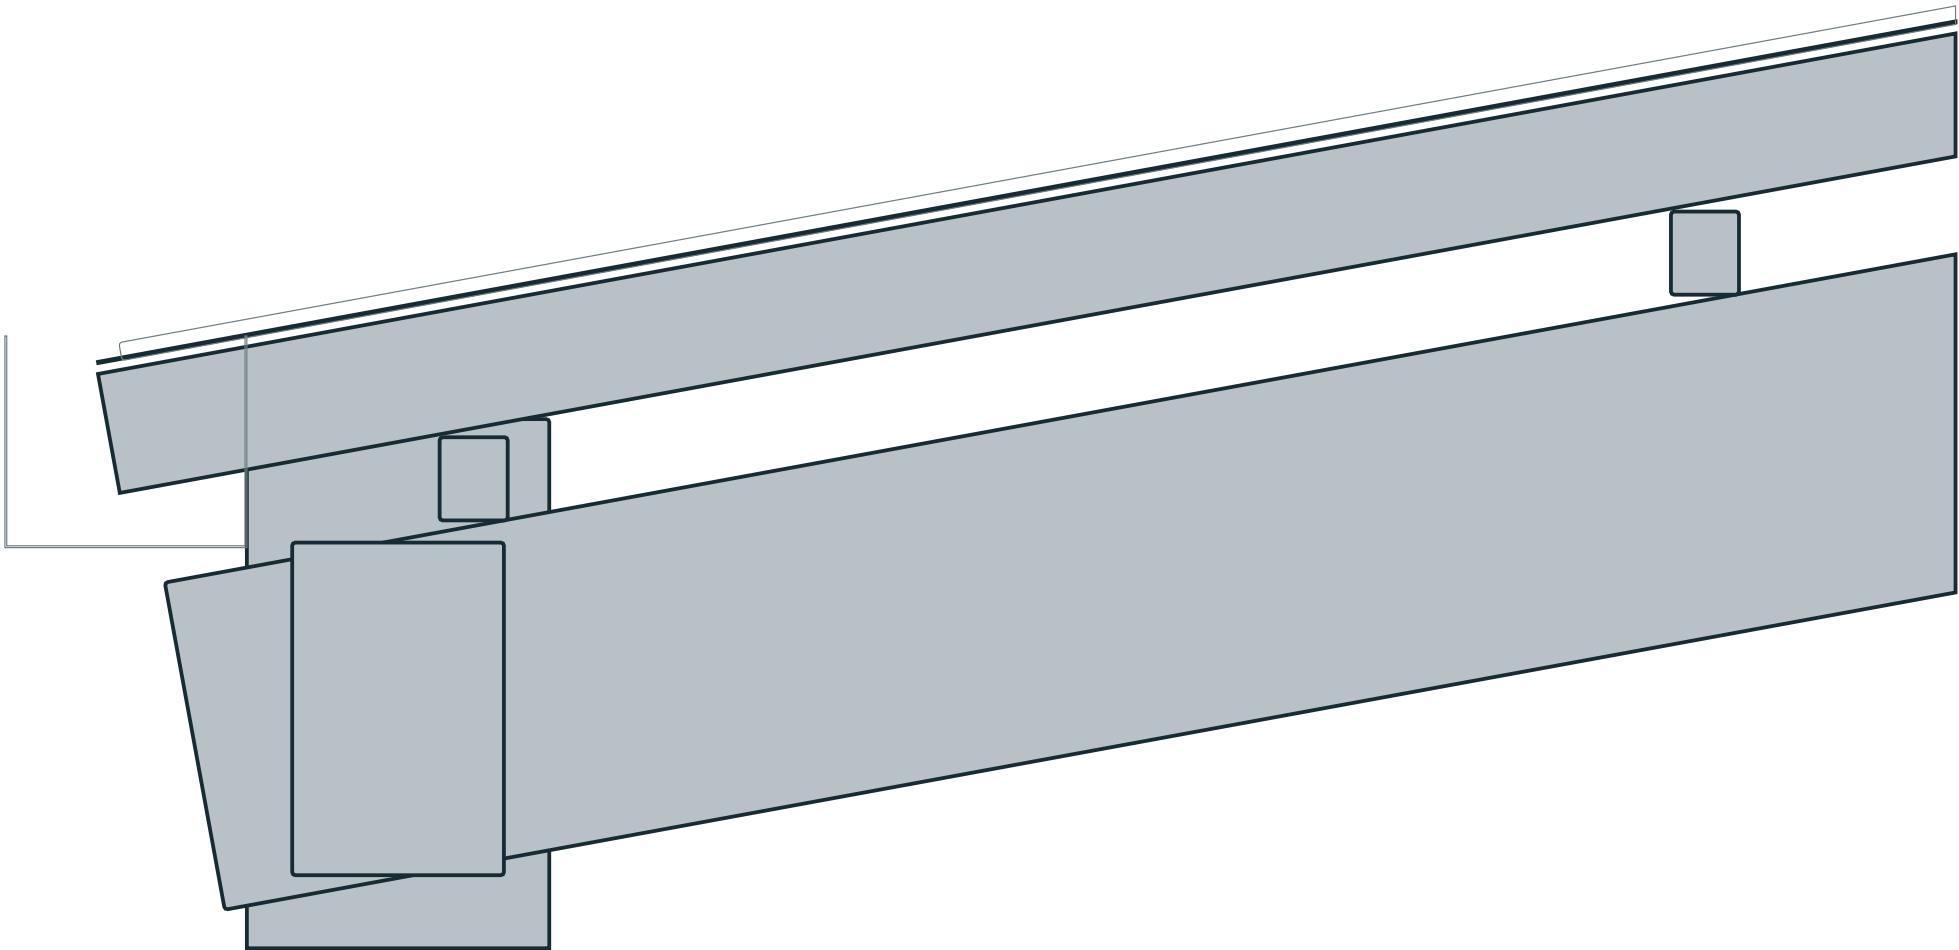

CAPAS Y GESTION DEL AGUA

- G: cubierta metalica, aislacion representada de 80 mm, revestimiento inferior y cabios/correas. La seccion corta las piezas de la malla a su escala real.
- P: chapa nominal 0,8 mm, fijaciones con sellos, continuidad y solape de membrana, goteron y conexion a canaleta deben confirmarse con el sistema constructivo.
- P: babeta/contrababeta del salto, retorno de membrana y sellos alrededor de conductos deben formar un drenaje continuo. Dimensionar solapes y fijaciones segun exposicion.
- P: validar condensacion, viento, dilatacion y puentes termicos con datos climaticos y especificaciones definitivas.


D02 Escalon cubiertas / X=17,80 | 1:5

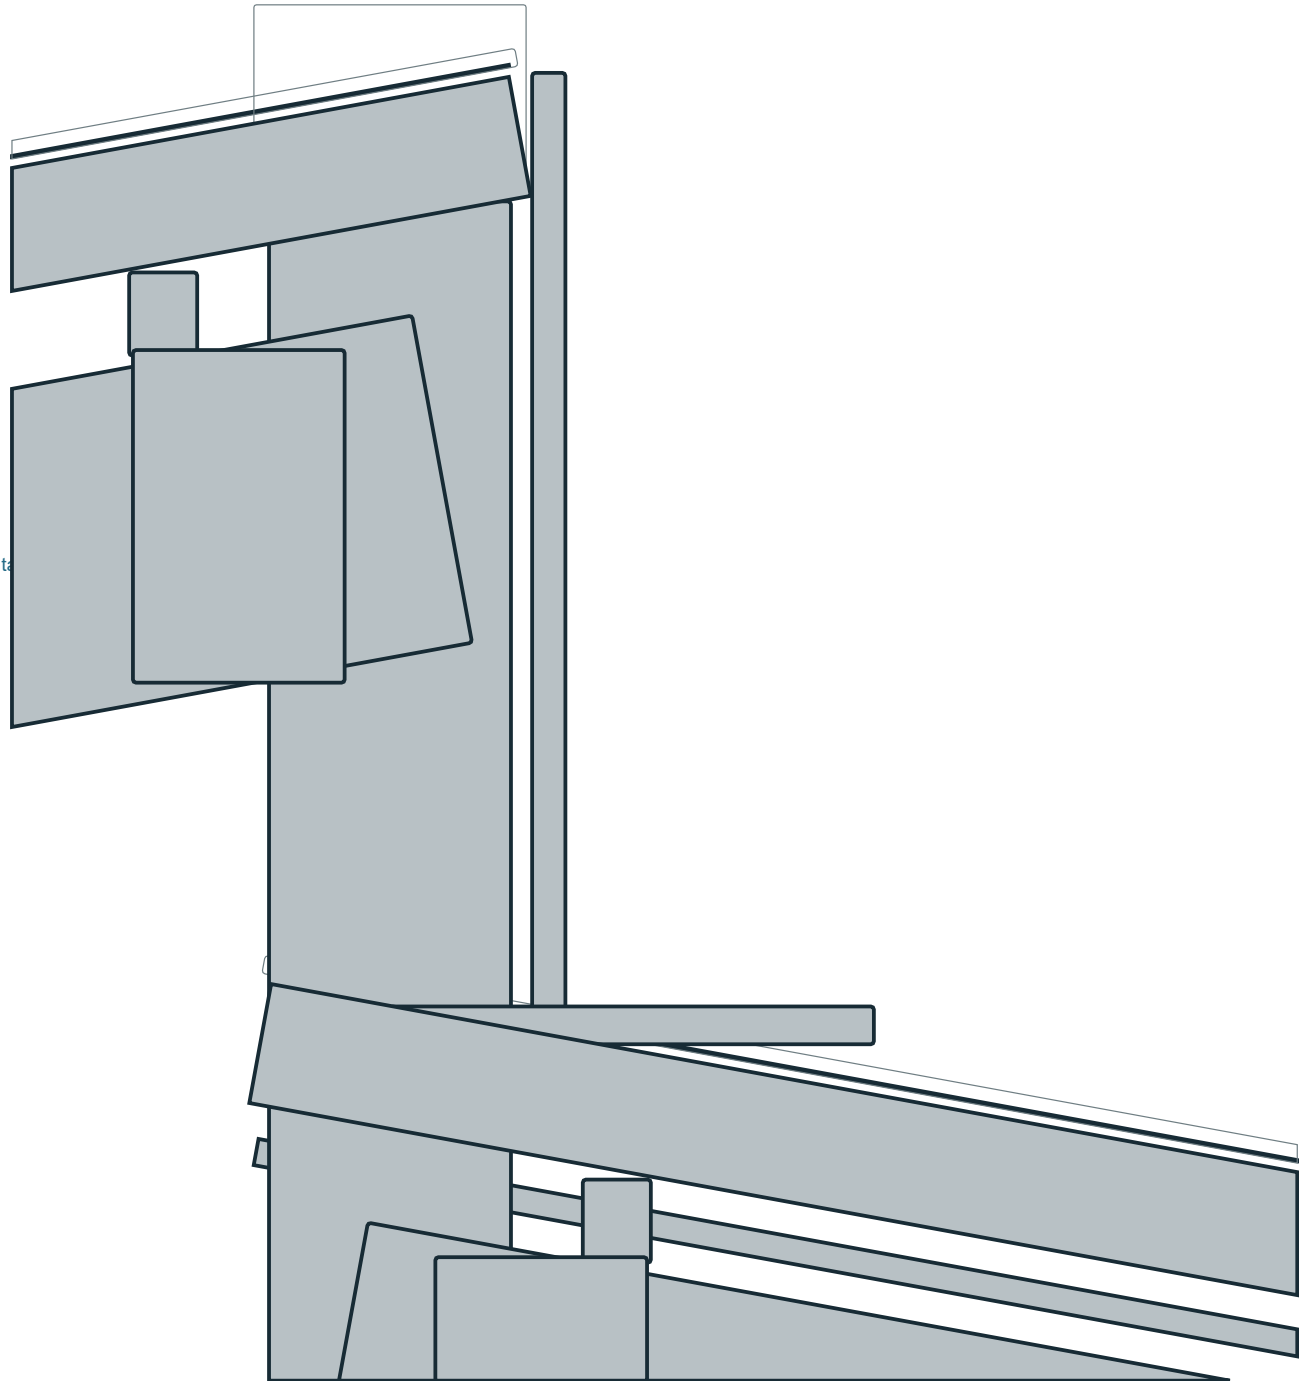

DVH, UMBRALES Y BALCON

- D03: umbral estudio ampliado en A07. D04: borde de balcon y anclaje en A14. D05-D07 en A13b.
 - P: junta perimetral con respaldo y sello compatible; apoyo y calzos de vidrio, drenaje del marco, continuidad de aislacion e impermeabilizacion.
- Estos textos describen decisiones por desarrollar; no sustituyen piezas ausentes del modelo ni especificaciones de fabricante.

D05 Canaleta abierta / X=14,00 | 1:2

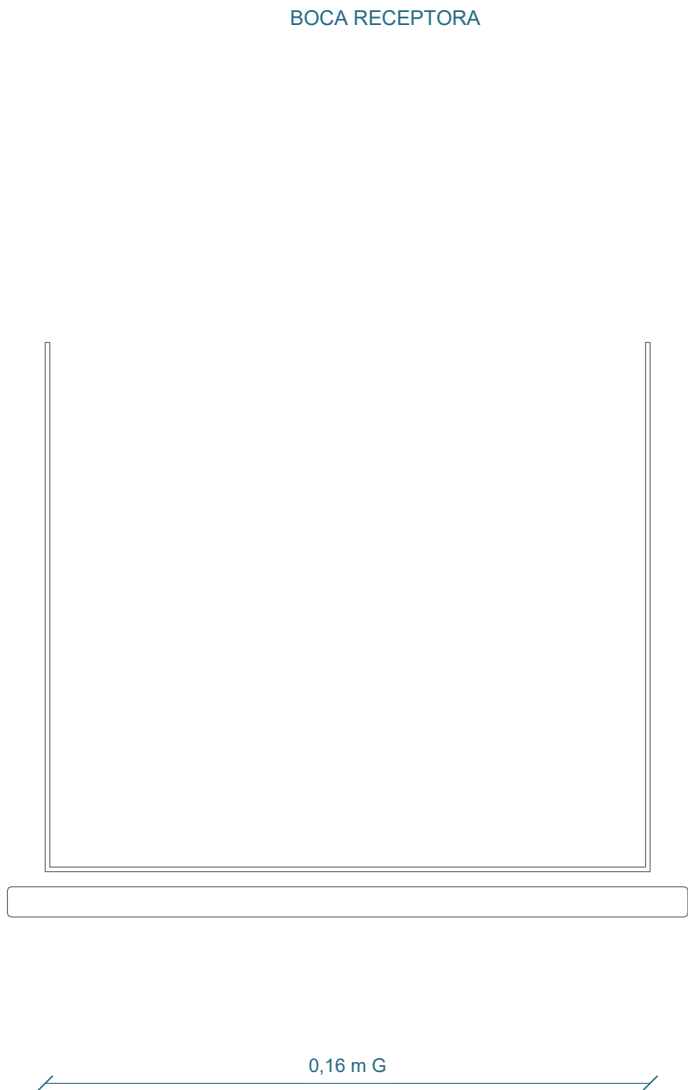


D05 CAPTACION / FIJACION

G: sección de canaleta recortada directamente de la malla. Verificar apertura superior, fondo, salida lateral y continuidad en la prueba del modelo.

P: pendiente longitudinal, caudal, fijación y sellos requieren dimensionado; el ancho gráfico no certifica capacidad pluvial.

D06 DVH / antepecho / Z=3,00 | 1:5

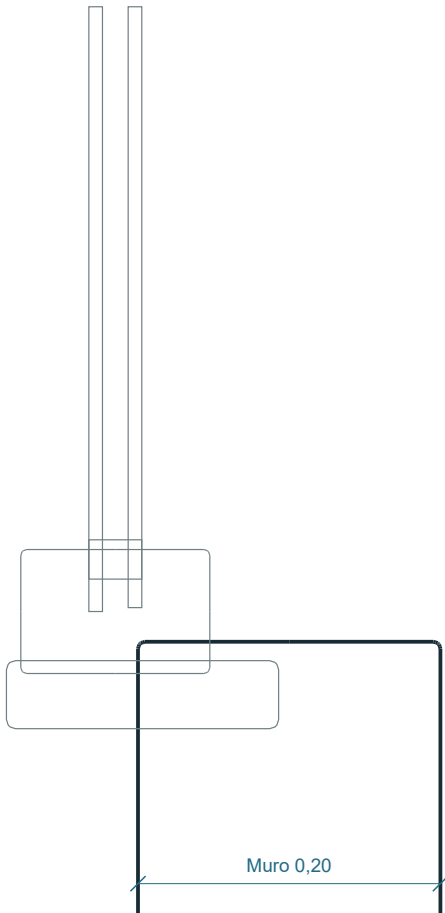


D06 ENCuentro de VENTANA

G: dos paños, marco, antepecho y alféizar representados. La ampliación permite revisar solapes y contacto.

P: definir calzos de apoyo, sellos perimetrales, drenaje del marco y conexión de aislamiento sin bloquear las salidas.

Ver A12 para anchos, alturas y cotas de cada pieza.

D07 Paso de conductos / X=21,50 | 1:5

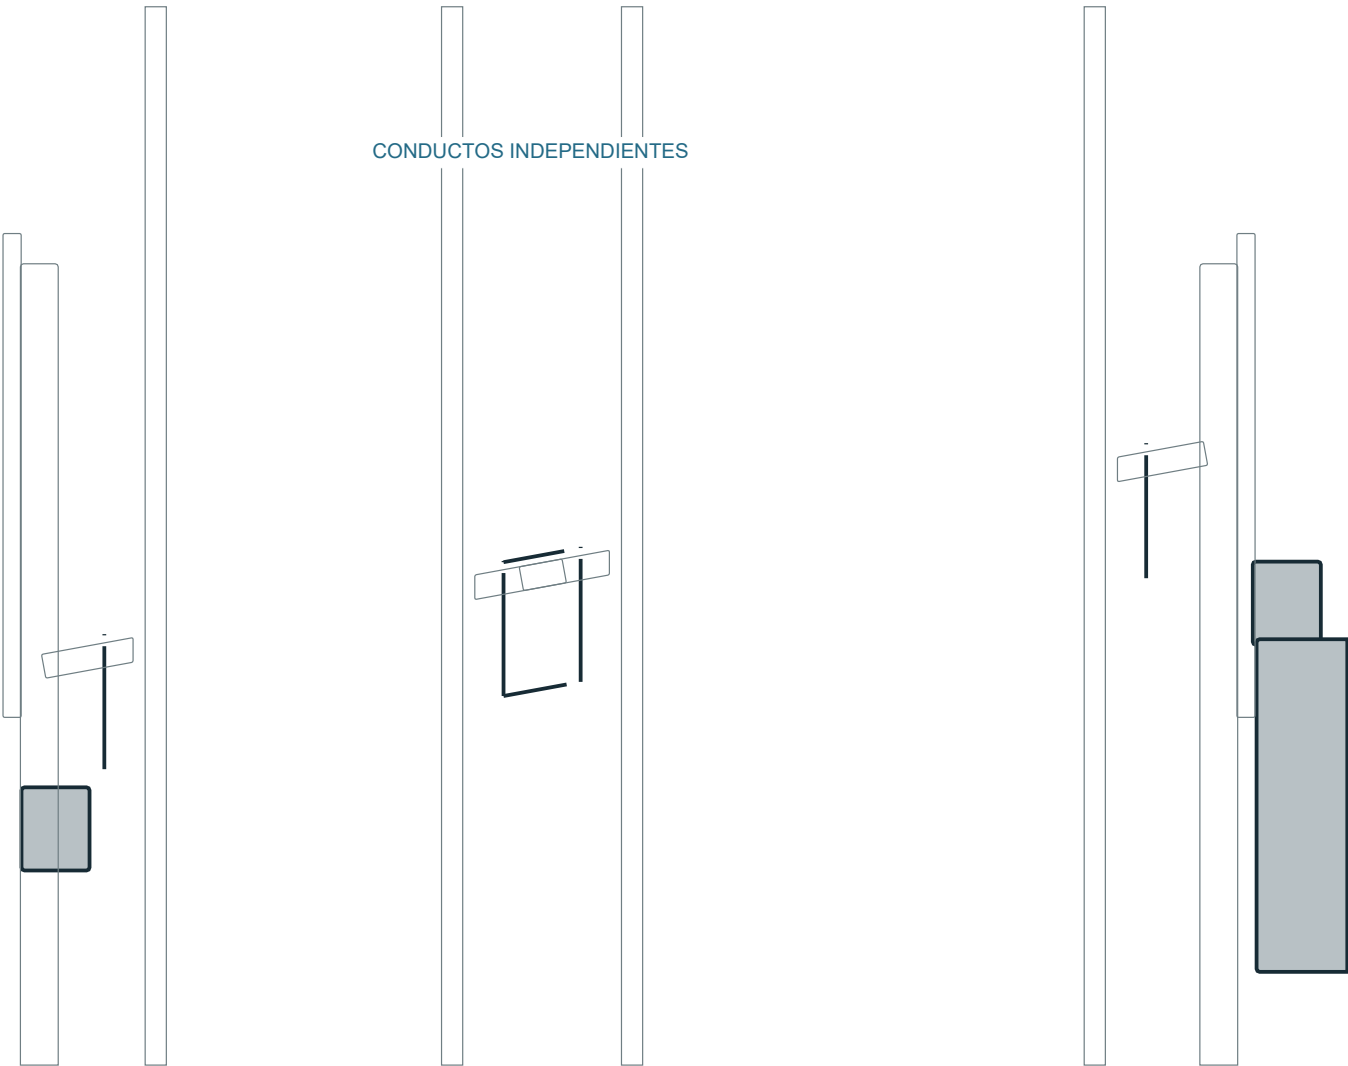


D07 PENETRACION / PATINILLO

G: conductos independientes, babetas perforadas y remate de patinillo. Se muestra la intersección con cubierta.

P: continuidad de membrana, cuello y contrababetas, dilataciones, aislamiento térmico y acceso de limpieza por especificar.

No se asignan distancias reglamentarias a combustibles ni caudales sin proyecto de combustión.


01 Planta de apoyos y líneas estructurales | 1:50

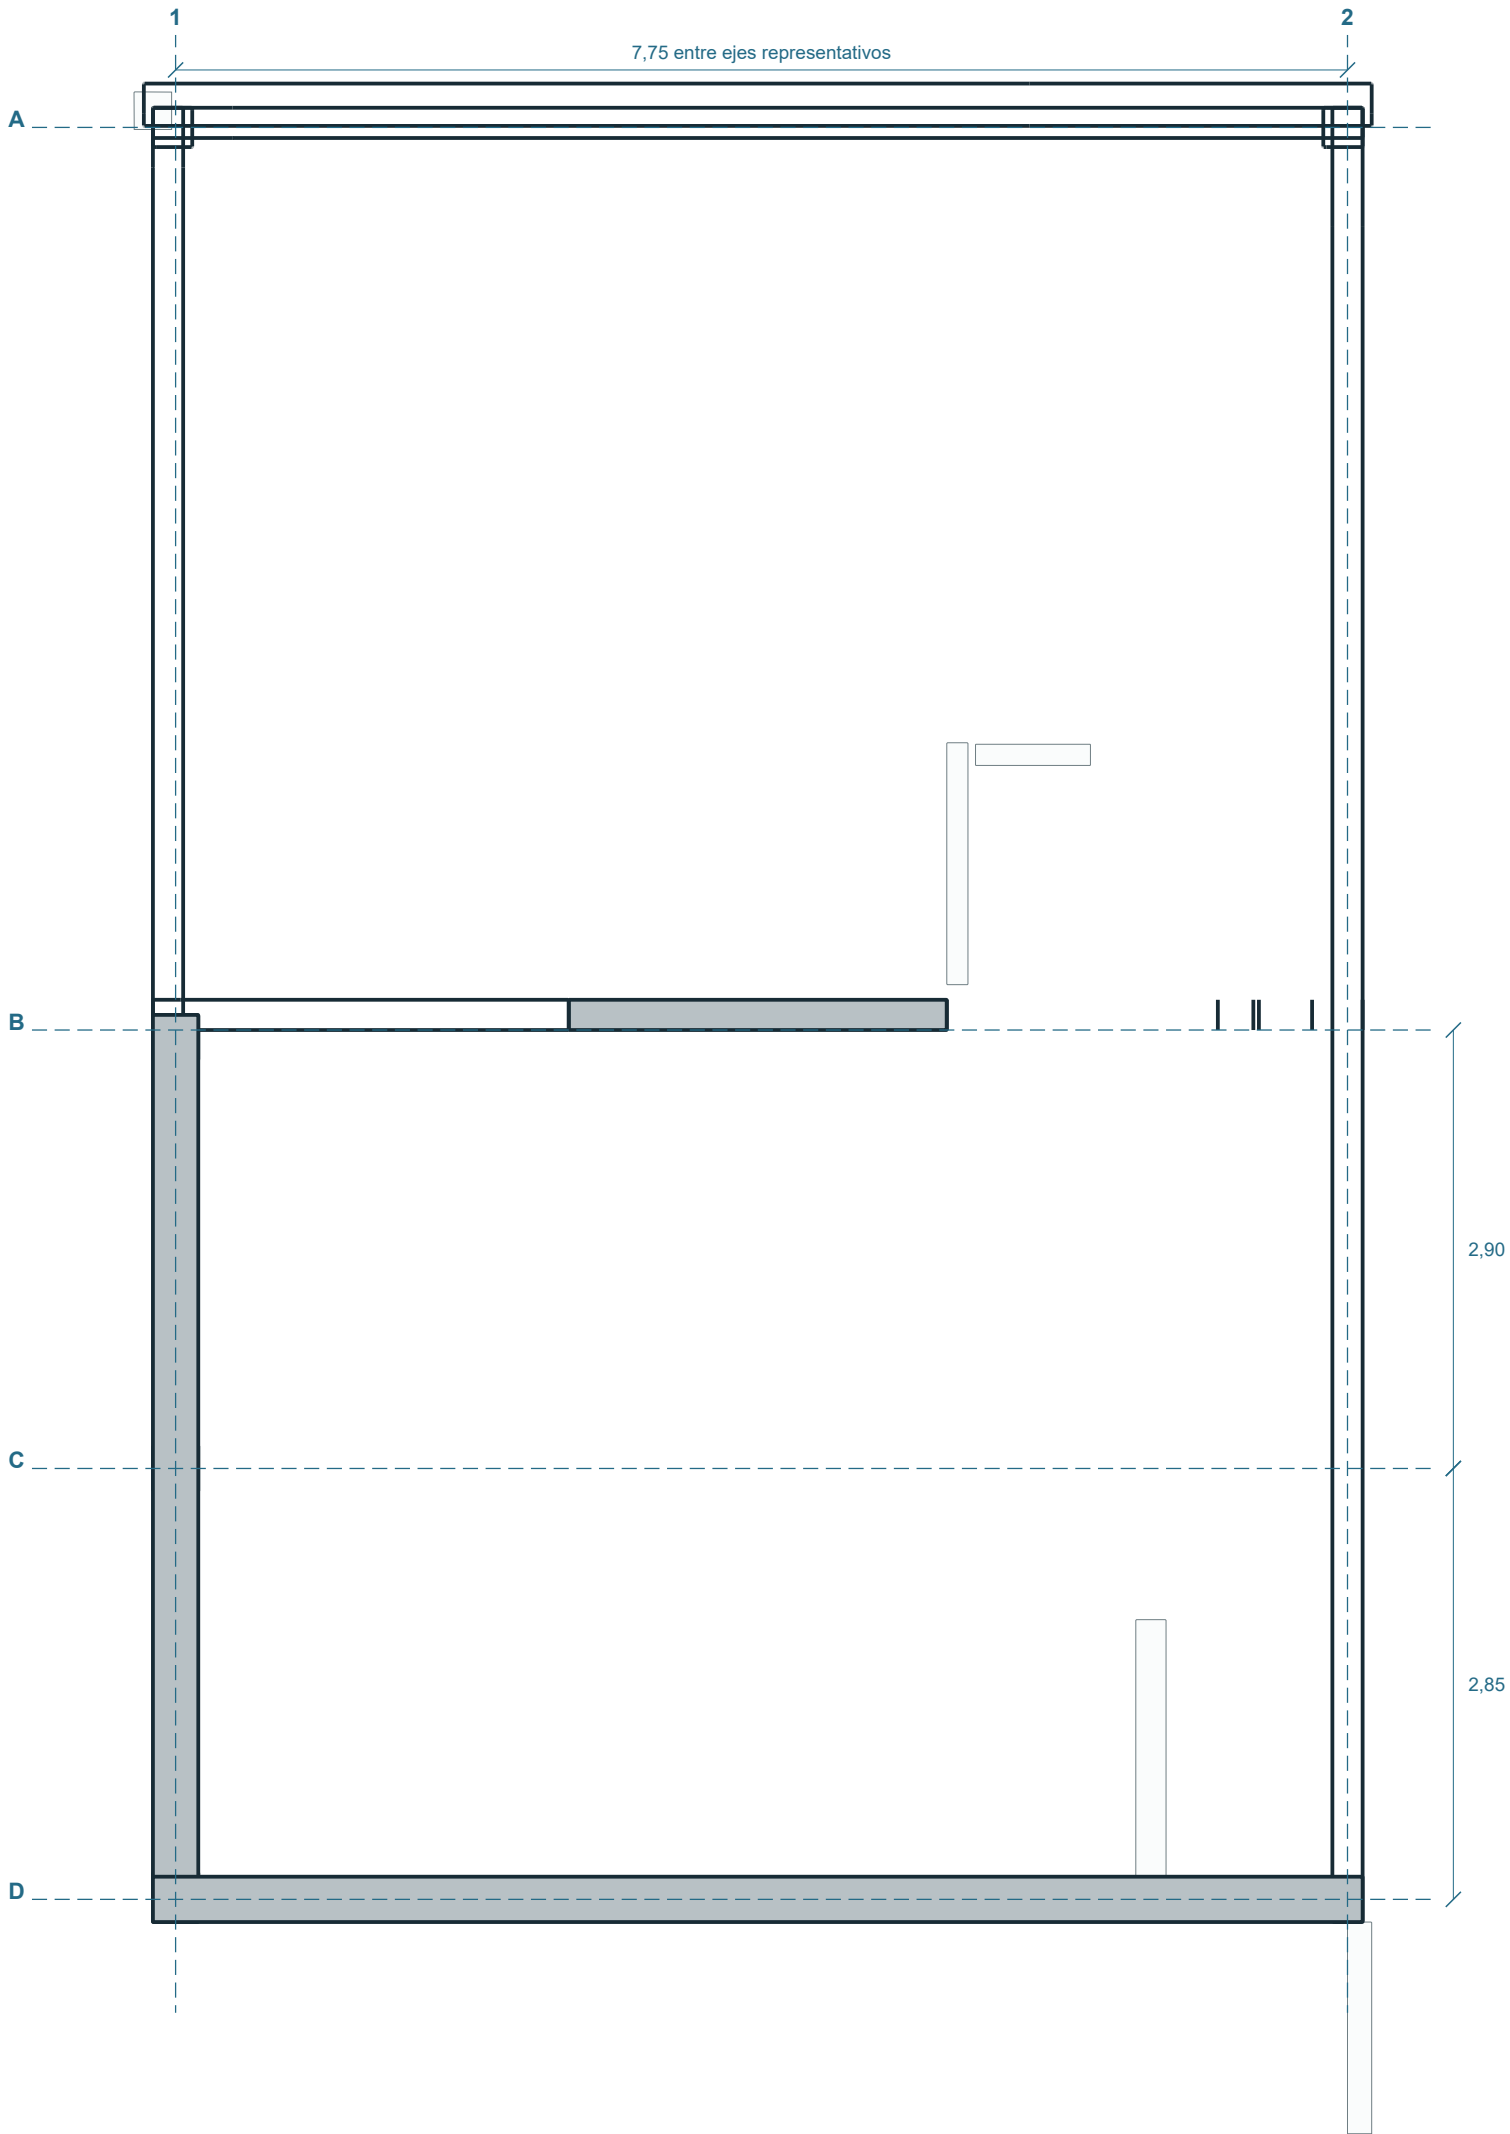

CAMINO DE CARGAS A VALIDAR

- Cubierta: chapa / aislacion -> correas -> cabios -> vigas de apoyo -> cerramientos / apoyos inferiores.
- Entrepiso: losa de 0,20 m -> muros y vigas / columnas representados -> fundacion por proyectar.
- Quincho: columnas 0,30 x 0,30 m y vigas de 0,30 x 0,36 m representadas. Son secciones de malla, no un dimensionado estructural.
- Balcones: proyeccion 1,00 m; verificar voladizo, continuidad y anclaje con la losa. No se infieren armaduras.
- Escalera: dos zancas y apoyos de peldaños; definir placas, soldaduras, bulones y anclajes superior/inferior con calculo.
- Fundaciones ausentes de la fuente: tipo, profundidad, armaduras y capacidad del terreno pendientes de estudio geotecnico y proyecto profesional.


D04 Balcon / baranda / Z=9,00 | 1:20

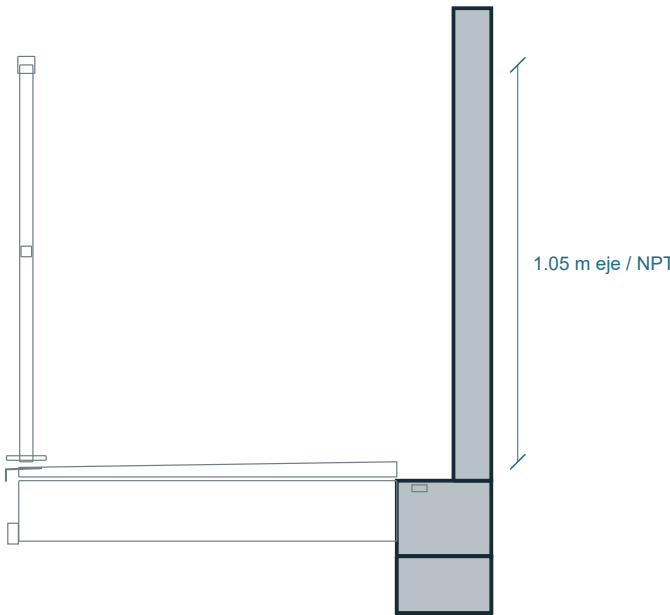

UNIONES

- El corte documenta las piezas presentes y sus apoyos aparentes.
- Los anclajes no se consideran resueltos por estar dibujados: validar sustrato, borde, profundidad y solicitudes.
- Acero/hormigon: especificar corrosion, drenajes y juntas.

01 Coordinacion general / PB | 1:100

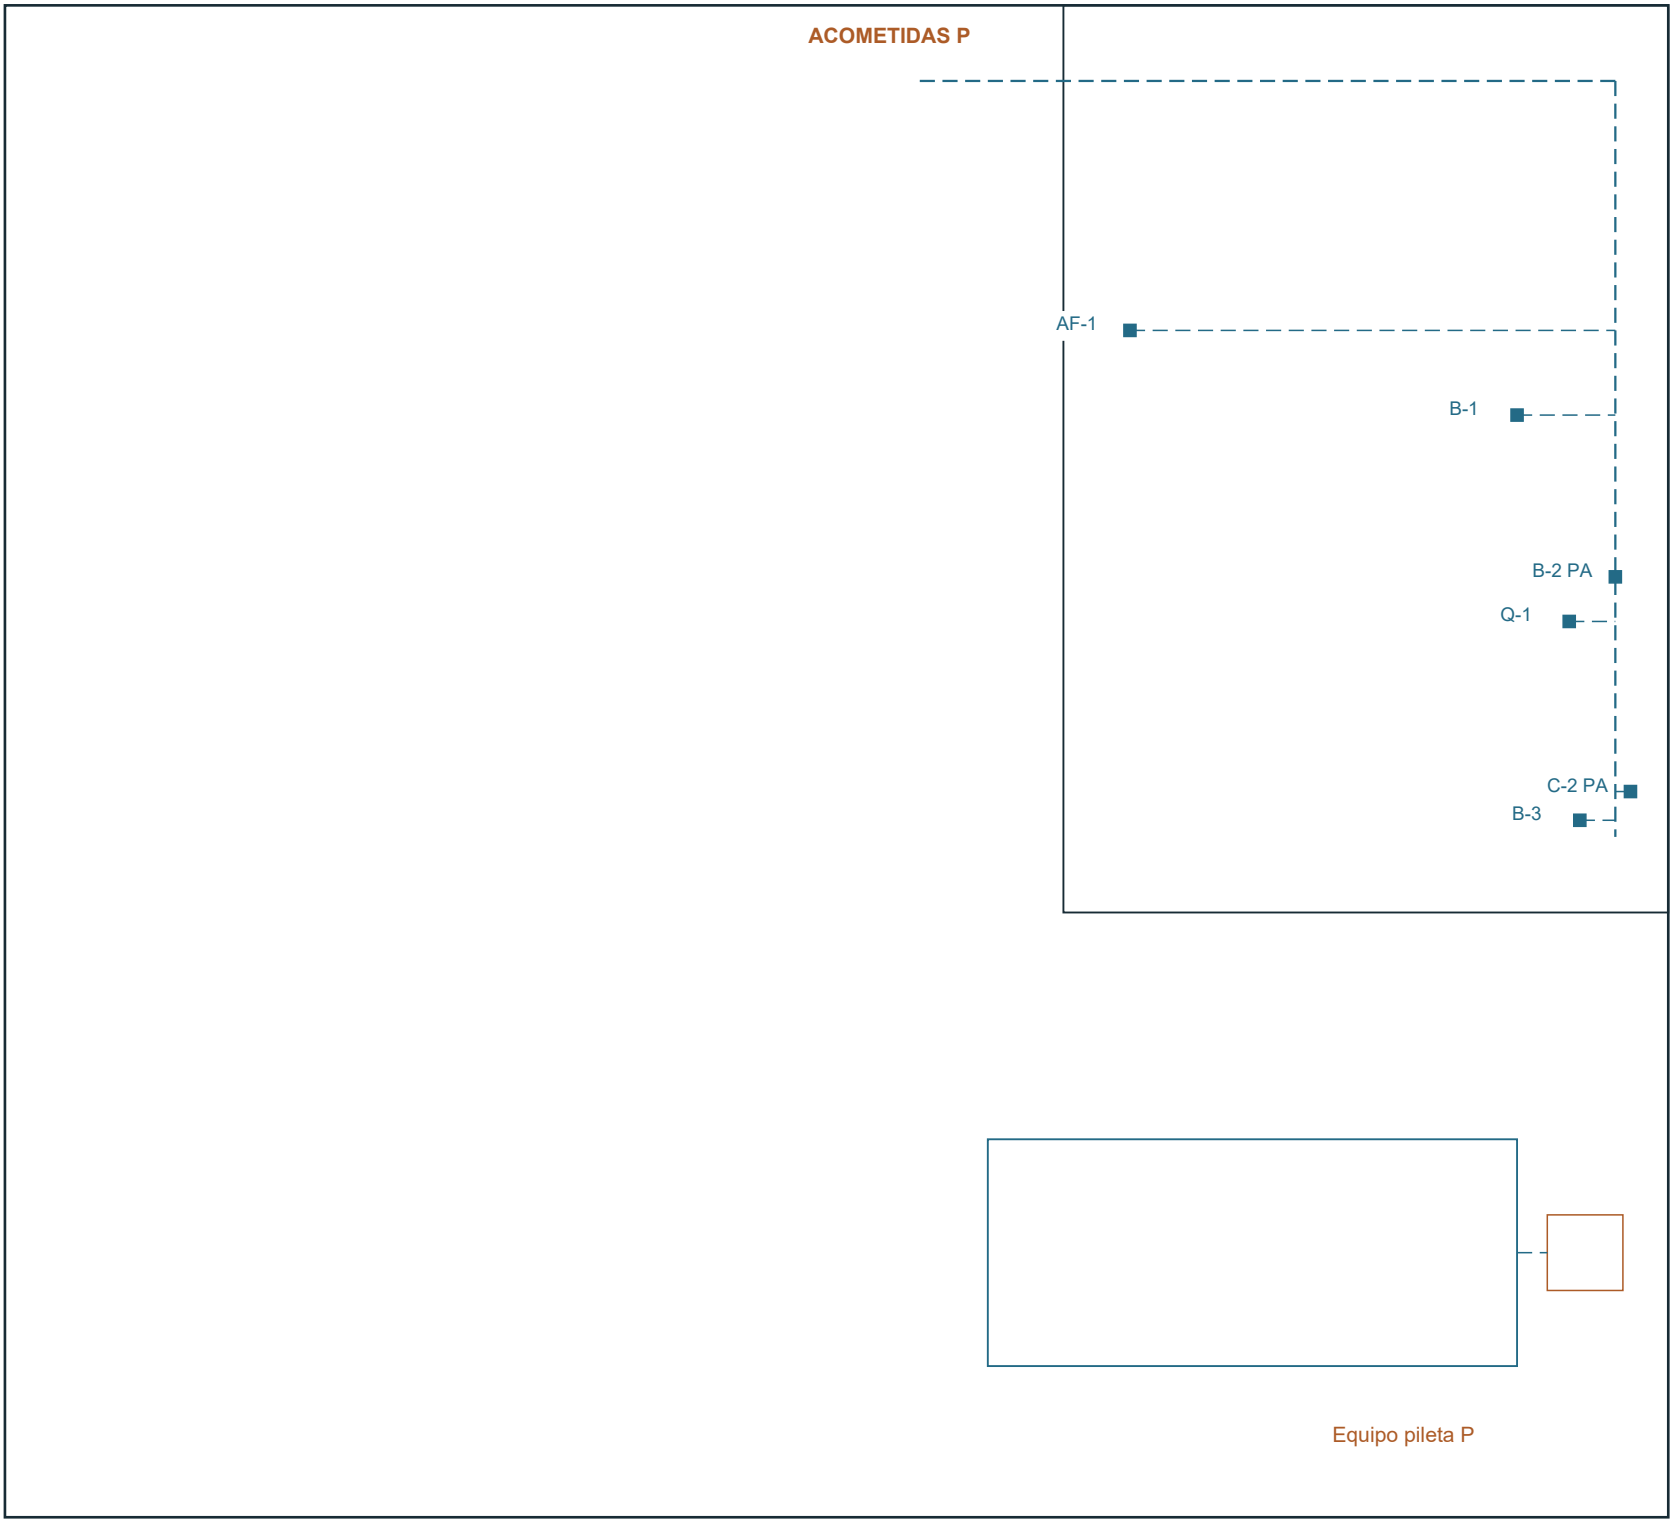

CRITERIO DE COORDINACION: localizar consumos y cruces antes de dimensionar redes. Sin cotas de servicio ni calculos no se presenta este esquema como instalacion completa o certificada.

AGUA / DESAGUE / PLUVIAL

AF-1 cocina mono; B-1 baño mono; Q-1 quincho; B-3 baño pileta; B-2 baño PA; C-2 cocina PA. Nodos sobre equipos reales del modelo.

Las líneas punteadas son relaciones funcionales, no tuberías ejecutivas. Recorridos, diámetros, pendientes, ventilaciones, registros y acometidas se definen con el proyecto sanitario.

Pluvial: captacion y bajadas en A04. Destino final de descarga propuesto; red y cota de conexion exactas pendientes.

Pileta P: skimmer / toma de fondo -> prefiltro / bomba -> filtro -> retornos. Prever valvulas, vaciado, renovacion y medidas de seguridad; equipo y tuberías por calcular.

ELECTRICIDAD / ILUMINACION / EXTRACCION

Servicios de red disponibles segun propietario. Tablero y medidor propuestos junto al acceso; ubicacion final segun prestador.

P: separar circuitos de iluminacion, tomas generales, cocinas, pileta y estudio. Definir potencias, protecciones, puesta a tierra y equipotencialidad.

G: luminarias representadas no equivalen a calculo luminotecnico ni conexion electrica.

G: conductos de horno, parrilla y cocina presentes. Ver A10: caudal, limpieza, aislamiento y reposicion de aire pendientes.

P: ventilacion sanitaria y acondicionamiento del estudio sin dimensionar. Coordinar penetraciones para mantener continuidad termica, acustica y de agua.

Area / pieza	m2	Metodo / alcance
Lote nominal F	440.00	22,00 x 20,00; limites nominales
Huella casa F	96.00	8,00 x 12,00; incluye quincho
Dos niveles nominales F	192.00	192 m2 brutos geometricos; no computo legal
Vaso pileta F	21.00	7,00 x 3,00 nominal
Borde pavimentado F	24.00	Anillo de 1,00 m nominal
Piso estudio G	41.74	Proyeccion real de la pieza; puede solapar otras
Piso vivienda G	41.89	Proyeccion real de la pieza; puede solapar otras
Piso monoambiente G	43.21	Proyeccion real de la pieza; puede solapar otras
Piso baño mono G	4.26	Proyeccion real de la pieza; puede solapar otras
Piso baño vivienda G	5.28	Proyeccion real de la pieza; puede solapar otras
Piso quincho G	47.99	Proyeccion real de la pieza; puede solapar otras
Piso baño quincho G	2.61	Proyeccion real de la pieza; puede solapar otras
Balcón lateral G	6.00	Proyeccion real de la pieza; puede solapar otras
Balcón posterior G	8.98	Proyeccion real de la pieza; puede solapar otras
Descanso escalera G	1.00	Proyeccion real de la pieza; puede solapar otras

FUENTES Y REVISION

F: source/scene.json, configuracion y geometria original. Coordenadas fuente X / Z horizontal; Y altura. Blender X / -Z / Y.

F: docs/DECISIONES.md: estudio 3,20 m libres, vivienda 2,60 m y video pausado.

G: modelo Casa_de_Campo_95_Pass1c.blend; SHA256 fba22fb65c02f4e82e400abb...

G: extraccion de mallas evaluadas a cuadro 150, con puertas en su pose de documentacion. Los detalles omiten microgeometria menor para permitir lectura.

P: desarrollos constructivos y sistemas inferidos se identifican en sus hojas. No se presentan como verificacion profesional.

Las superficies de piezas no son utiles netas de recintos. Existen superposiciones: no sumar pisos de banos a pisos generales sin descontar intersecciones.

PENDIENTES PARA EMISION FINAL

Mensura y topografia; servicios y cotas exactas; suelos; calculo de estructura, instalaciones, seguridad, clima y acustica.

Cierre de observaciones de la auditoria y coherencia con modelo / visor congelados. Umbral critico 9,5 y realismo fotografico siguen siendo condiciones de entrega.

ARCHIVOS: un PDF multipagina vectorial A2; un SVG y un DXF por lamina; geometria.json de extraccion; manifest.json de versiones; verification.json de controles. Los DXF contienen las vistas metricas separadas y cotas; la cartela completa se conserva en PDF/SVG.