

LA PROPIEDAD COMPLETA, EN UNA MISMA VERSION

Plantas, fachadas, cortes y detalles extraídos del archivo Blender indicado en cada cartela. Las anotaciones distinguen fuente dimensional, geometría medida y propuestas pendientes.

Hoja	Contenido	Escala
A01	Implantacion, paisaje y perimetro	1:100 / 1:50
A02	Planta baja y vanos	1:50
A03	Planta alta, estudio y vivienda	1:50
A03b	Vivienda / uso y recorridos	1:25
A04	Cubiertas y coordinacion pluvial	1:50 / esquema
A05a / A05b	Cuatro fachadas	1:50
A06	Cortes generales A-A y B-B	1:50
A07	Escalera, descanso y acceso	1:20 / 1:5
A08	Pileta y bordes	1:25
A09	Banos: plantas y elevaciones	1:20 / 1:25
A10	Quincho y cocinas	1:25 / 1:50
A10b	Monoambiente: uso y cotas G	1:25 / 1:20
A11	Estudio y tratamiento acustico	1:25 / 1:50
A12	Carpinterias y herreria	Cuadros / 1:25
A13 / A13b	Encuentros de envolvente	1:5 / 1:10
A14	Estructura conceptual	1:50 / 1:10
A15	Instalaciones coordinadas	1:100 / esquemas
A16	Superficies, decisiones y trazabilidad	Cuadros
D01-D11	Suplemento G/P (incluye D05b)	1:1 a 1:50
D13 / D14	Uso MIDI e isla / apoyo y recorridos	1:5 / 1:10 / 1:20


COMO LEER ESTE JUEGO

- F - Fuente: cotas expresas del HTML original y decisiones del propietario.
- G - Geometria: medida derivada de la version Blender identificada por SHA256. No equivale a un relevamiento de obra.
- P - Propuesta: coordinacion o solucion grafica inferida. Validar antes de construir.
- Niveles referidos al cero del modelo. No hay relevamiento altimetrico ni mensura catastral.
- Ubicacion: Virrey del Pino, Partido de La Matanza, Buenos Aires. Norte orientativo segun propietario: con la calle arriba, abajo a la izquierda.
- Servicios de red disponibles segun propietario. Posiciones, cotas y condiciones exactas de acometida pendientes.
- Escalas fisicas para impresion al 100 %. DXF en metros; cada vista se separa horizontalmente en espacio modelo.

JERARQUIA GRAFICA

- 0,50 mm: contorno de piezas cortadas. Relleno gris: material seccionado.
- 0,18 / 0,13 mm: proyecciones, mobiliario y contexto.
- Azul: cotas, niveles, referencias y criterios de coordinacion.
- No constituye proyecto ejecutivo ni calculo estructural, sanitario, electrico o acustico.


01 Implantacion general | 1:100

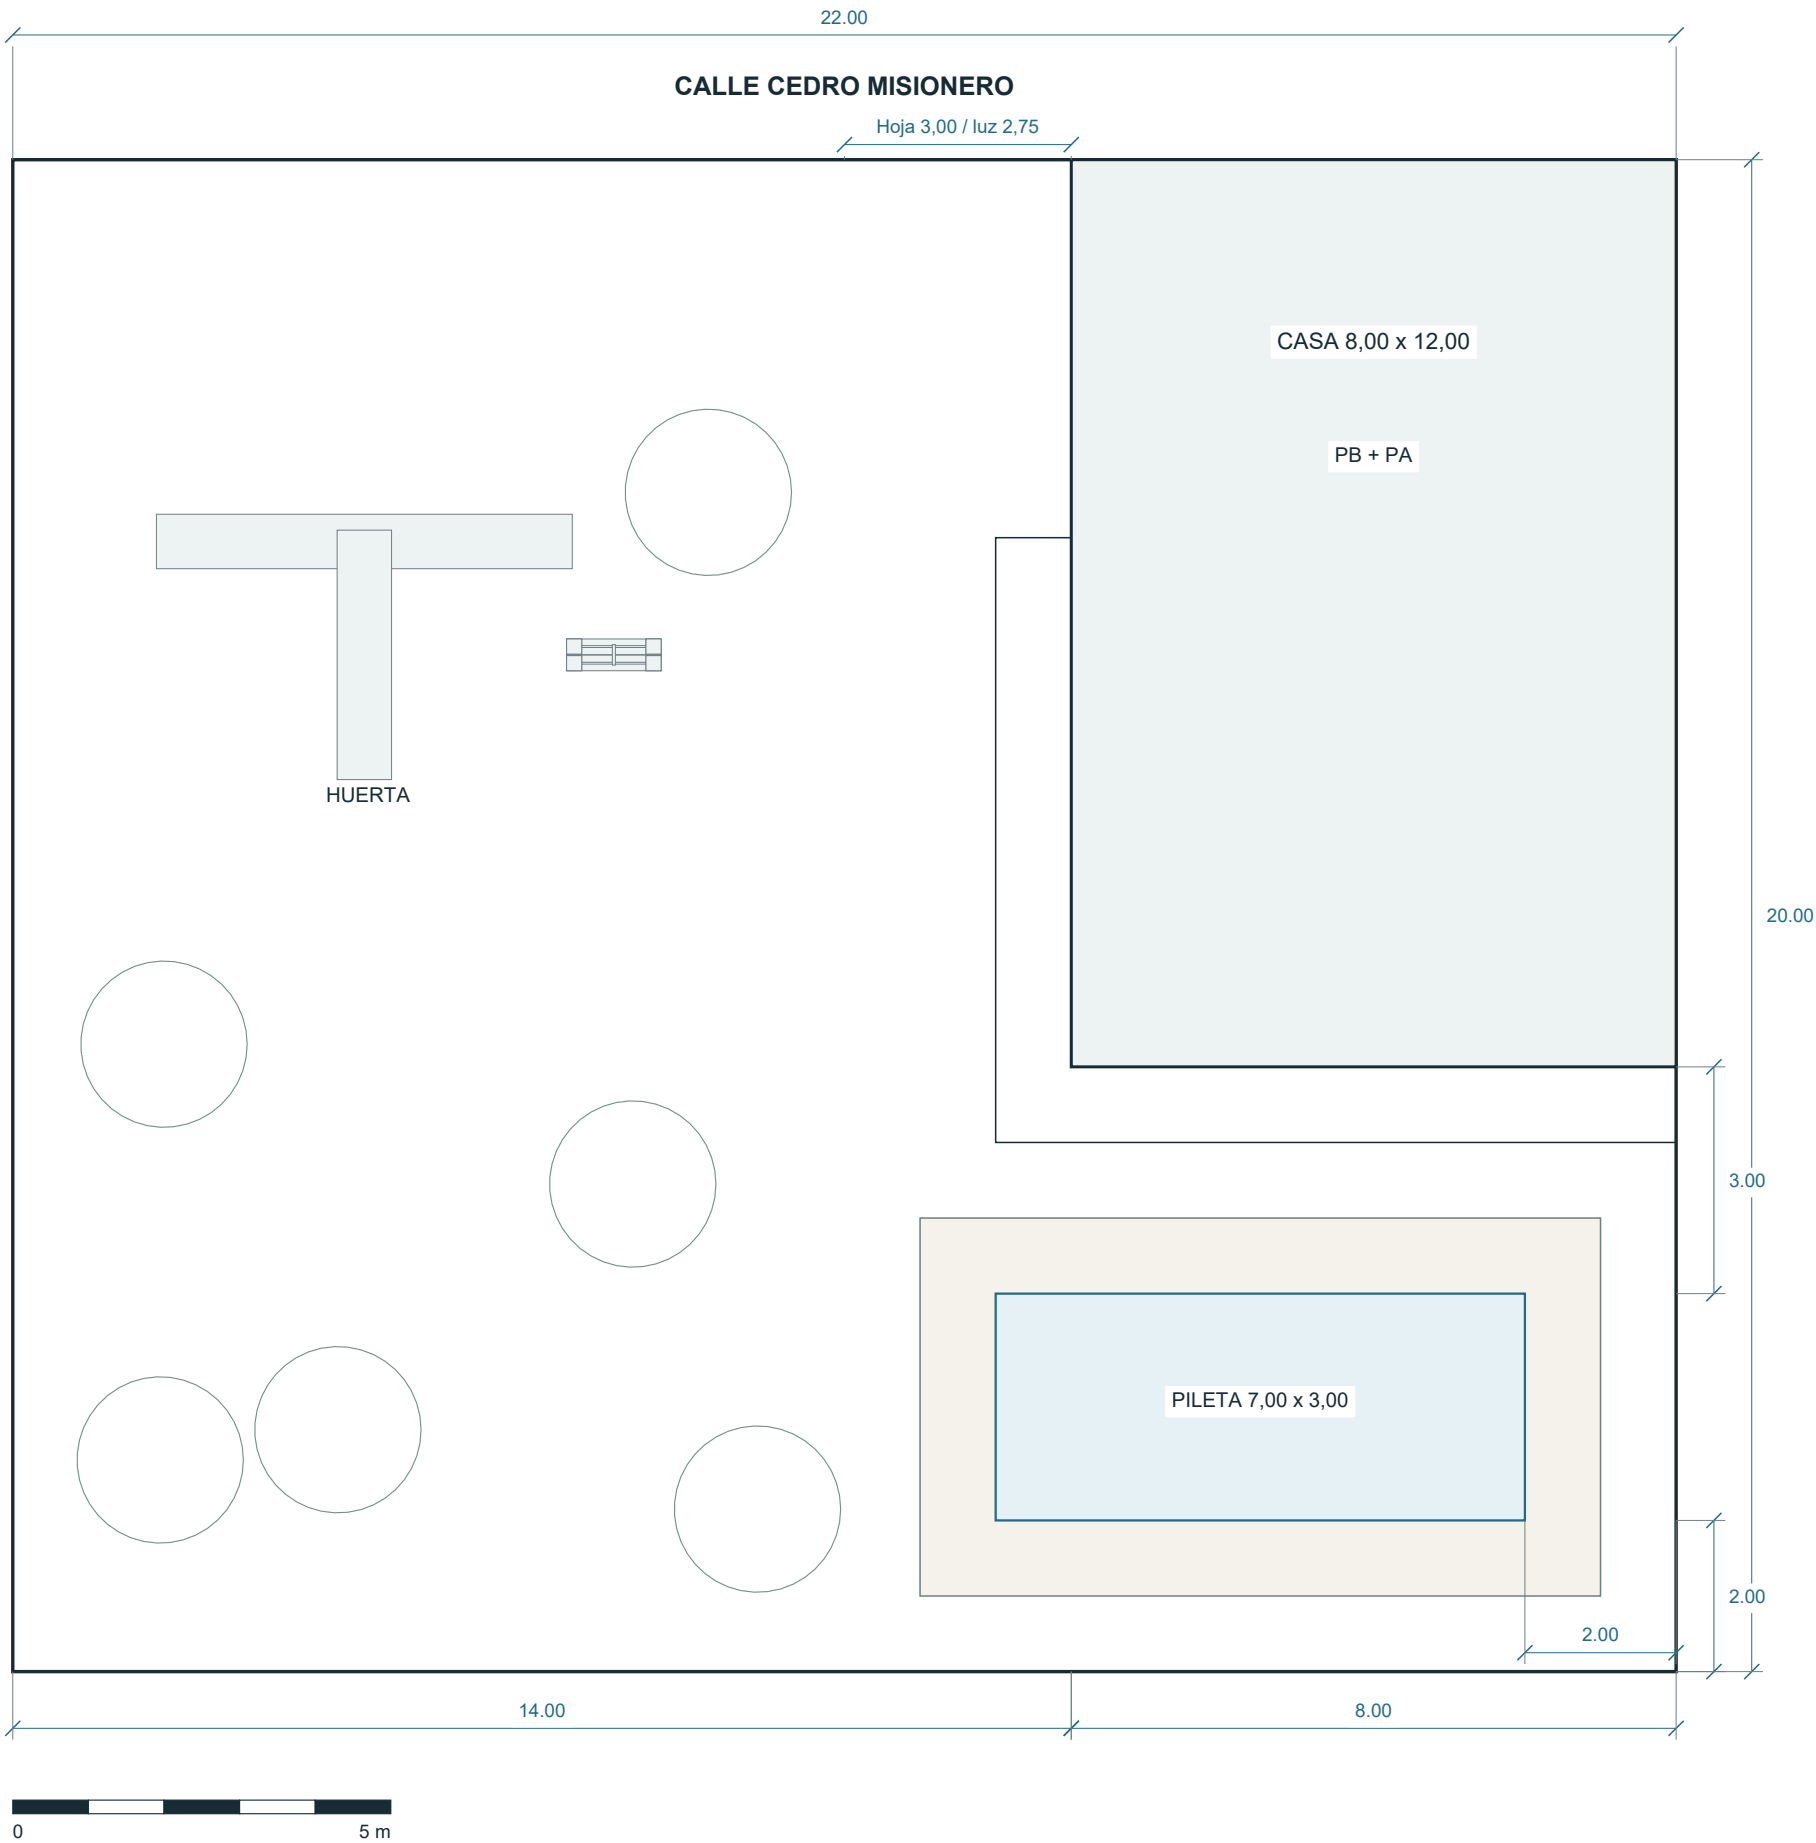

IMPLANTACION CONSERVADA


- F: lote nominal 22,00 x 20,00 m. Casa X=14,00; Z=0,00. Dos modulos de 6,00 m.
- F: pileta X=13,00; Z=15,00. Distancias nominales del vaso: 2,00 m al fondo y 2,00 m al lateral derecho.
- F: borde pavimentado de 1,00 m; huerta y centros de los seis arboles de fuente conservados.
- G: cotas de pavimentos se detallan en A02, A07 y A08. Rasante general del terreno por relevar.
- G: porton de hoja 3,00 m, luz entre pilares 2,75 m y carrera 3,05 m. No confundir hoja con paso libre.

02 Huerta y caminos | 1:50

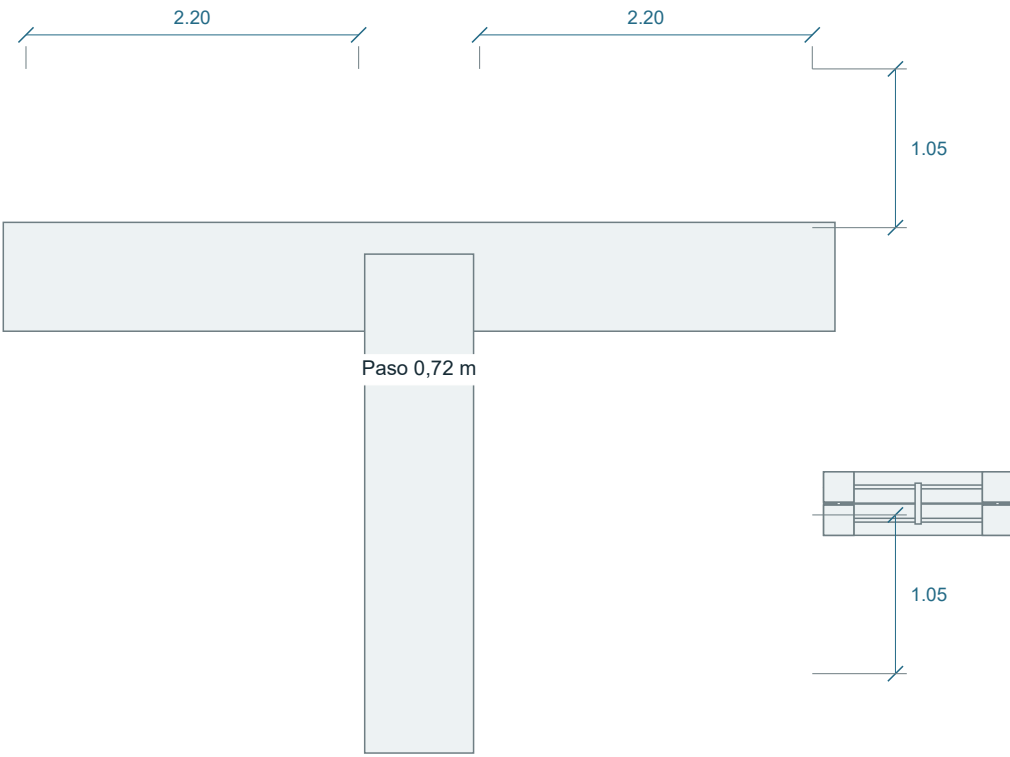

Perimetro y desniveles: confirmar mensura, cotas de terreno y drenajes exteriores. El norte grafico refleja la referencia del propietario y no un azimut topografico.

01 Planta baja amoblada | 1:50

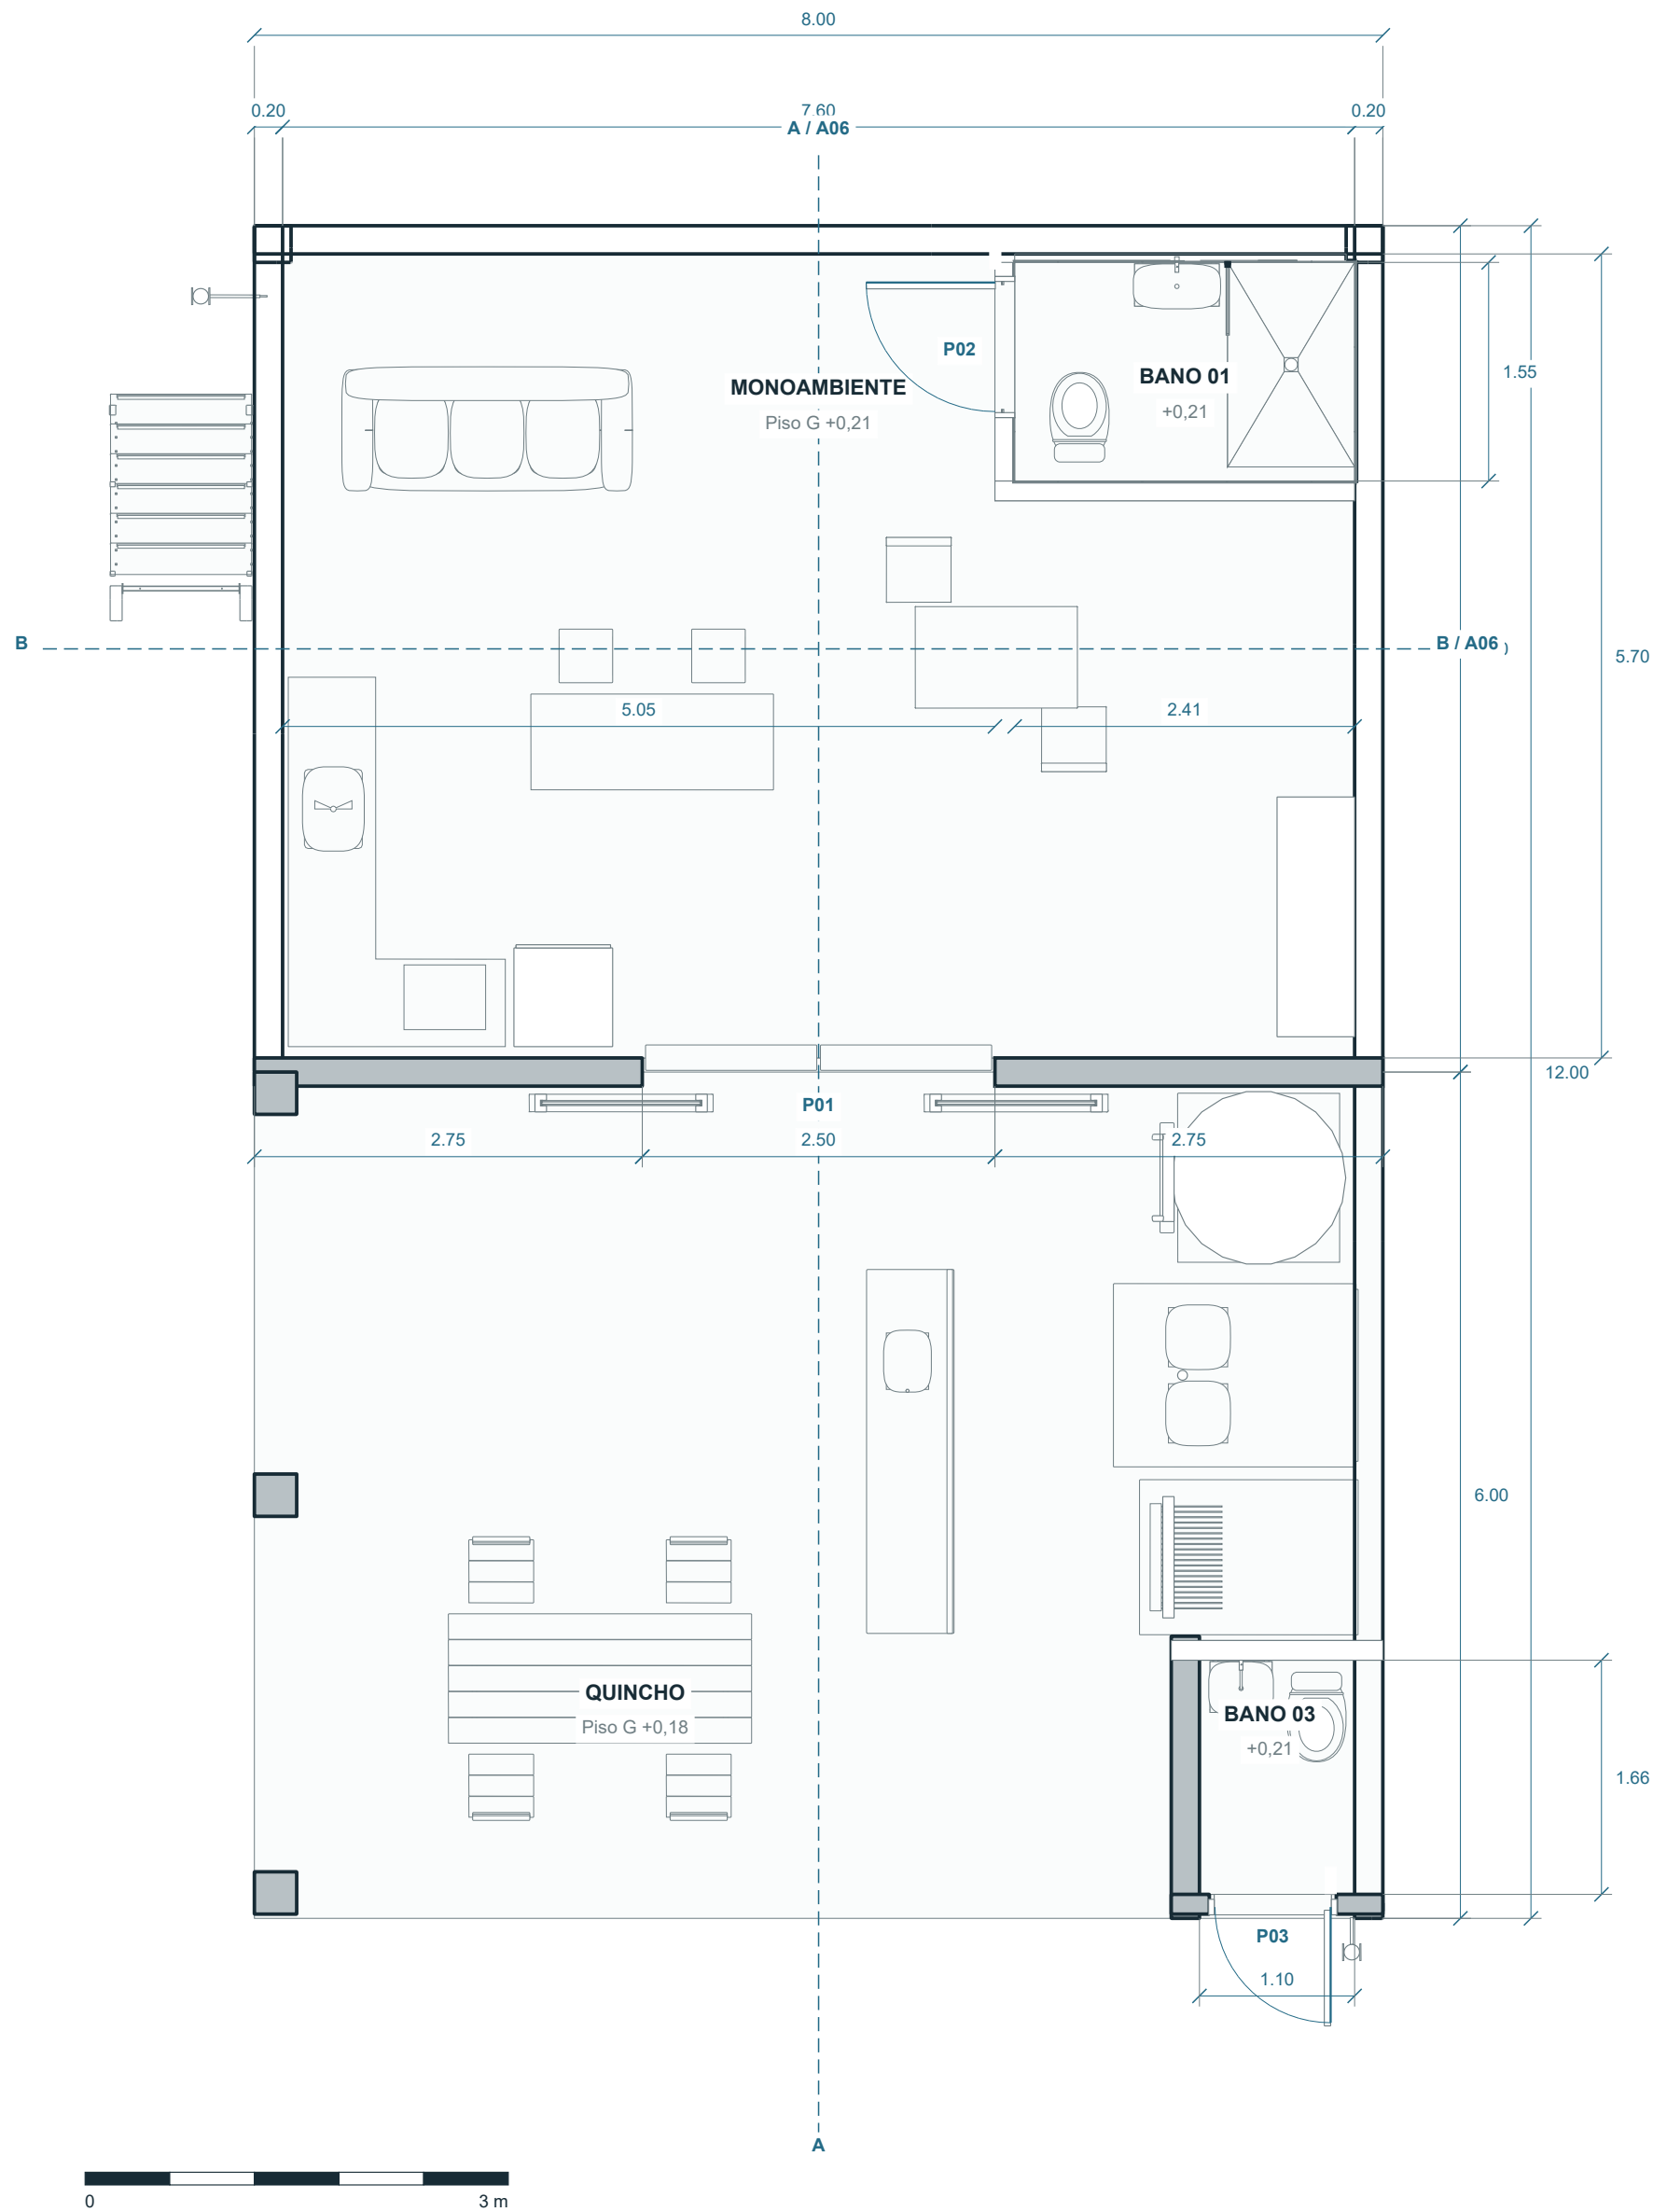

DIMENSIONES Y NIVELES


- F: envoltente nominal 8,00 x 12,00 m; espesor exterior 0,20 m. La geometría de piezas puede incluir juntas y salientes.
- G: piso monoambiente +0,21; quincho +0,18; ambos banos PB +0,21. Saltos entre acabados visibles: no se omiten.
- G: vano doble monoambiente 2,50 m entre jambas. Las hojas y rieles se describen en A12.
- G: baño mono en fachada Cedro y medianera: X19,39.21,80 / Z0,26..1,81. Luz entre acabados2,41 x1,55; tabique lateral0,14. Acceso por oeste.
- G: baño de pileta exterior con acceso desde jardín. Detalle acotado en A09.
- Barridos azules: pose de apertura esquemática de hojas; la ausencia de colision se audita en el modelo y no se presume por este símbolo.

LECTURA DE LOS EQUIPOS

- Cocina en L e isla: A10b. D14 amplía las dos plazas, rodillas, apoyos y trayectorias de uso.
- Quincho: horno, bacha y parrilla mantienen la línea de fuente; extracciones independientes hacia patinillo. Ver A10 y A15.
- La circulación y los usos se muestran con el mobiliario actual. No se certifican accesibilidad ni condiciones reglamentarias locales.

Ref.	Ambito	Consultar
P01	Corredera PB	A12 carpinterías
P02 / P03	Banos PB / pileta	A09 locales
A-A / B-B	Secciones reales	A06 cortes generales

01 Planta alta amoblada | 1:50

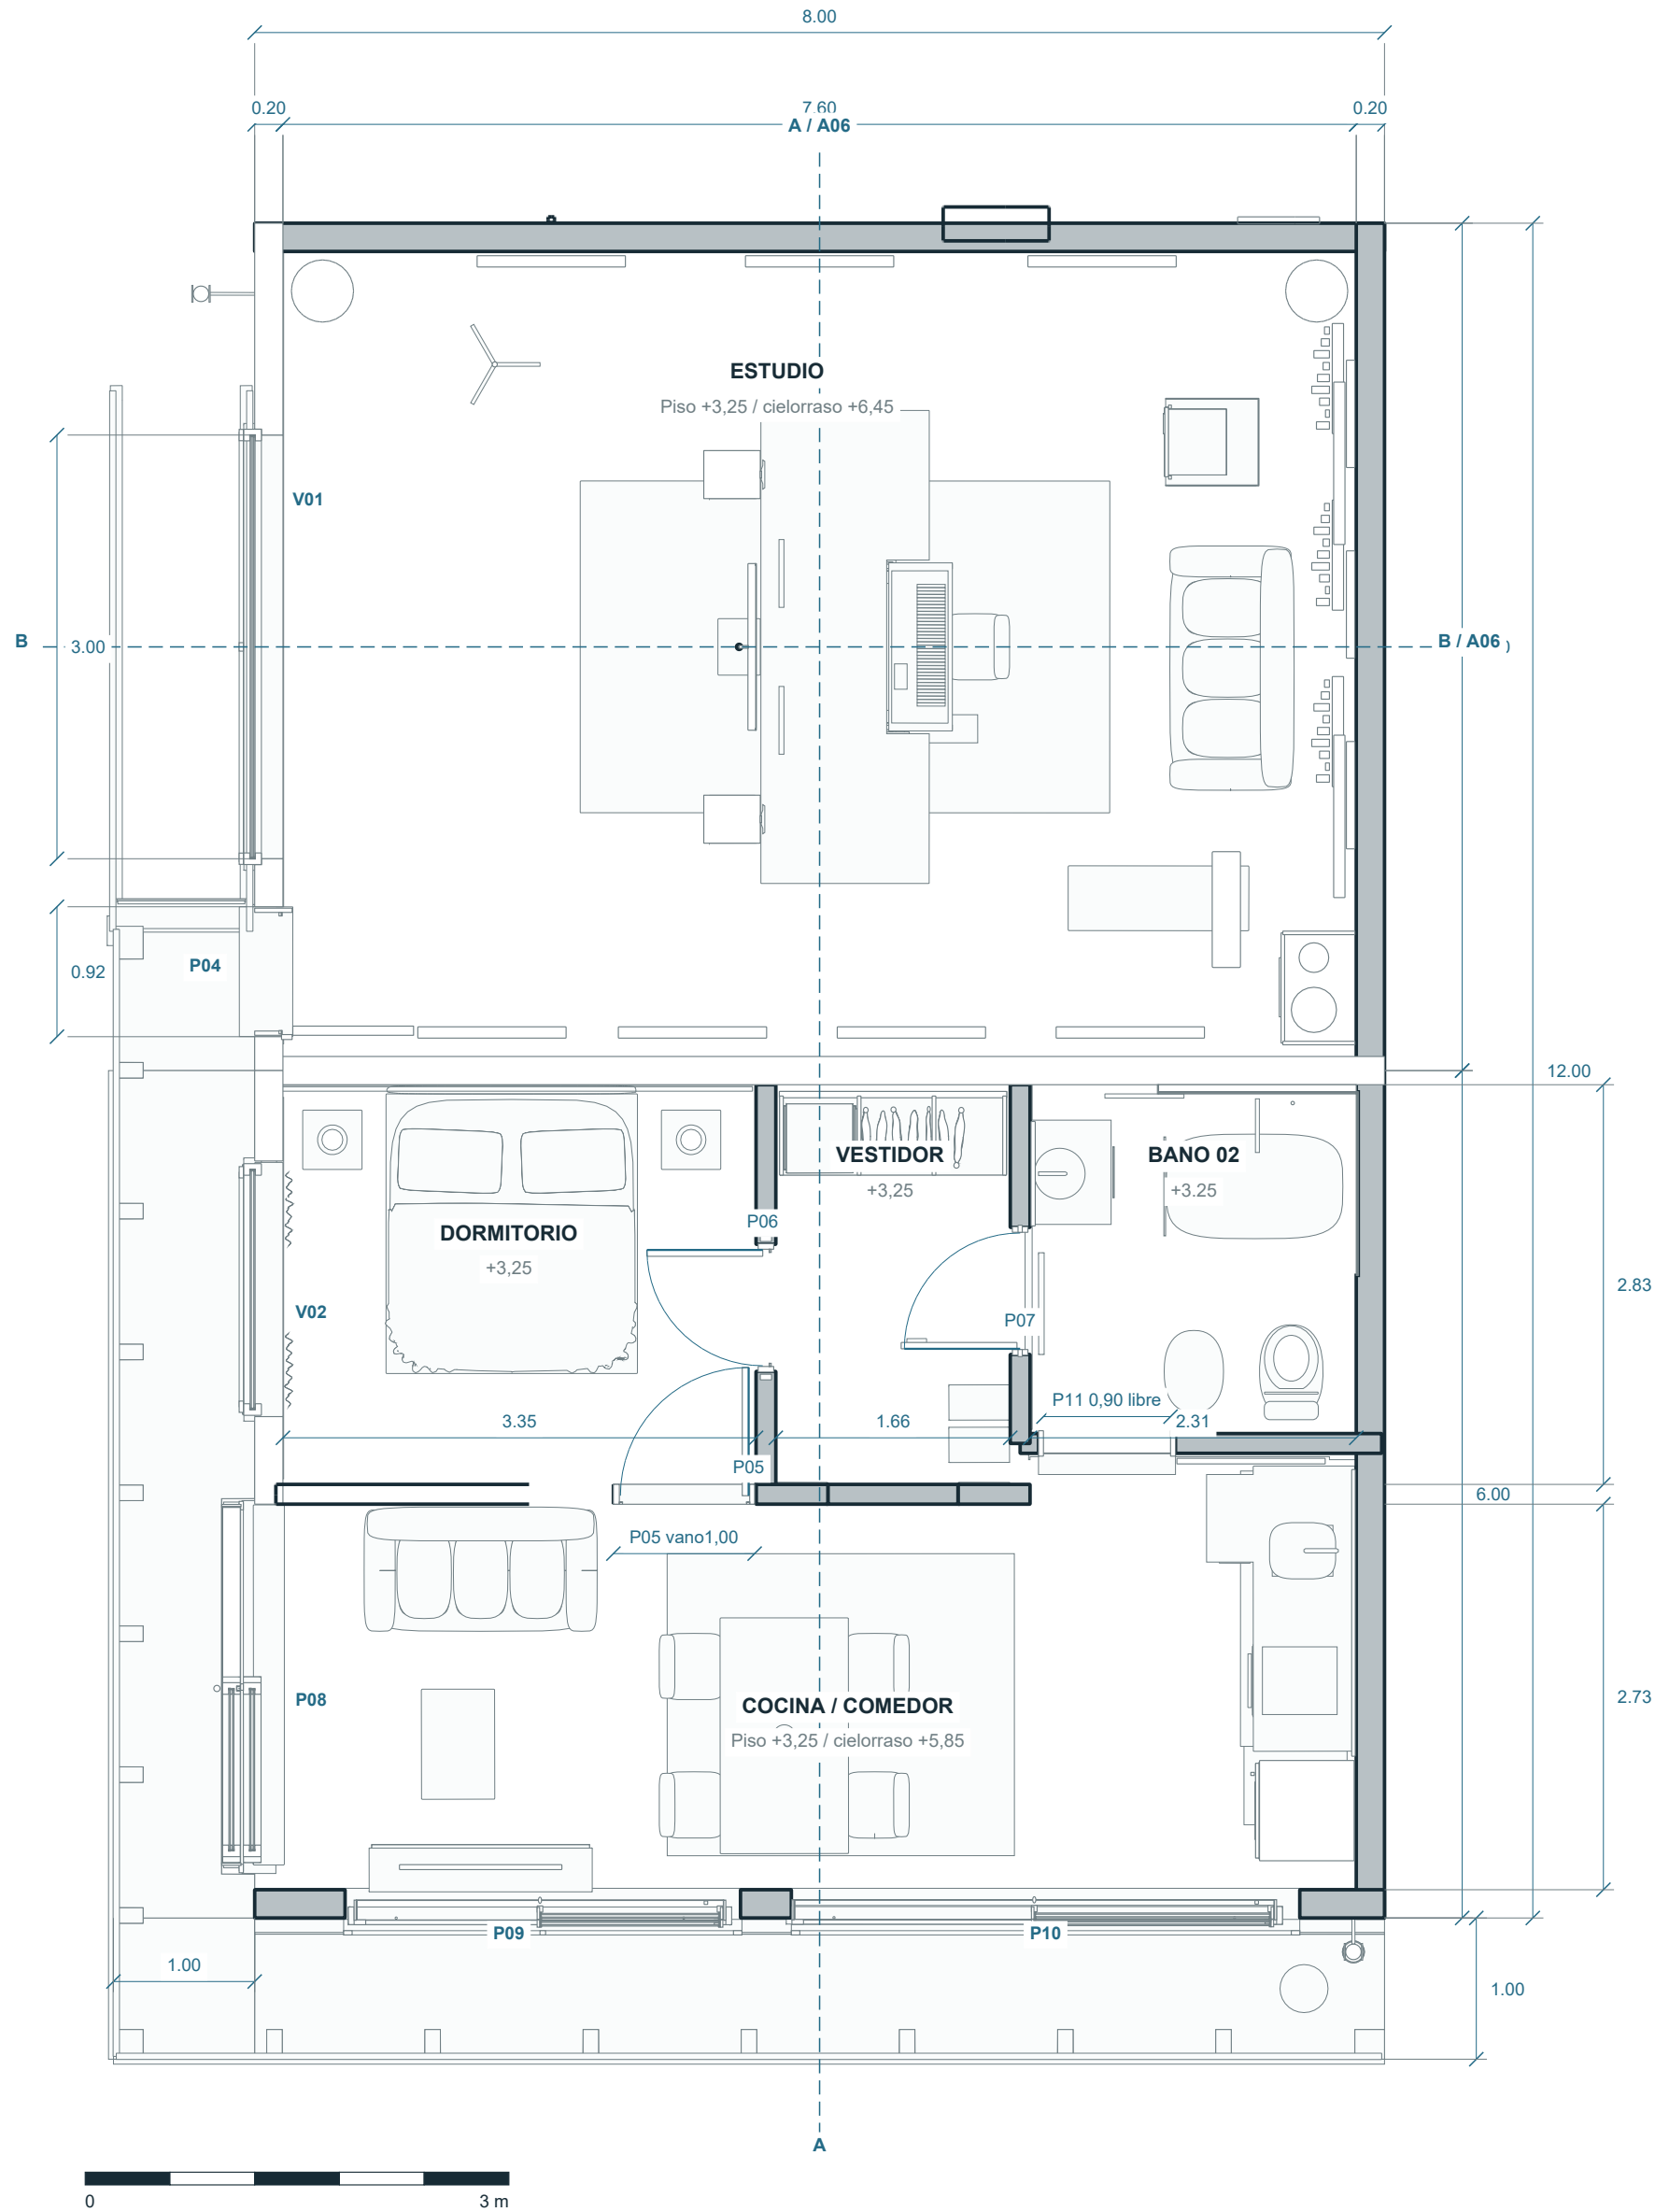


ALTURAS AUTORIZADAS

- F/G: piso estudio +3,25; cara inferior del cielorraso +6,45 = 3,20 m libres.
- F/G: piso vivienda +3,25; cielorraso general +5,85 = 2,60 m libres.
- G: piso bano +3.25; cielorraso +5.85; altura libre 2.60 m. Transicion continua al comedor y corredera: suplemento D09.
- G: losa entre plantas +3,00 a +3,20; espesor 0,20 m. Acabado general superior 0,05 m.
- F: acceso exterior unico al nivel alto. Escalera y descanso 1,00 m nominal; detalle del umbral en A07.

CERRAMIENTOS Y VANOS

- F: ventana del estudio 3,00 m. G: paños DVH y marco segun cuadro A12.
- G: P05 conecta dormitorio con estar; P06 comunica dormitorio y vestidor; P07 vestidor y bano; P11 bano y comedor. Vestidor cerrado al estar.
- G: balcon lateral 1,00 m y posterior 1,00 m nominal. Barandas y borde de losa en A12/A13.
- Acustica, ventilacion y sellado: A11 y suplemento D06-D08. Prestaciones aun no calculadas.

01 Vivienda / accesos, mobiliario y huellas de uso | 1:25

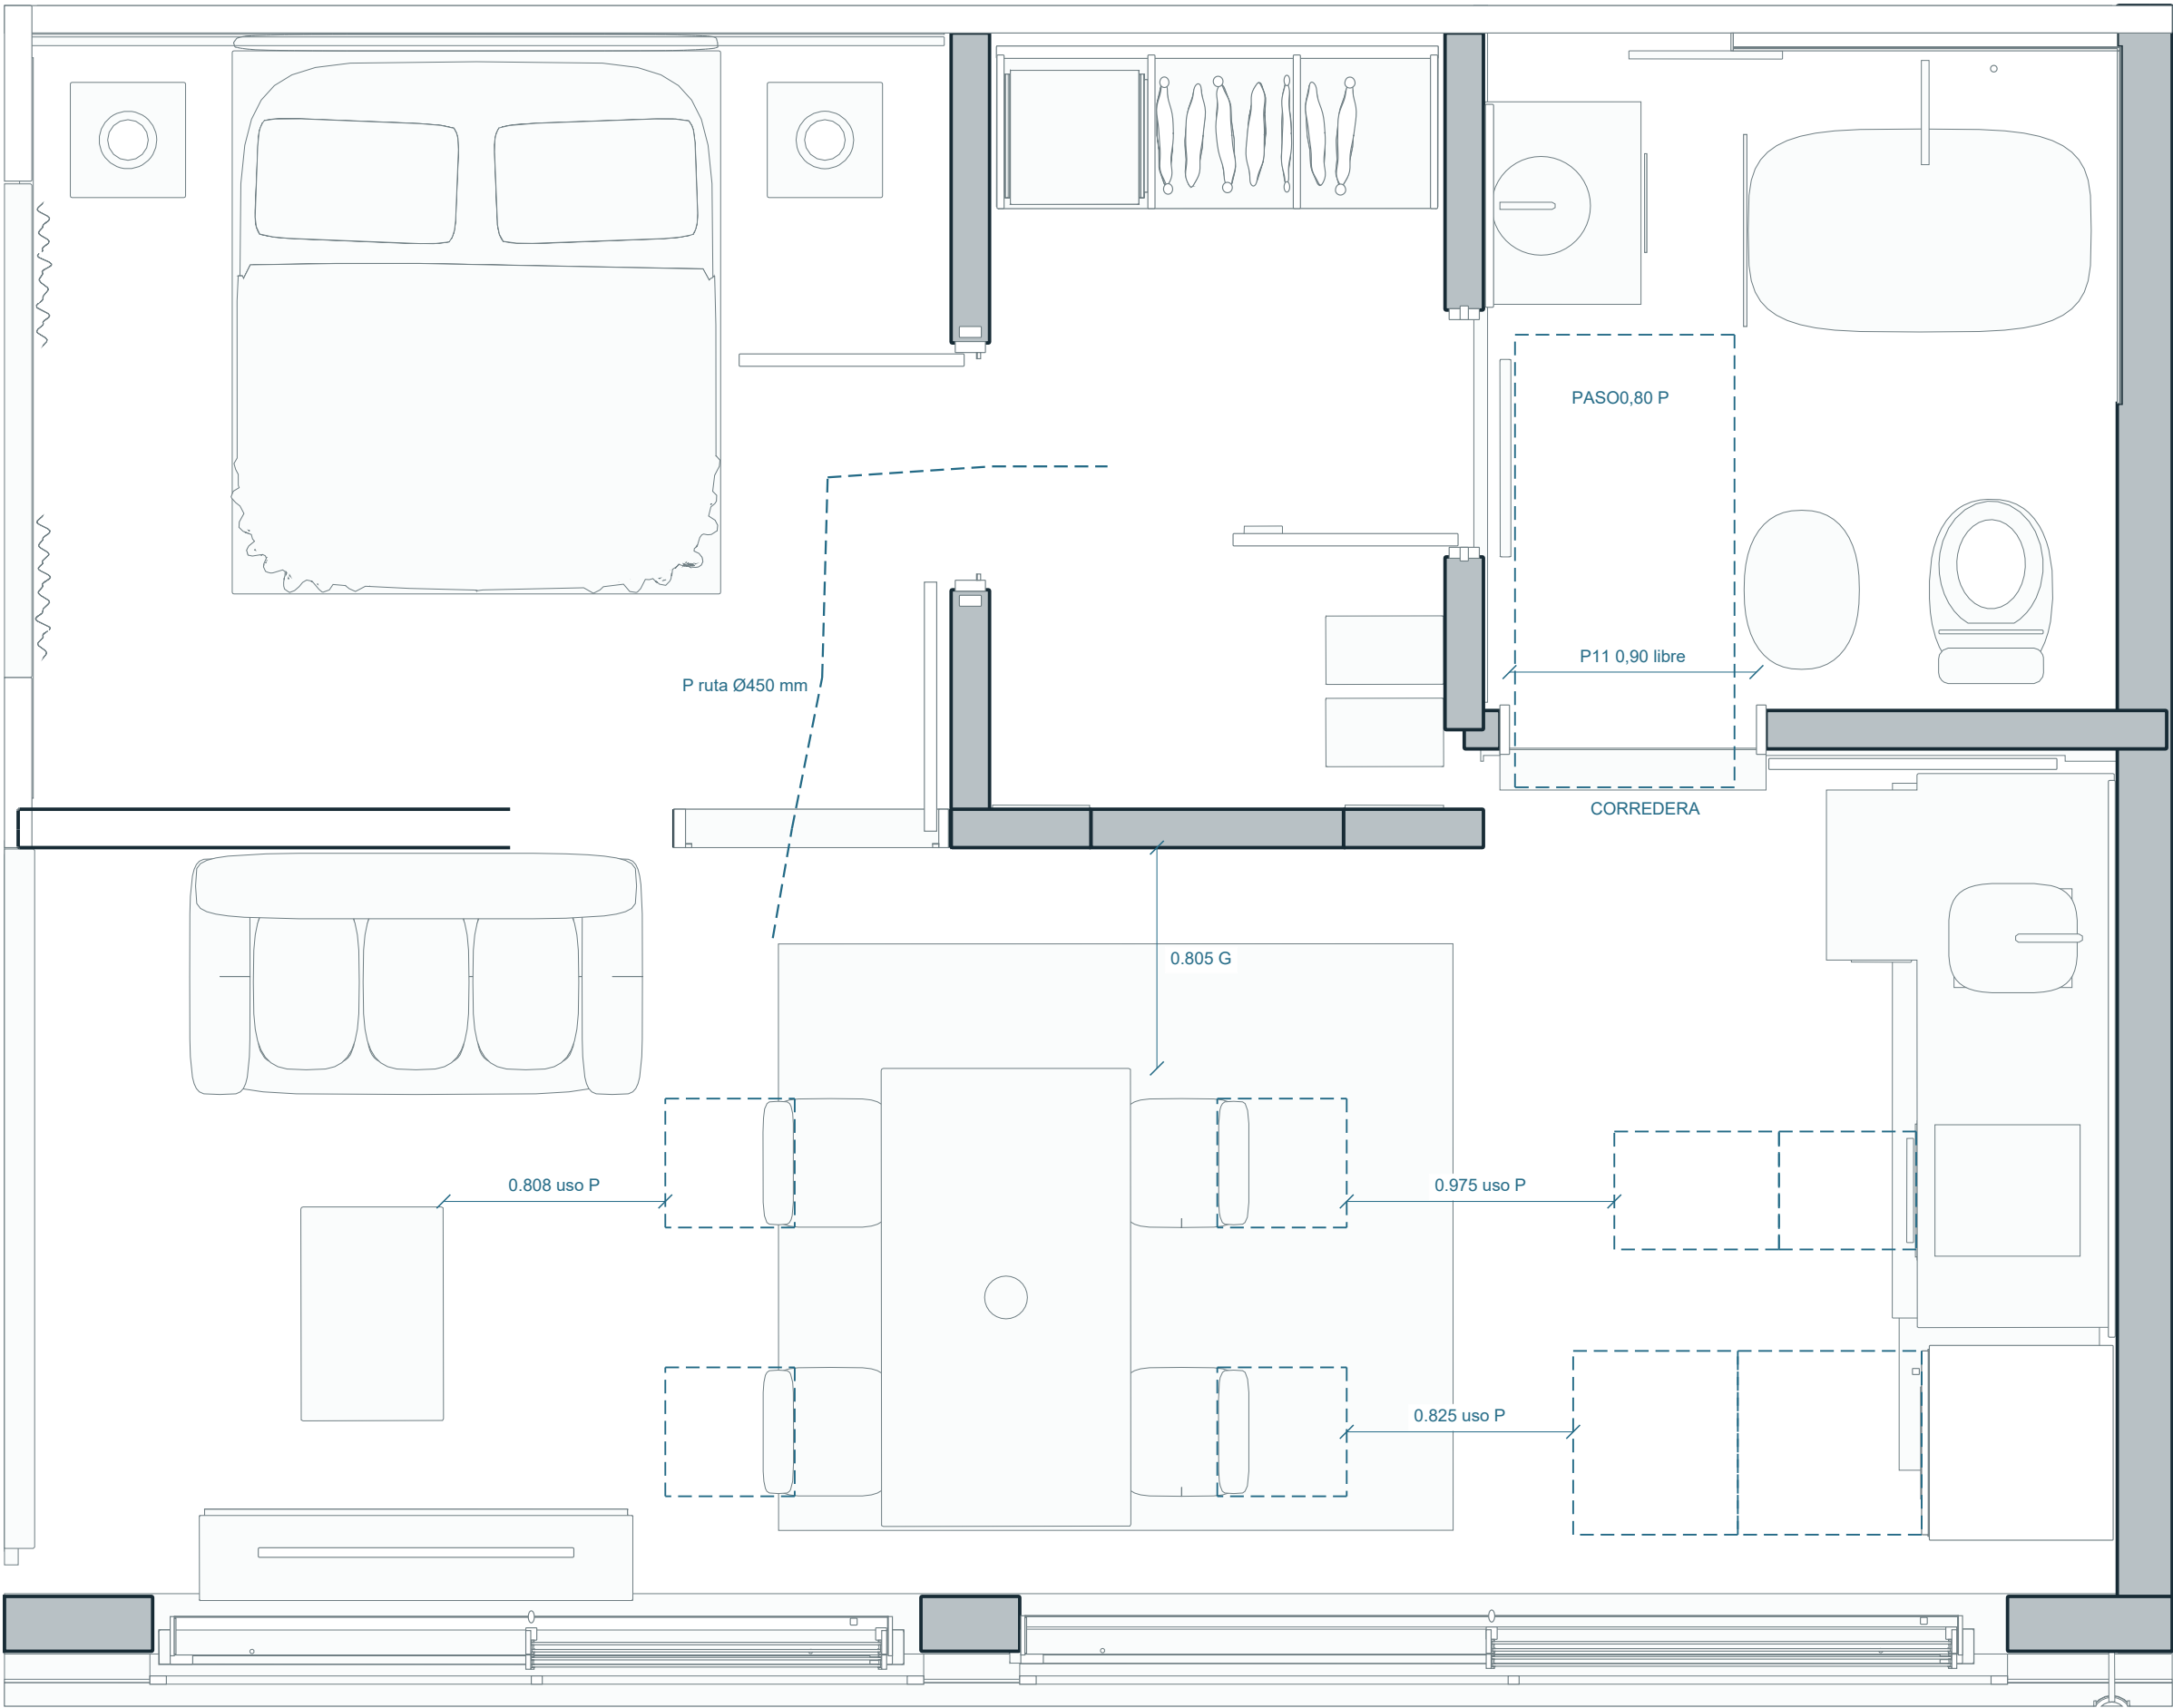

GEOMETRIA Y HUELLAS DE USO

G: muebles, mesadas y aparatos proceden del mismo modelo que esta cartela. Cotas a sus envolventes, no a centros.

P: cada silla se retira350 mm perpendicular al lado largo de la mesa. Se conserva su ancho y profundidad medidos.

P: profundidad de apertura de horno igual a altura de su frente; heladera igual a ancho de hoja. La abertura se dibuja como envolvente conservadora y requiere herraje real.

P: usuario de600 mm detras de hoja abierta. Estas huellas sirven para revisar simultaneidad; no acreditan accesibilidad normativa.

Caso simultaneo P	Paso m
Silla retirada / horno + usuario	0.975
Silla retirada / heladera + usuario	0.825
Silla oeste retirada / mesa baja	0.808

RECORRIDOS Y LECTURA


Estar -> dormitorio -> vestidor -> baño; P05 y P06 abren hacia dormitorio. P11 baño-comedor conservado; vestidor cerrado al estar.

G P05: paso conservador806mm: galce X16.6045 hasta manija X17.4105, hoja90°. Proyeccion sobre toda la profundidad de hoja; garganta848mm. A12.

Si muebles o herrajes cambian, recalcular estas envolventes; la ausencia de choque no sustituye la prueba de uso.

NPT vivienda y baño continuo +3,25. Se verifican trayectorias y espacios de uso como propuestas dimensionales; la evaluacion de confort y las aperturas finales se confirman sobre la nueva escena y los herrajes elegidos.

01 Cubiertas y captacion | 1:50

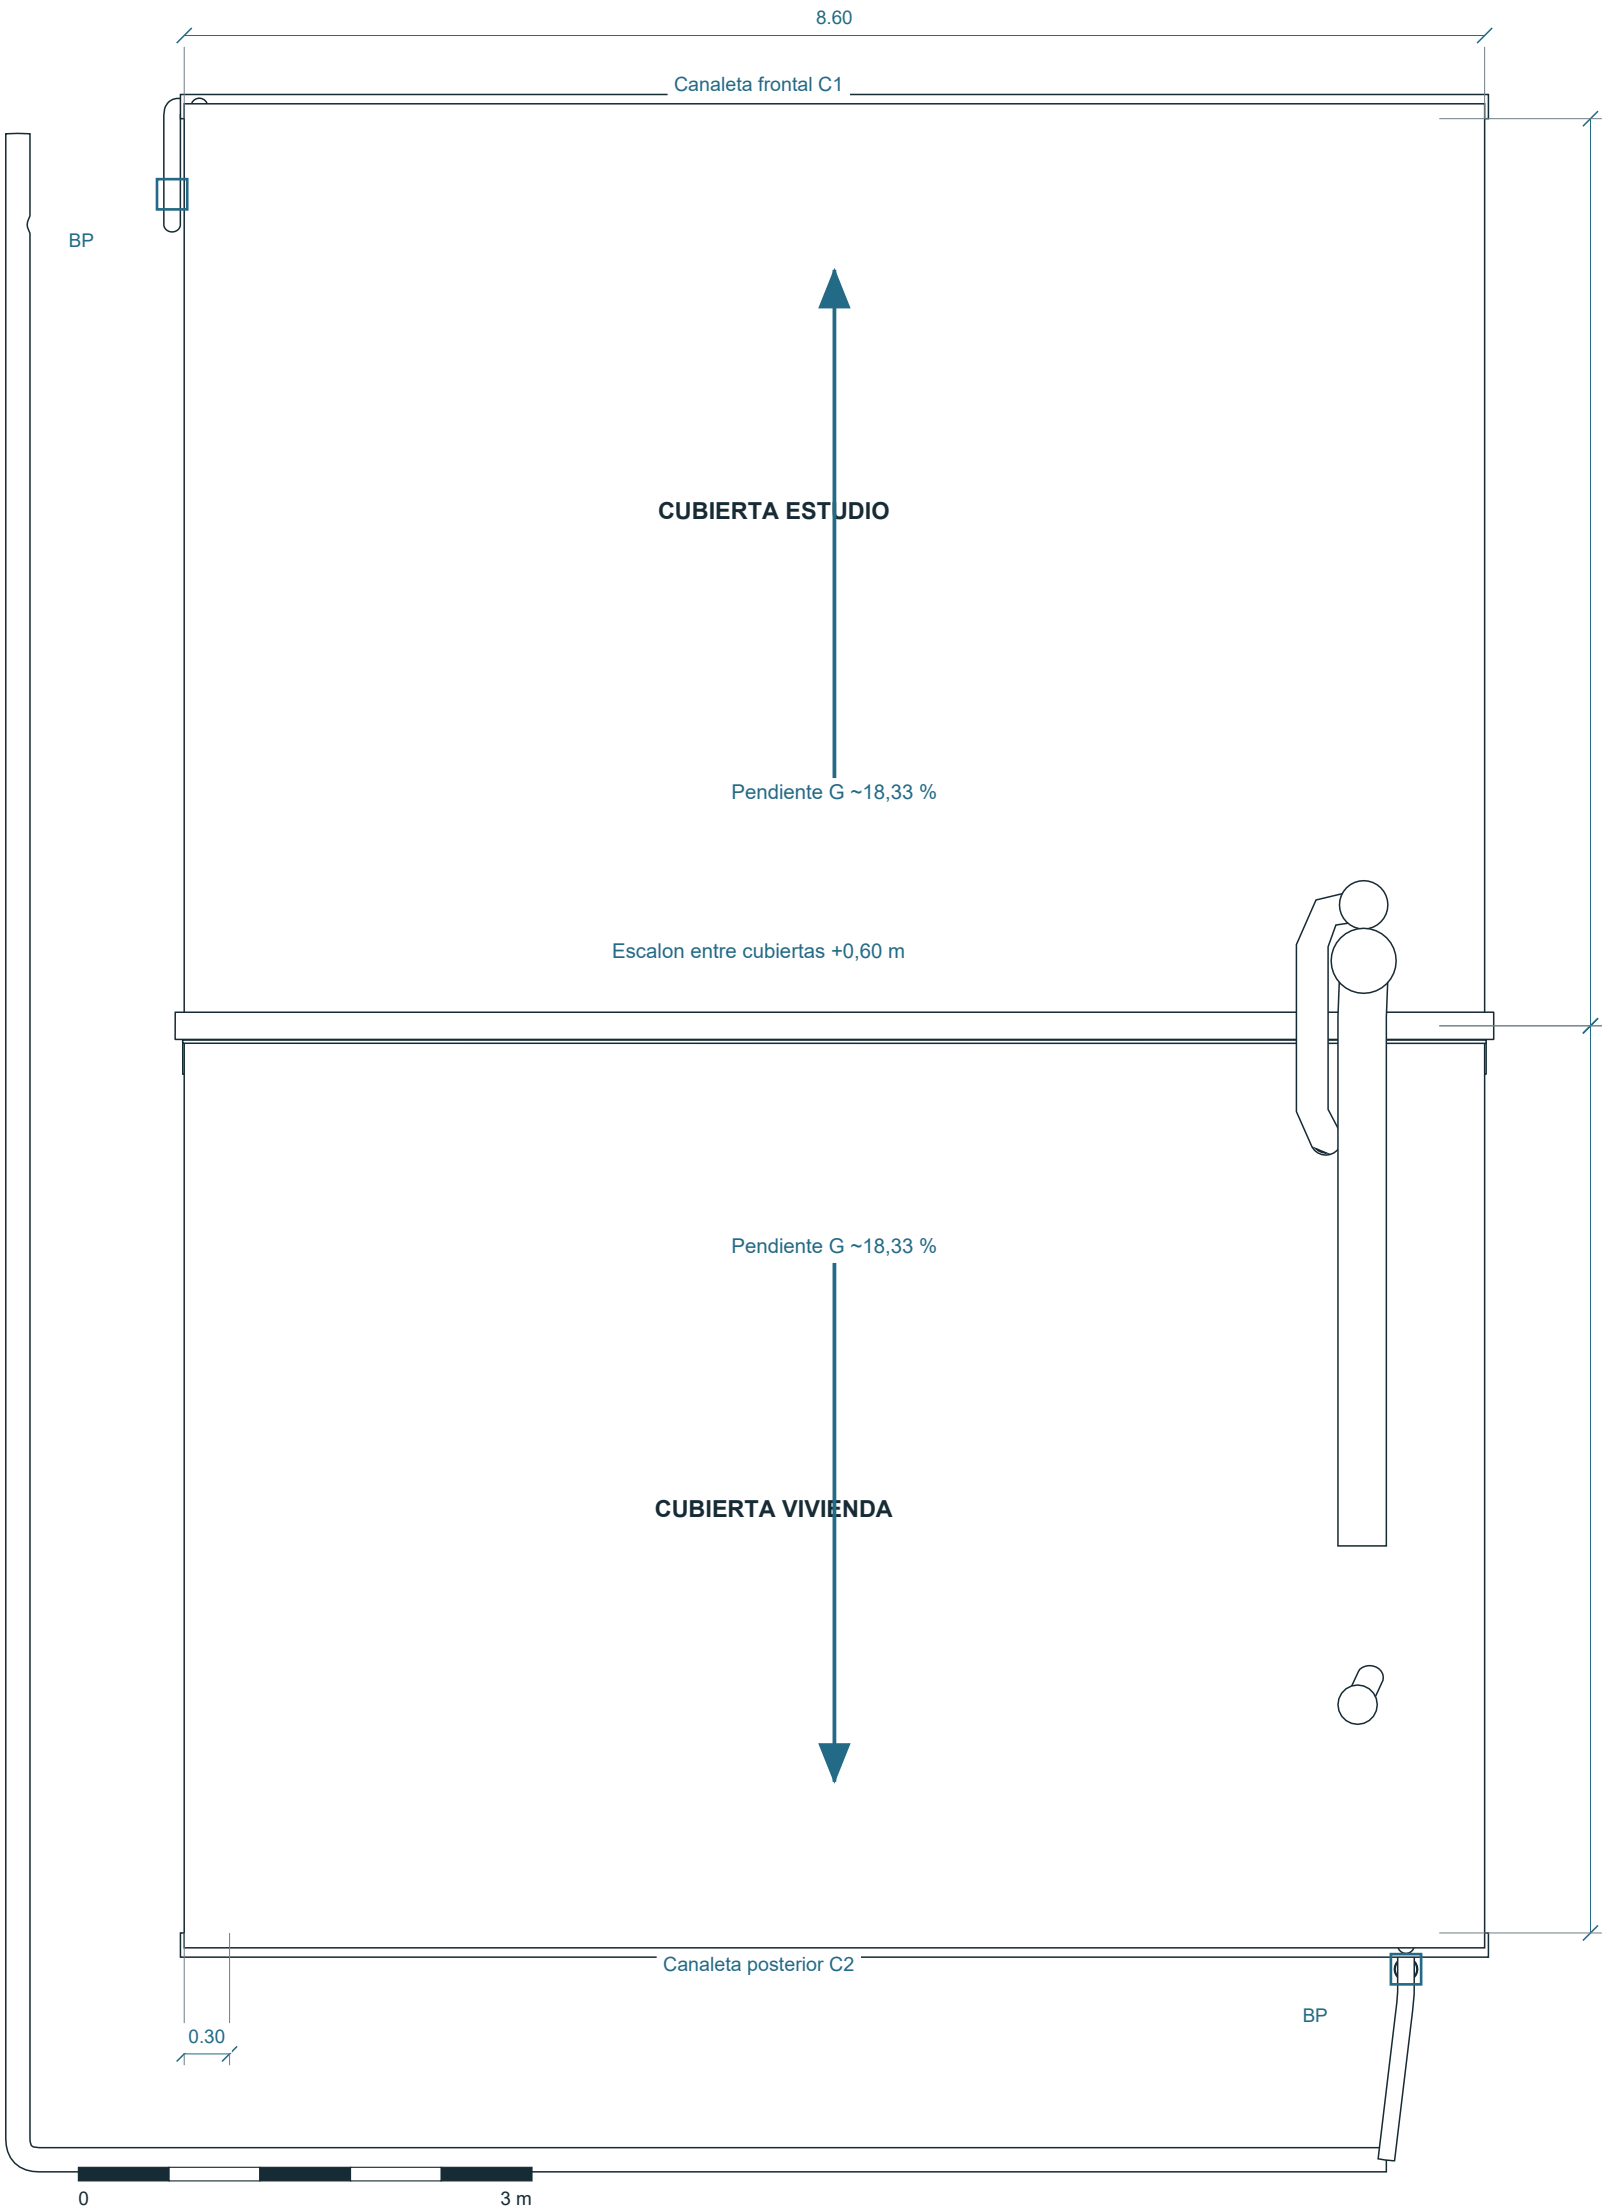

CONTINUIDAD DEL AGUA

G: pendientes principales conservadas, 1,10 m de subida en 6,00 m de desarrollo horizontal nominal (18,33 %). No es una pendiente pluvial de canería.


G: estudio elevado 0,60 m respecto de la cubierta de vivienda. Alero lateral nominal 0,30 m.

Captacion: revisar seccion abierta, embudo, codo y abrazaderas en el modelo de esta emision. El corte de abajo reproduce sus piezas reales.

P: conduccion de descarga hasta punto de red pluvial propuesto. Conexion, cota, caudal y diametros finales pendientes de datos de servicio y calculo.

No se presume que una bajada dibujada llega a una red existente. A15 identifica el limite de coordinacion.

02 Circuito frontal / proyeccion | 1:50

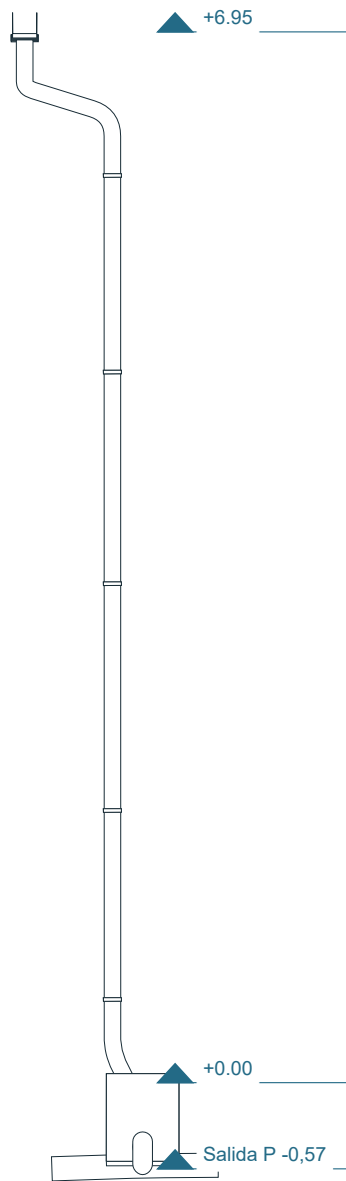


PUNTOS DE CONTROL

1. Cubierta hacia canaleta receptora.
2. Fondo de canaleta hacia salida.
3. Conexion estancia entre piezas.
4. Bajada continua y registrable.
5. Descarga con destino definido.

La continuidad física y la prueba de paso se documentan en la auditoria del modelo.

01 Frente / Cedro Misionero | 1:50

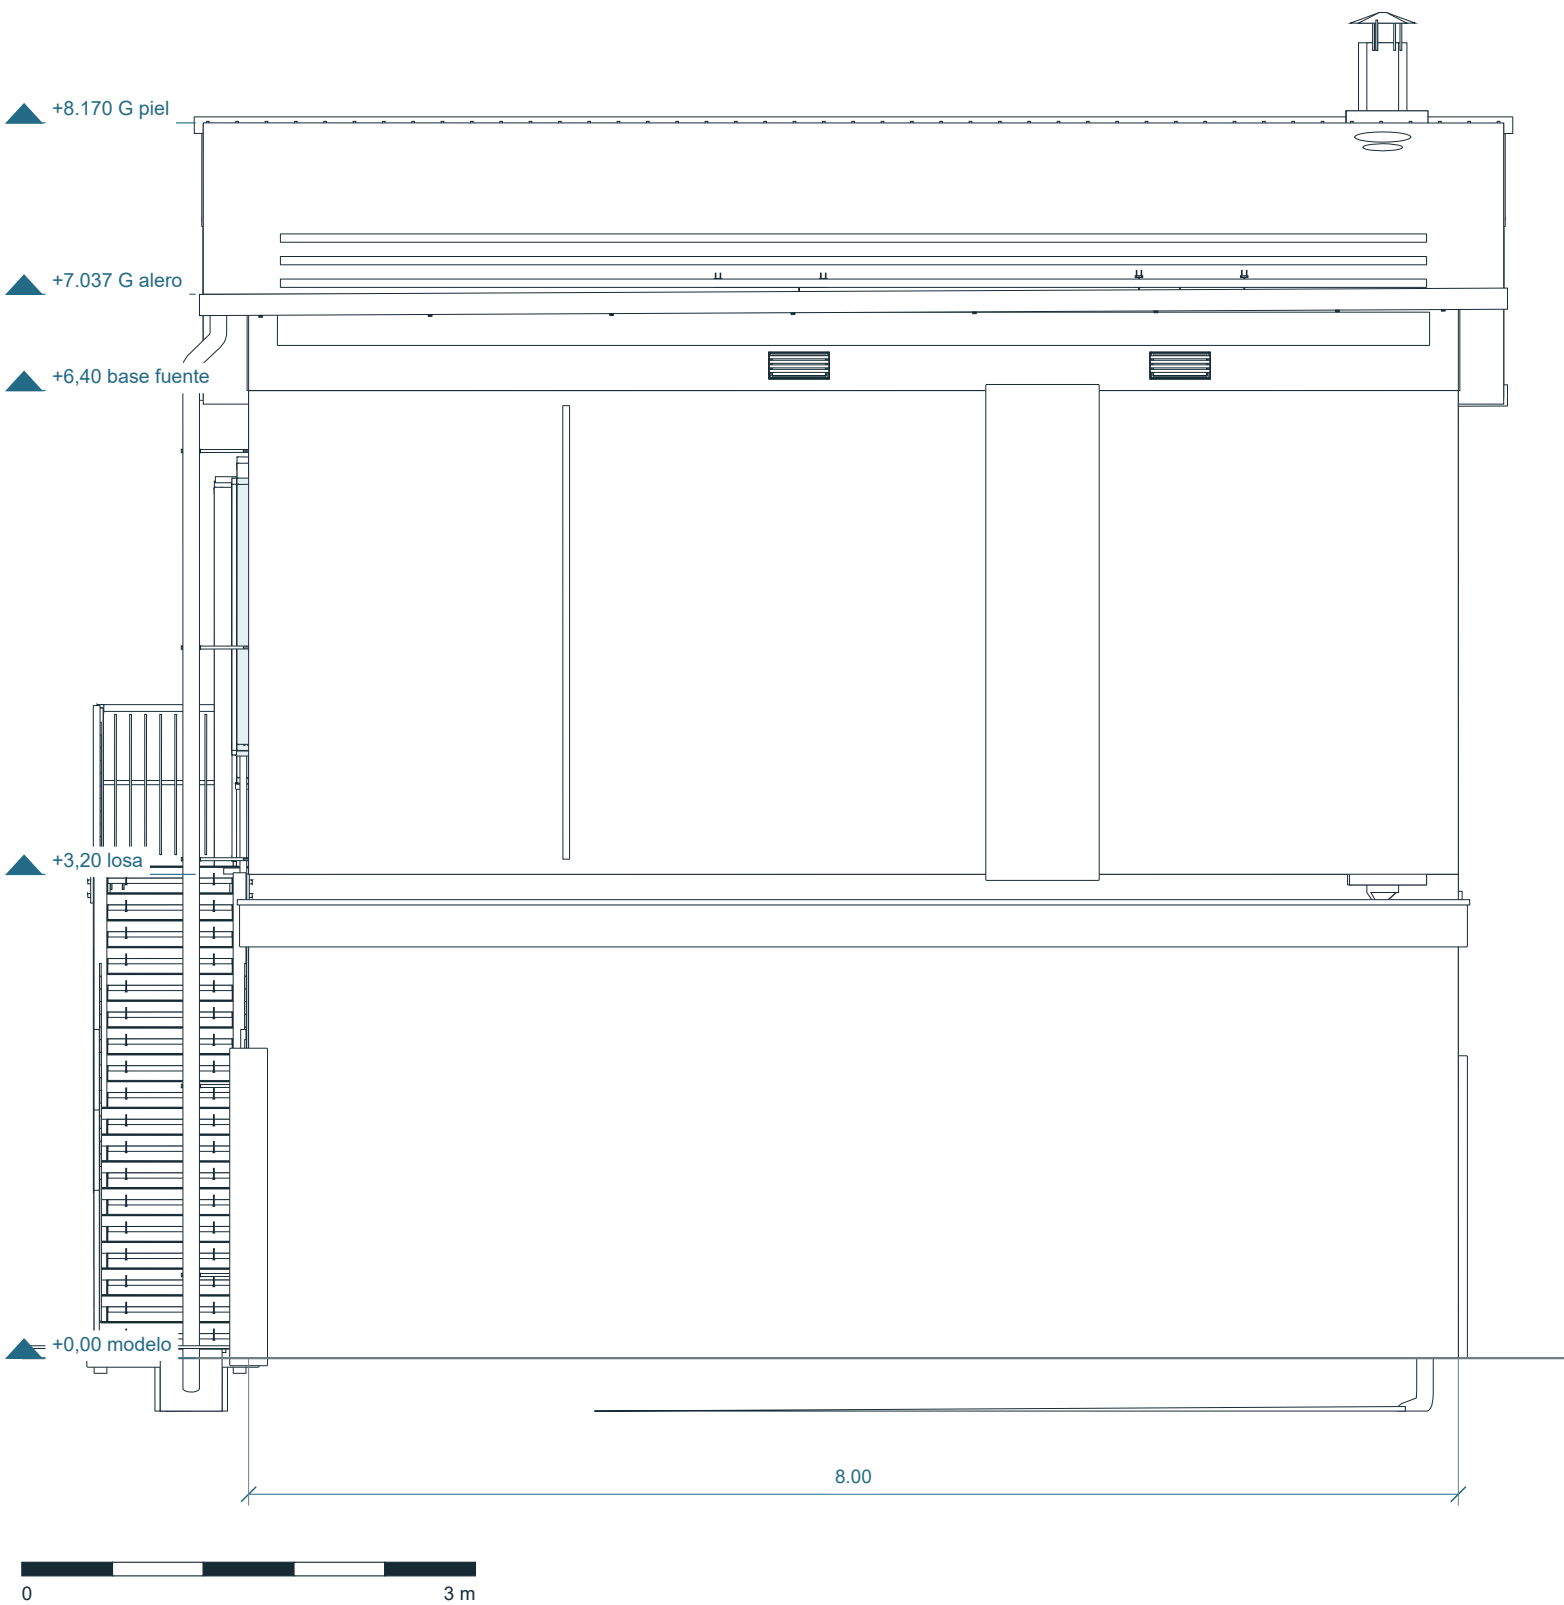

MATERIALIDAD REPRESENTADA


Ladrillo visto en cerramientos; hormigon en losas, pilares y vigas; cubierta metalica con encuentros y remates; DVH en carpinterias; herreria en balcones y escalera.

G cotas de piel exterior de cubierta extraidas de malla. F+7,00/+8,10 son referencias de fuente y no coronamiento terminado. A12/A13 y suplemento amplian hojas, capas y fijaciones; sin despiece certificado.

02 Contrafrente / pileta | 1:50



03 Lateral de acceso | 1:50

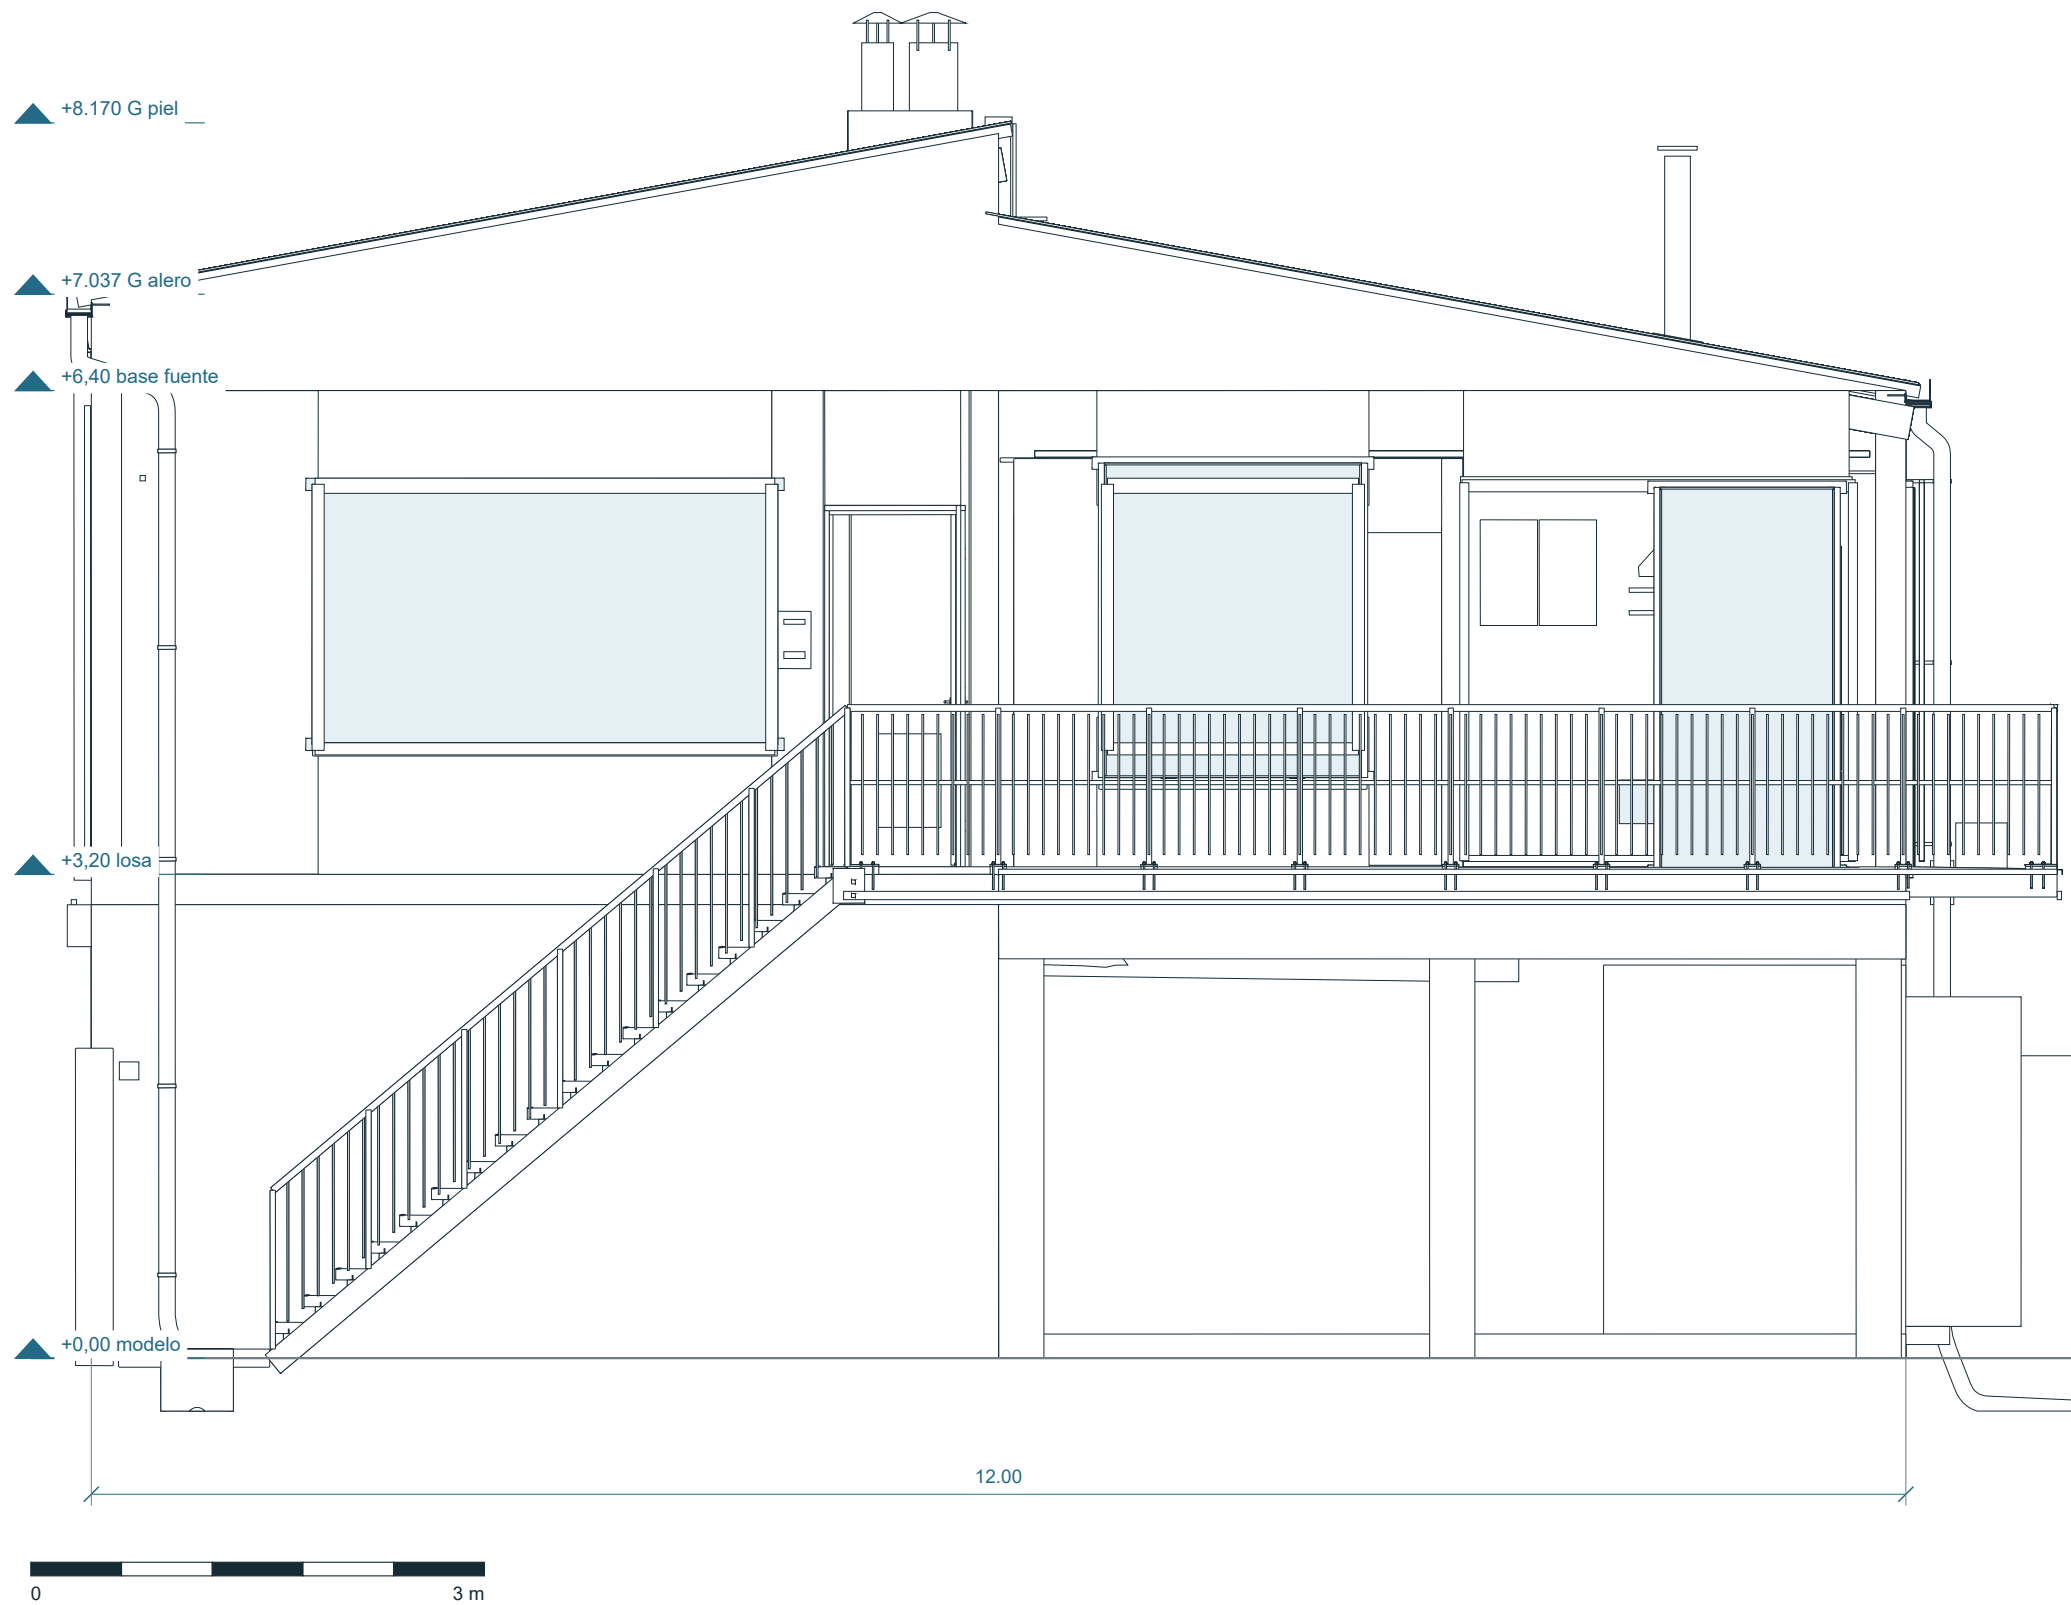


MATERIALIDAD REPRESENTADA


Ladrillo visto en cerramientos; hormigon en losas, pilares y vigas; cubierta metalica con encuentros y remates; DVH en carpinterias; herreria en balcones y escalera.

G cotas de piel exterior de cubierta extraidas de malla. F+7,00/+8,10 son referencias de fuente y no coronamiento terminado. A12/A13 y suplemento amplian hojas, capas y fijaciones; sin despiece certificado.


04 Medianera lateral | 1:50

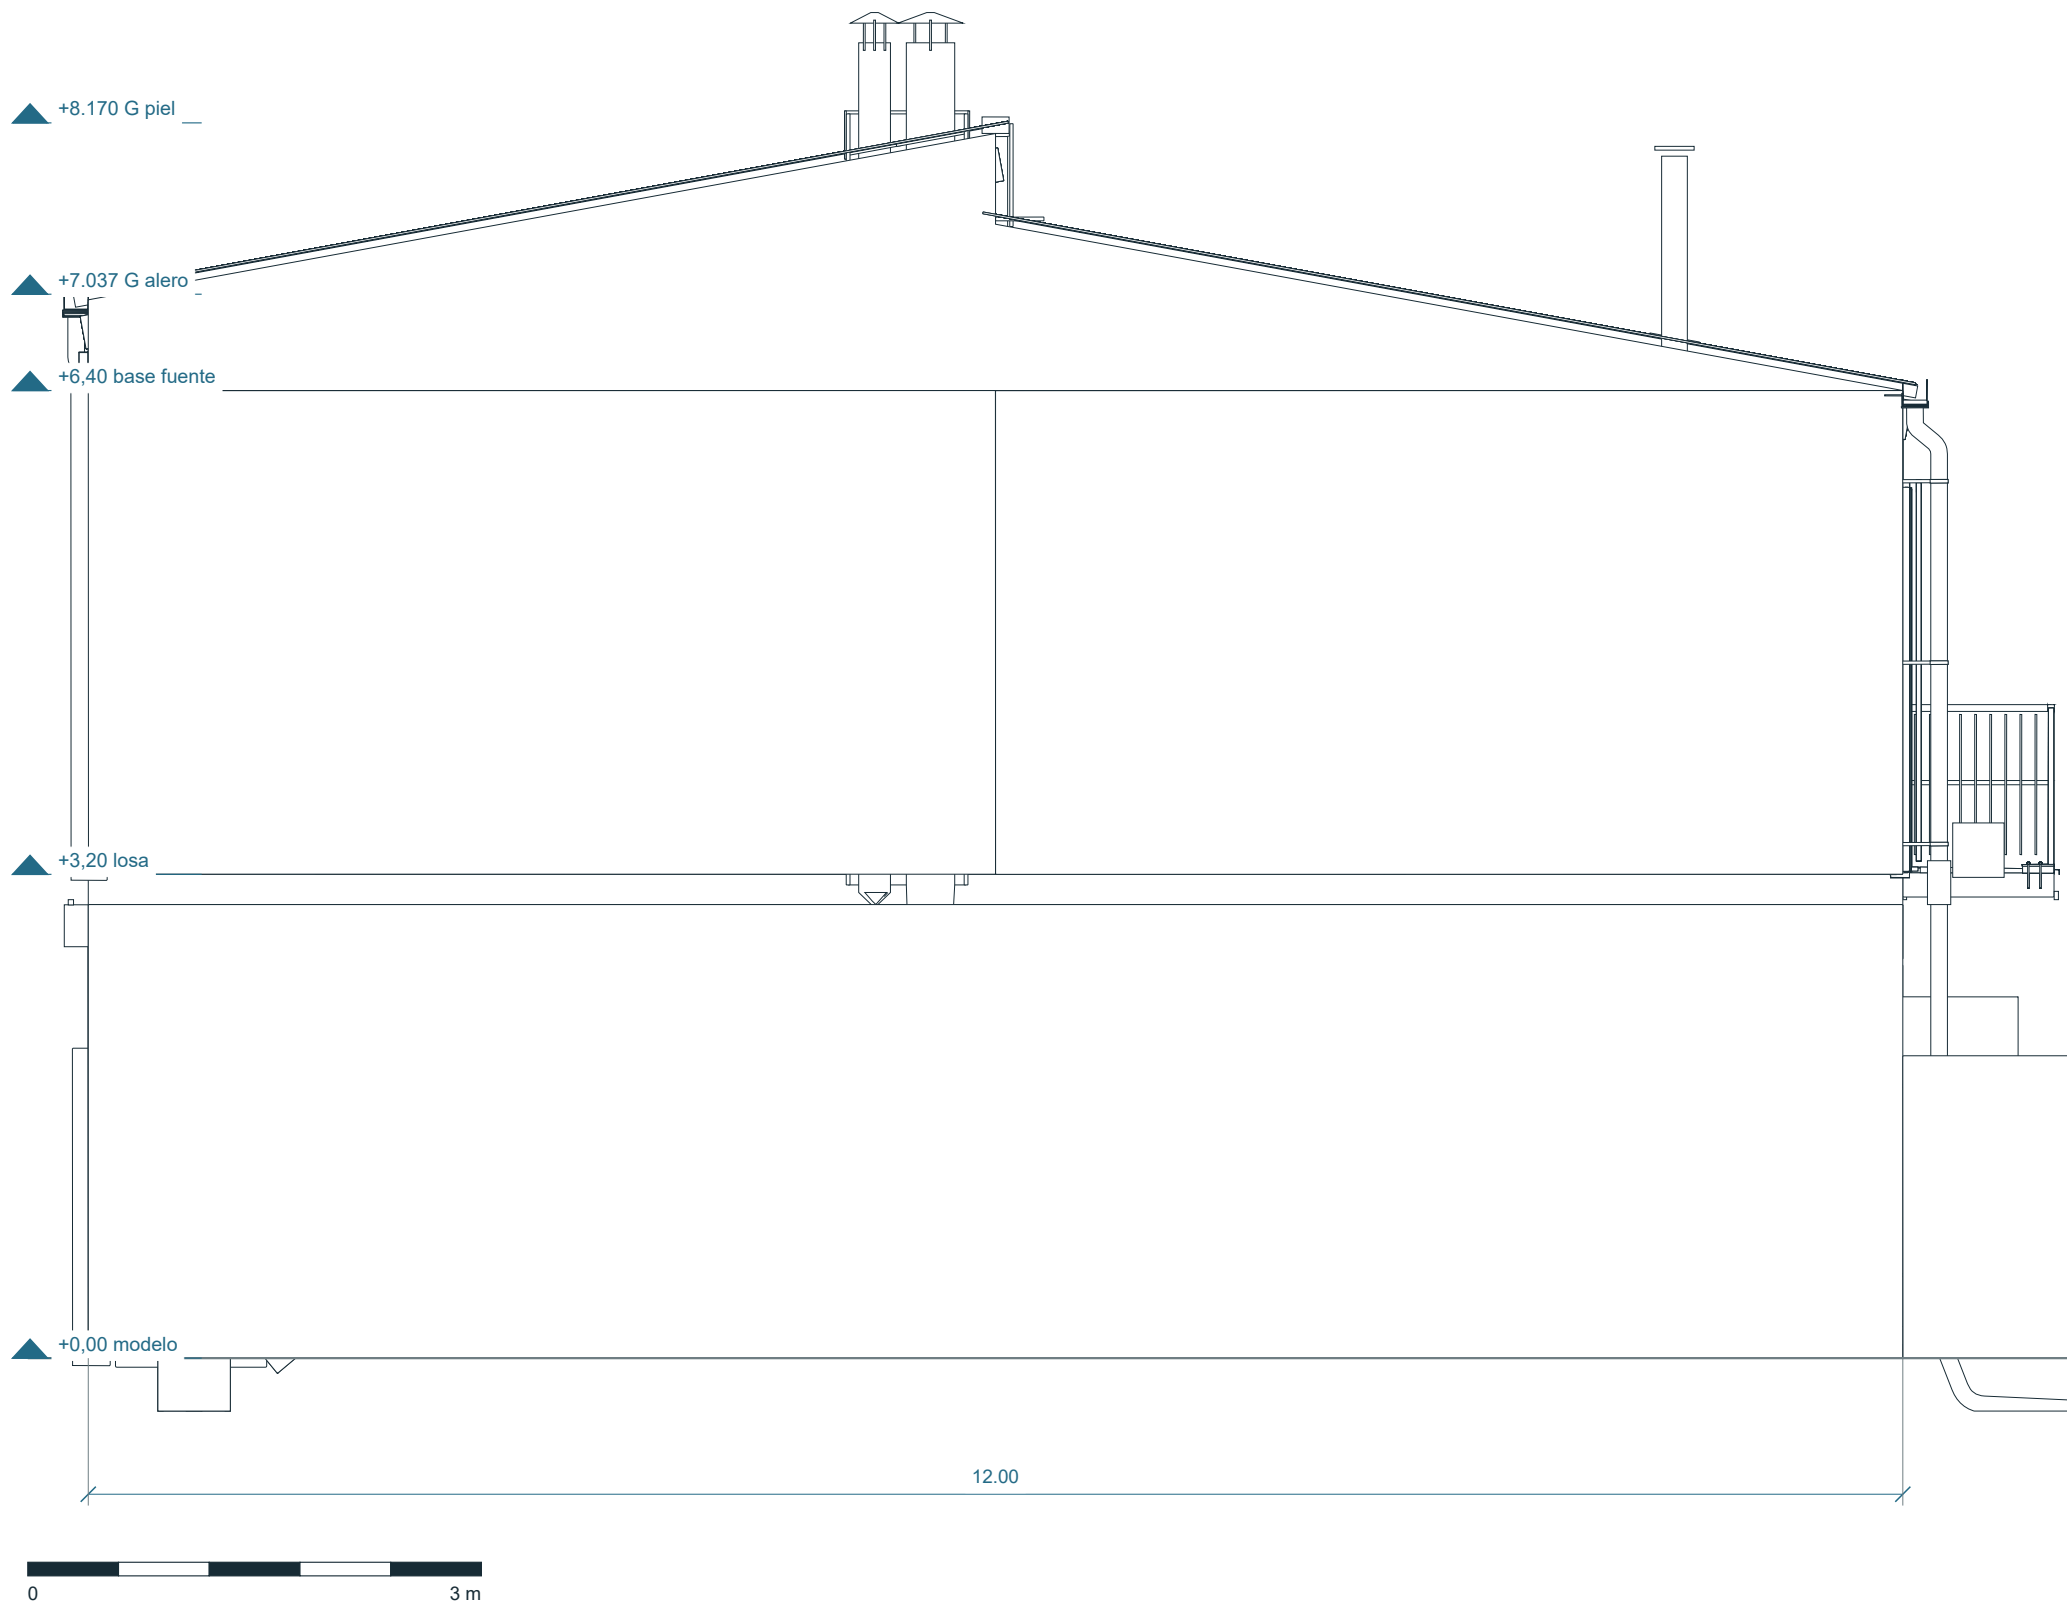

A-A Longitudinal por ambas alturas | 1:50

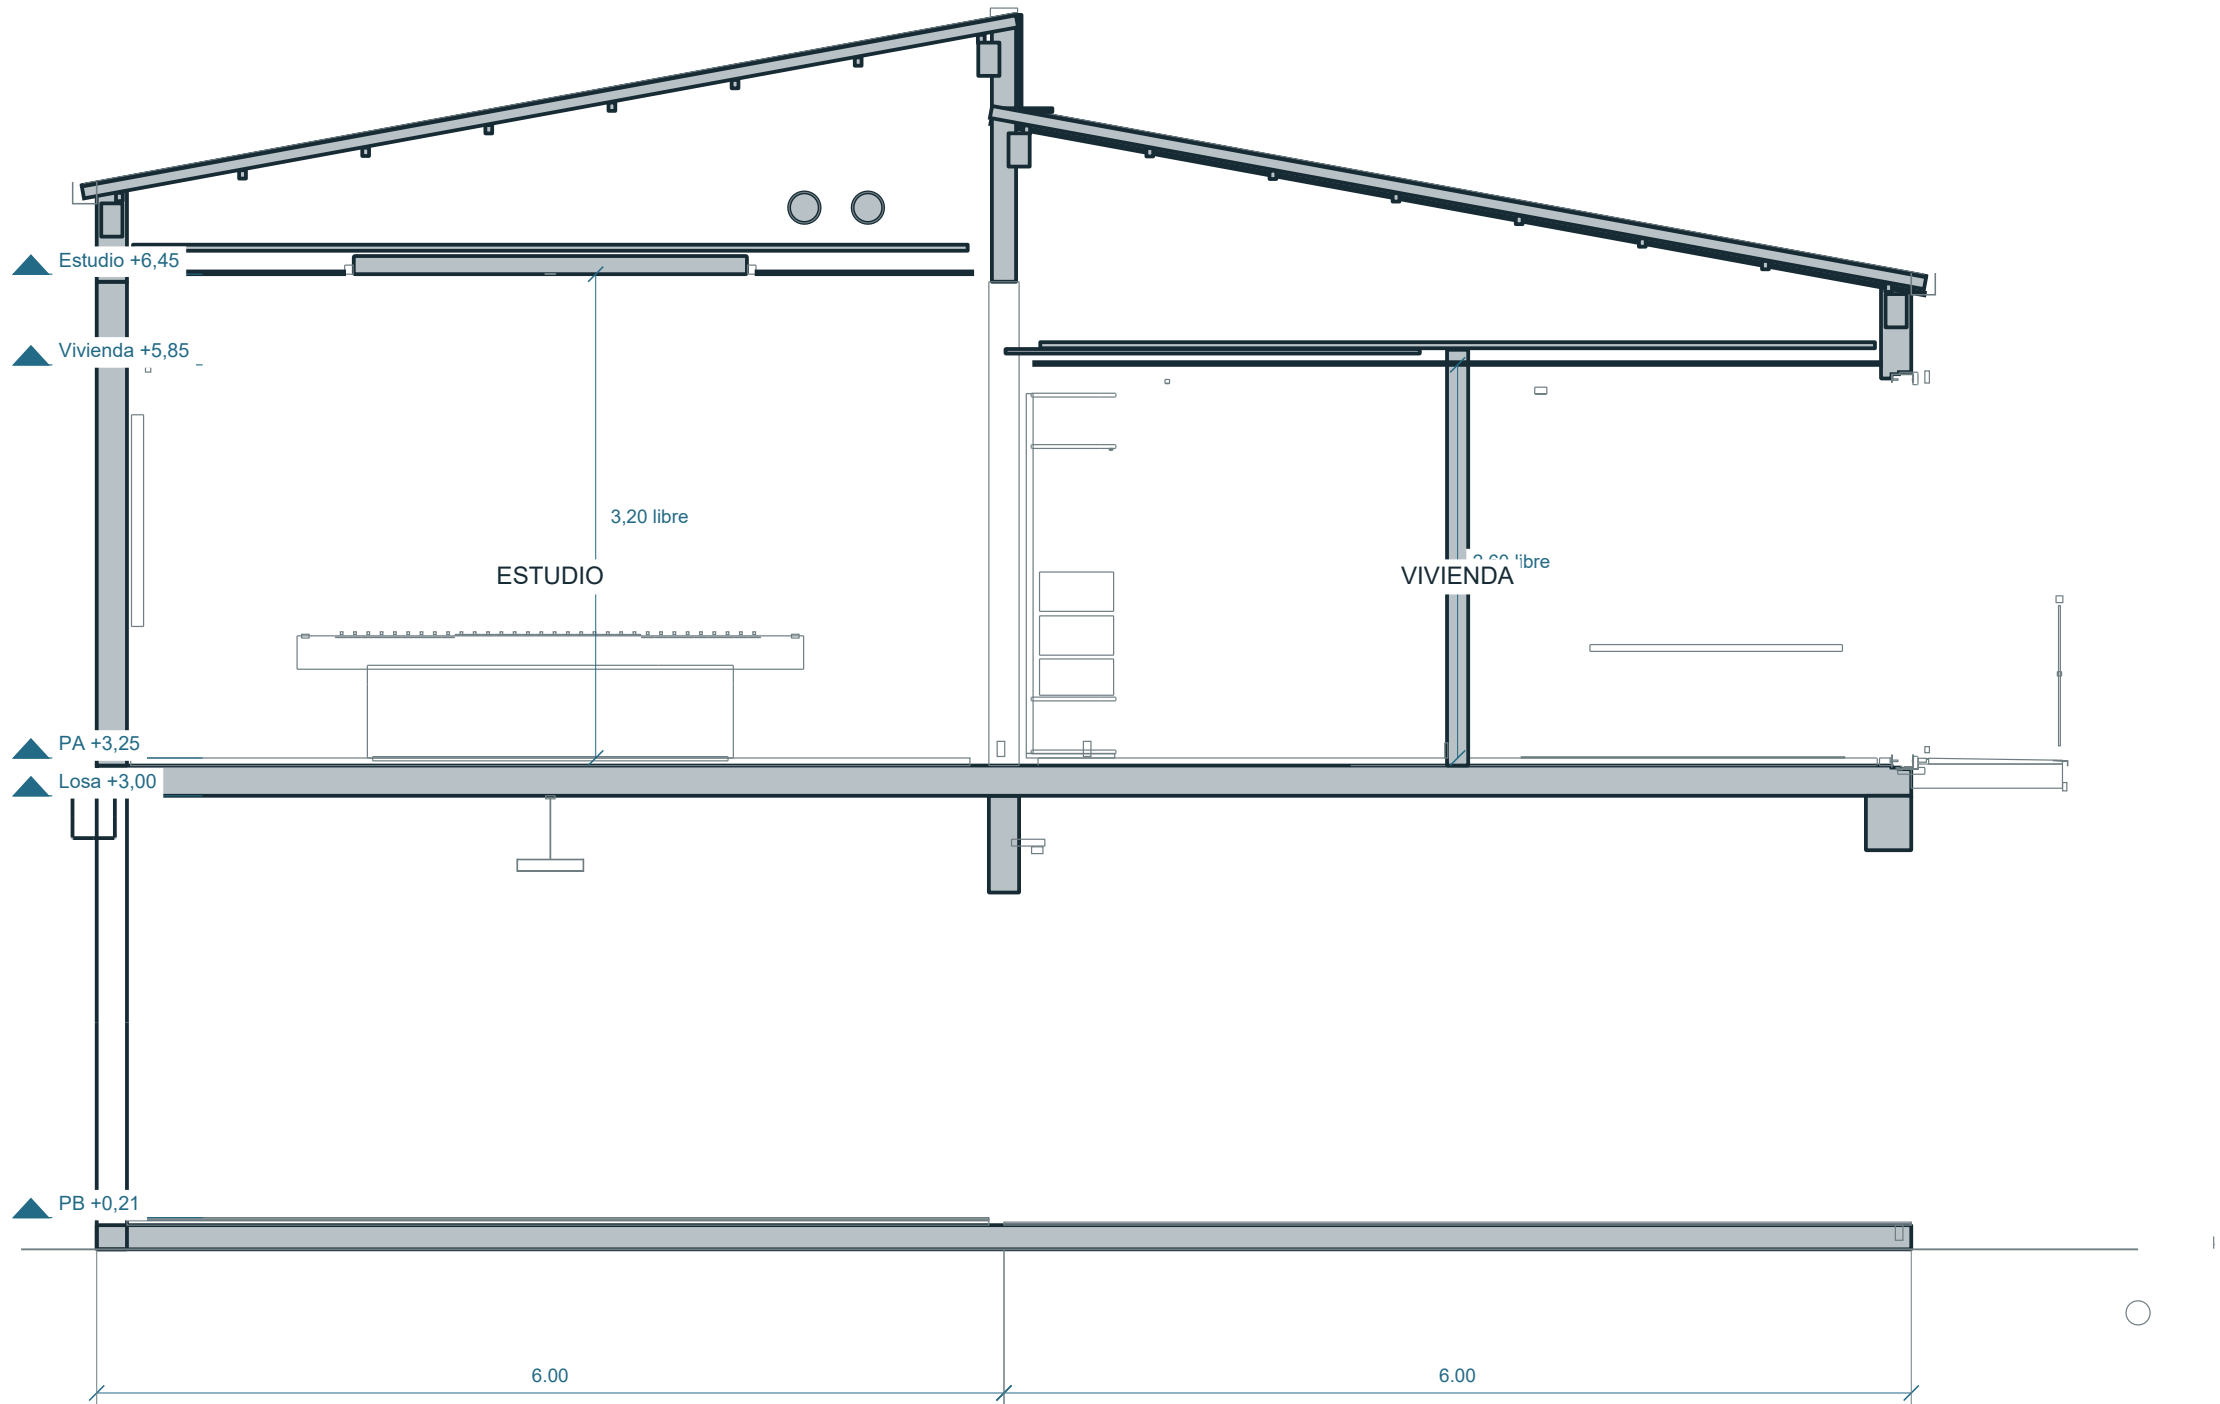

B-B Transversal por estudio | 1:50

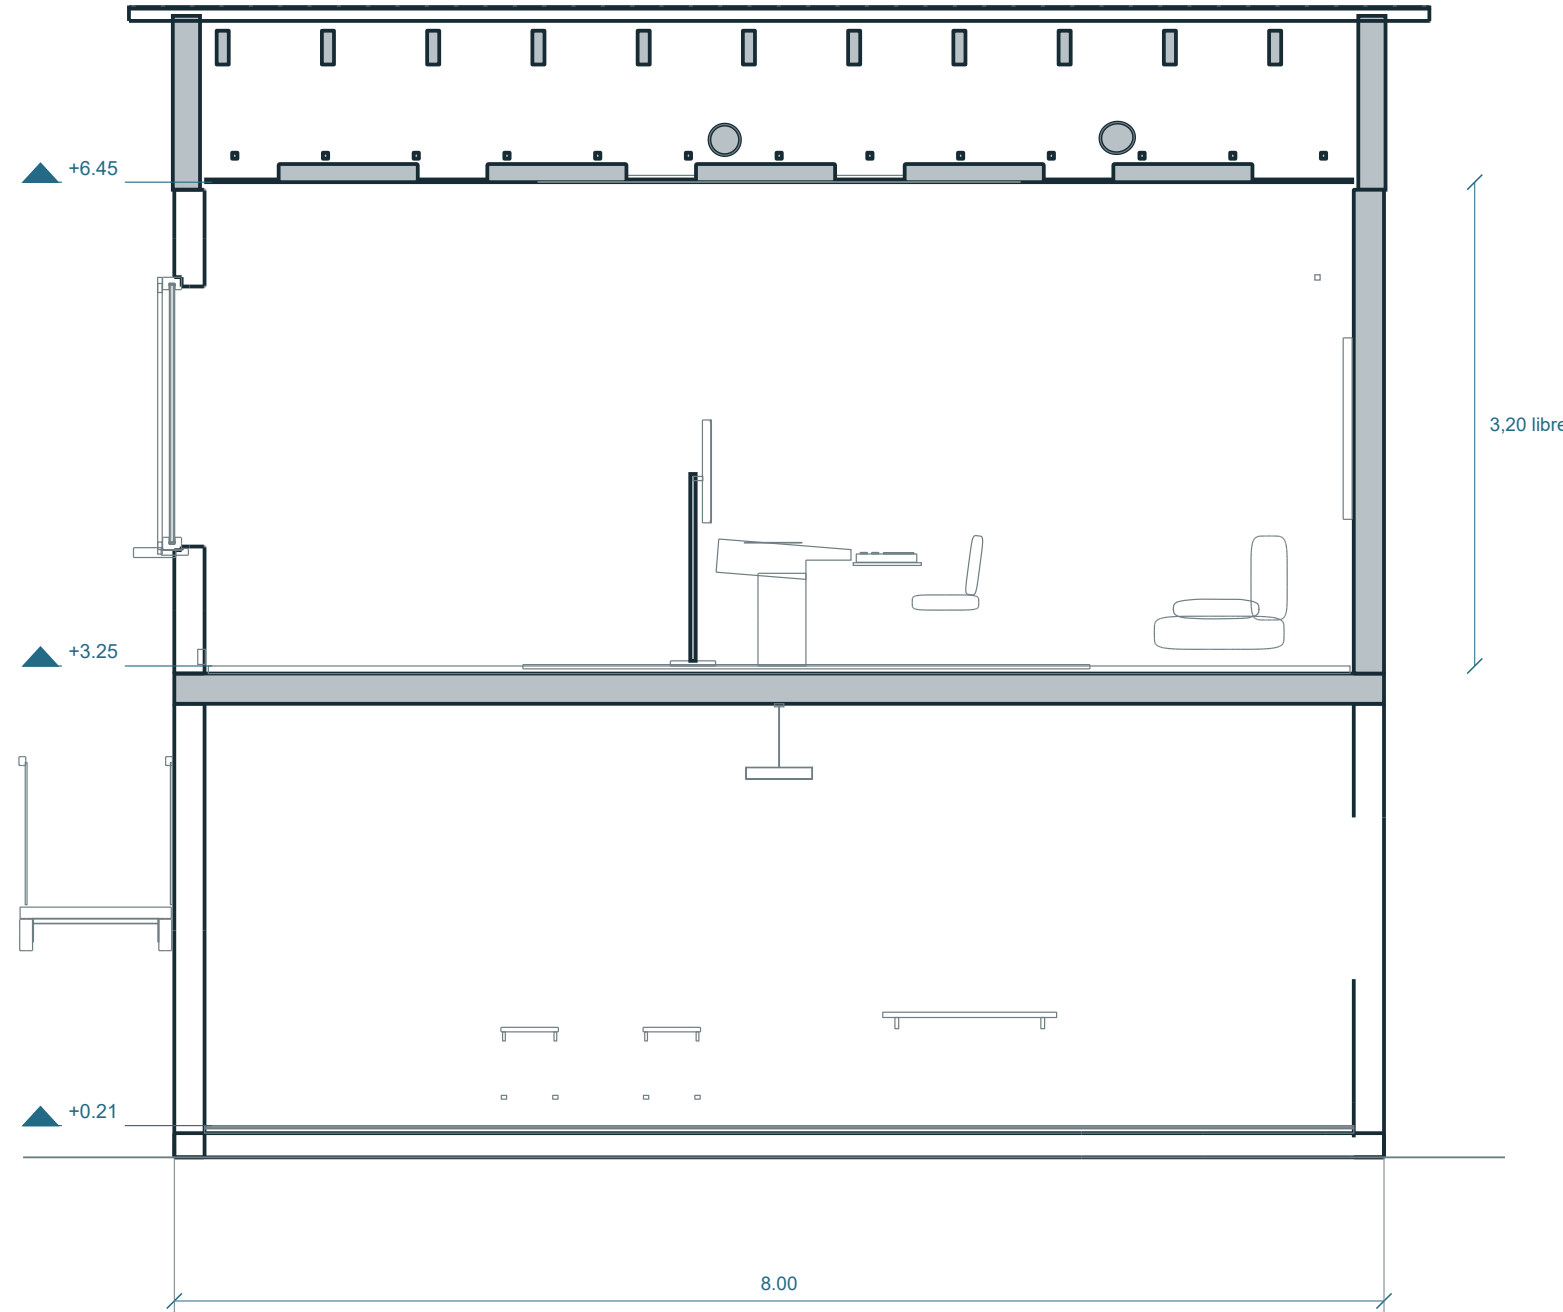


NIVELES Y CONSTRUCCION

G: losa entre plantas 0,20 m; piso general superior 0,05 m; cielorraso estudio +6,45 y vivienda +5,85. Corte A-A comprueba ambos volúmenes y el escalon exterior.


F: alturas libres autorizadas 3,20 / 2,60 m. La diferencia se conserva sin desplazar la implantación ni las huellas de los ambientes.

P: continuidad de cargas, fundaciones y conexiones por dimensionar. No hay estudio geotécnico ni verificación estructural; ver A14.


01 Planta / acceso | 1:20

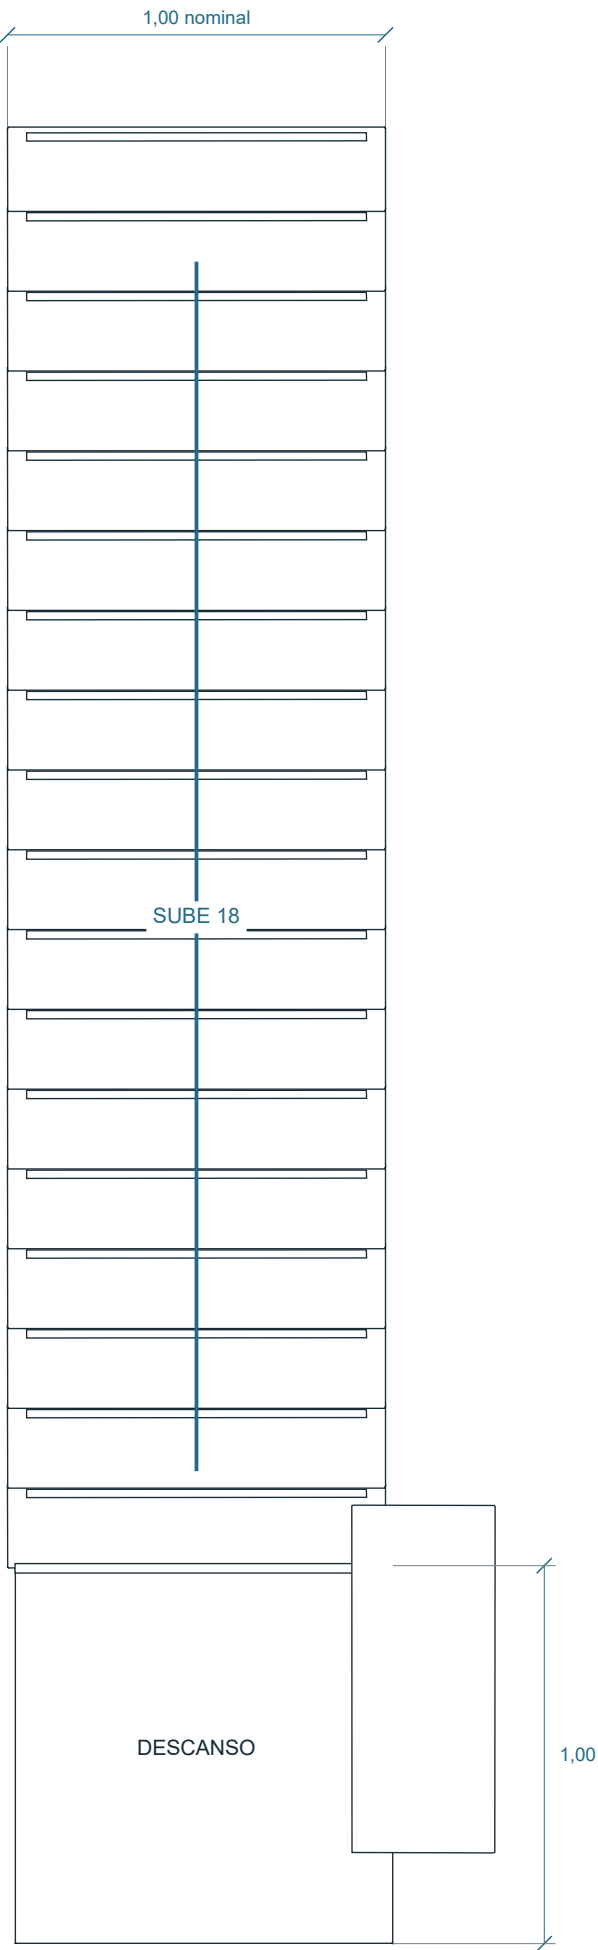

02 Seccion y proyeccion lateral | 1:20

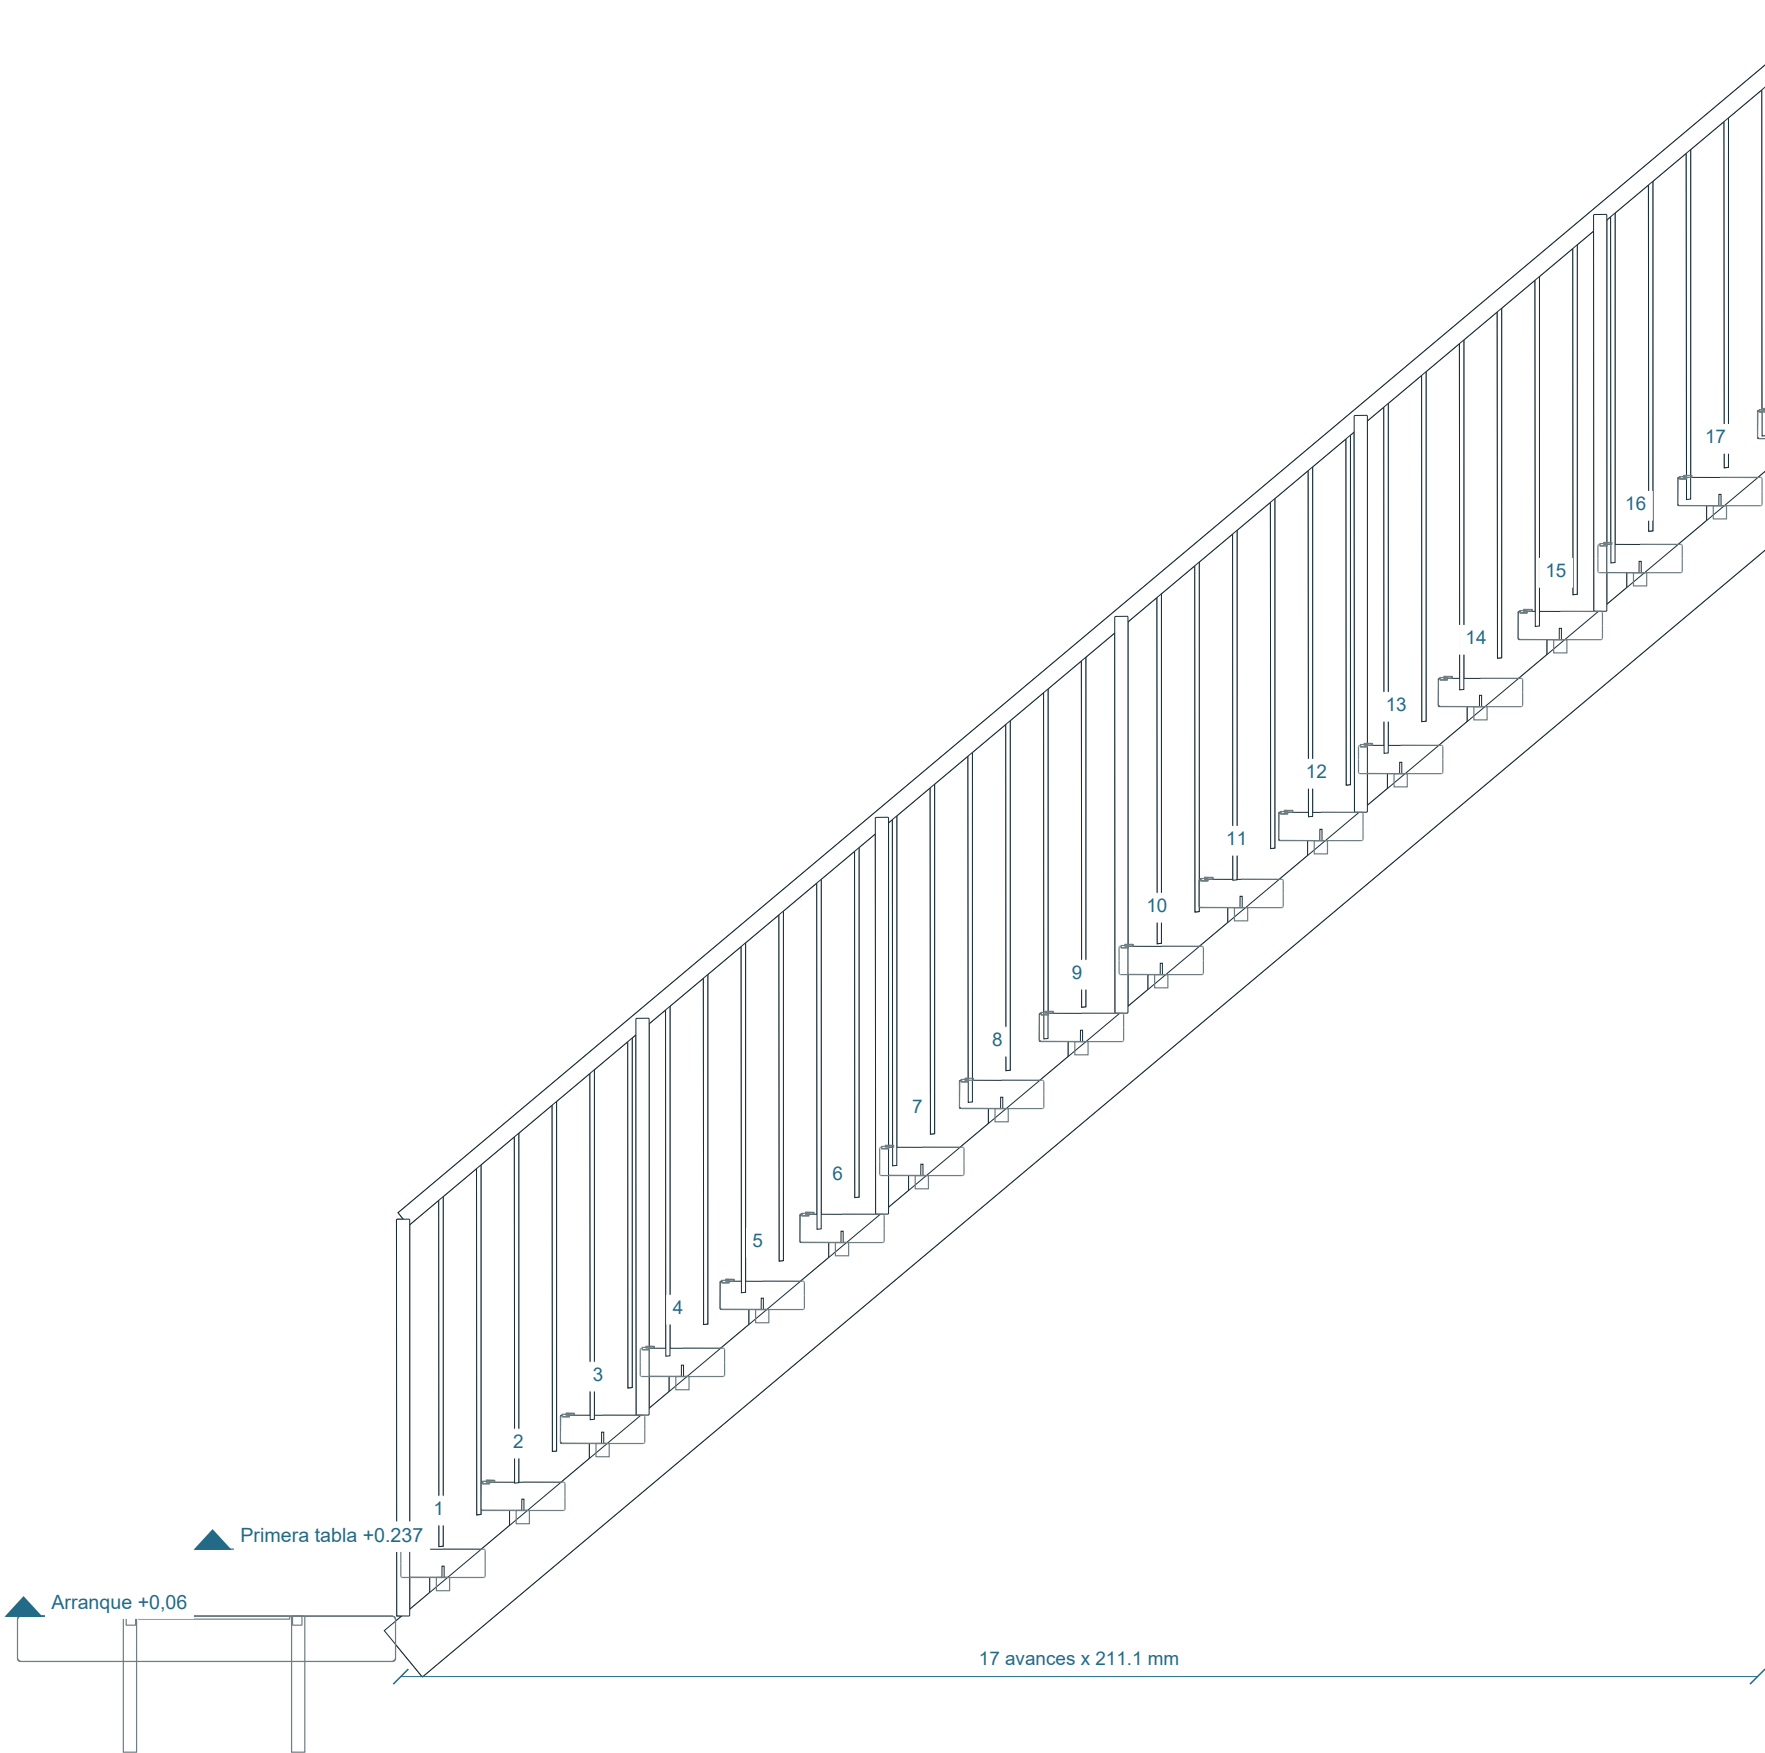

03 Umbral / corte Z=5,30 | 1:5

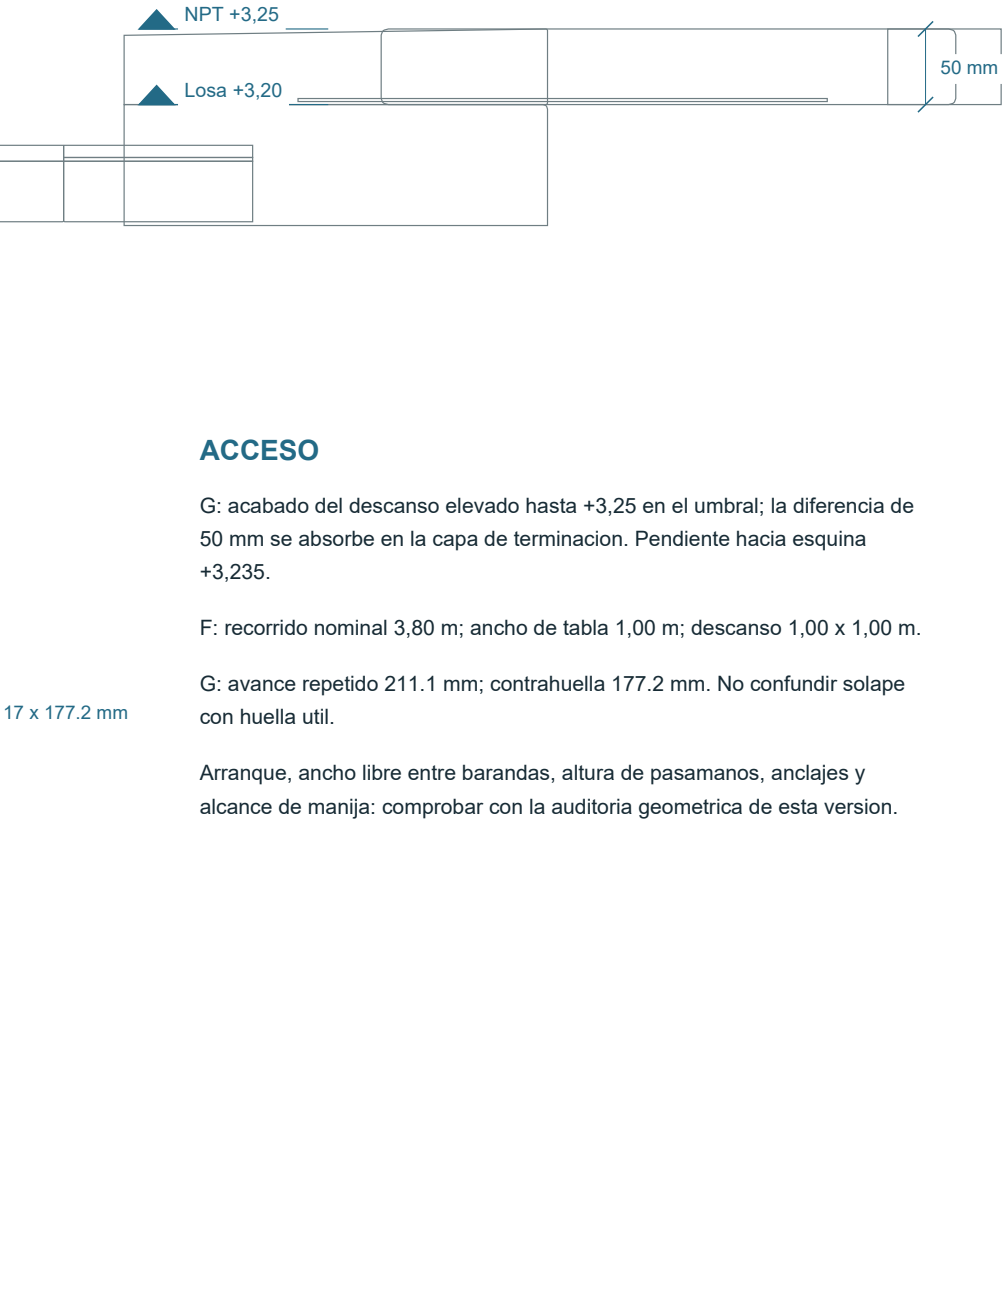

ACCESO

G: acabado del descanso elevado hasta +3,25 en el umbral; la diferencia de 50 mm se absorbe en la capa de terminacion. Pendiente hacia esquina +3,235.

F: recorrido nominal 3,80 m; ancho de tabla 1,00 m; descanso 1,00 x 1,00 m.


G: avance repetido 211.1 mm; contrahuella 177.2 mm. No confundir solape con huella util.

Arranque, ancho libre entre barandas, altura de pasamanos, anclajes y alcance de manija: comprobar con la auditoria geometrica de esta version.

COMPROBACIONES DE USO Y ANCLAJES

G soportes peldaños: tubo hueco35x35x3 sobre cartelas6 a zancas; narices embutidas4 y saliente2mm. Geometria de fijacion propuesta, capacidad pendiente. A14 y D05/D05b amplian apoyos.

01 Planta del vaso y playa humeda | 1:25

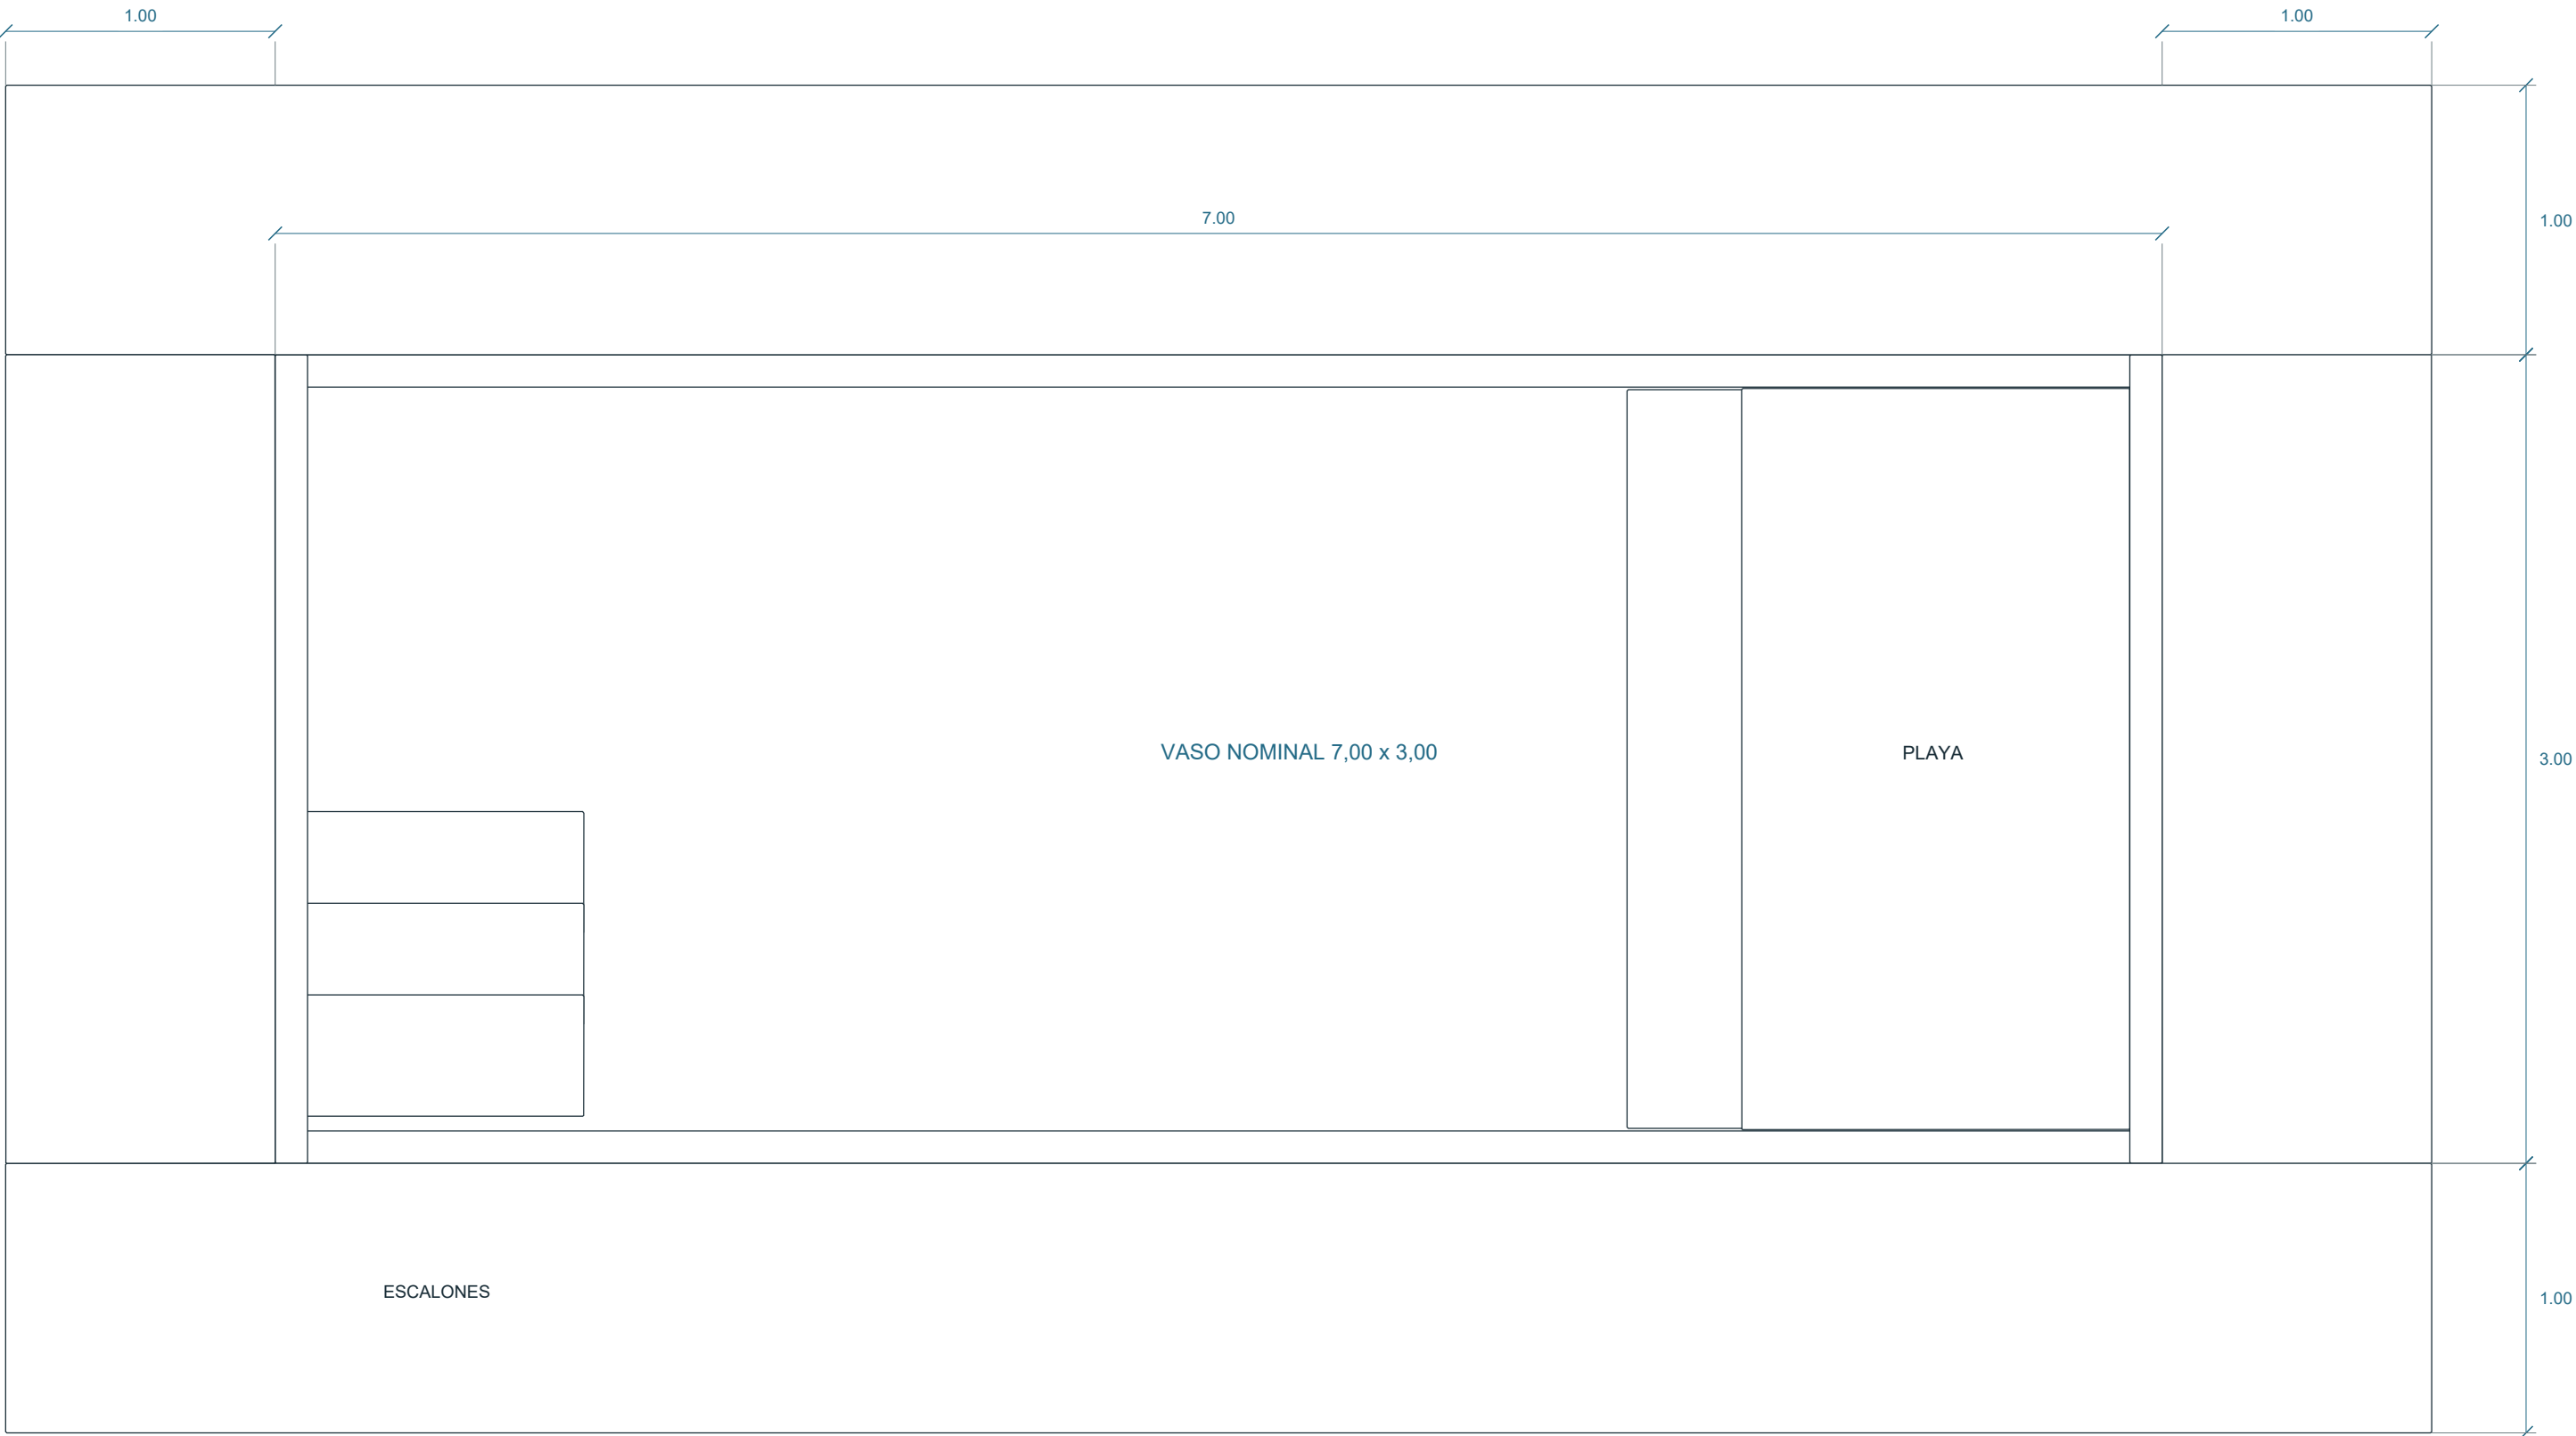

NIVELES DEL MODELO

G: pavimento perimetral +0,09 m; borde vertical del vaso hasta +0,07 m.

G: fondo del vaso entre -1,57 y -1,39 m; espesor representado 0,18 m.

G: tres escalones con caras superiores -0,14 / -0,43 / -0,72 m.


G: playa humeda -0,080 m; agua -0.030 m; profundidad actual 50 mm.
Escalon intermedio -0,31 m.




G cresta de agua -0.030 m; resguardo geometrico 100 mm al borde. P nivel operativo sujeto a proyecto hidraulico.

G: agua recortada contra vaso, playa y escalones; fondo de agua -1.390 m, coincidente con cara superior del vaso. Proyecto hidraulico P pendiente.

P: skimmer, retornos, filtrado y desague por dimensionar y coordinar.
Esquema en A15.


02 Corte transversal al largo / Z=16,50 | 1:50

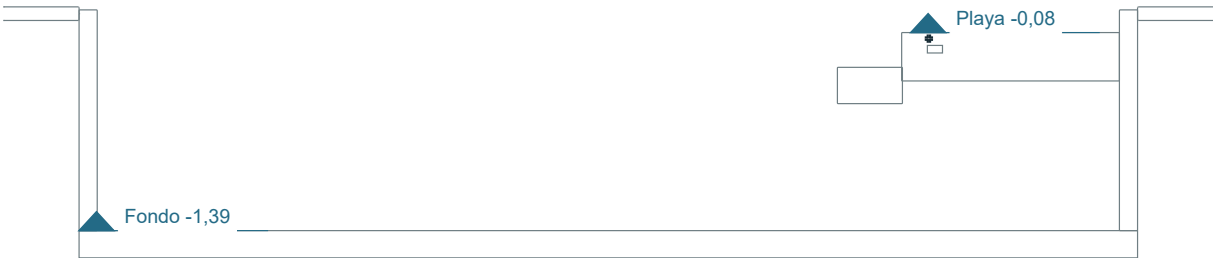

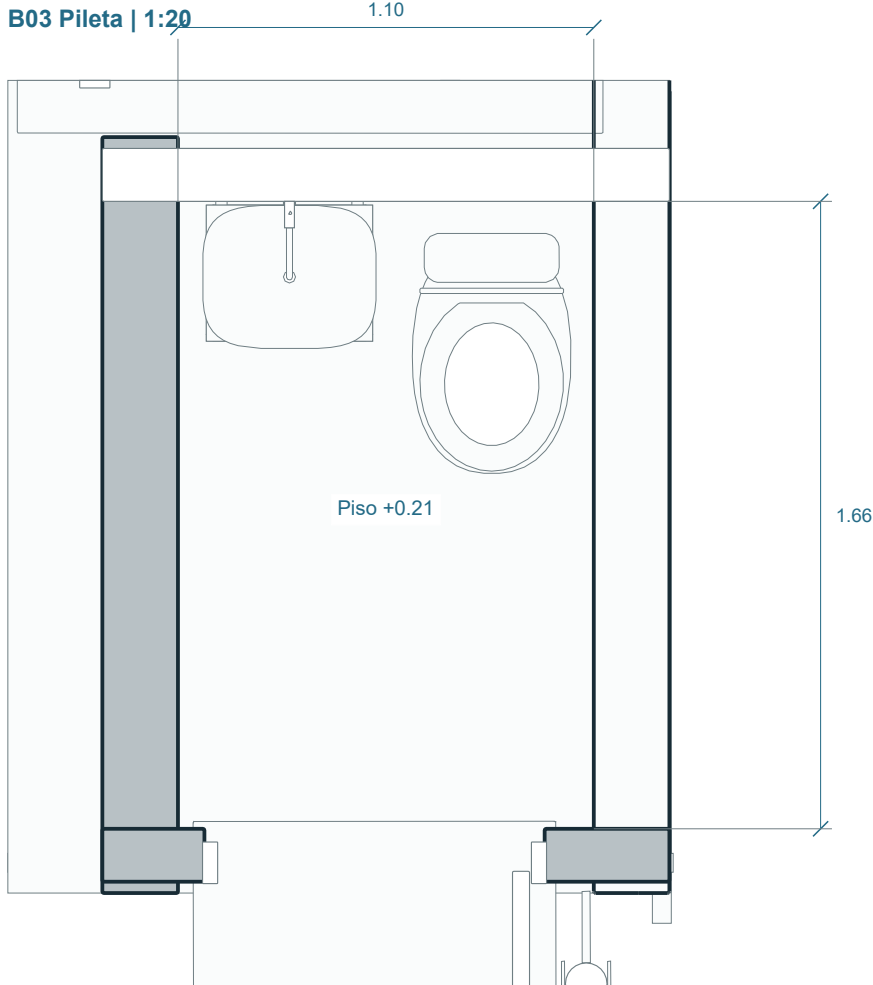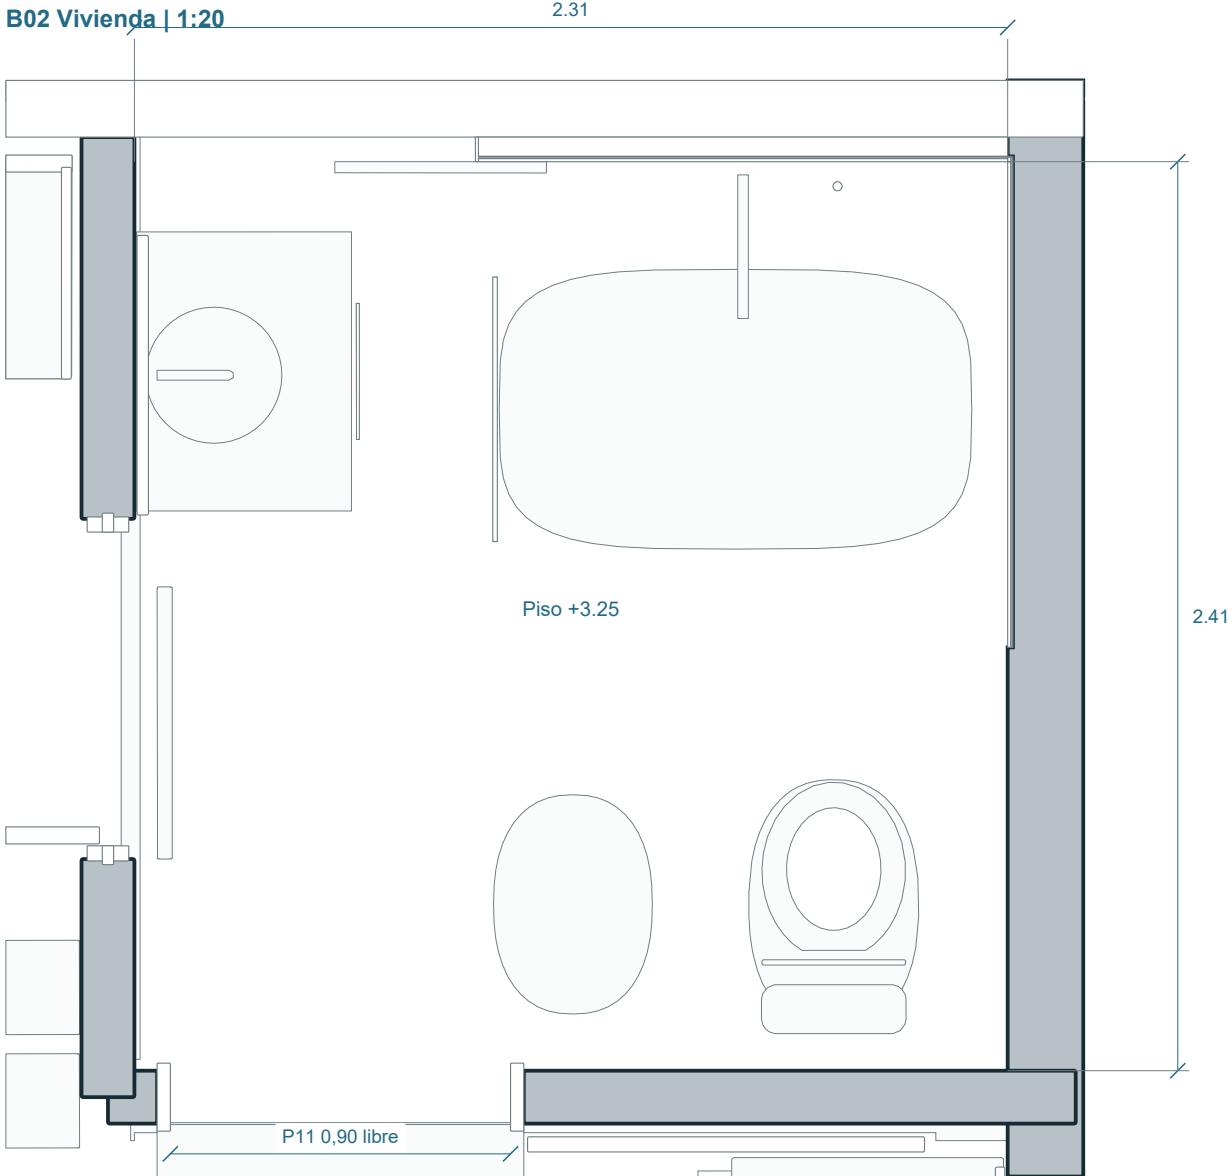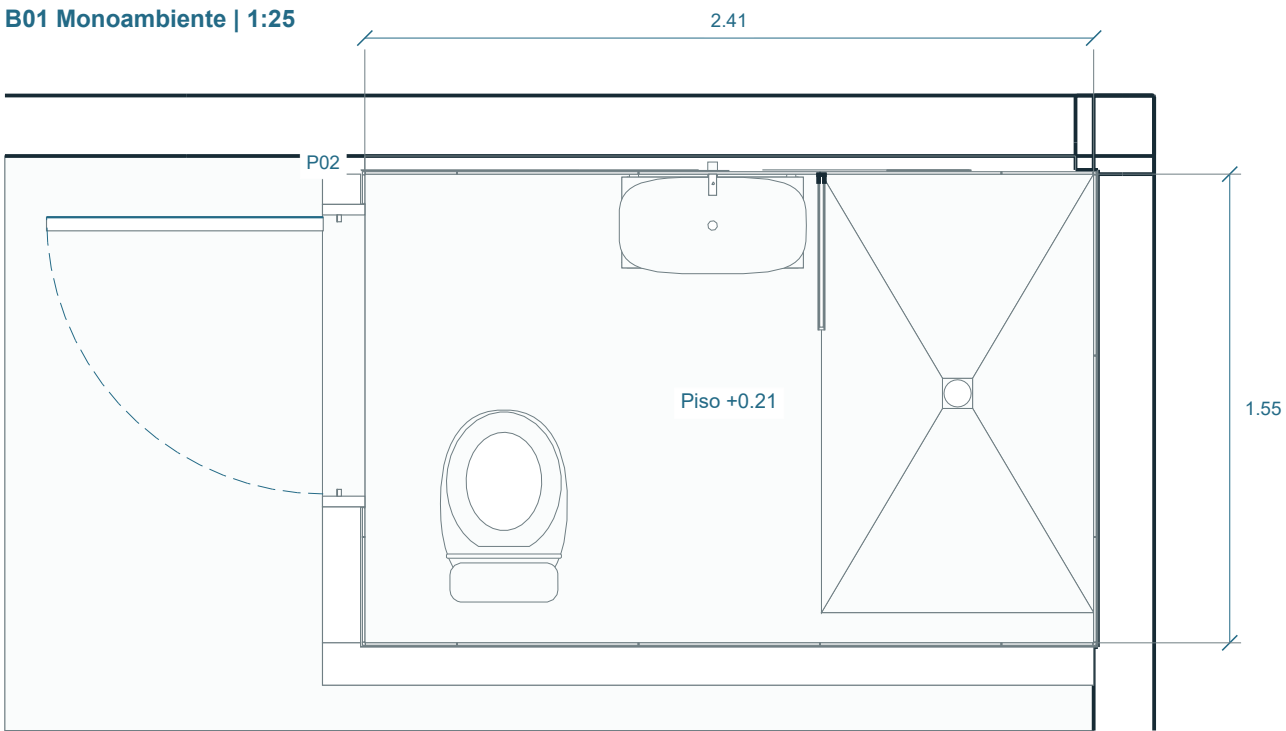


G: artefactos y mamparas de la malla actual; cotas interiores entre caras. D09 detalla piso continuo PA; D11 capas, sumidero y altura de ducha PB. Accesos de mantenimiento, productos y ensayos pendientes; hojas en A12.


Elevacion interior / artefactos | 1:25

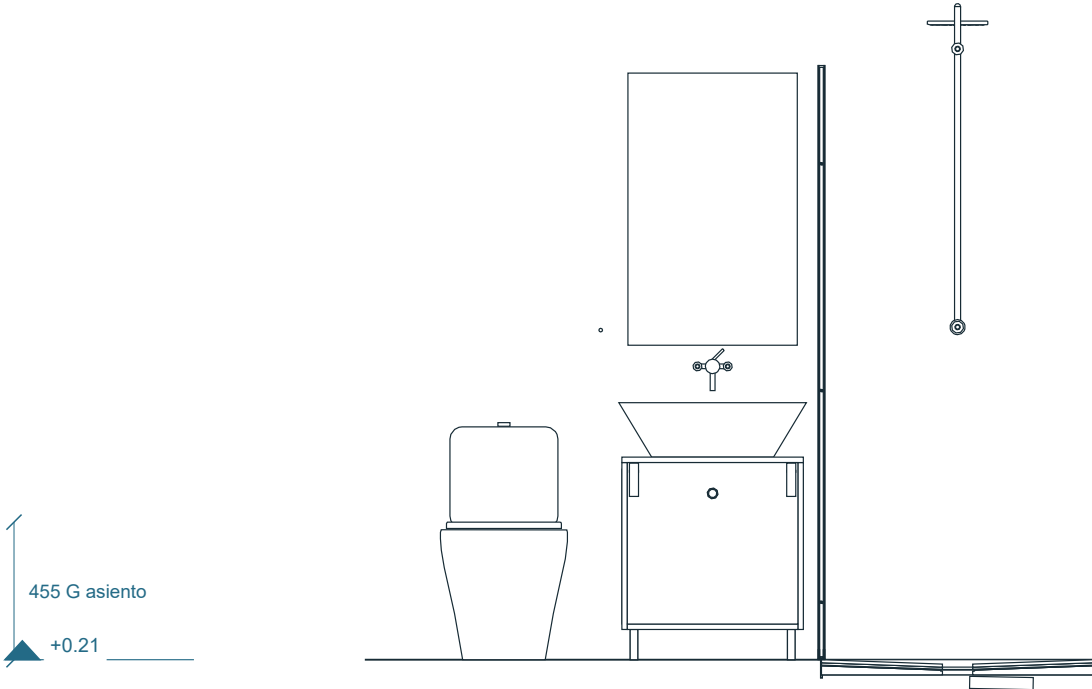


WC y bidet / hacia muro posterior | 1:20

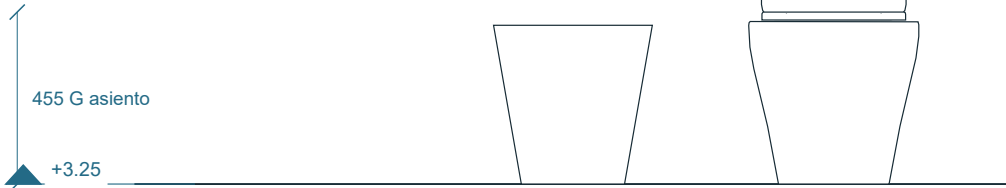

Elevacion interior / artefactos | 1:20

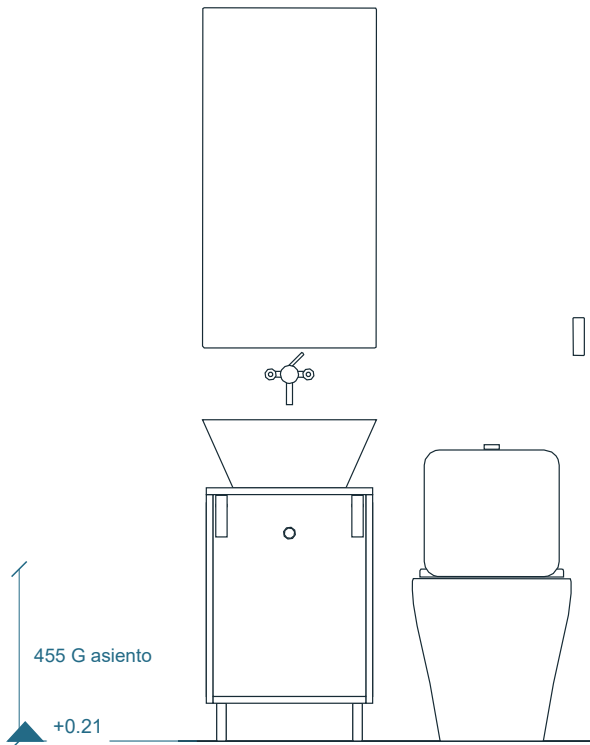

01 Línea del quincho | 1:25

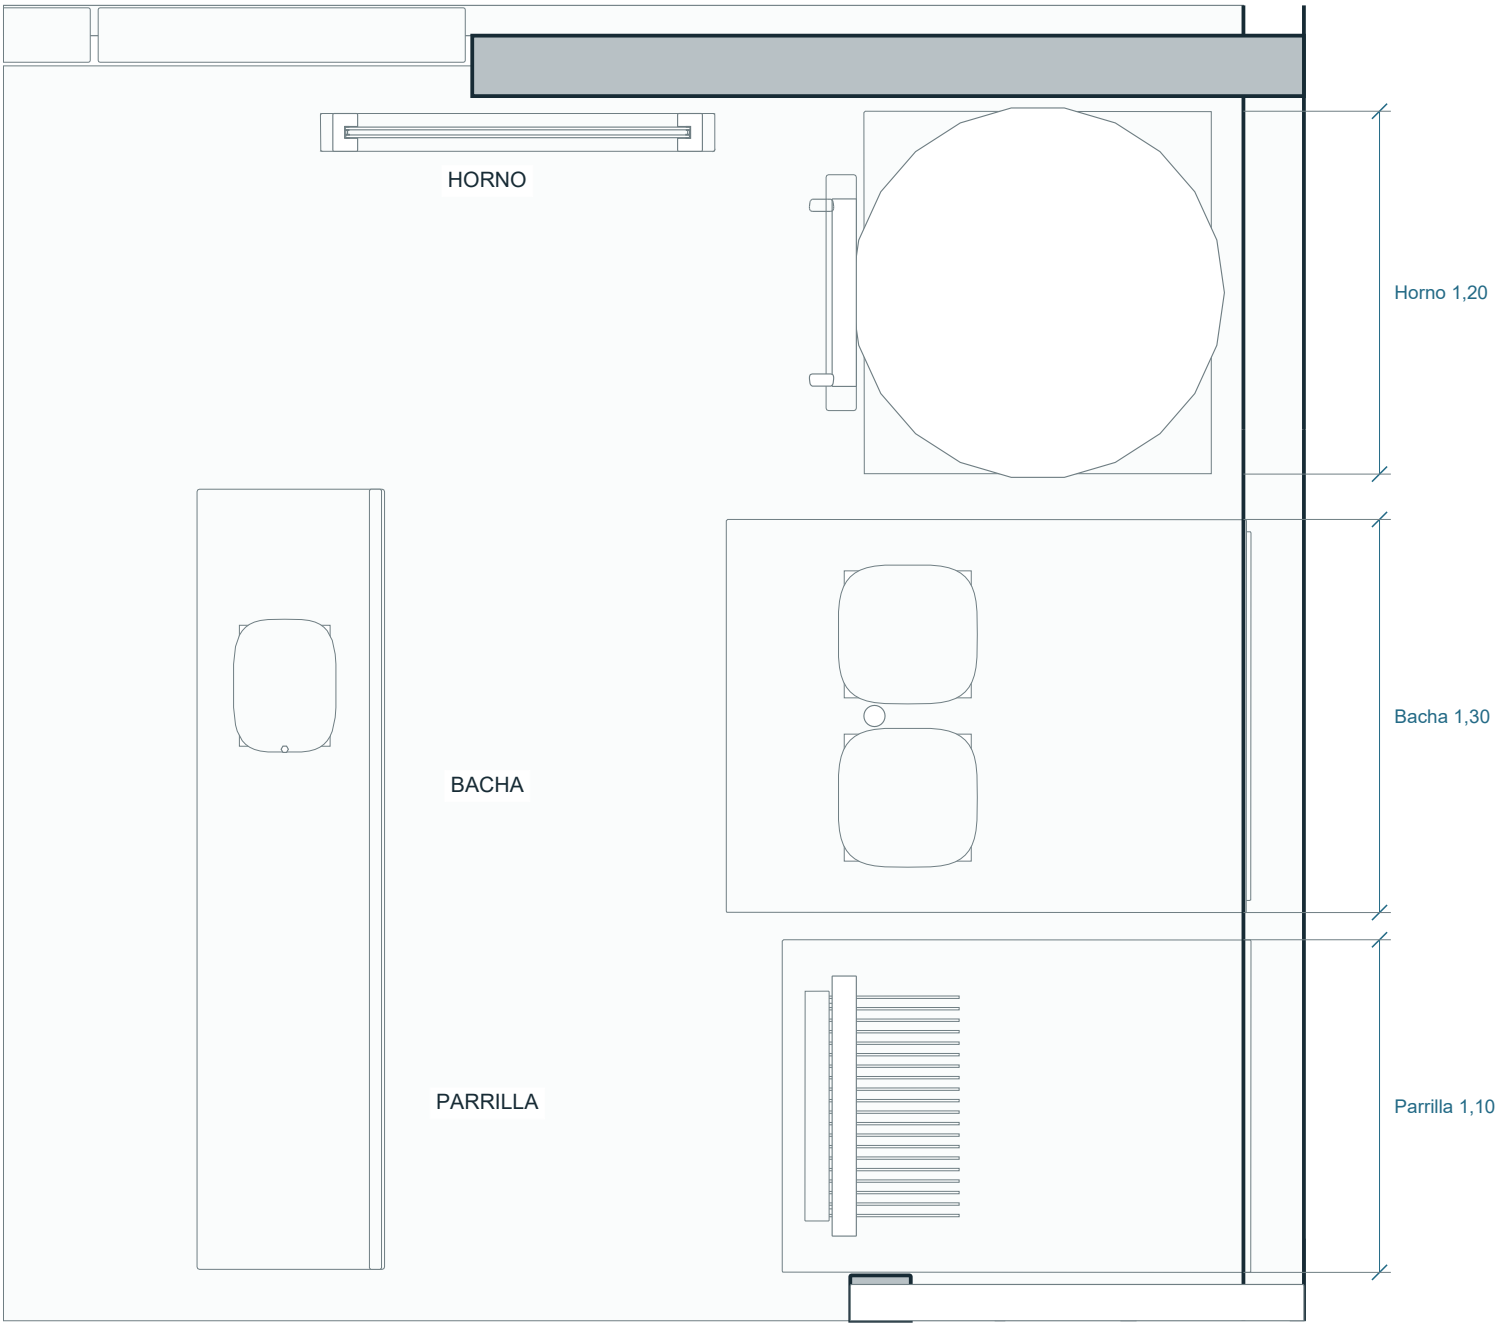


ALTURAS Y RELACION CON LOS LOCALES

G: cotas absolutas medidas de trabajo: mesa quincho +0.930; mesa comedor +4.000. No equivalen a altura desde el piso.


Comparar alturas de trabajo descontando el piso terminado de cada ambiente. No se confunden cotas absolutas con altura sobre piso.

La campana, el faldon y la boca de cada equipo se leen en los cortes del modelo. El tiro de combustion no esta certificado.

02 Cocina mono / ver A10b | 1:50

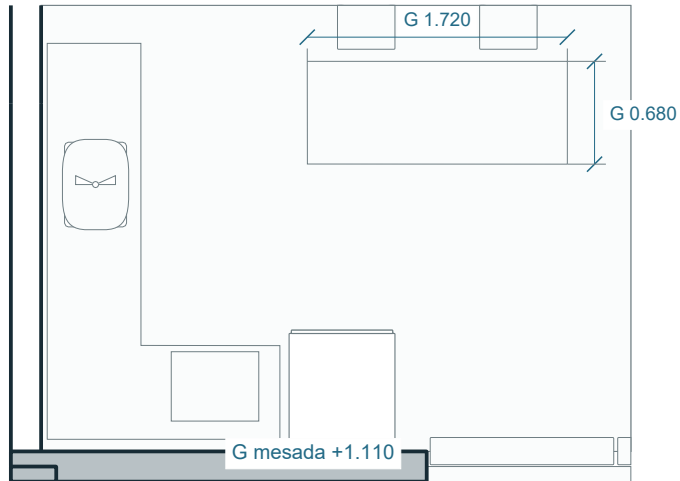

03 Cocina vivienda | 1:25

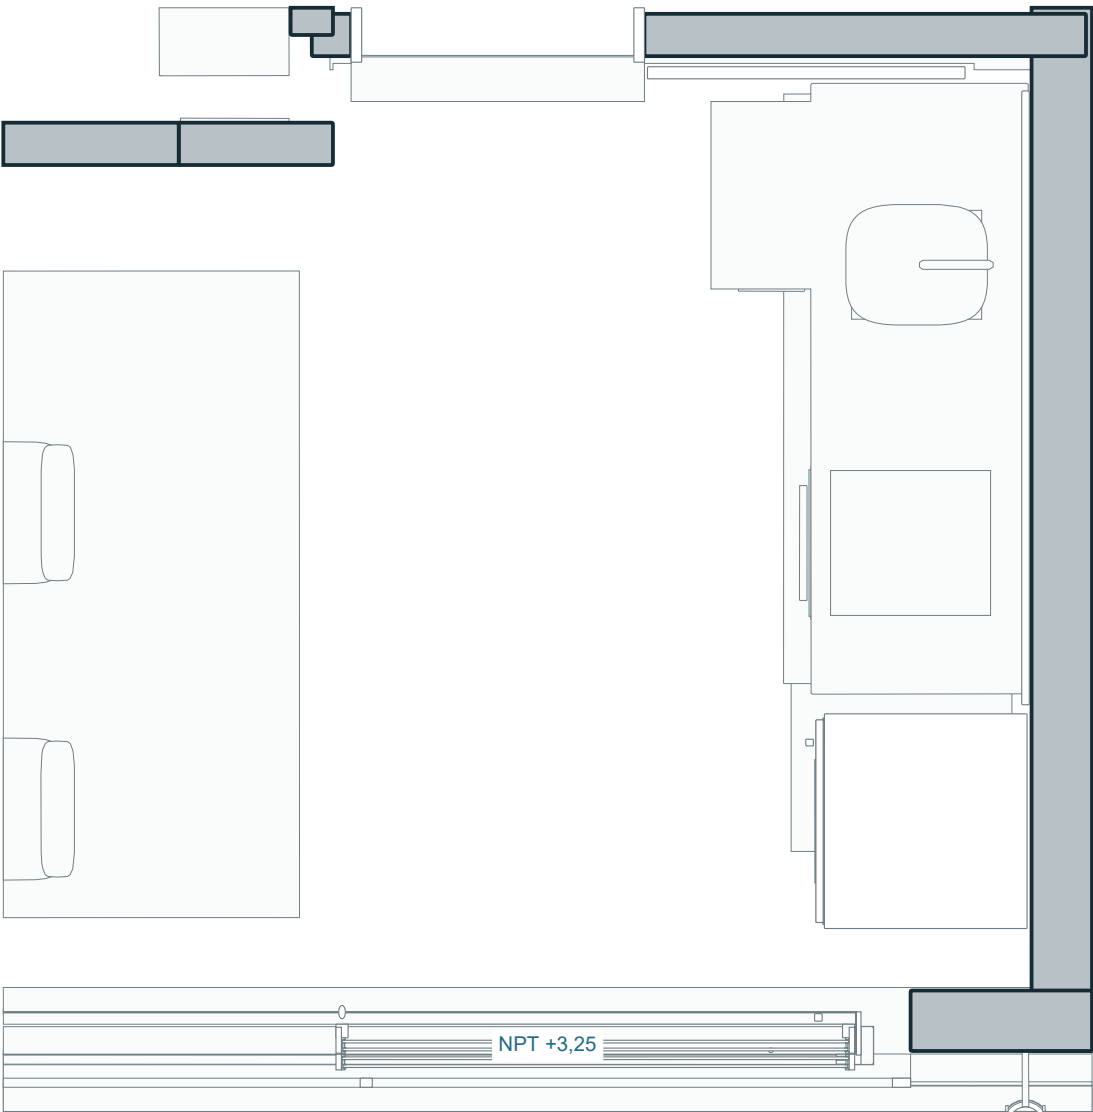

EXTRACCION Y MANTENIMIENTO

G: horno y parrilla con conductos independientes hacia el patinillo junto al estudio; cocina vivienda con salida independiente.


G: diametros representados de horno / parrilla ~0,21 / 0,32 m; son dimensiones de malla, no resultado de calculo.

P: verificar longitud desarrollada, radios, caudal, reposicion de aire, temperatura, aislamiento, registro y limpieza.

P: conexiones sanitarias de bachas y lavatorios, llaves de corte y sifones requieren detalle de instalacion. A15 ubica los puntos de coordinacion.

El patinillo comparte proximidad con el estudio. A11 identifica control termico, vibratorio y acustico pendiente.

01 Planta completa / piso +0,21 | 1:25

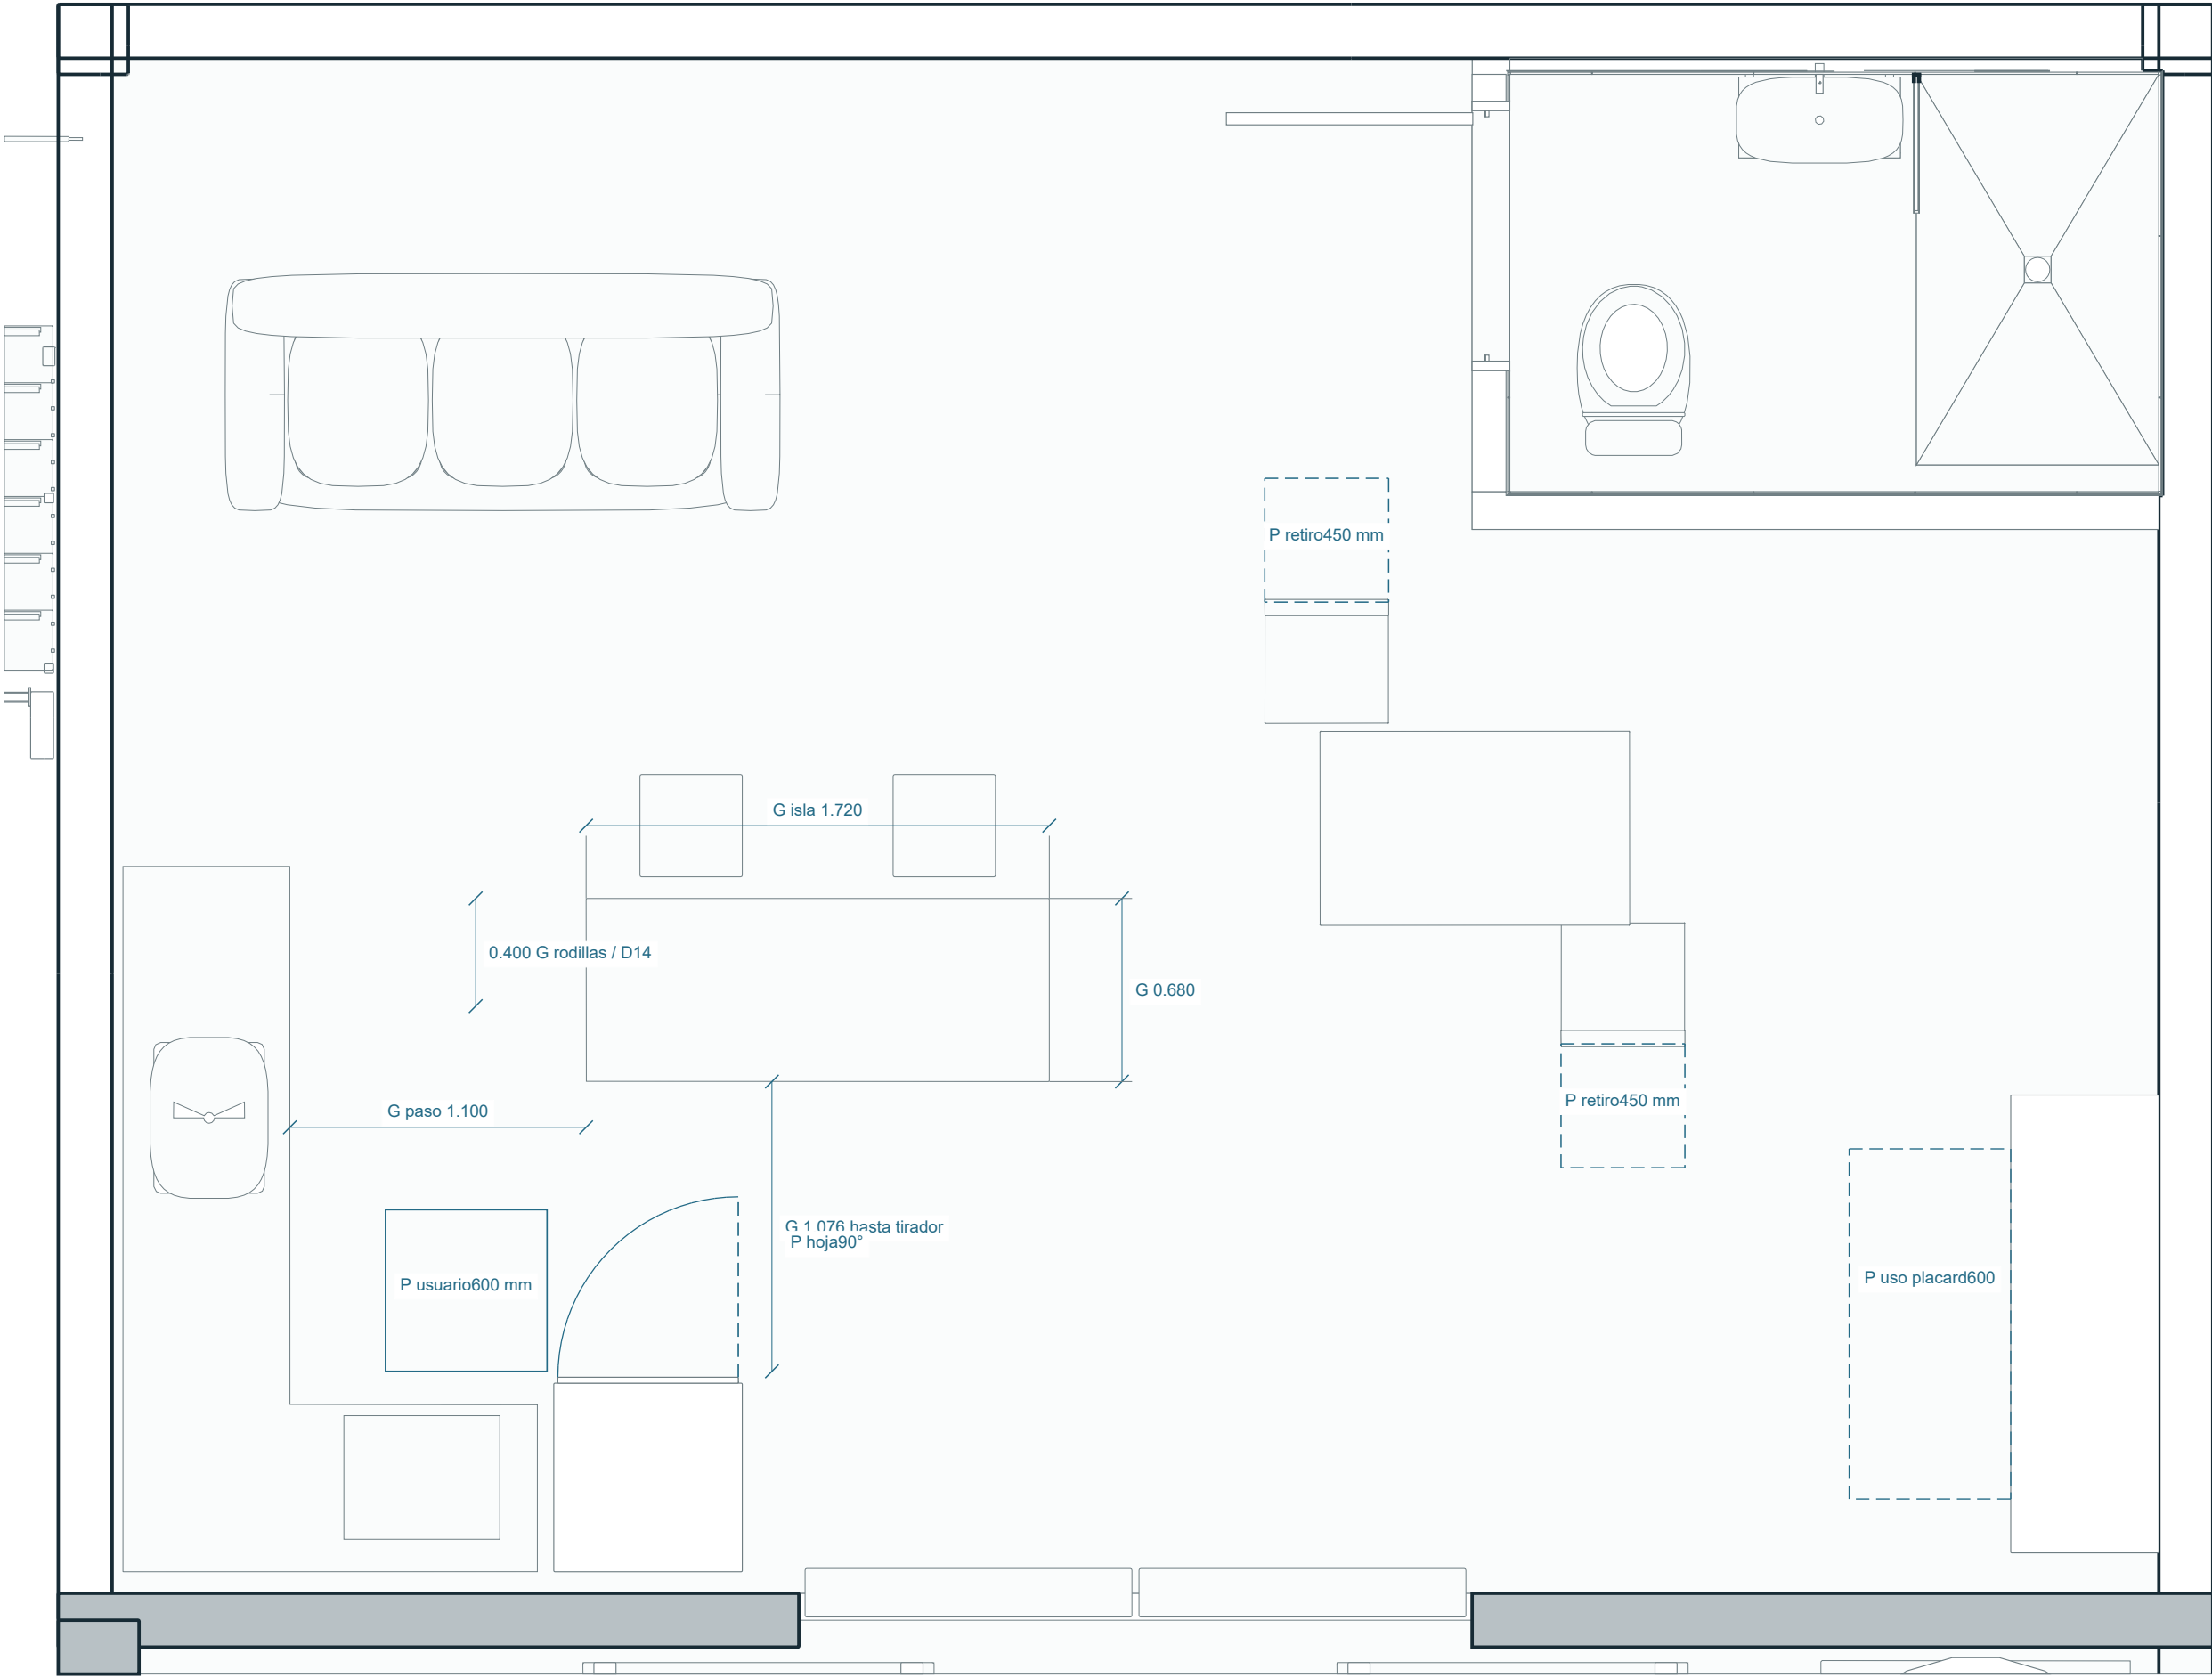

G: cotas tomadas del modelo, incluyendo el tirador que reduce el paso a la heladera. P: huella de uso y criterios de coordinacion. No se sustituyen medidas por dimensiones nominales de catalogo.

Mesa / altura G	0.750 m
Asiento silla / G	0.460 m
Mesada-isla / G	0.900 m
Piso terminado / G	+0,210 m
Paso hasta tirador / G	1.076 m
Rodillas / fondo G	0.400 m
Taburete / entre patas G	0.305 m

ALCANCE DE LAS HUELLAS P


P: usuario600 mm al lado del barrido de heladera y hoja abierta90° con eje derecho propuesto por tirador izquierdo. La seleccion del equipo debe confirmar mano, carrera y acceso.

G: posicion de muebles y sanitarios del modelo. P: retiro450 mm de ambas sillas en trazo discontinuo; no es pose guardada. A09 y D11 amplian los banos.

Herrajes, electrodomesticos y muebles no tienen marca/producto confirmados. G documenta geometria, no conformidad del producto o accesibilidad.


D14: cuerpos declarados, rodillas, bastidor y retirada alternada de taburetes. El paso posterior corresponde a plazas ocupadas; no equivale a accesibilidad certificada.


02 Mesa y sillas / elevacion G | 1:20

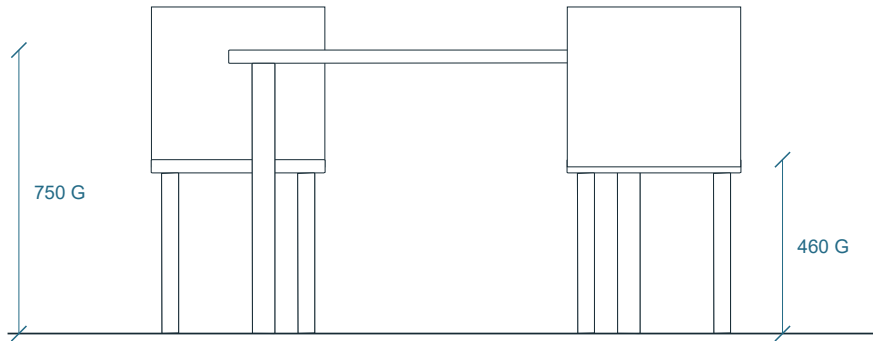

Alturas G sobre NPT +0,21. Aparatos y muebles genericos; sin producto ni capacidad certificados.

03 Mesada / Z3,60 | 1:20

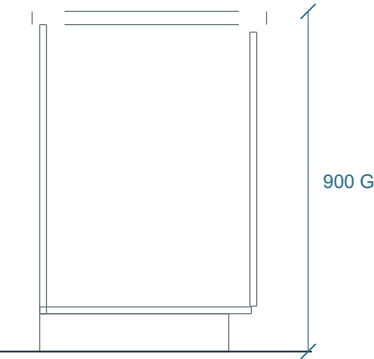

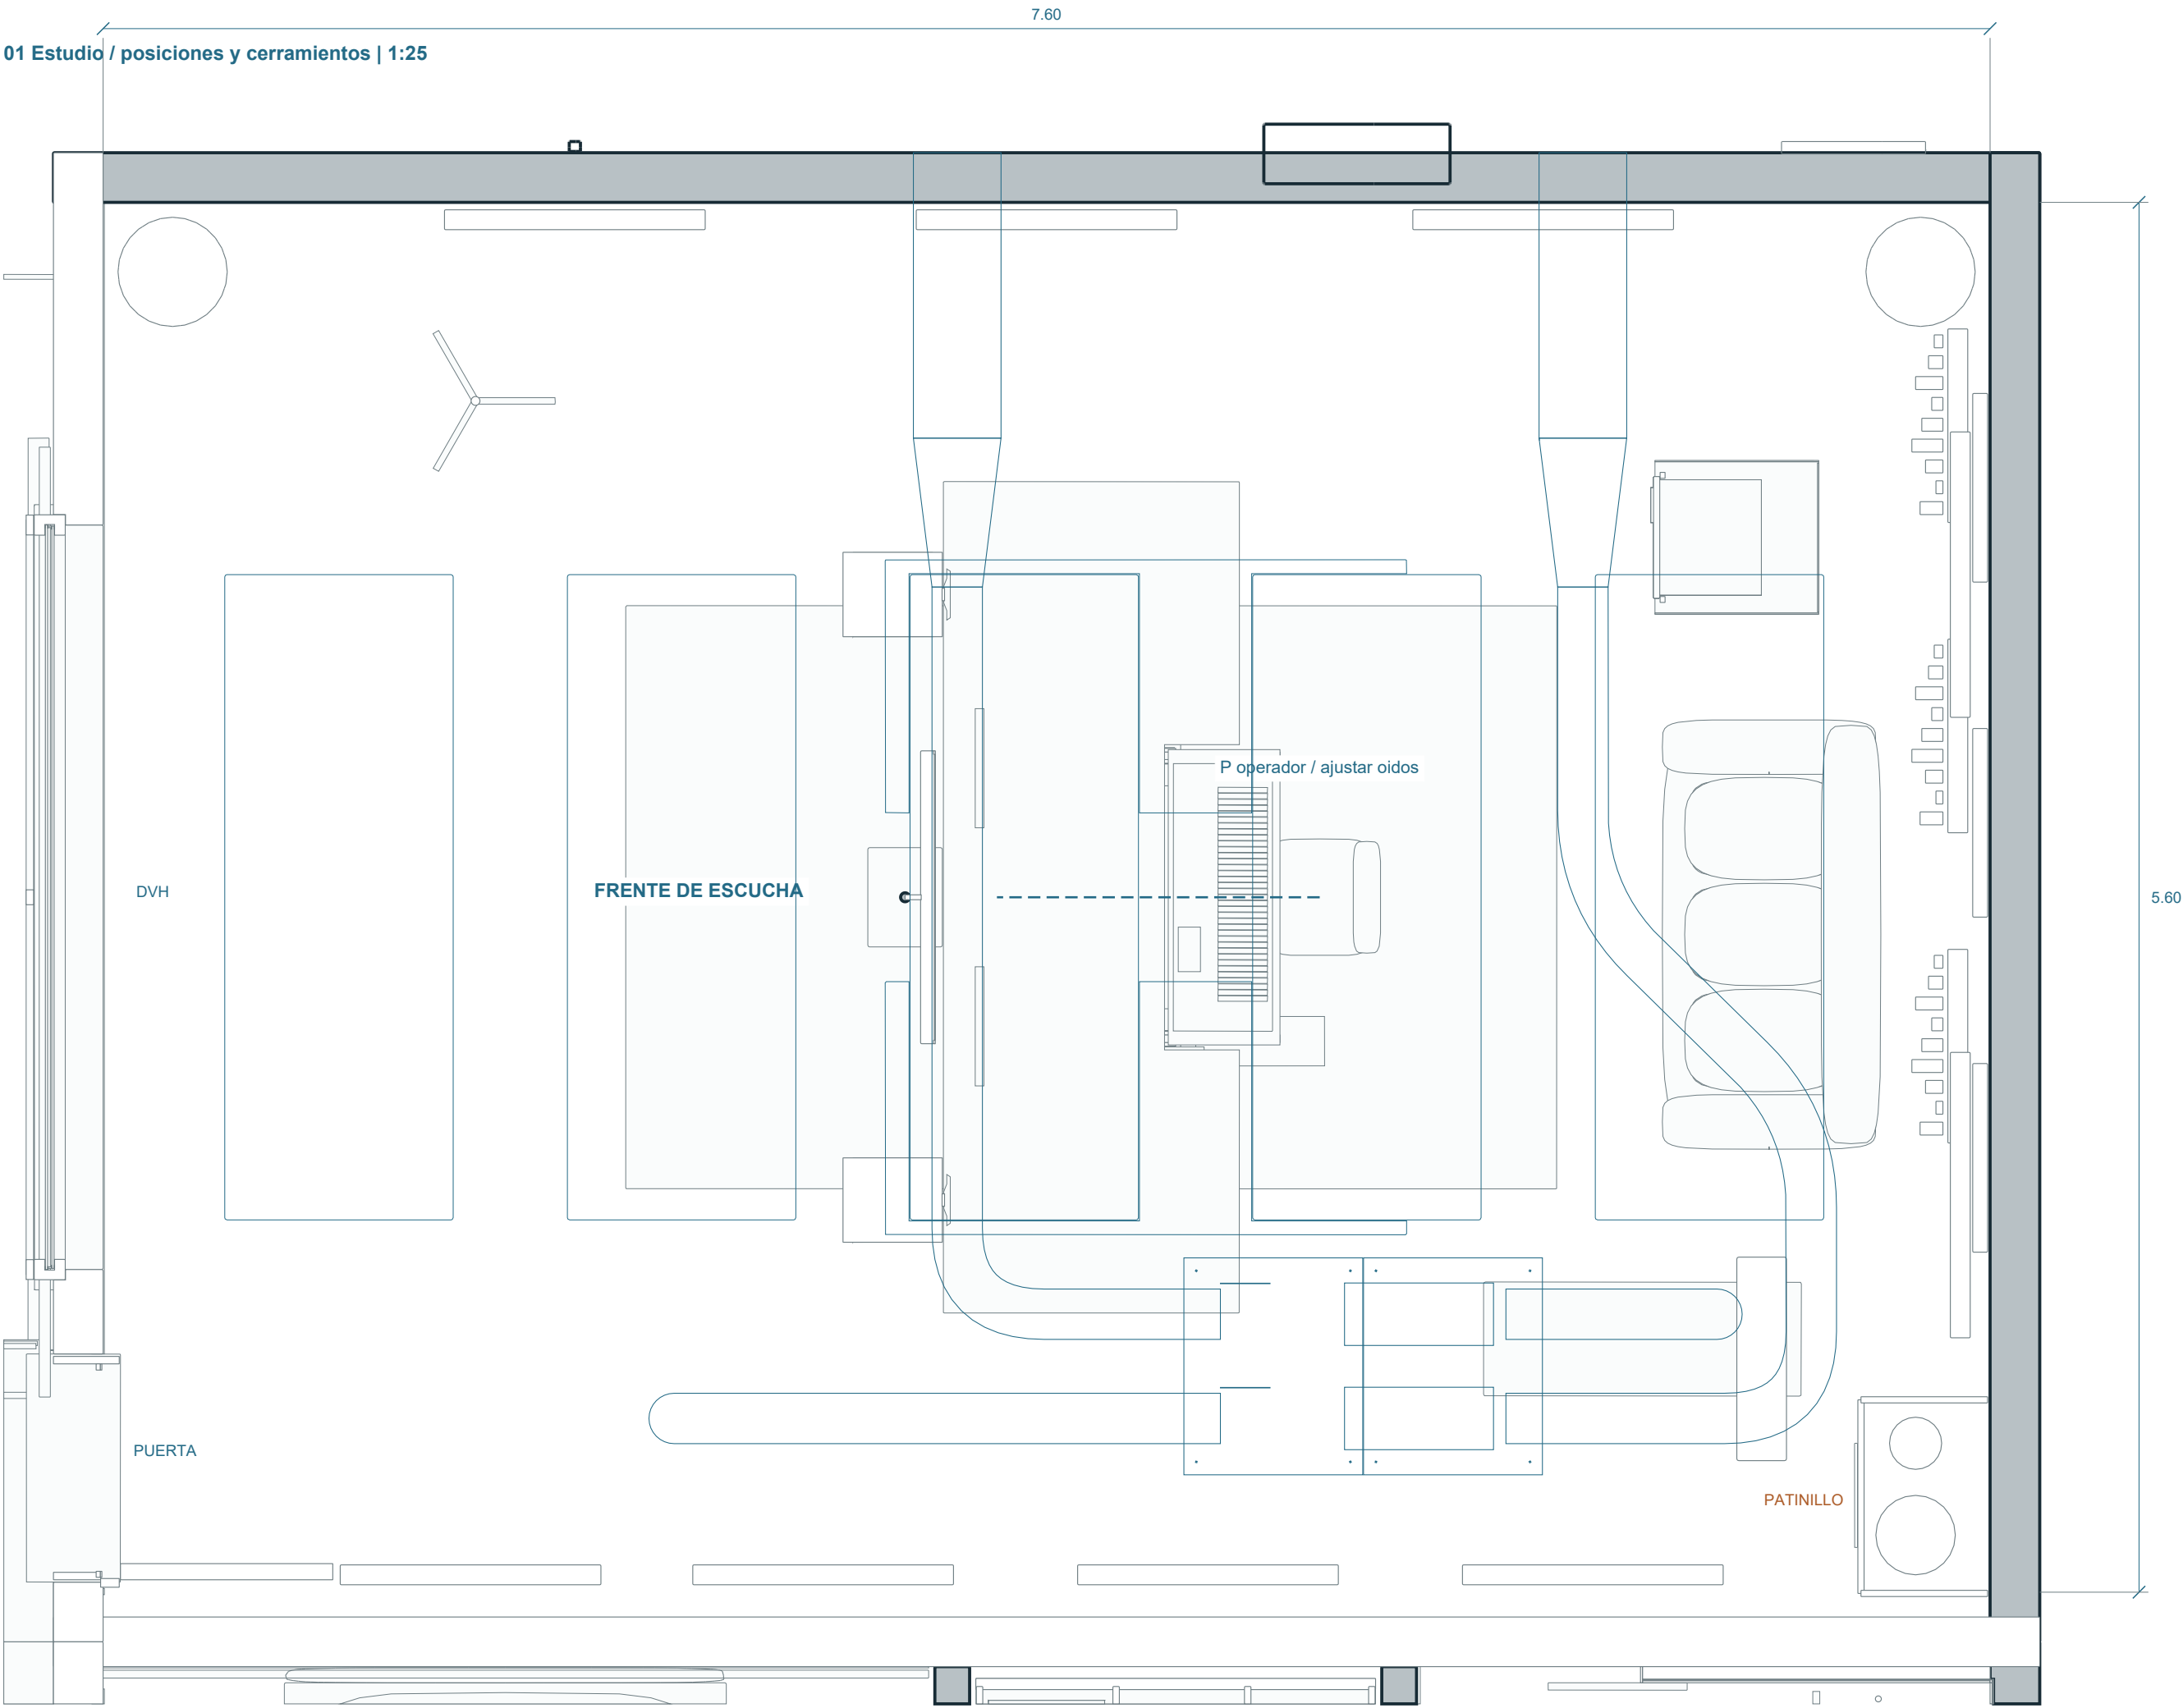

CRITERIO ACUSTICO PROPUESTO

- G: altura libre 3,20 m; cielorraso a +6,45. Paneles y nubes seccionados/coordinados con esa cota.
- P: identificar primeras reflexiones con posicion final de monitores y oidos. El trazado de escucha es una referencia grafica, no un calculo acustico.
- P: montaje dimensional, cierre hermetico y ventilacion en suplemento D06-D08; aislamiento, RT60 y ruido de fondo requieren calculo/medicion.
- P: sellado perimetral continuo en puerta, DVH y pasos; juntas elasticas y desacople donde el sistema constructivo lo requiera.
- P modelado:2 circuitos con filtros, ventiladores, silenciadores600 y ductosØ150; pasos frontales300x80. Registro1,40x0,83 y accesorios desde+6,453. D08 muestra montaje y retirada.
- P: patinillo de combustion: definir proteccion termica, separacion, juntas y acceso de limpieza sin comprometer el estudio.

PUESTO MIDI / VER D13

- G teclas blancas 750.0 / negras 762.5 mm; asiento 470 mm sobre NPT.
- G bandeja libre 665 mm. D13 muestra recorte, brazos, apoyo y operador P dimensionado.
- La postura y el montaje se distinguen de la capacidad resistente y del ajuste a cada usuario.

VERIFICACION PENDIENTE

Medicion o simulacion acustica con absorcion real de materiales, volumen util, posiciones definitivas y ruido de instalaciones. No se asignan valores de dB ni tiempos de reverberacion sin evidencia.

Ref.	Pieza medida G	Ancho m	Alto m	Base	Tope
P01i	Corredera PB / vidrio	1.140	2.300	+0.270	+2.570
P01d	Corredera PB / vidrio	1.140	2.300	+0.270	+2.570
P02	Abatible bano mono	0.915	2.200	+0.220	+2.420
P03	Abatible bano piletá	0.820	2.180	+0.210	+2.390
P04	Acceso estudio	0.855	2.340	+3.260	+5.600
P05	Dormitorio / estar	0.908	2.200	+3.260	+5.460
P06	Dormitorio	0.820	2.170	+3.260	+5.430
P07	Bano vivienda	0.820	2.180	+3.250	+5.430
V01	DVH estudio / paño	3.000	1.720	+4.060	+5.780
V02	Lateral dormitorio / paño	1.700	2.080	+3.840	+5.920
P08a	Corredera lateral A / vidrio	1.150	2.540	+3.220	+5.760
P08b	Corredera lateral B / vidrio	1.150	2.540	+3.220	+5.760
P09	Corredera posterior A / vidrio	1.275	2.540	+3.220	+5.760
P10	Corredera posterior B / vidrio	1.675	2.540	+3.220	+5.760
H01	Porton / hoja	3.000	2.000	+0.085	+2.085
P11	Corredera bano/comedor	1.050	2.240	+3.260	+5.500

LECTURA DEL CUADRO

Dimensiones de hoja o vidrio; no equivalen al vano. P11: luz entre jambas0,90; hoja1,05 y carrera1,02; ver A09 / suplemento D09.

G: P05 vano1000, hoja908, marco923mm; garganta848mm y paso conservador806mm con manija a90°. P02 vano1000 / marco930mm.


G: DVH con dos paños de vidrio; espesor y separacion segun modelo. Prestaciones y composicion final por especificar.

P08/P09/P10: correderas vivienda; replantear rieles, solapes, desagues y retenedores a partir del vano real.

Porton: hoja 3,00 m; paso libre 2,75 m; carrera 3,05 m. Paso medido entre caras de pilares.

01 P05 / jambas y hoja cerrada G | 1:10

Hoja908 x45 G; apertura en A03

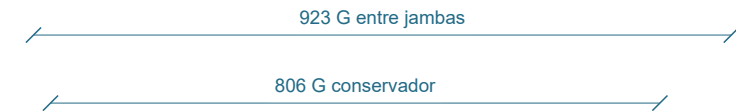

HERRERIA Y PROTECCION

F: baranda nominal 1,05 m sobre nivel de balcon. G: eje pasamanos lateral +4.30; NPT alto +3.25; diferencia 1.05 m. Medir altura util donde cambie el acabado.

G: postes, barrotes y zancas representados. Separacion de barrotes, resistencia horizontal, soldaduras, placas y anclajes requieren validacion de proyecto.

Escalera: 18 tablas de 1,00 m; avance entre tablas ~211,1 mm. A07 muestra el recorrido y el encuentro de acceso; A14 las piezas de soporte.


Pendiente: cuadro de fabricacion definitivo con materiales, espesores, tratamientos, sellos, drenajes, tolerancias y accesorios del fabricante.

02 Cierre vestidor-estar / corte G | 1:10



Sin puerta ni paso al estar


01/A13 Alero estudio / X=17,80 | 1:5

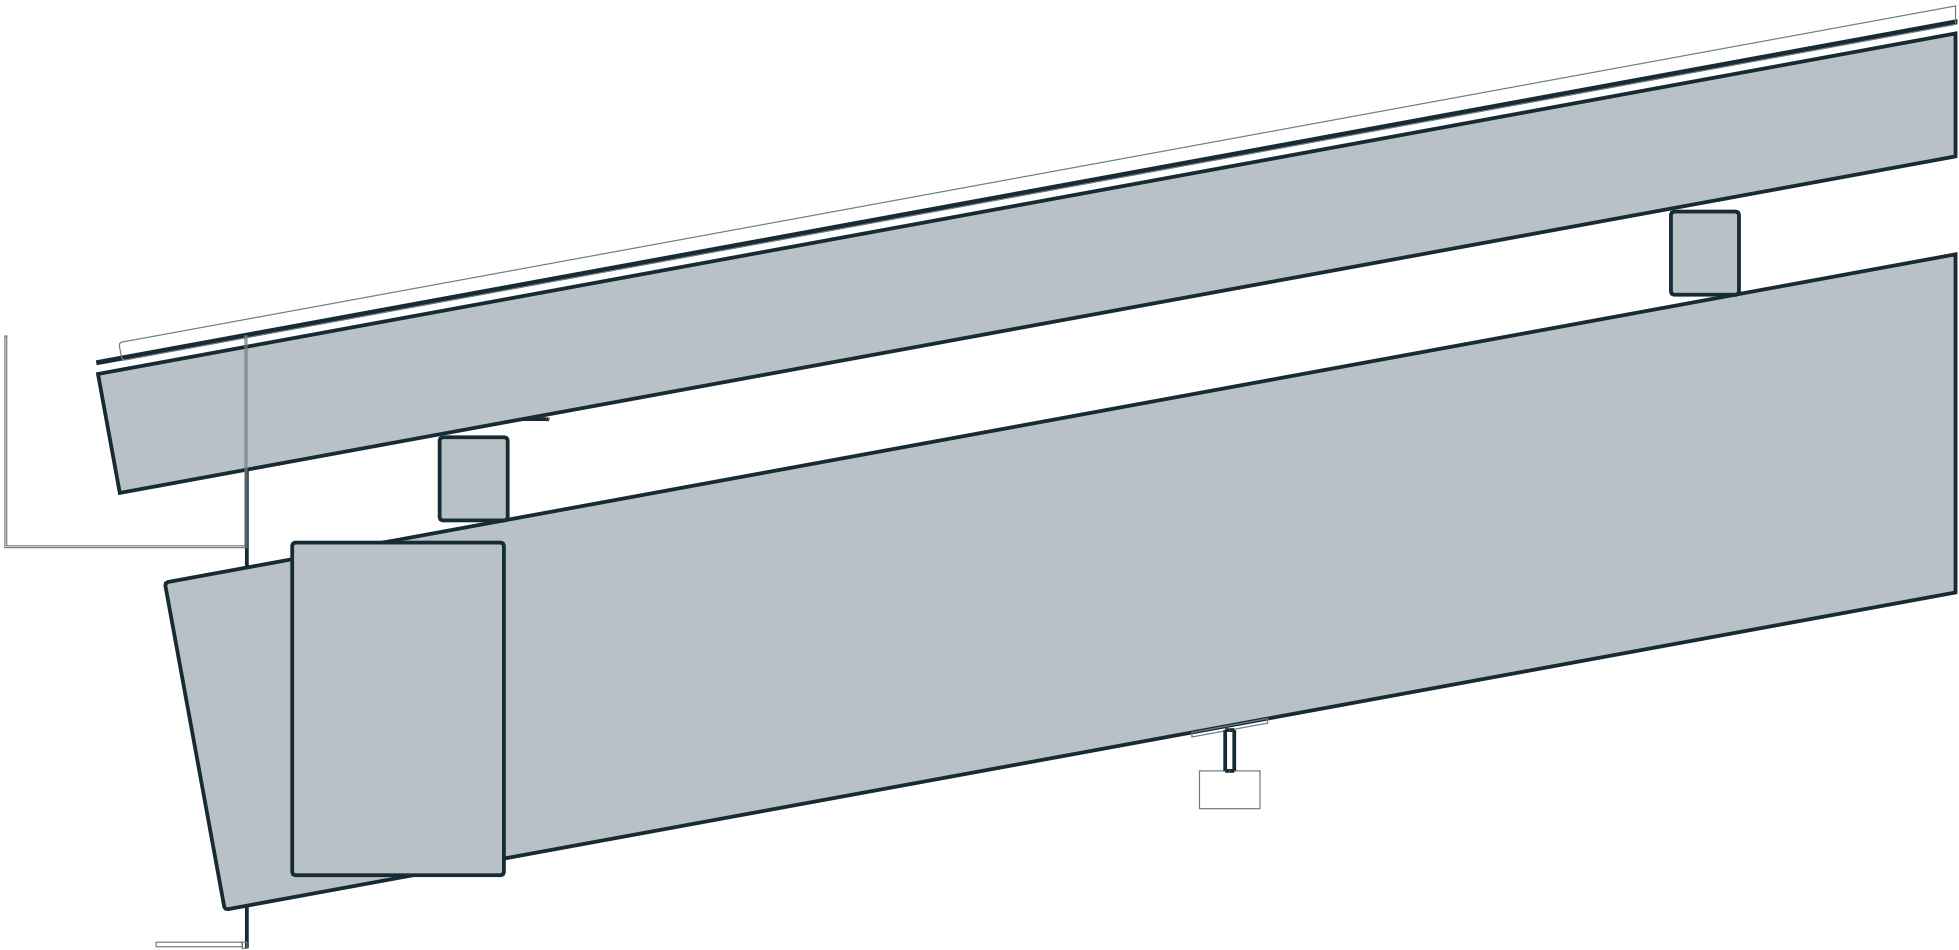

CAPAS Y GESTION DEL AGUA

- G: cubierta metalica, aislacion representada de 80 mm, revestimiento inferior y cabios/correas. La seccion corta las piezas de la malla a su escala real.
- G: chapa nominal0,8 mm. Suplemento D01 propone capas, goteron, solape150 y fijaciones selladas; compatibilidad y resistencia por verificar.
- P: babeta/contrababeta del salto, retorno de membrana y sellos alrededor de conductos desarrollados en suplemento D02; verificar frente a exposicion real.
- P: validar condensacion, viento, dilatacion y puentes termicos con datos climaticos y especificaciones definitivas.


02/A13 Escalon cubiertas / X=17,80 | 1:5

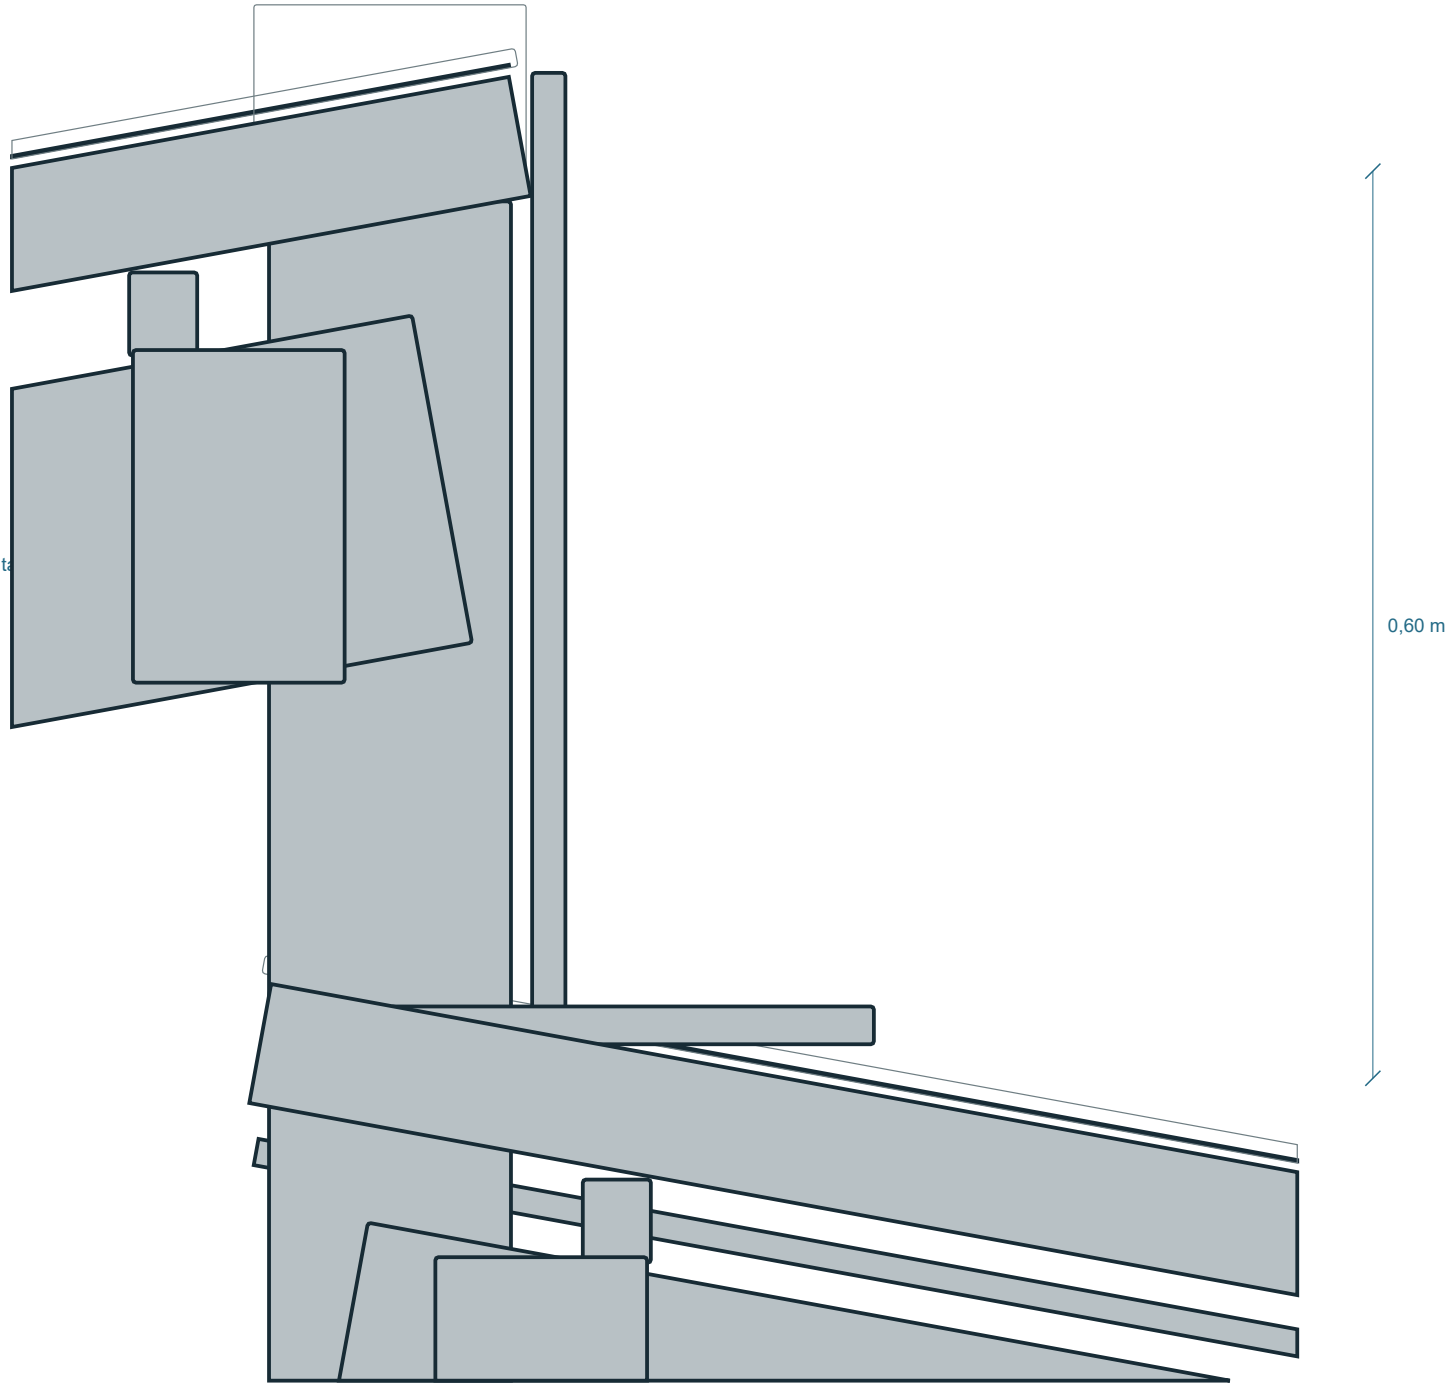

DVH, UMBRALES Y BALCON

- Encuentros generales: A07, A14 y A13b. Suplemento D01-D04 desarrolla capas, solapes, sellos y anclajes con cotas en mm.
- P: junta perimetral con respaldo y sello compatible; apoyo y calzos de vidrio, drenaje del marco, continuidad de aislacion e impermeabilizacion.
- El suplemento distingue las piezas G de las propuestas P; las especificaciones finales dependen del sistema y fabricante seleccionados.

05/A13b Canaleta abierta / X=14,00 | 1:2

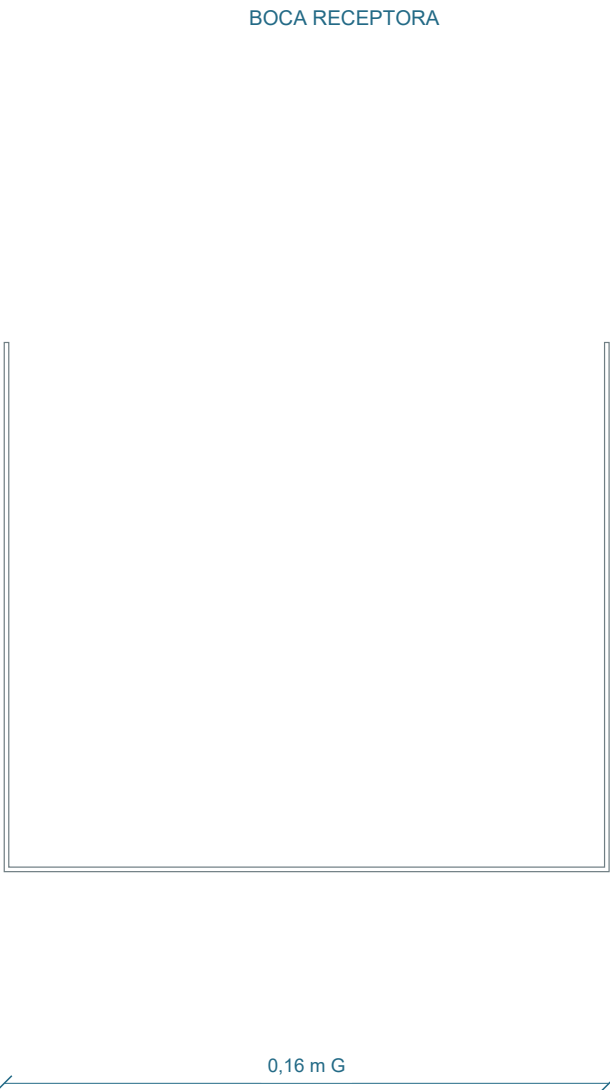


05/A13b CAPTACION / FIJACION

G: seccion de canaleta recortada directamente de la malla. Verificar apertura superior, fondo, salida lateral y continuidad en la prueba del modelo.

P: pendiente longitudinal, caudal, fijacion y sellos requieren dimensionado; el ancho grafico no certifica capacidad pluvial.

06/A13b DVH / antepecho / Z=3,00 | 1:5

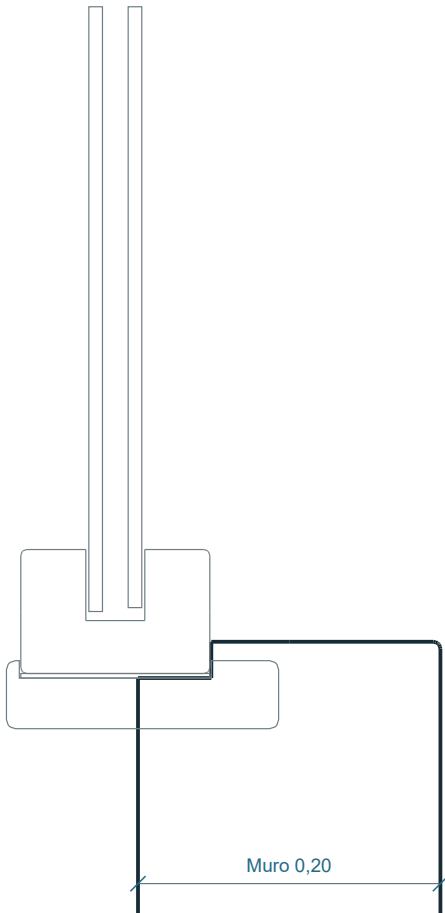


06/A13b ENCUENTRO DE VENTANA

G: dos paños, marco, antepecho y alféizar representados. La ampliacion permite revisar solapes y contacto.

P: apoyo, sellos, drenaje del marco y conexion de aislacion desarrollados a1:5 en suplemento D03.

Ver A12 para anchos, alturas y cotas de cada pieza.

07/A13b Paso de conductos / X=21,50 | 1:5

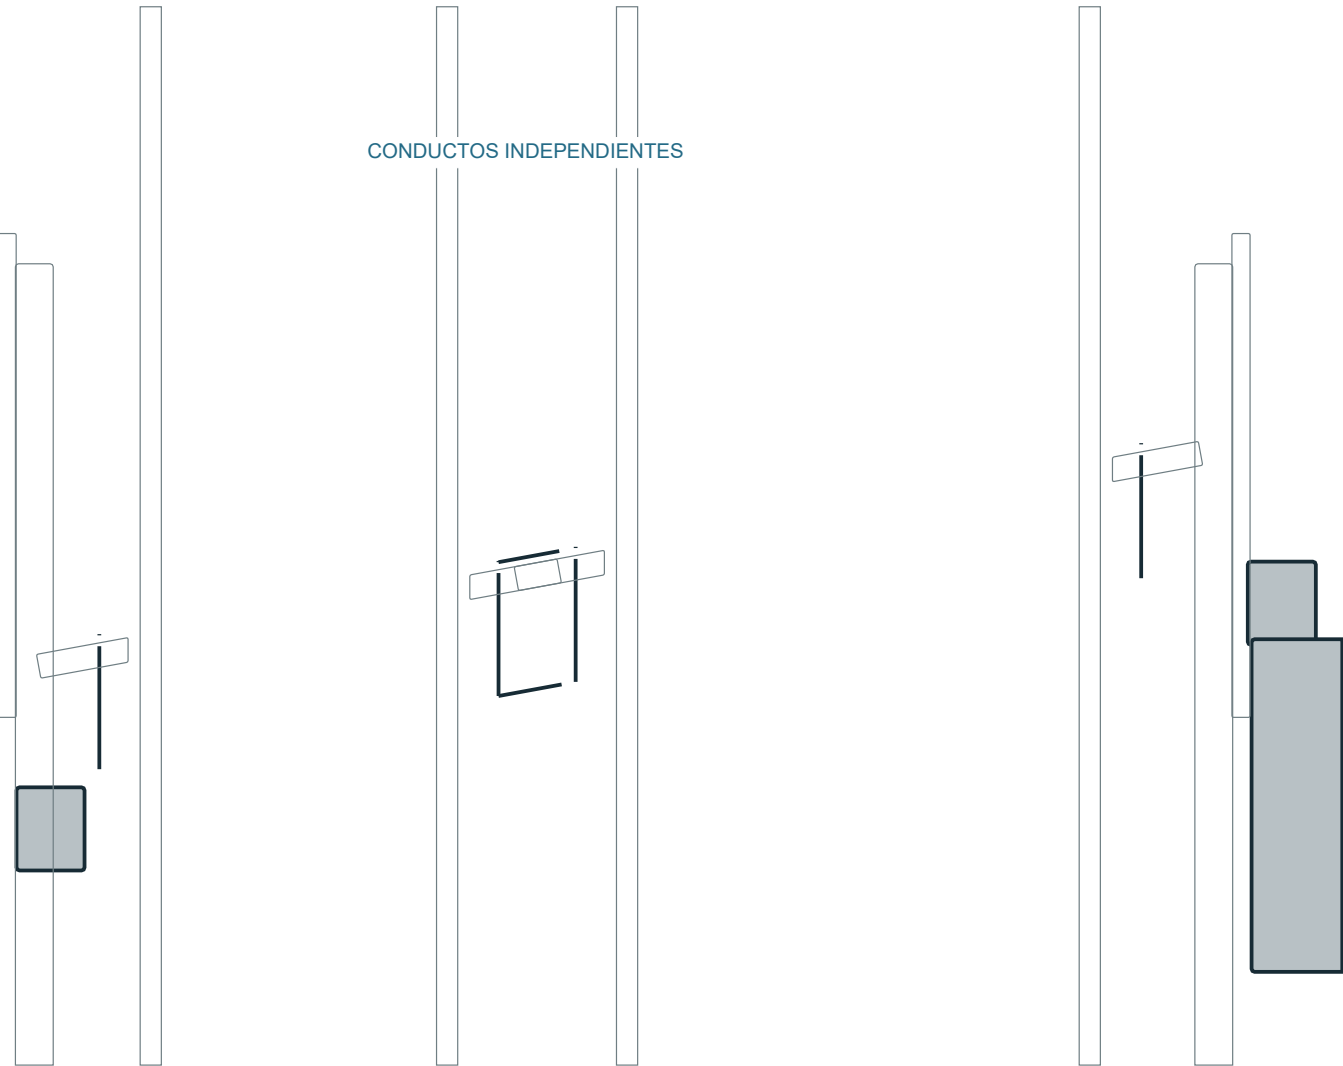


07/A13b PENETRACION / PATINILLO

G: conductos independientes, babetas perforadas y remate de patinillo. Se muestra la interseccion con cubierta.

P: continuidad de membrana, cuello y contrababetas, dilataciones, aislamiento termico y acceso de limpieza por especificar.

No se asignan distancias reglamentarias a combustibles ni caudales sin proyecto de combustion.


01 Planta de apoyos y líneas estructurales | 1:50

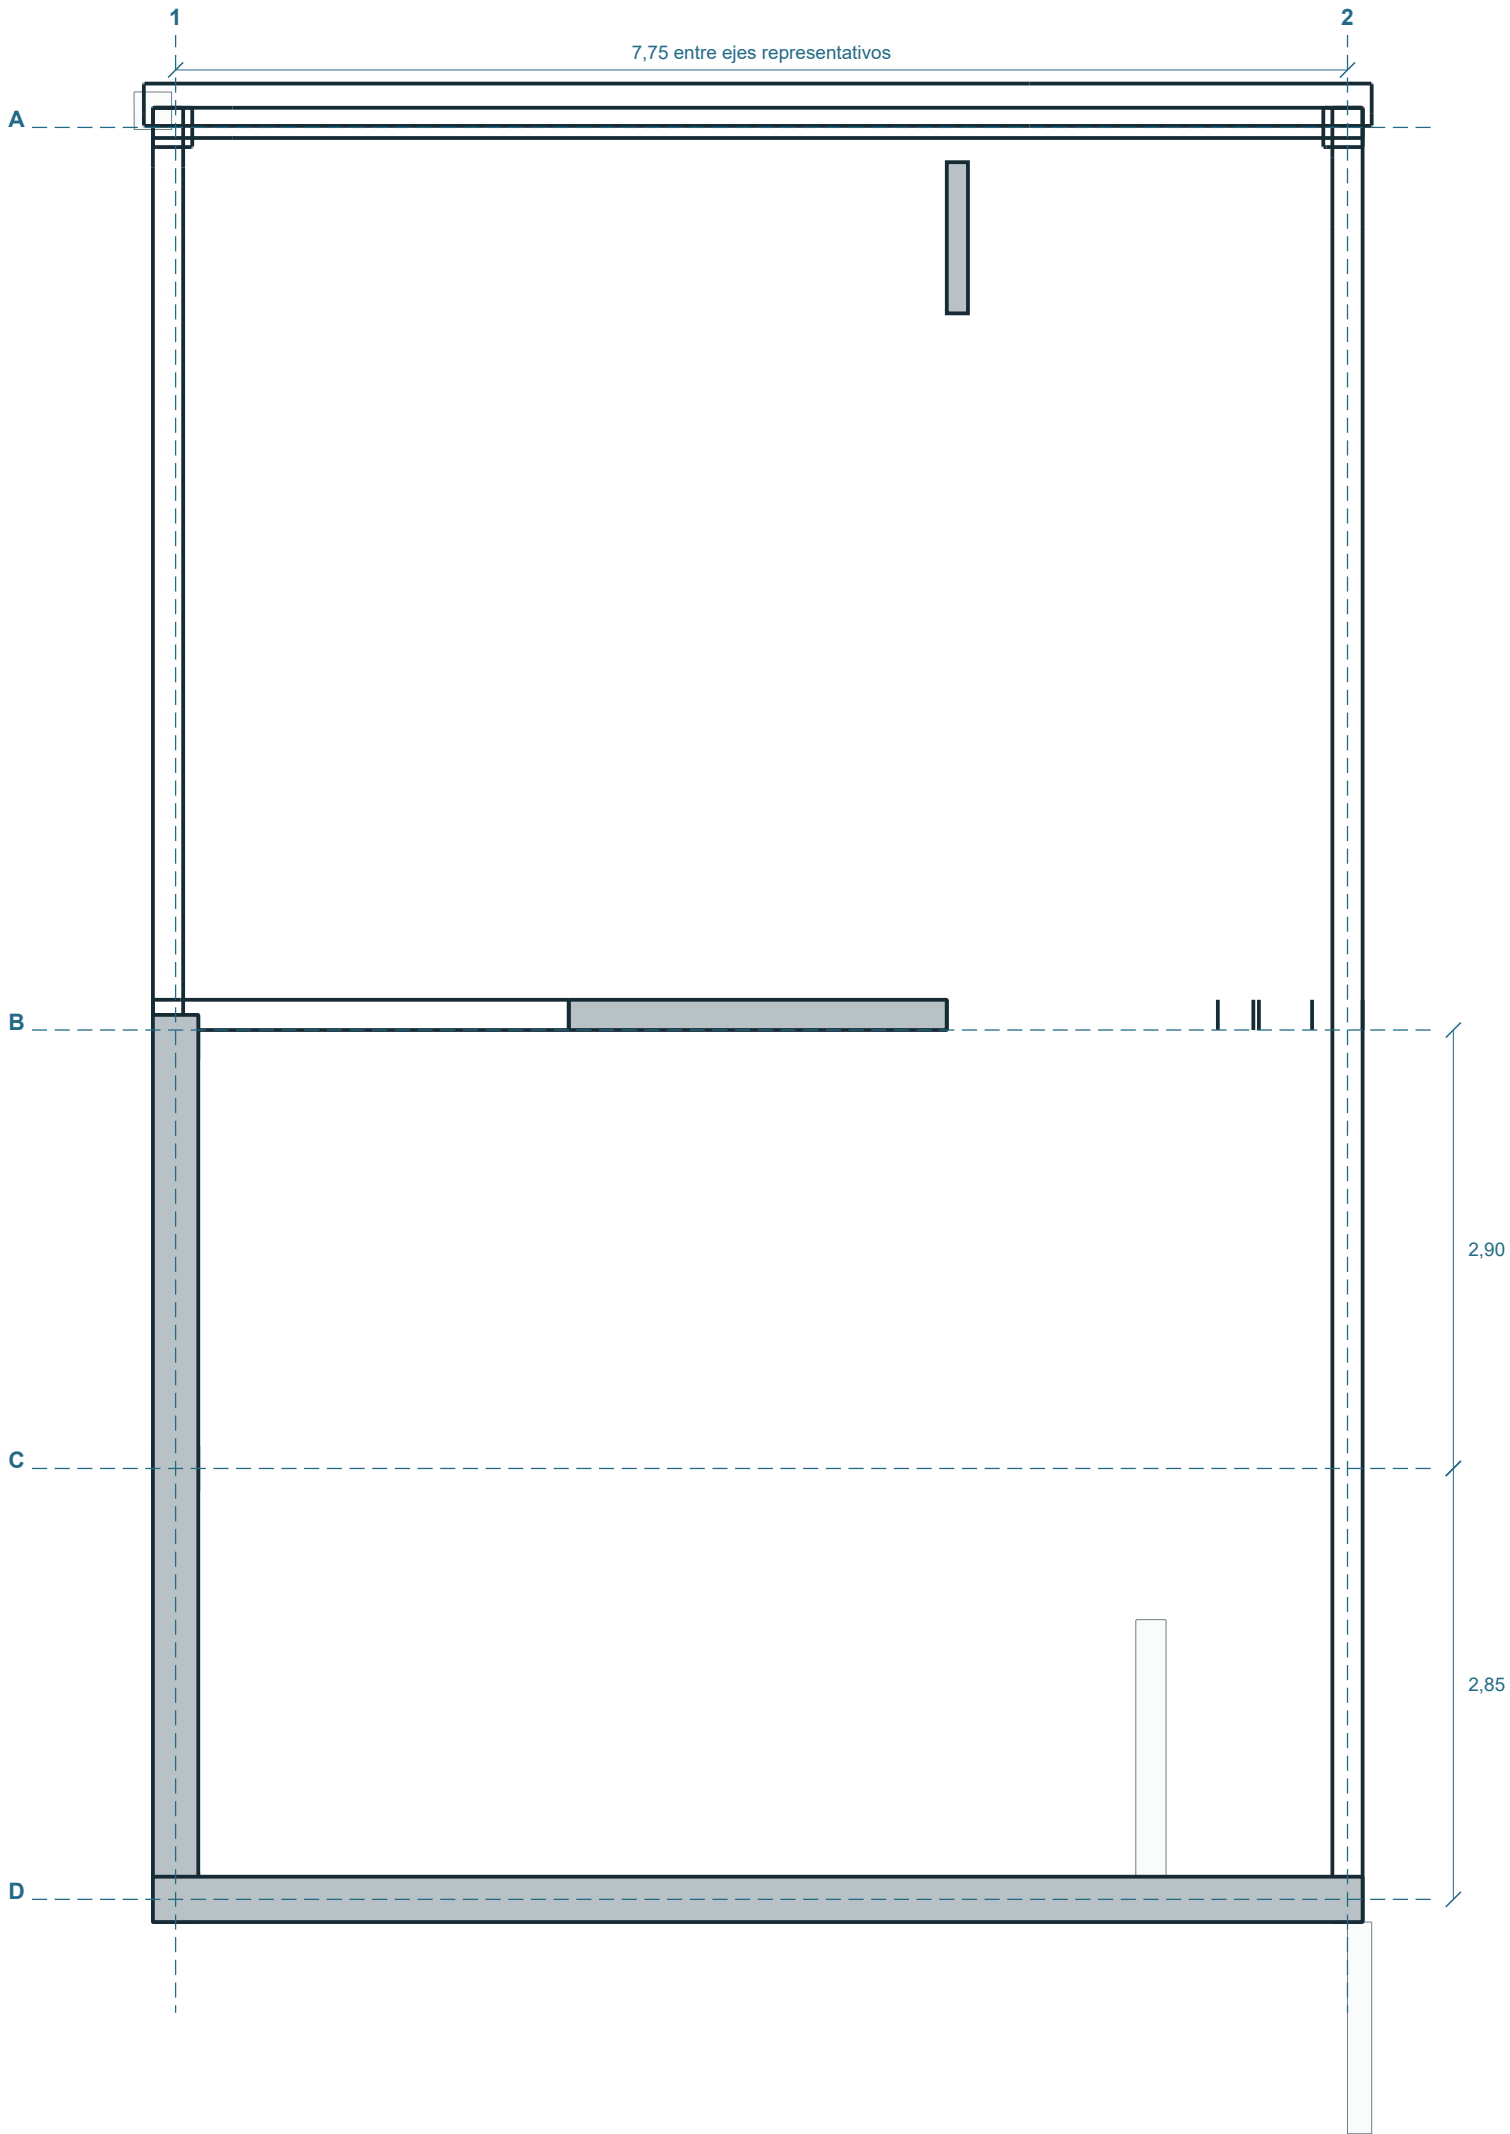

CAMINO DE CARGAS A VALIDAR

- Cubierta: chapa / aislacion -> correas -> cabios -> vigas de apoyo -> cerramientos / apoyos inferiores.
- Entrepiso: losa de 0,20 m -> muros y vigas / columnas representados -> fundacion por proyectar.
- Quincho: columnas 0,30 x 0,30 m y vigas de 0,30 x 0,36 m representadas. Son secciones de malla, no un dimensionado estructural.
- Balcones: proyeccion 1,00 m; verificar voladizo, continuidad y anclaje con la losa. No se infieren armaduras.
- Escalera: dos zancas; suplemento D05 dibuja cartelas, bulones y apoyo inferior P. Barandas: D04 muestra placas/anclajes G; capacidad pendiente.
- Fundaciones ausentes de la fuente: tipo, profundidad, armaduras y capacidad del terreno pendientes de estudio geotecnico y proyecto profesional.


04/A14 Balcon / baranda / Z=9,00 | 1:20

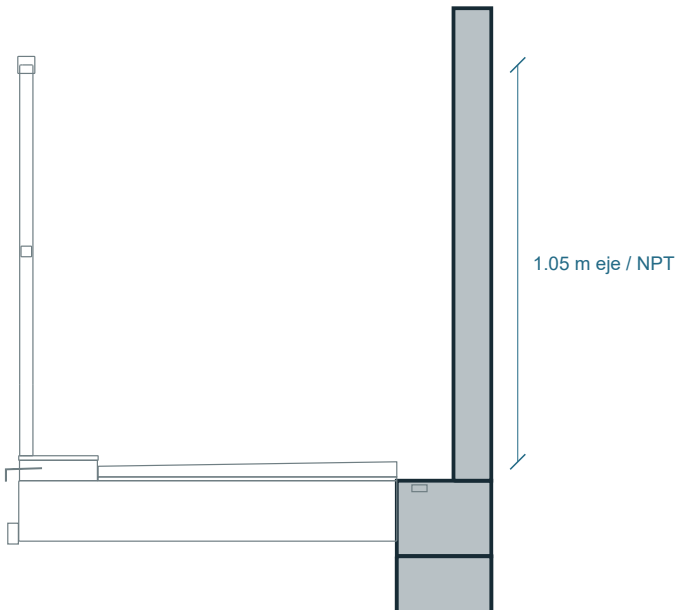

UNIONES

- El corte documenta las piezas presentes y sus apoyos aparentes.
- Los anclajes no se consideran resueltos por estar dibujados: validar sustrato, borde, profundidad y solicitudes.
- Acero/hormigon: especificar corrosion, drenajes y juntas.

01 Coordinacion general / PB | 1:100

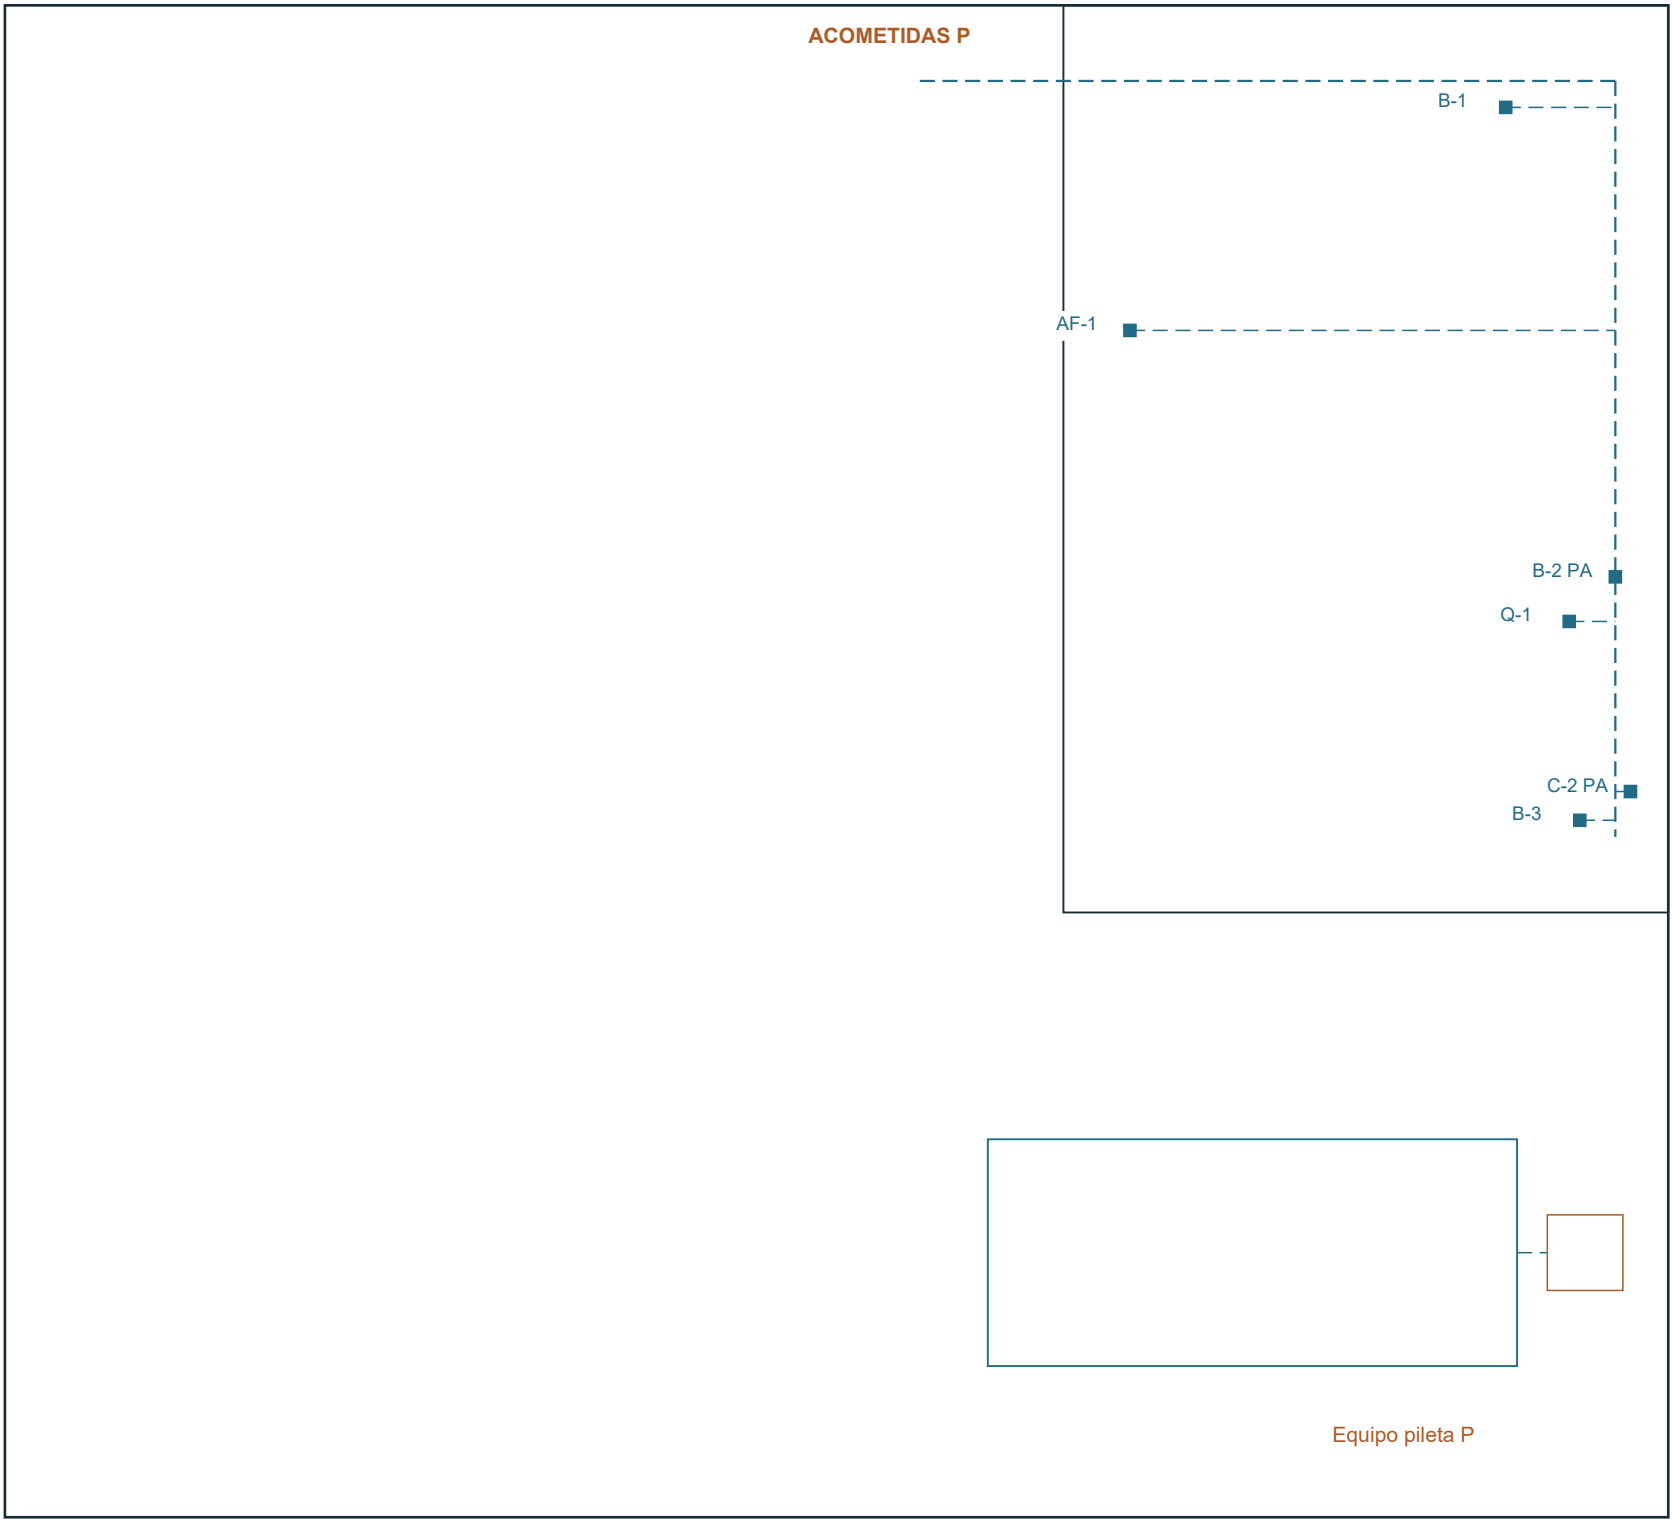

CRITERIO DE COORDINACION: localizar consumos y cruces antes de dimensionar redes. Sin cotas de servicio ni calculos no se presenta este esquema como instalacion completa o certificada.

AGUA / DESAGUE / PLUVIAL

AF-1 cocina mono; B-1 bano mono; Q-1 quincho; B-3 bano pileta; B-2 bano PA; C-2 cocina PA. Nodos sobre equipos reales del modelo.

Las líneas punteadas son relaciones funcionales, no tuberías ejecutivas. Recorridos, diámetros, pendientes, ventilaciones, registros y acometidas se definen con el proyecto sanitario.

Pluvial: captacion y bajadas en A04. Destino final de descarga propuesto; red y cota de conexión exactas pendientes.

Pileta P: skimmer / toma de fondo -> prefiltro / bomba -> filtro -> retornos. Prever válvulas, vaciado, renovación y medidas de seguridad; equipo y tuberías por calcular.

ELECTRICIDAD / ILUMINACION / EXTRACCION

Servicios de red disponibles segun propietario. Tablero y medidor propuestos junto al acceso; ubicacion final segun prestador.

P: separar circuitos de iluminacion, tomas generales, cocinas, pileta y estudio. Definir potencias, protecciones, puesta a tierra y equipotencialidad.

G: luminarias representadas no equivalen a calculo luminotecnico ni conexion electrica.

G: conductos de horno, parrilla y cocina presentes. Ver A10: caudal, limpieza, aislamiento y reposicion de aire pendientes.

P modelado: D08 representa impulsión y extracción independientes con soportes a cabios, registro, filtros y terminales separados2,52m. Caudales, productos y prestaciones pendientes.

Area / pieza	m2	Metodo / alcance
Lote nominal F	440.00	22,00 x 20,00; limites nominales
Huella casa F	96.00	8,00 x 12,00; incluye quincho
Dos niveles nominales F	192.00	192 m2 brutos geometricos; no computo legal
Vaso pileta F	21.00	7,00 x 3,00 nominal
Borde pavimentado F	24.00	Anillo de 1,00 m nominal
Piso estudio G	41.74	Proyeccion real de la pieza; puede solapar otras
Piso vivienda G	36.13	Proyeccion real de la pieza; puede solapar otras
Piso monoambiente G	38.86	Proyeccion real de la pieza; puede solapar otras
Piso baño mono G	2.42	Proyeccion real de la pieza; puede solapar otras
Piso baño vivienda G	5.61	Proyeccion real de la pieza; puede solapar otras
Piso quincho G	45.42	Proyeccion real de la pieza; puede solapar otras
Piso baño quincho G	1.81	Proyeccion real de la pieza; puede solapar otras
Balcón lateral G	6.00	Proyeccion real de la pieza; puede solapar otras
Balcón posterior G	8.98	Proyeccion real de la pieza; puede solapar otras
Descanso escalera G	1.00	Proyeccion real de la pieza; puede solapar otras

FUENTES Y REVISION

F: source/scene.json, configuracion y geometria original. Coordenadas fuente X / Z horizontal; Y altura. Blender X / -Z / Y.

F: docs/DECISIONES.md: estudio 3,20 m libres, vivienda 2,60 m y video pausado.

G: modelo Casa_de_Campo_99_R8.blend; SHA256 60810e1945f53b339c070c6e...

G: extraccion de mallas evaluadas a cuadro 150, con puertas en su pose de documentacion. Los detalles omiten microgeometria menor para permitir lectura.

P: desarrollos constructivos y sistemas inferidos se identifican en sus hojas. No se presentan como verificacion profesional.

Las superficies de piezas no son utiles netas de recintos. Comprobar uniones y areas comunes antes de sumar; los pisos PB de banos se recortaron de las superficies generales.

PENDIENTES PARA EMISION FINAL


Mensura y topografia; servicios y cotas exactas; suelos; calculo de estructura, instalaciones, seguridad, clima y acustica.

Cierre de observaciones de la auditoria y coherencia con modelo / visor congelados. Umbral critico 9,9 e hiperrealismo siguen siendo condiciones de entrega.

ARCHIVOS: un PDF multipagina vectorial A2; un SVG y un DXF por lamina; geometria.json de extraccion; manifest.json de versiones; verification.json de controles. Los DXF contienen las vistas metricas separadas y cotas; la cartela completa se conserva en PDF/SVG.

Todas las cotas en mm salvo niveles en m

02 Solape de babetas / fijacion P | 1:5

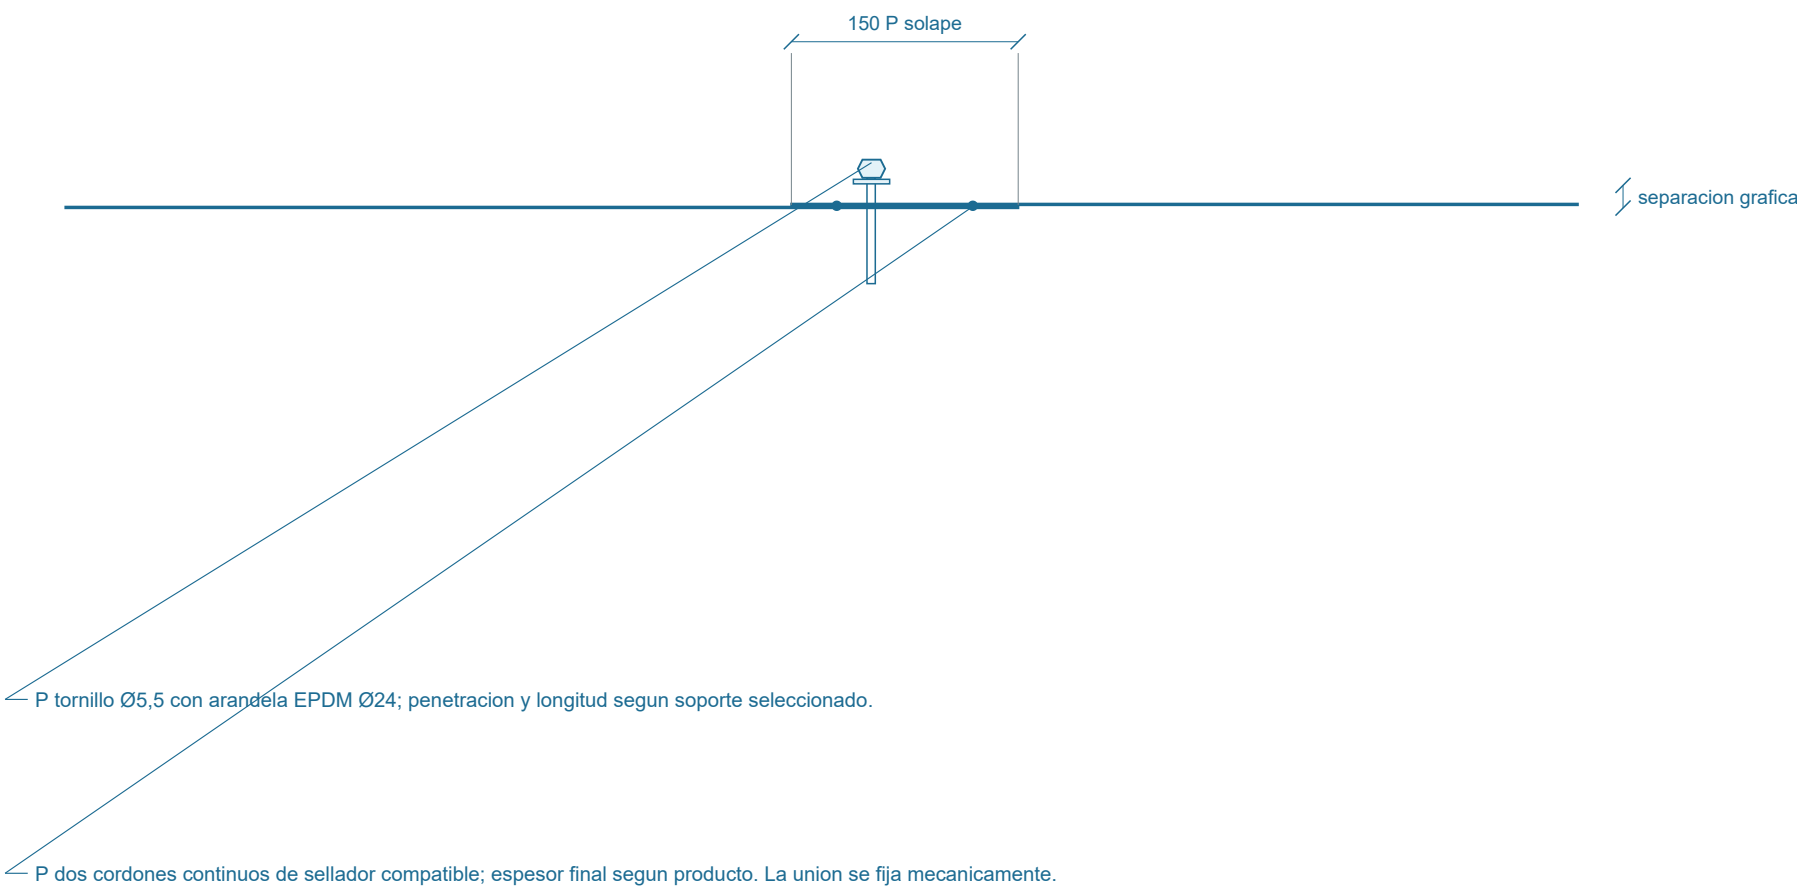

DECISION DIMENSIONAL P


Solape150 de remates; retorno20 de borse; sello neutro compatible; fijacion inicial cada300 en remate. No se traslada como tabla de fijacion de la chapa a correas

El detalle muestra orden de capas y salida del agua. Los espesores submilimetricos se dibujan con peso de linea legible, sin escalarlos como material mas grueso.

R1 | Lysaght: Roofing & Walling Installation Manual, §§7.9 y1


G = medido / gris P = propuesta dimensional / azul Todas las cotas en mm salvo niveles en m

03 Encuentro escalonado / seccion P | 1:5

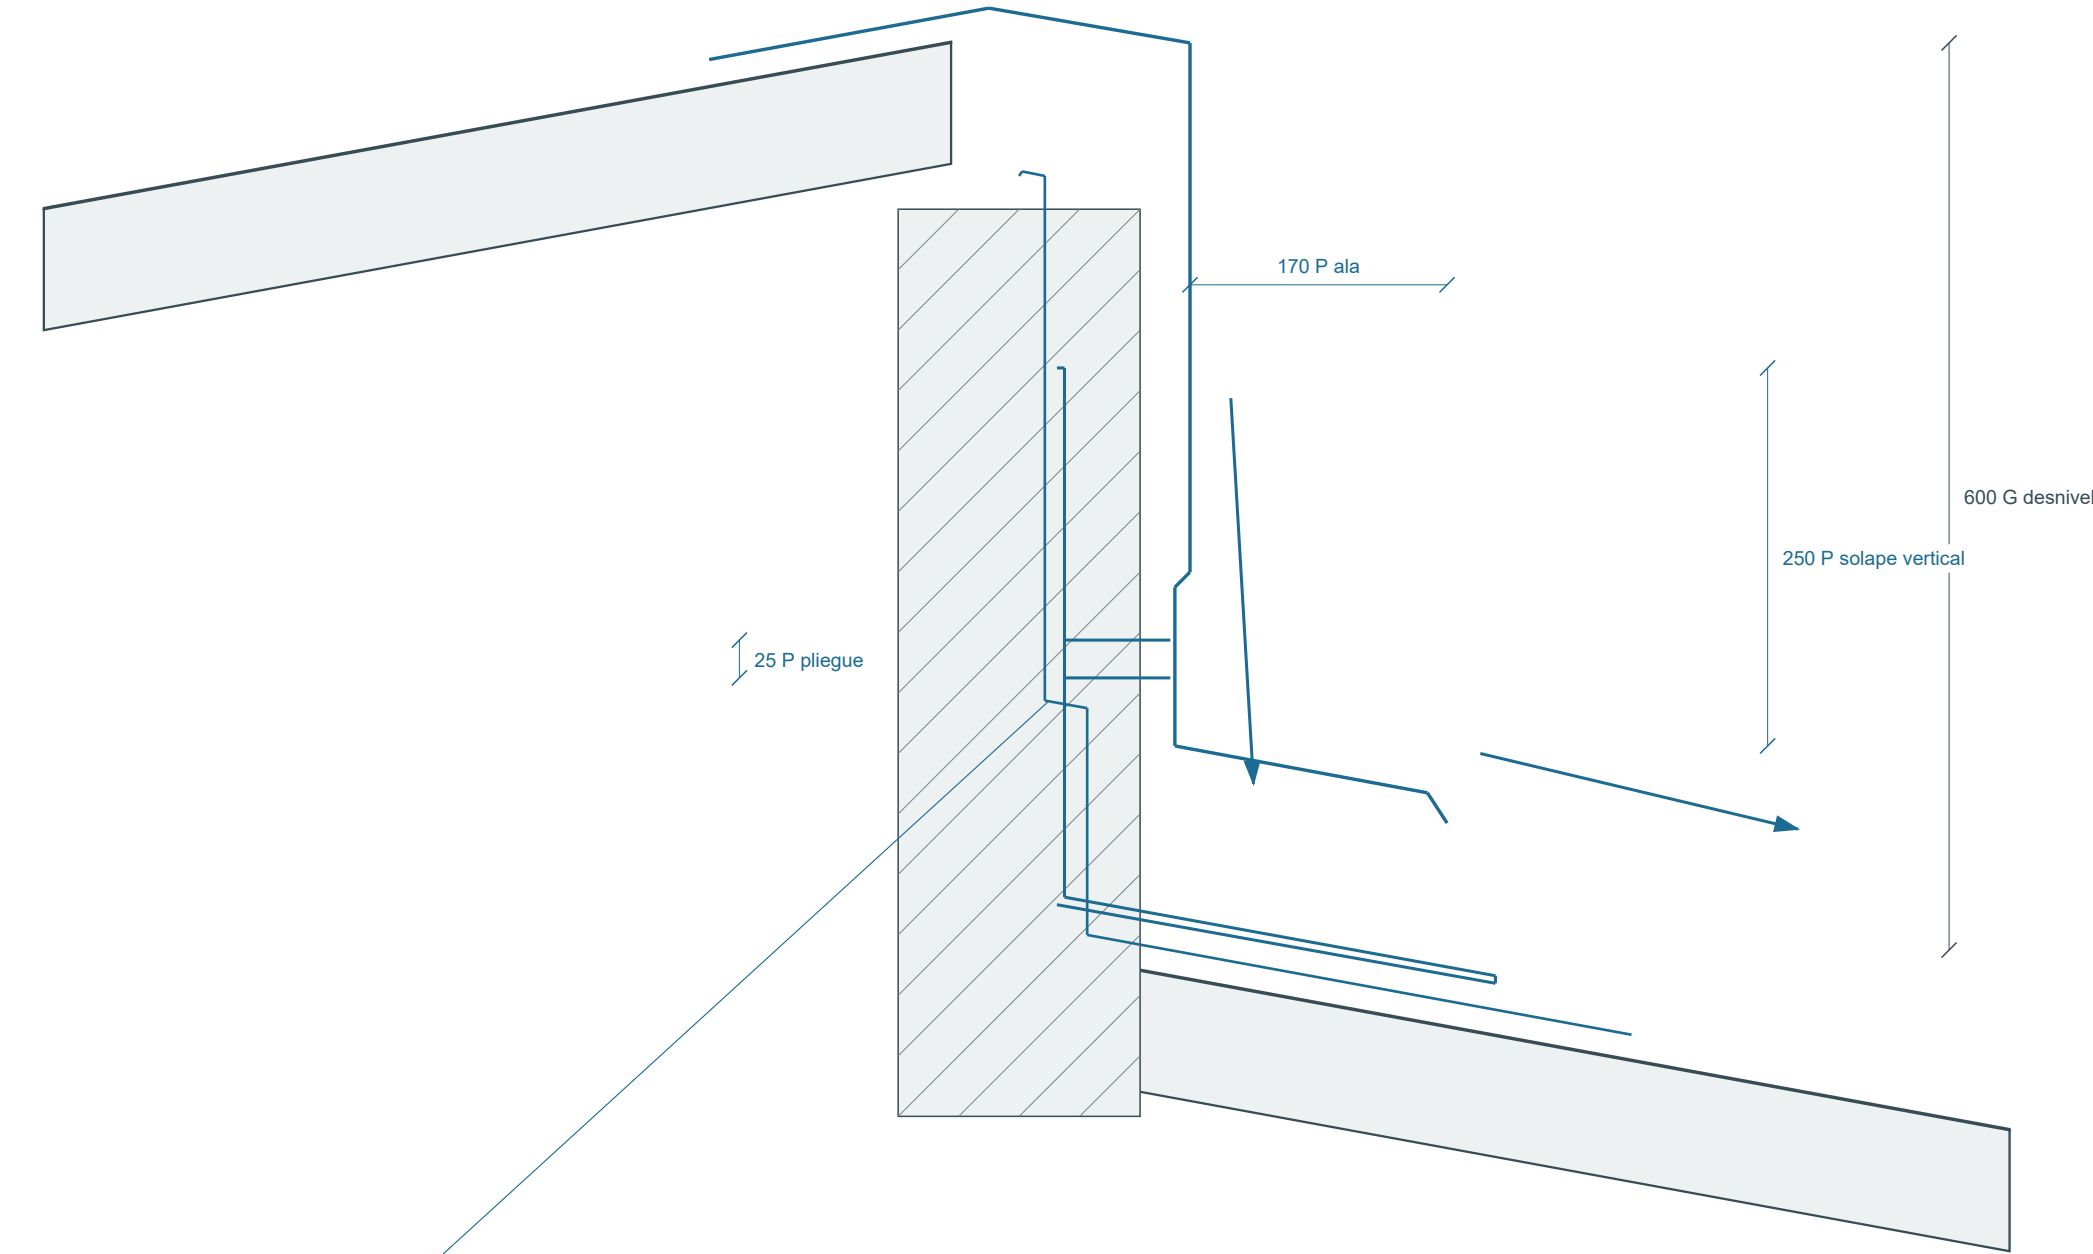

P membrana continua con pliegue flexible25; retorno vertical180 sobre faldon inferior. No puente rígido entre paños que impida dilatacion.

04 Paso de conducto / remate P | 1:5

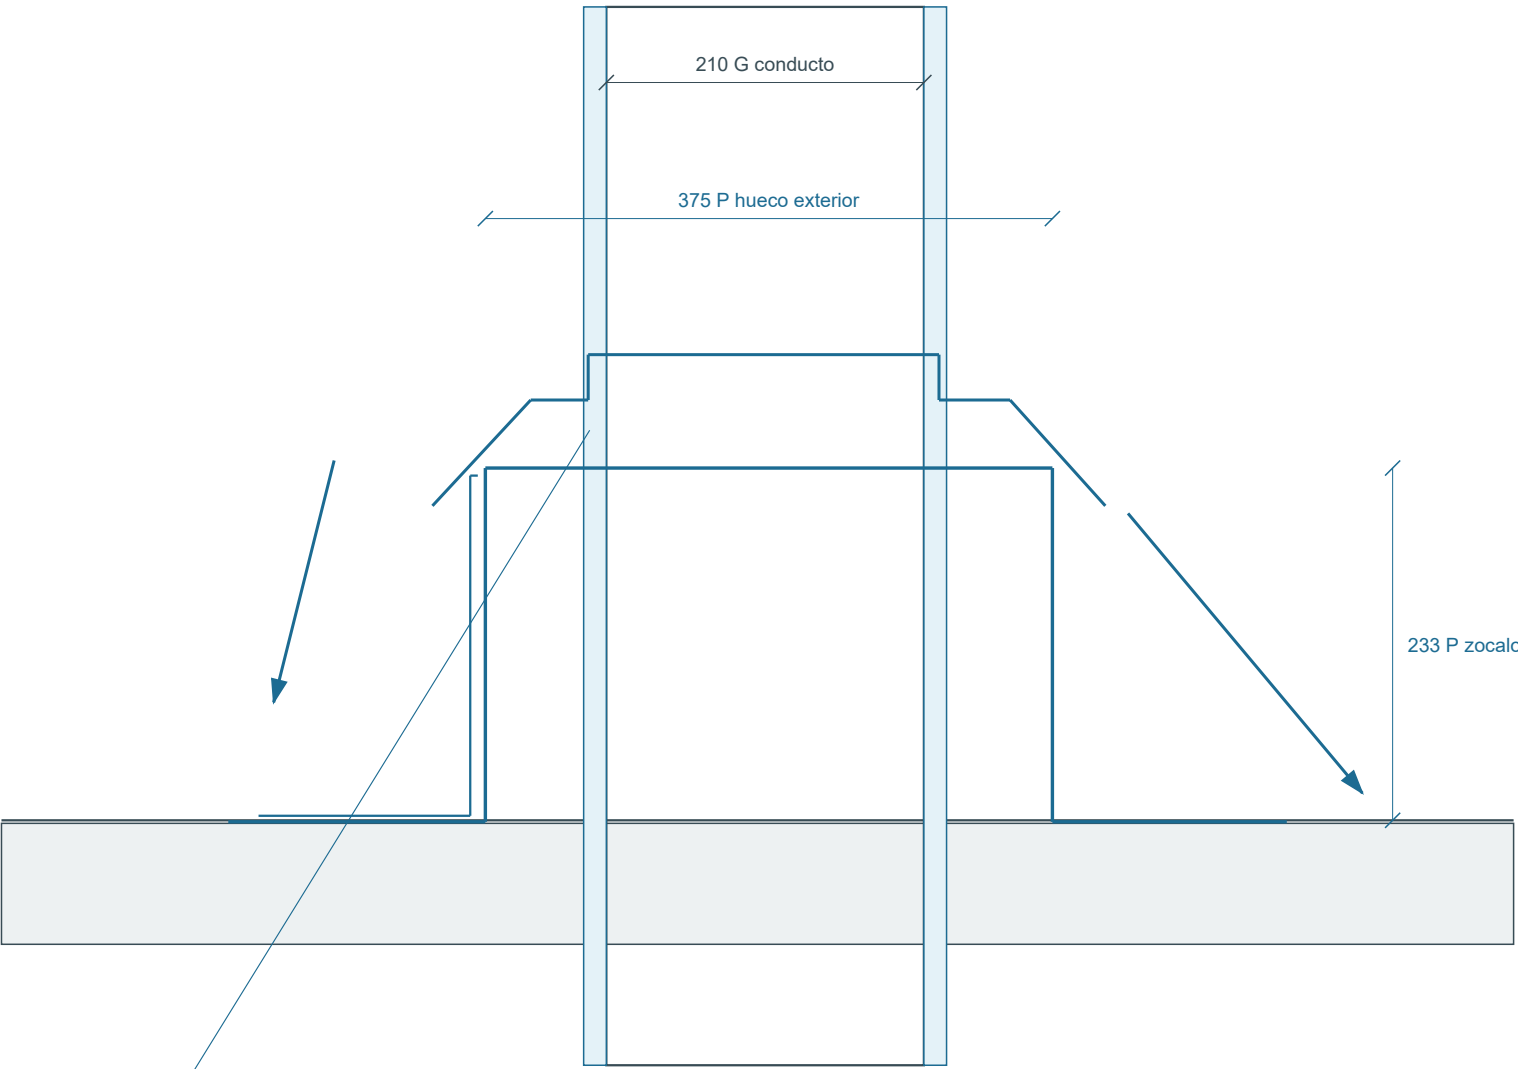

P collar partido desmontable, abrazadera y junta compatible con temperatura. Conducto aislado no queda rigidamente pegado a la babeta.


SERVICIO Y AGUA

P bandeja superior con desvio lateral; retorno200 contra cuello, solape150 en falda y goteron20. No obstruir canales del perfil.
P acceso desmontable de300 x300 al registro del patinillo. Aislamiento y distancias a combustibles requieren seleccion del sistema de combustion.

R1 | Lysaght: Roofing & Walling Installation Manual, §§7.9 y11

G = medido / gris P = propuesta dimensional / azul Todas las cotas en mm salvo niveles en m

05 Antepecho / corte real G | 1:2

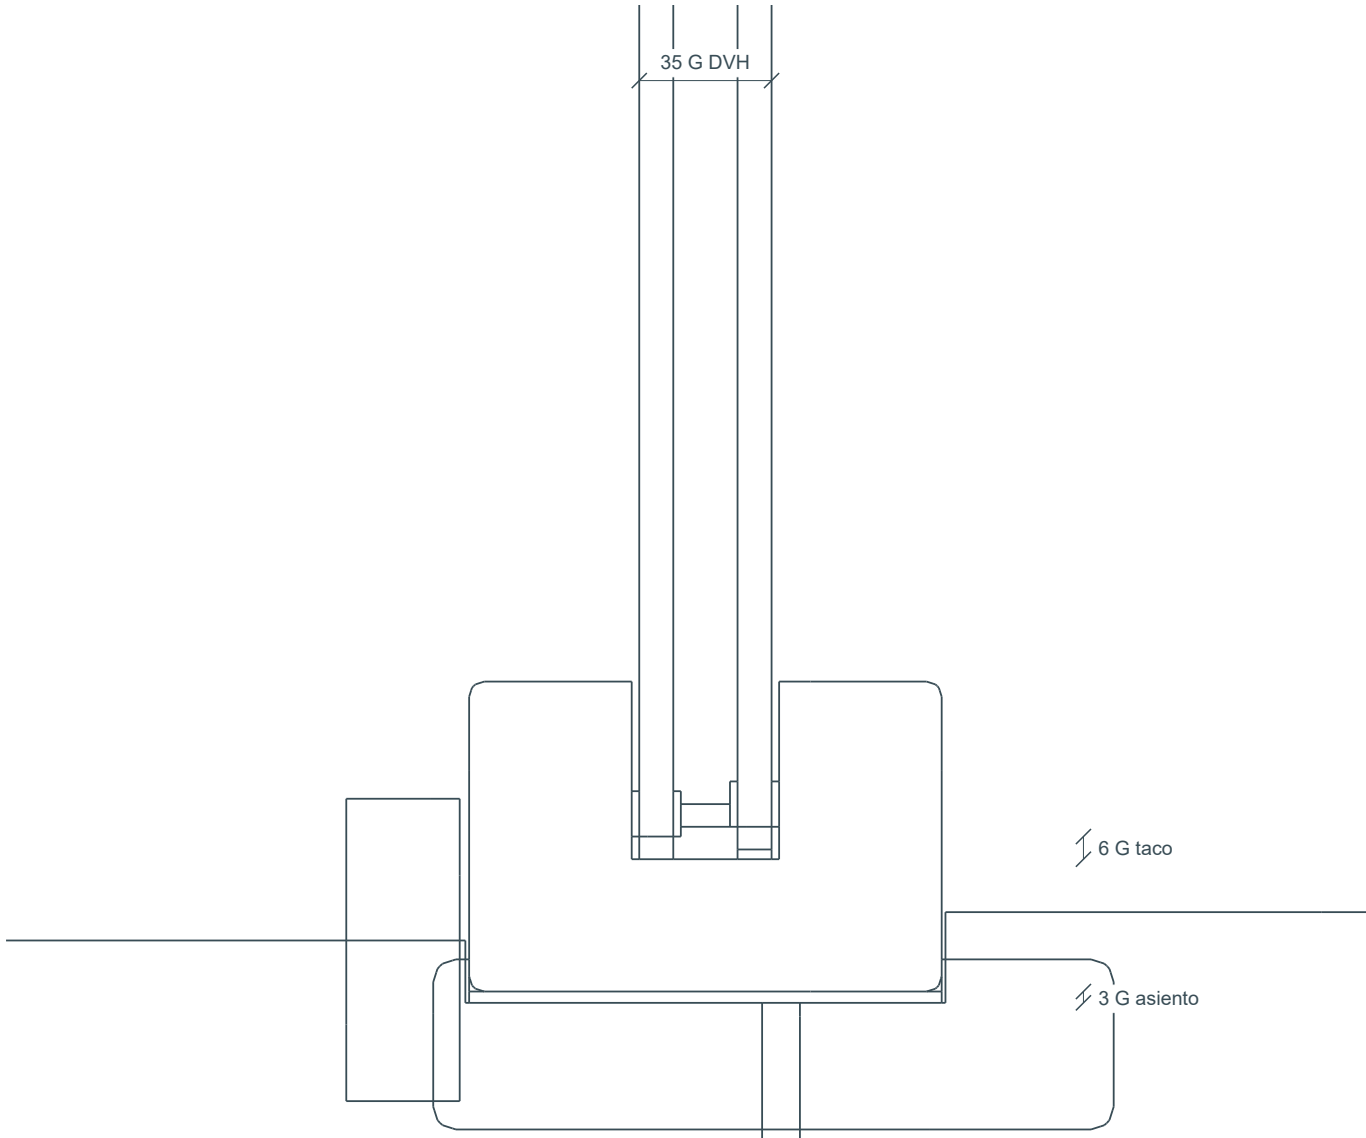


G galce comun39: paquete35 y2mm por cara exterior. Juntas elastomericas2mm a cada cara de los vidrios; toma12mm. El sellador de borde une ambas caras internas sin atravesar los vidrios.

G tacos100x6 por vidrio a1/4 y3/4 de luz; calzo conformado bajo el vidrio interior. Bajo el marco: apoyo continuo3 y juntas1 en rebaje local. Envolvente original conservada; sin carga sobre sello de camara.


G se retiraron los24 burlletes metalicos macizos incompatibles. Las juntas nuevas son geometria P incorporada; no certifican hermeticidad, capacidad, termica ni acustica. D10 amplía las correderas de balcon.

R2 | Vitro TD-140: Large Insulating Glass Units, p.4

06 Jamba / corte real G | 1:2

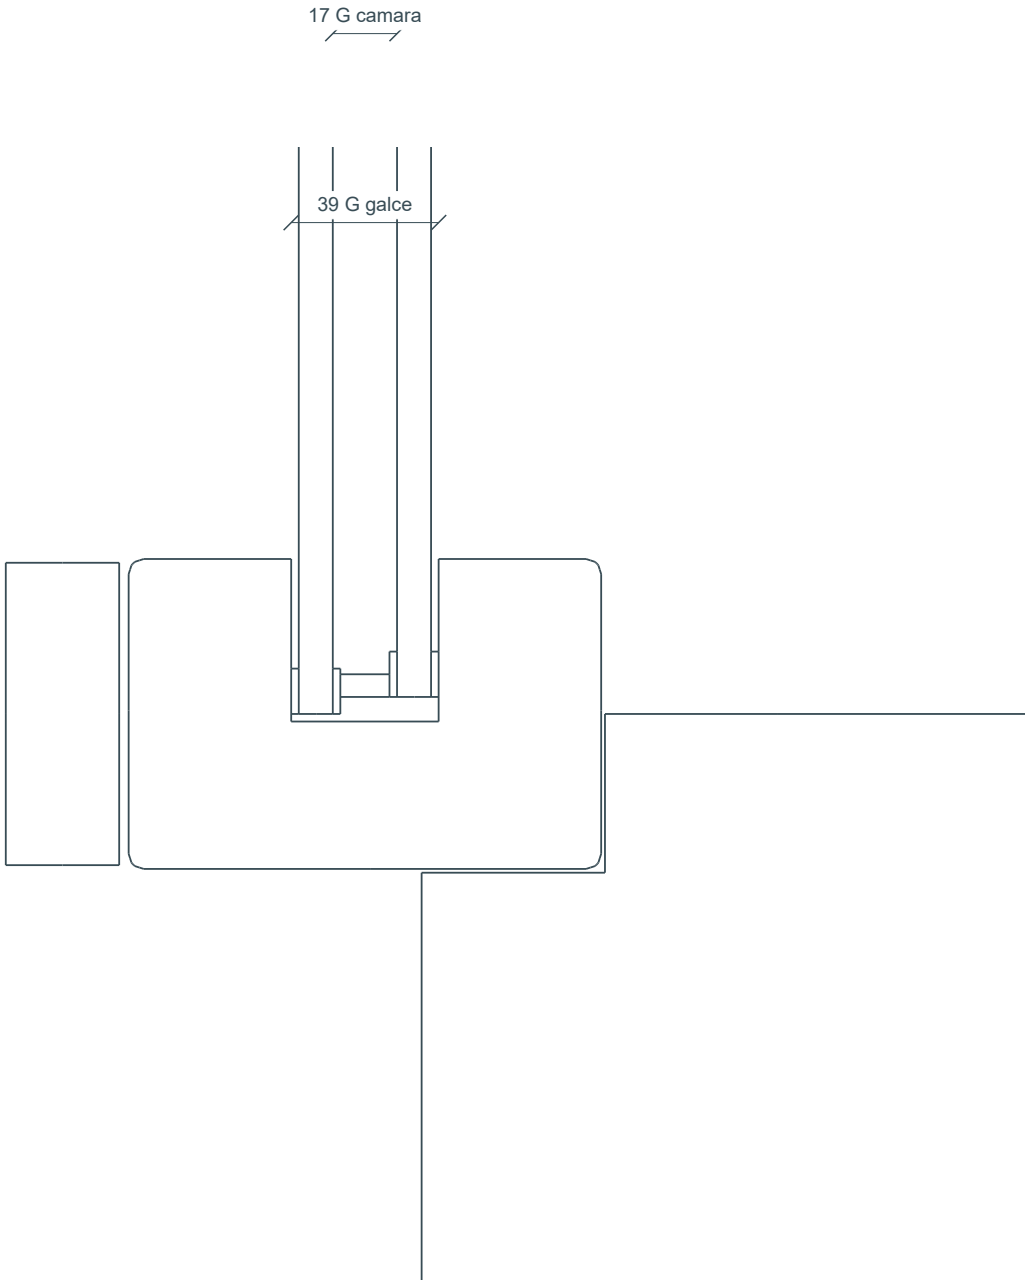


P Conexion del marco al soporte | 1:5

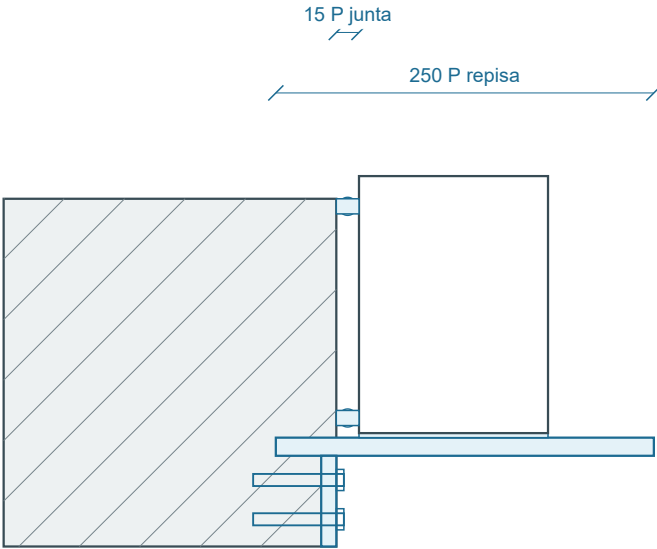

P apoyo continuo12 sobre escuadra10, fijacionesØ8 por dimensionar. Junta15 con respaldo y sellos; drenaje a exterior y compatibilidad del sistema pendientes de proyecto.

G = medido / grisP = propuesta dimensional / azulTodas las cotas en mm salvo niveles en m


07 Planta G / placa lateral regular | 1:5

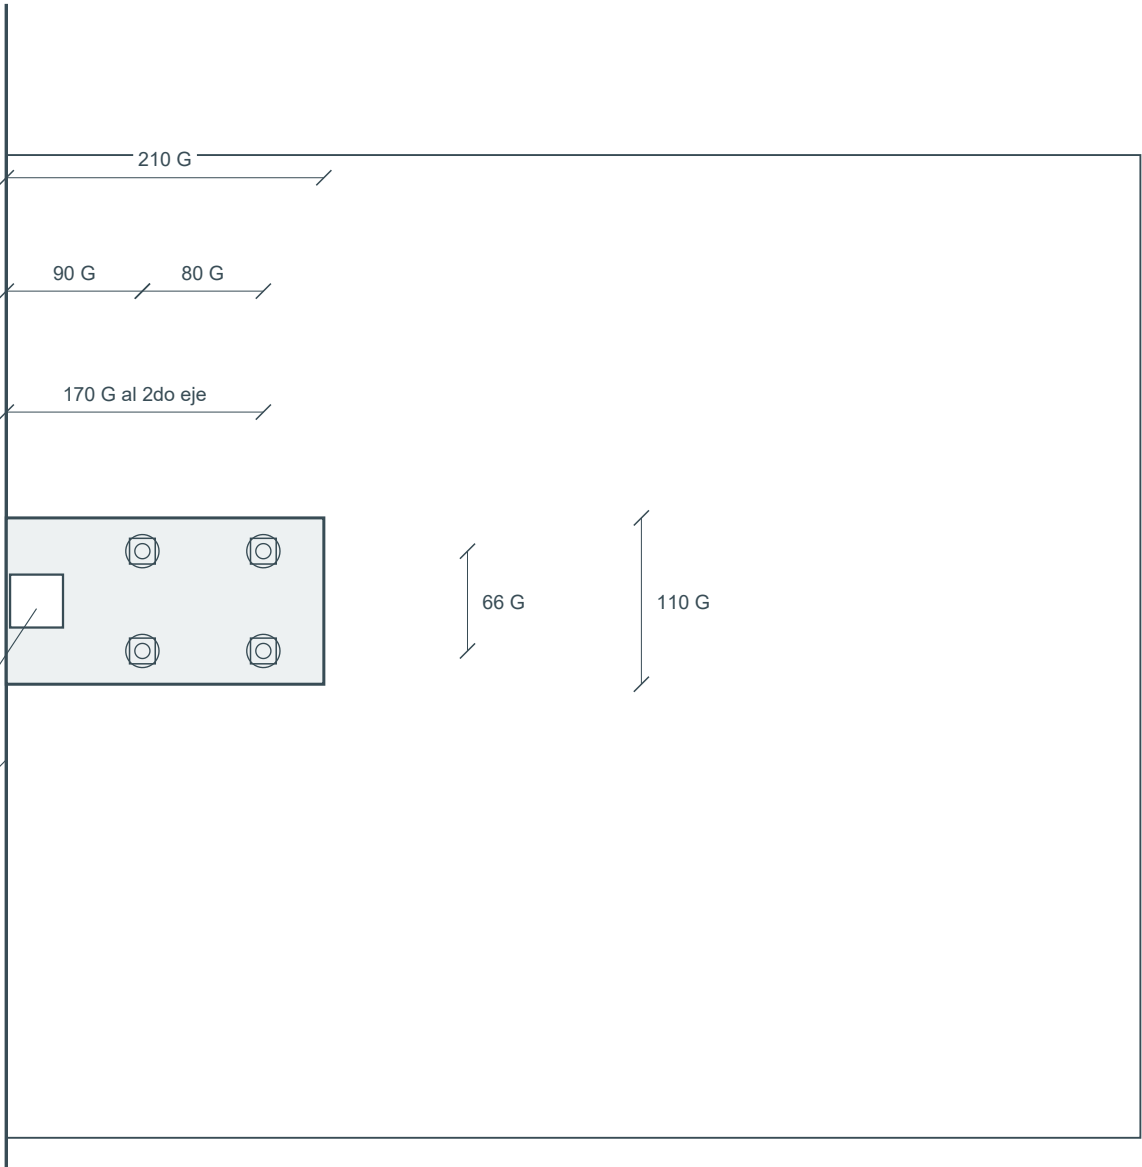

G canto de losa X=13,00. Ejes interiores a90 y170 mm. Reticula80 x66; cuatro vastagos continuos Ø10 por placa.

G poste35 x35, centro a20 del canto. La placa210 x110 x12 desarrolla el apoyo hacia el interior.

08 Corte G / sustrato y anclaje continuo | 1:5

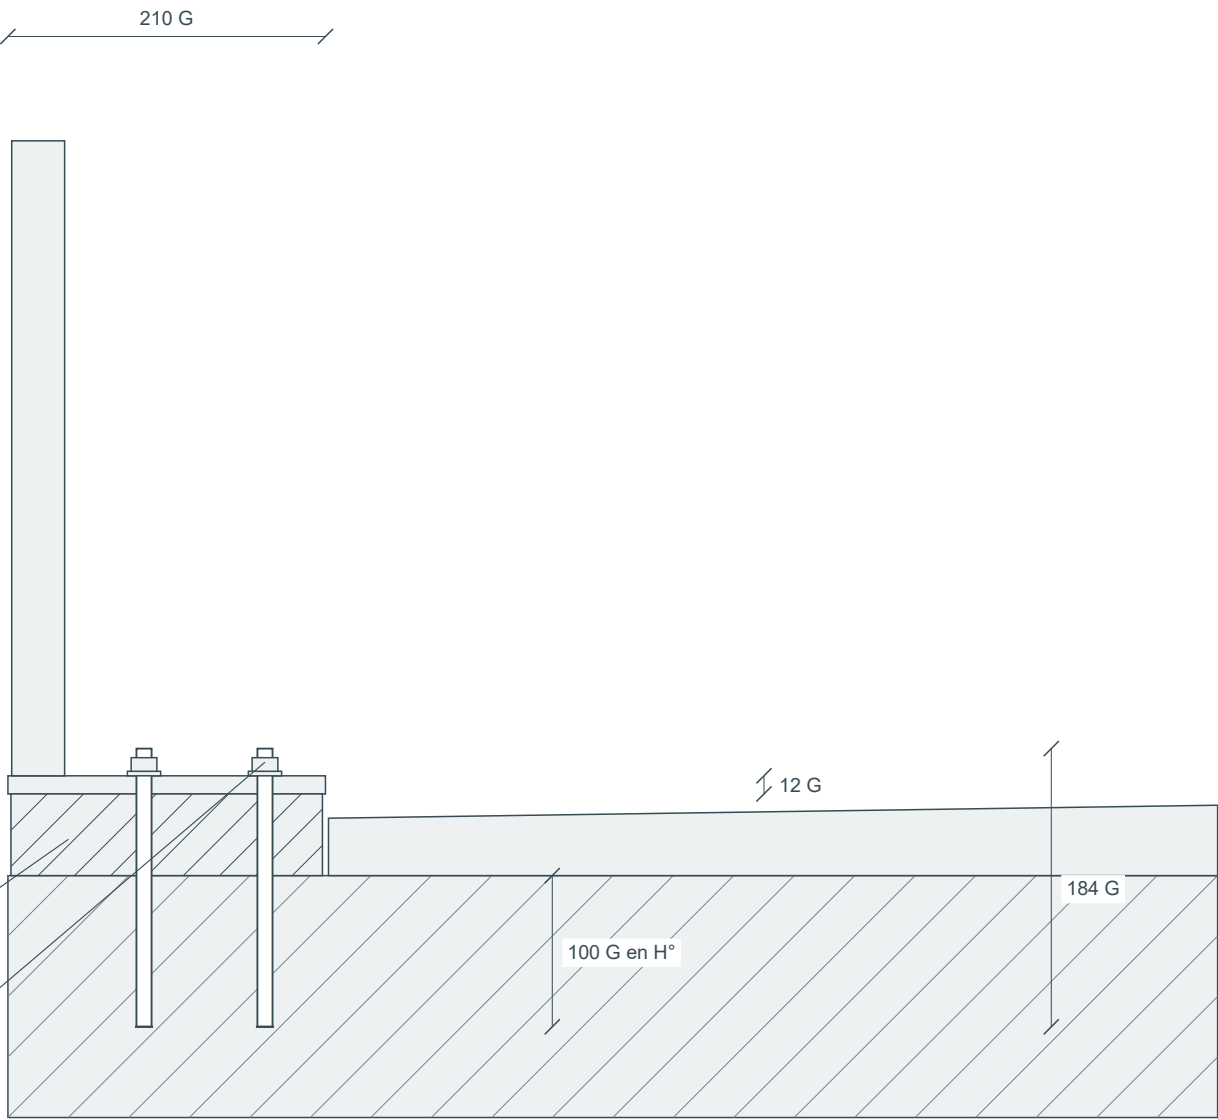

G cajeadado y grout conformado al H° real:54 sobre+3,20;44 sobre+3,21. En junta se adapta al escalon. Placa inferior+3,254.

G arandelaØ22 x3, tuerca17 x17 x9 y vástagoØ10 hasta+3,284. Extremo inferior+3,10/+3,11:100 mm dentro de H°.


CASOS Y ALCANCE RESISTENTE

G17 postes unicos. Esquinas:210 x210; primera placa envolvente210 x232 por prolongacion al descanso. Capacidad de placa, soldadura, anclajes, borde y hormigon pendiente por cargas/armado [R5].


R5 | Hilti: Base plates - design considerations

G = medido / gris P = propuesta dimensional / azul Todas las cotas en mm salvo niveles en m

09 Union superior G / envoltentes reales | 1:5

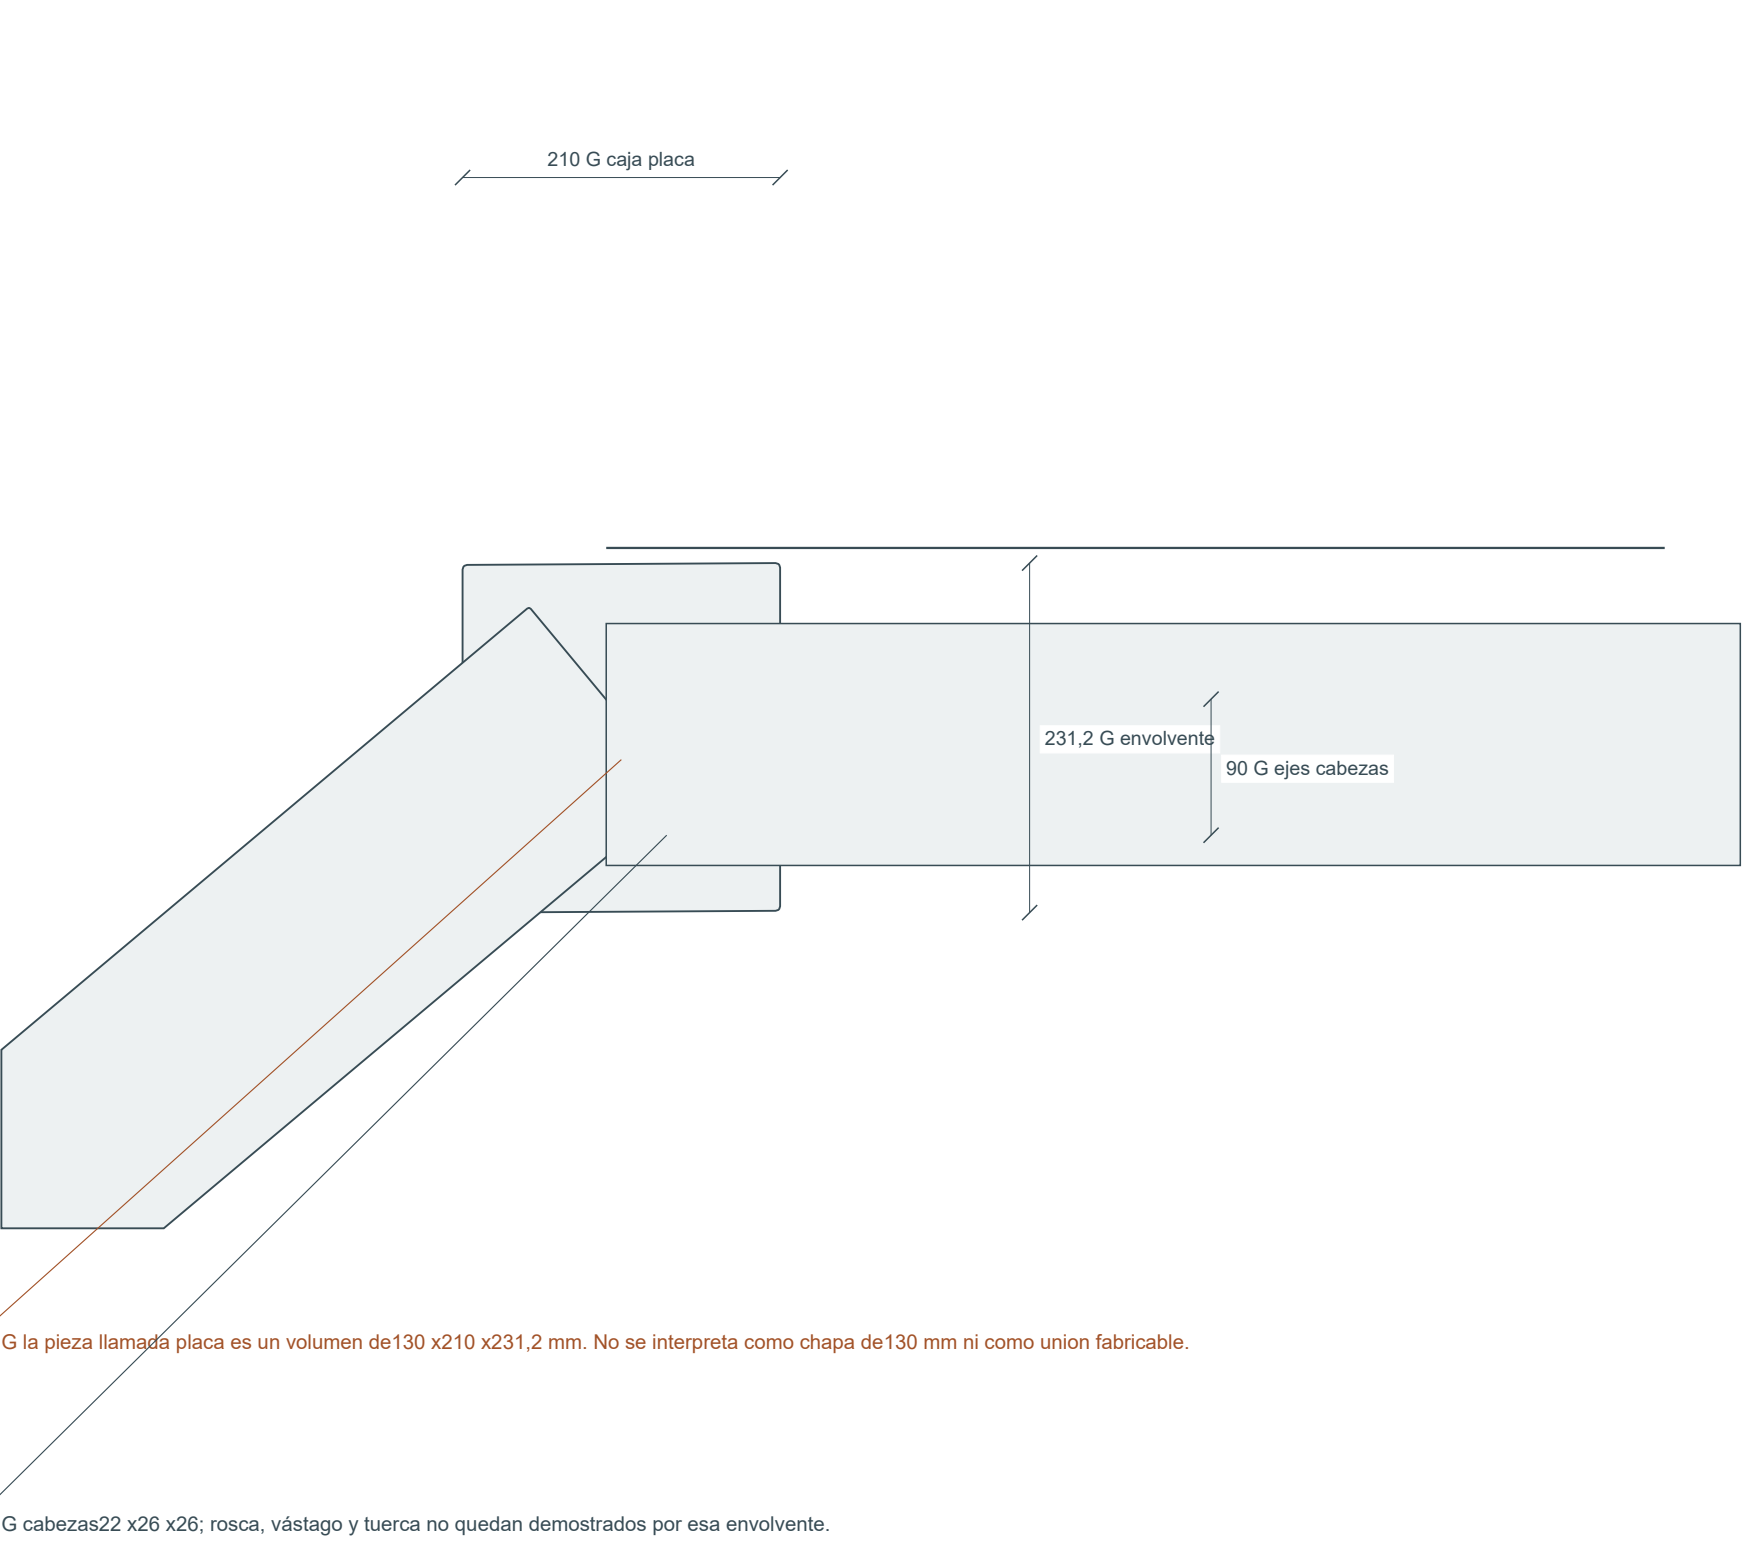

10 P doble cartela / seccion transversal | 1:5

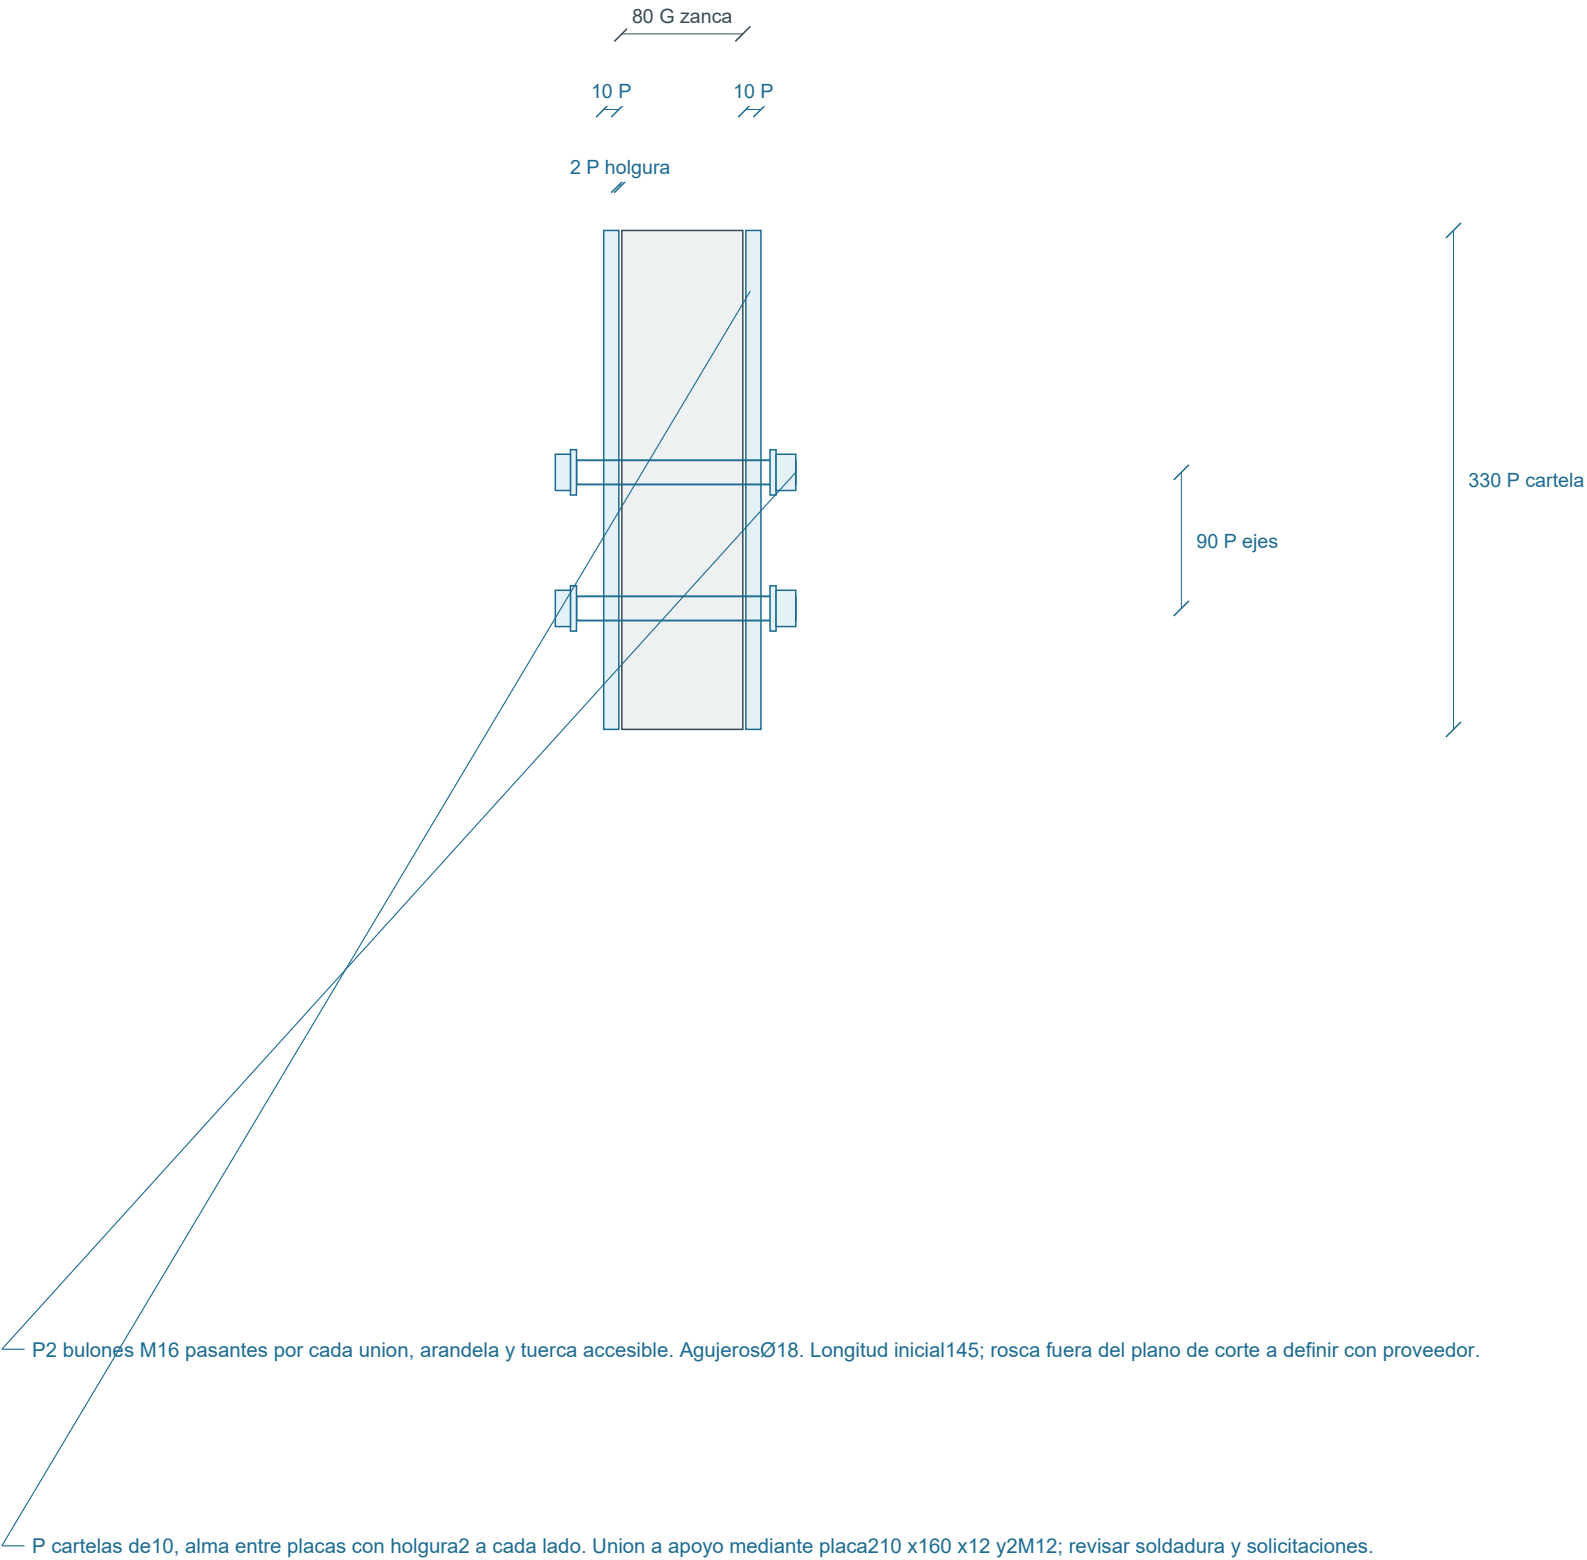

ARRANQUE PROPUESTO P

Placa inferior 180 x 160 x 12 sobre grout 20; 2M12 ejes 100 con empotramiento conceptual 100 en dado 300 x 300 x 250. Estos tamaños dibujan una reserva de coordinacion: suelo, fundacion, armado y resistencia no estan calculados.


R5 | Hilti: Base plates - design considerations

G = medido / gris

P = propuesta dimensional / azu

Todas las cotas en mm salvo niveles en m

11 Apoyo inferior / seccion P | 1:5

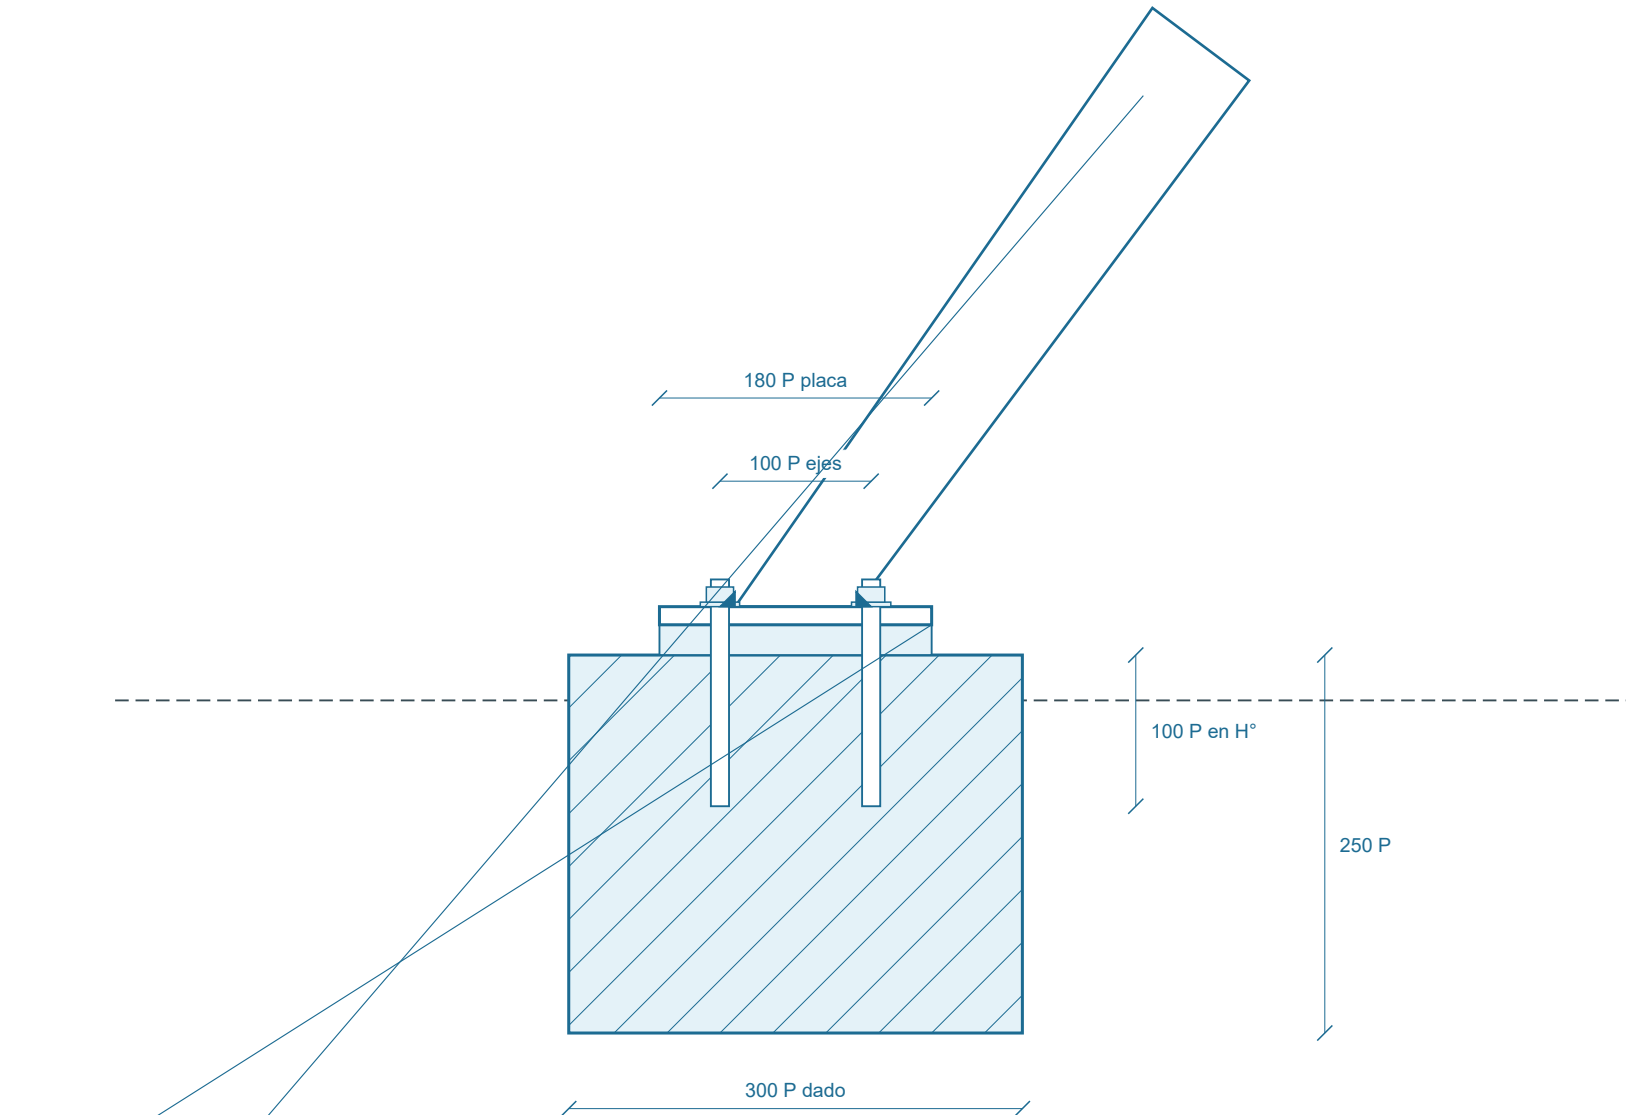


≤ P placa 180 x 160 x 12; grout 20 sobre dado 300 x 300 x 250. Vástagos M12 con 100 dentro del hormigón; cabeza, arandela y tuerca accesibles.

— P zanca soldada a placa: contacto continuo, limpieza y proteccion anticorrosiva. Espesor y largo del cordon requieren solicitudes y material.

R5 | Hilti: Base plates - design considerations

12 Plantilla de arranque / planta P | 1:5

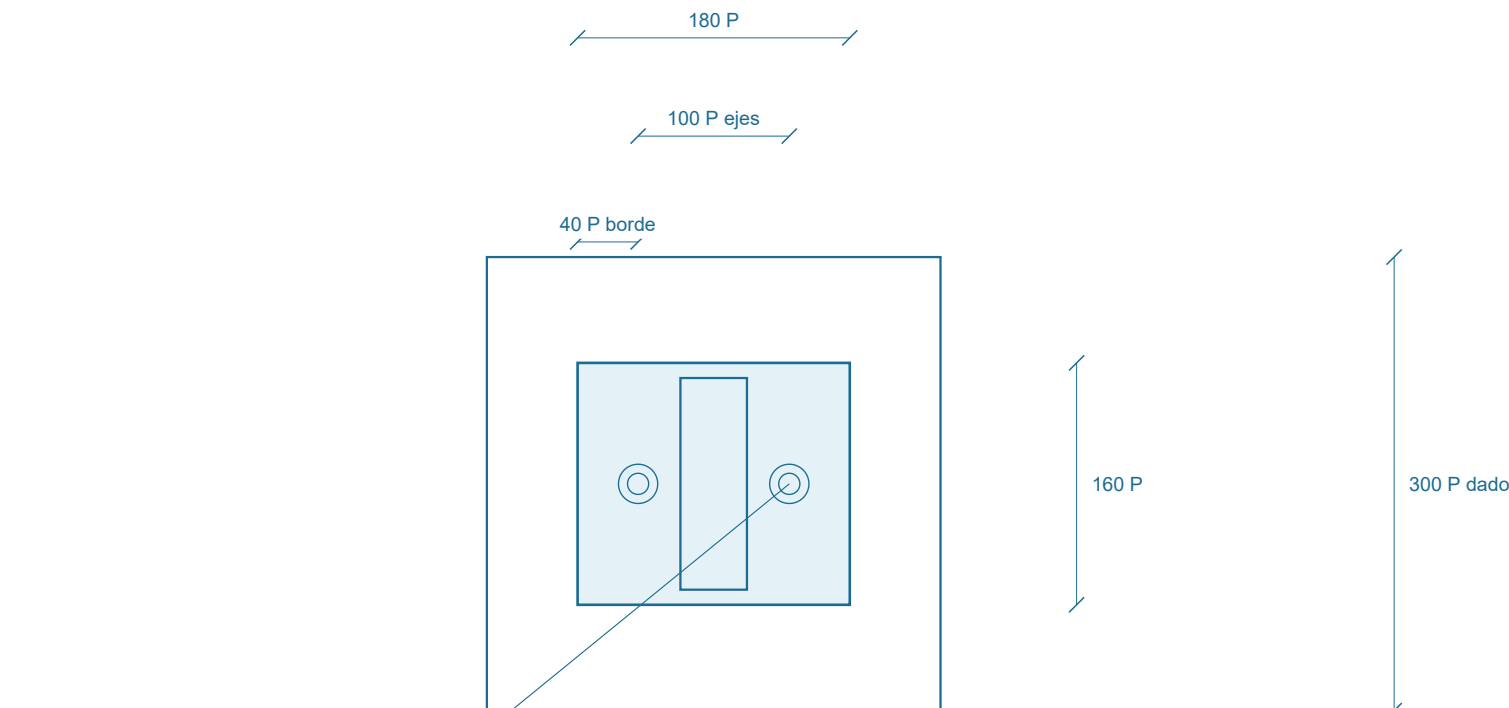

∠ P2 agujerosØ14 para M12. El dibujo reserva montaje y acceso de llave; diametro, tipo de anclaje y tolerancias finales segun sistema seleccionado.

— P apoyo propuesto fuera del pavimento terminado; ajustar cota a la primera contrahuella del recorrido A07. Suelo, zapata real, armado y cargas no calculados

R8 EN REVISION / SIN APROBACION9,9 / SIN CALCULO DE CAPACIDAD


A2 / imprimir al 100 %

G = medido / gris

P = propuesta dimensional / azul


Todas las cotas en mm salvo niveles en m

11 Panel de80 / montaje P dentro de huella | 1:5

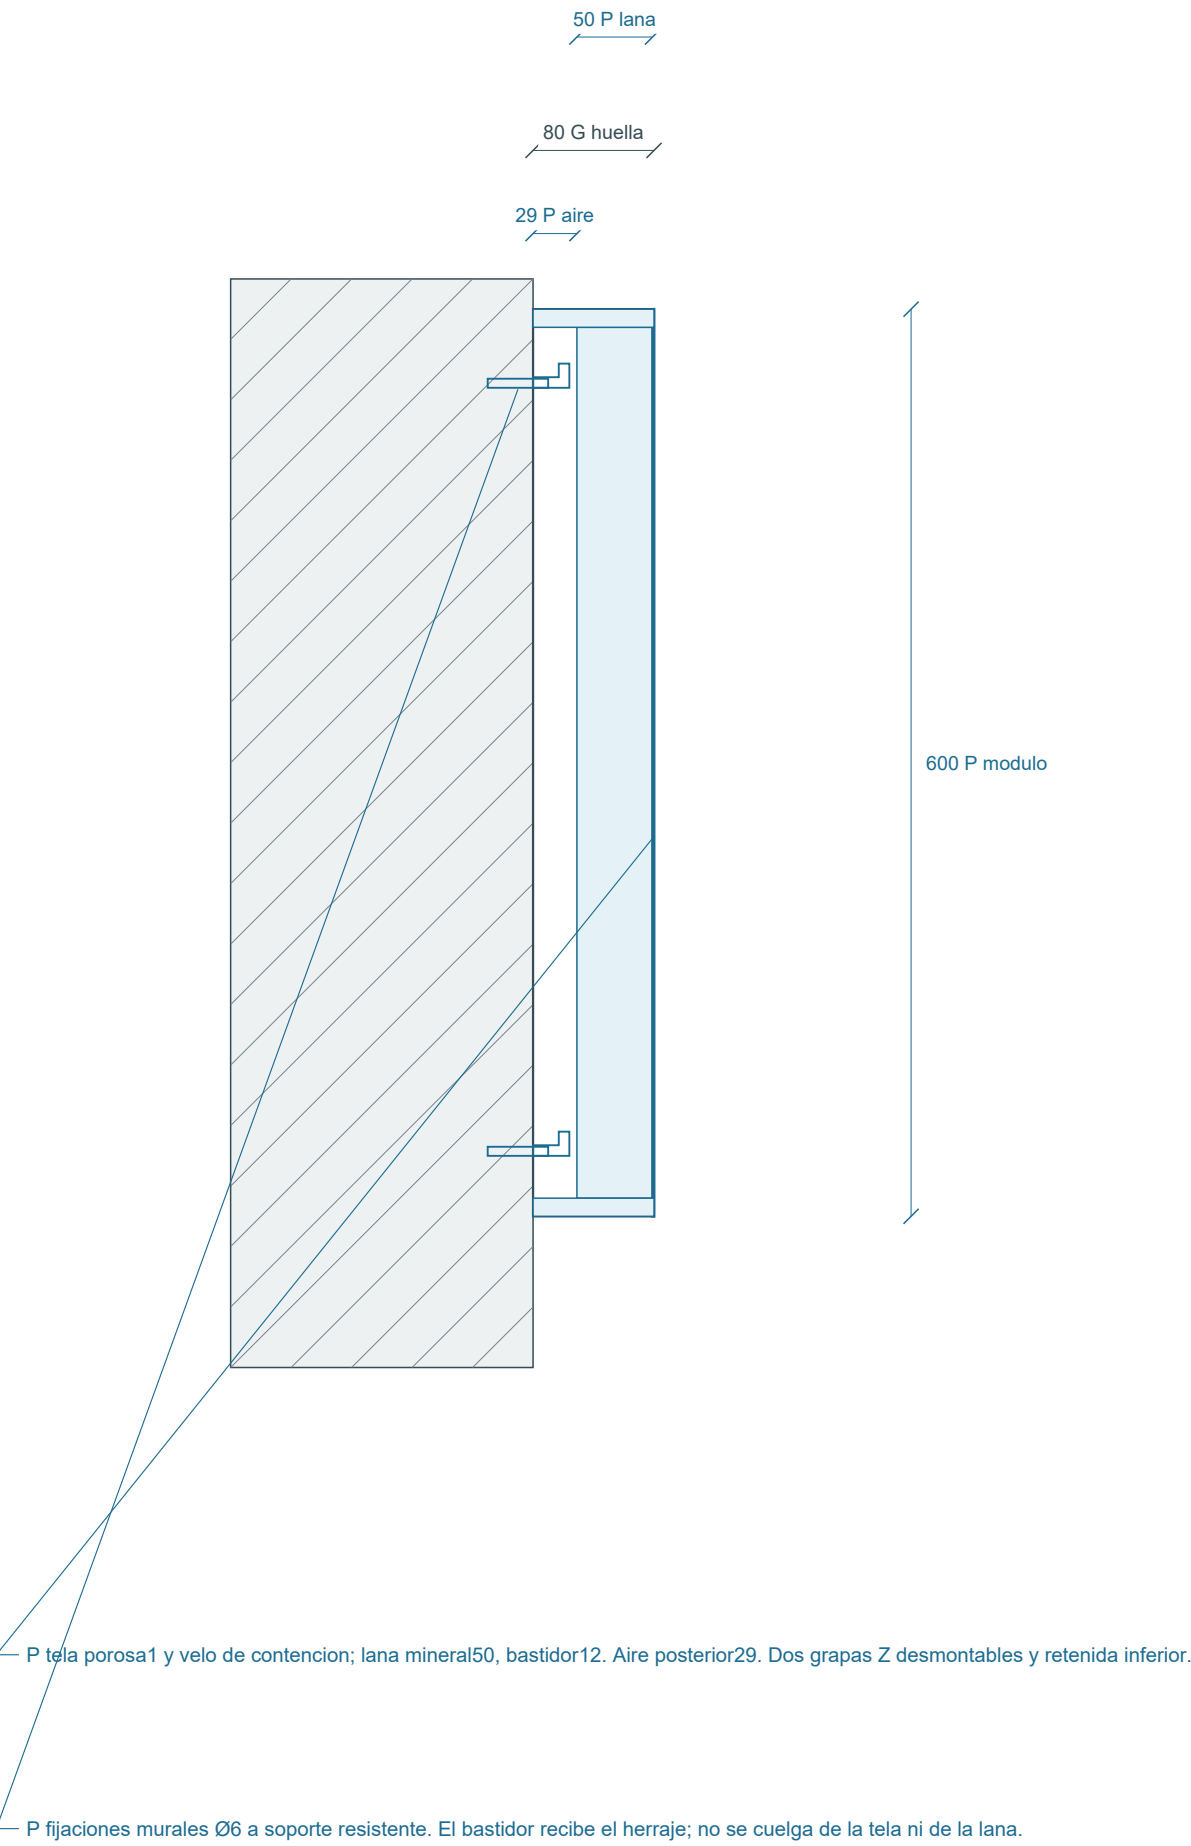

R3 | GIK Acoustics: How to Hang Acoustic Panels


Cielorraso P sobre baffle G / corte parcial | 1:5

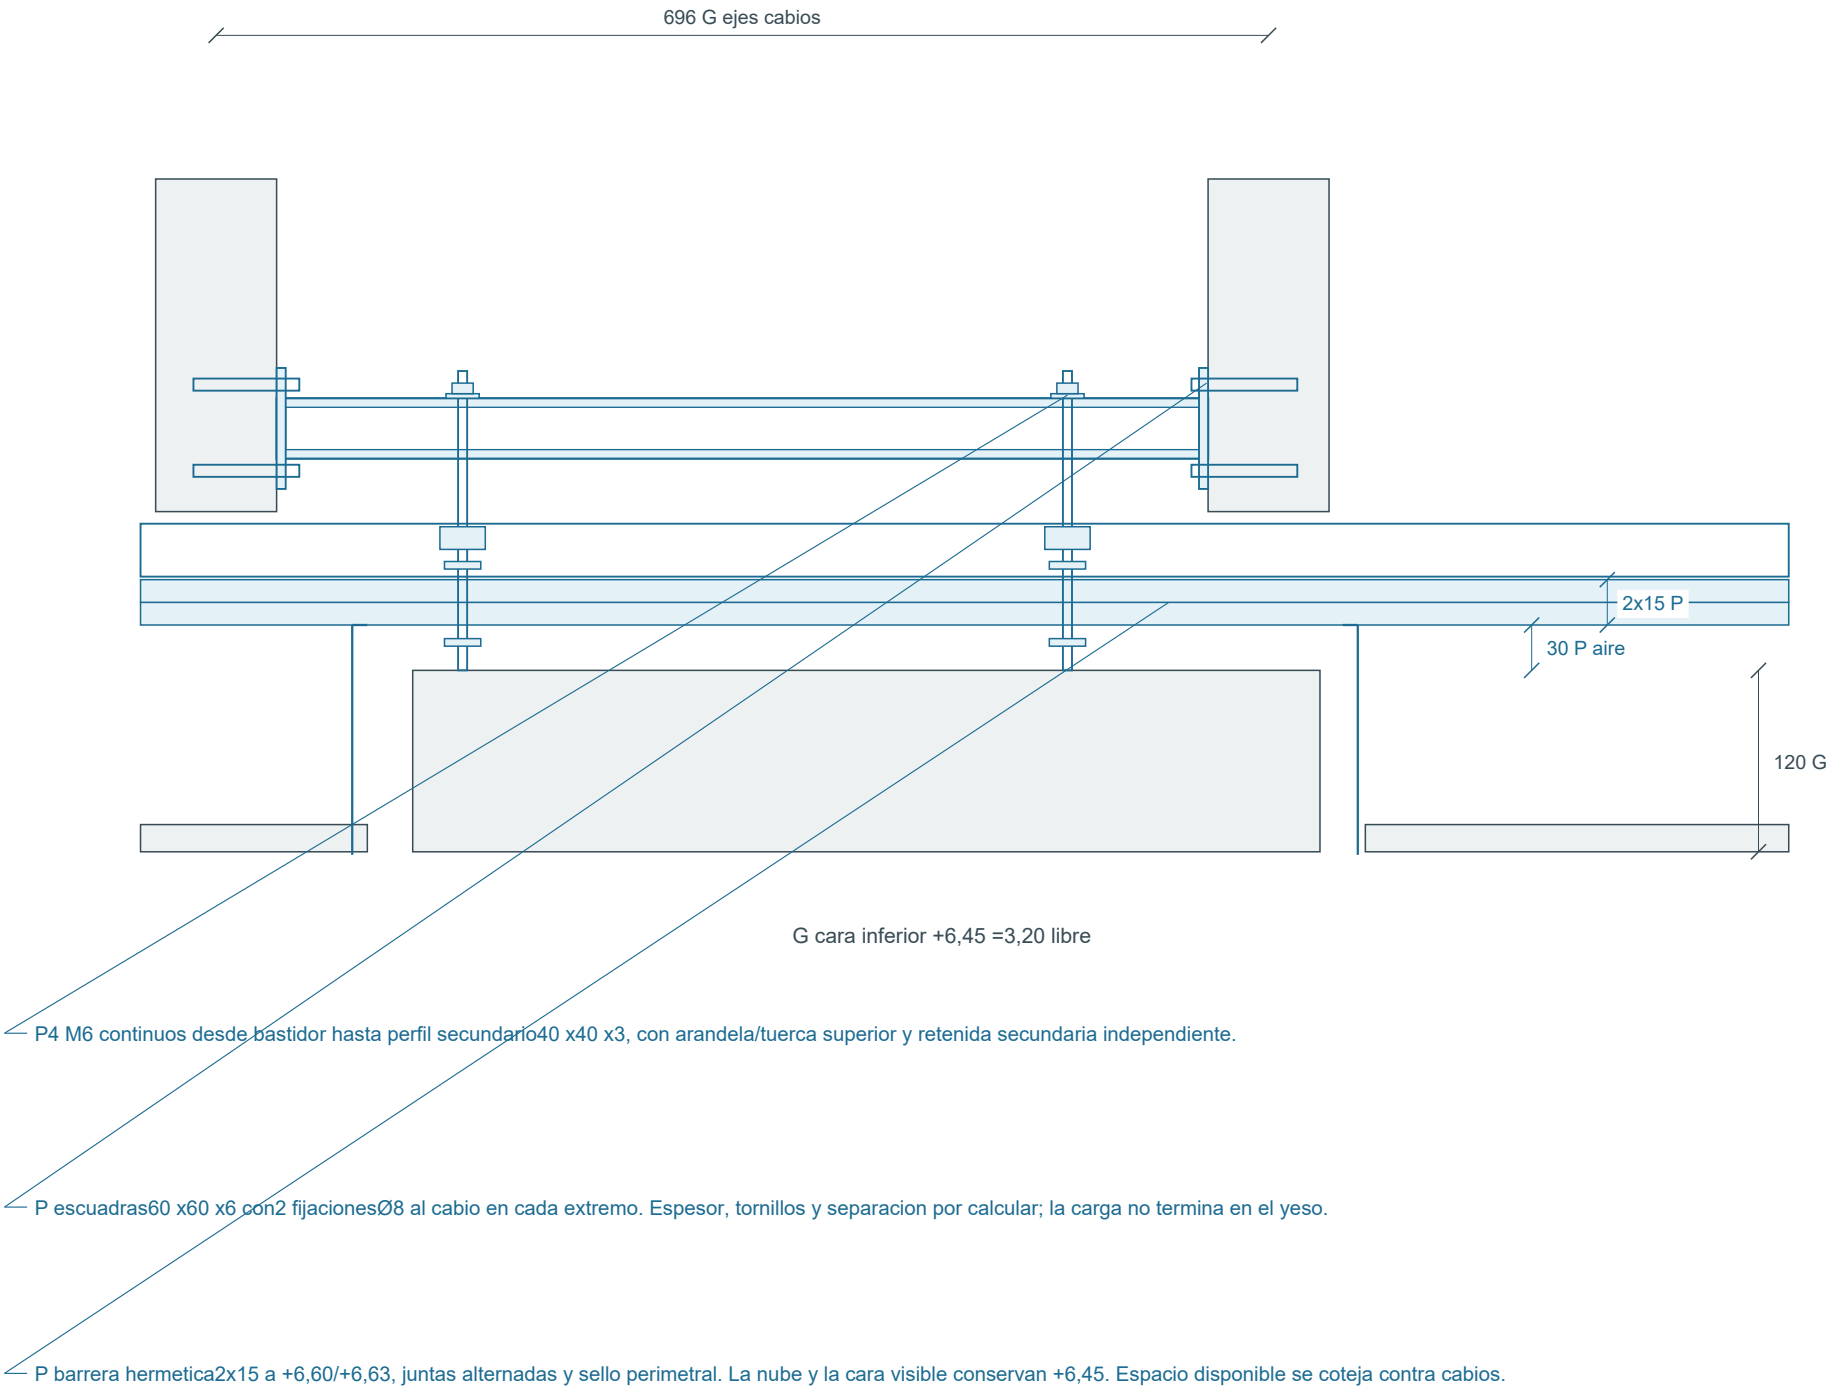

R6 | ROCKWOOL: Acoustic insulation - installation and flanking


G = medido / gris P = propuesta dimensional / azul Todas las cotas en mm salvo niveles en m

13 Puerta estudio / umbral y doble sello P | 1:5

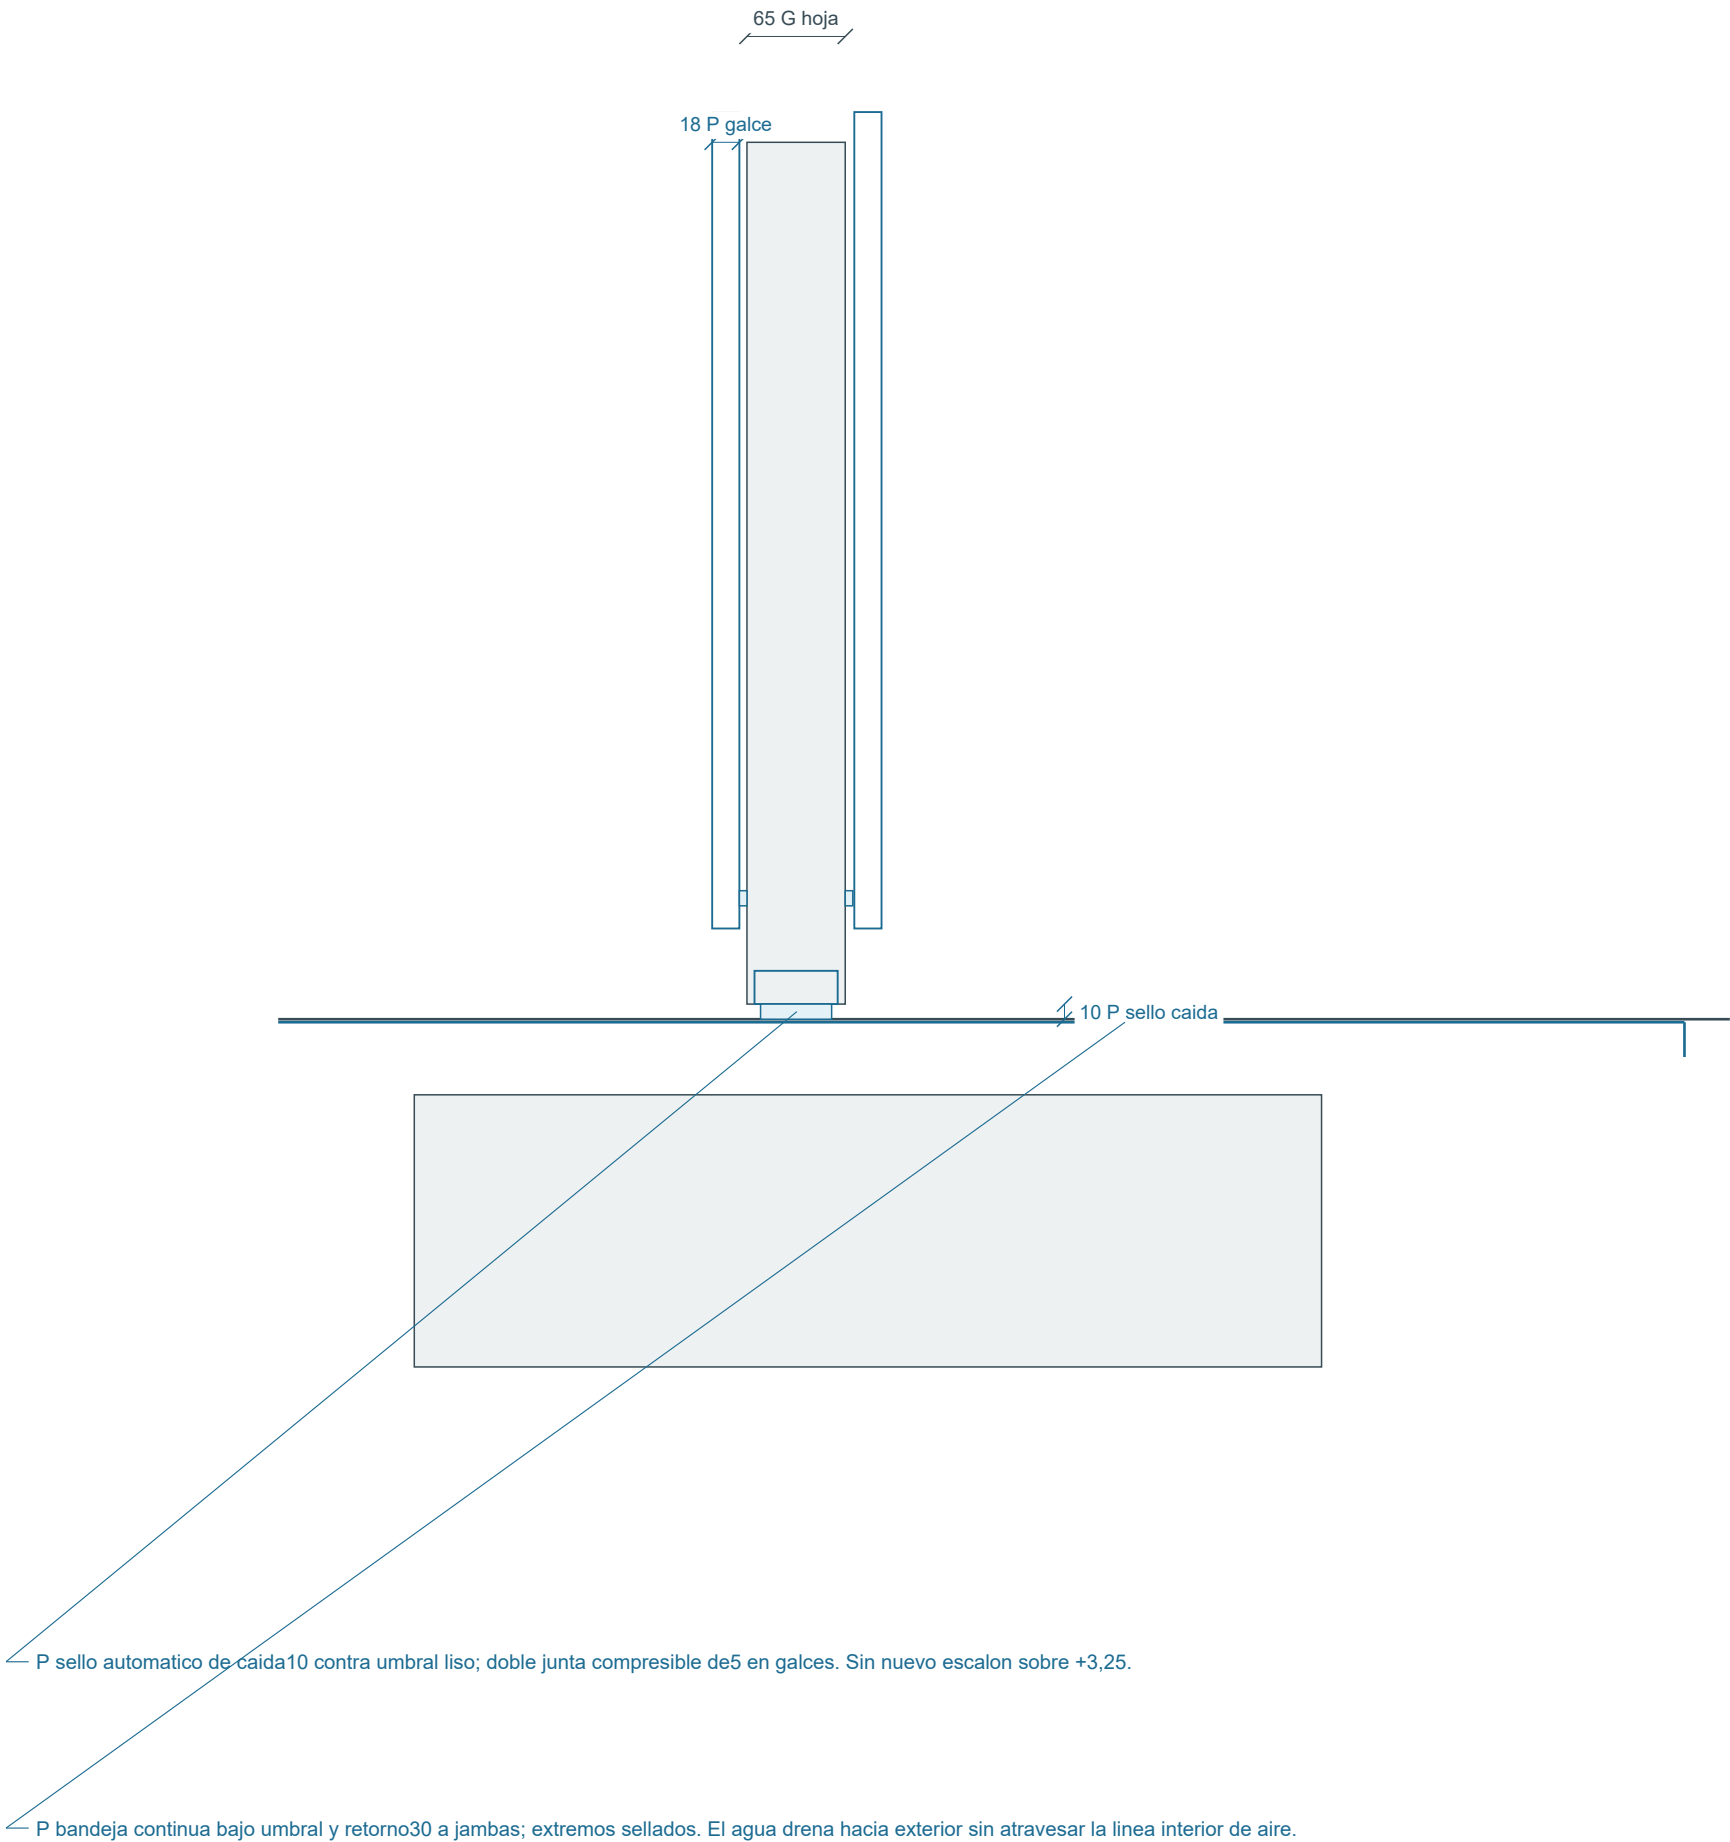


R6 | ROCKWOOL: Acoustic insulation - installation and flanking

14 Paso de servicio frio / sellado P | 1:5

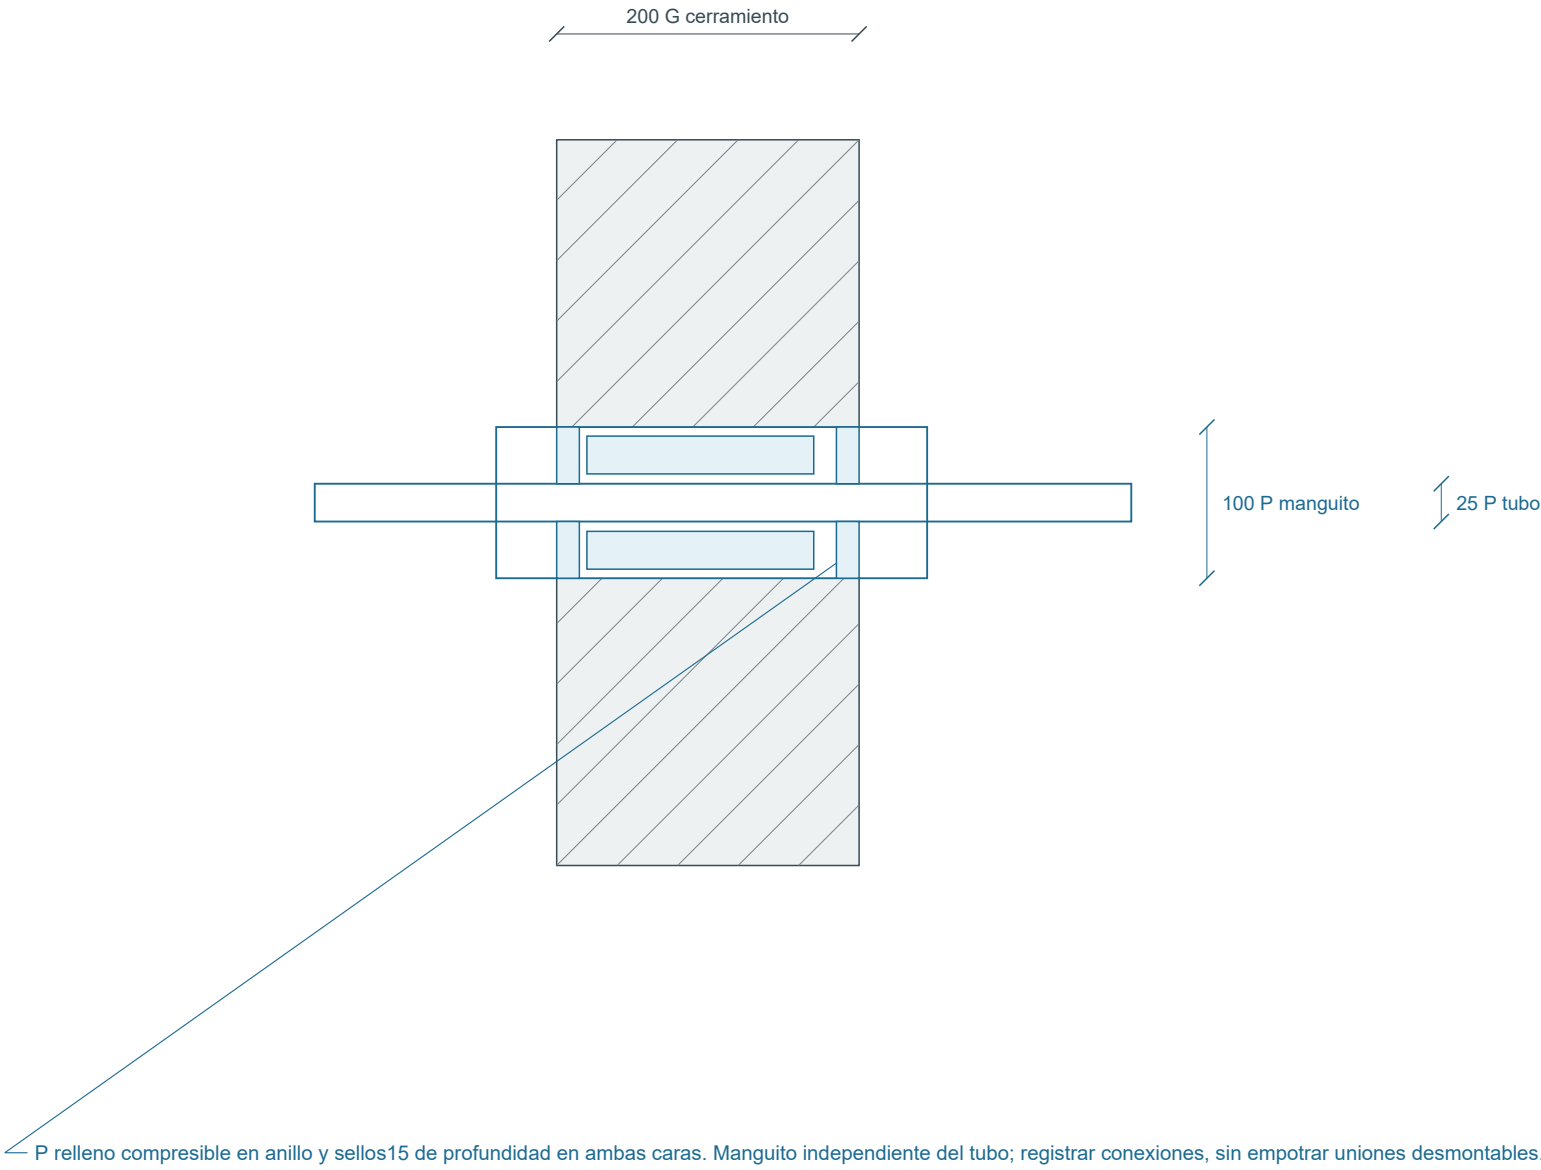

15 Relieve G / soporte posterior P | 1:5

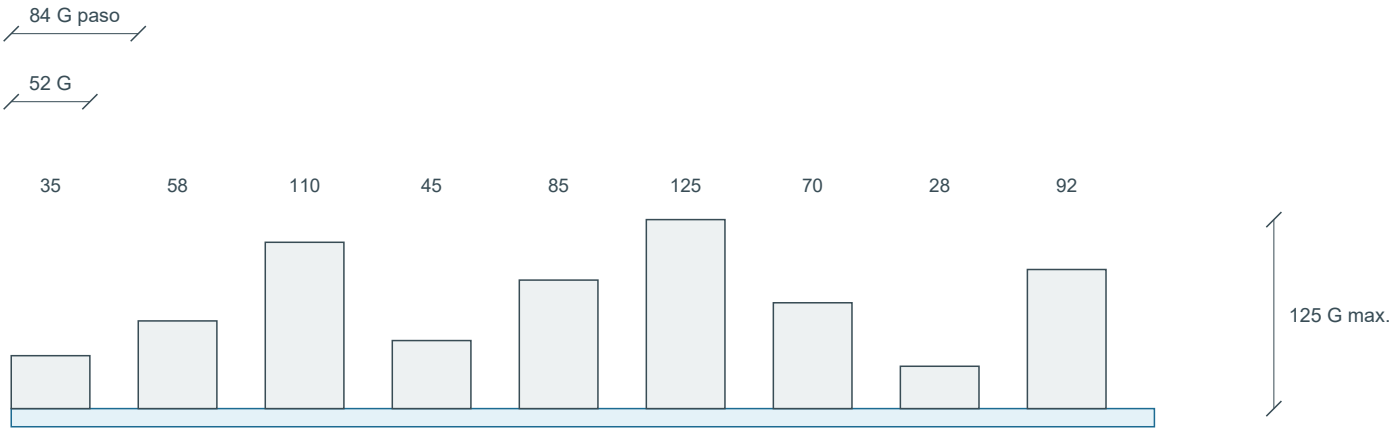


G relieve sin desempeño QRD demostrado. P respaldo12, grapa Z18 y retenida inferior; absorcion/difusion se verifican con sala terminada.

G = medido / gris

P = propuesta dimensional / azul


Todas las cotas en mm salvo niveles en m

16 Planta de cielorraso y plenum | 1:50

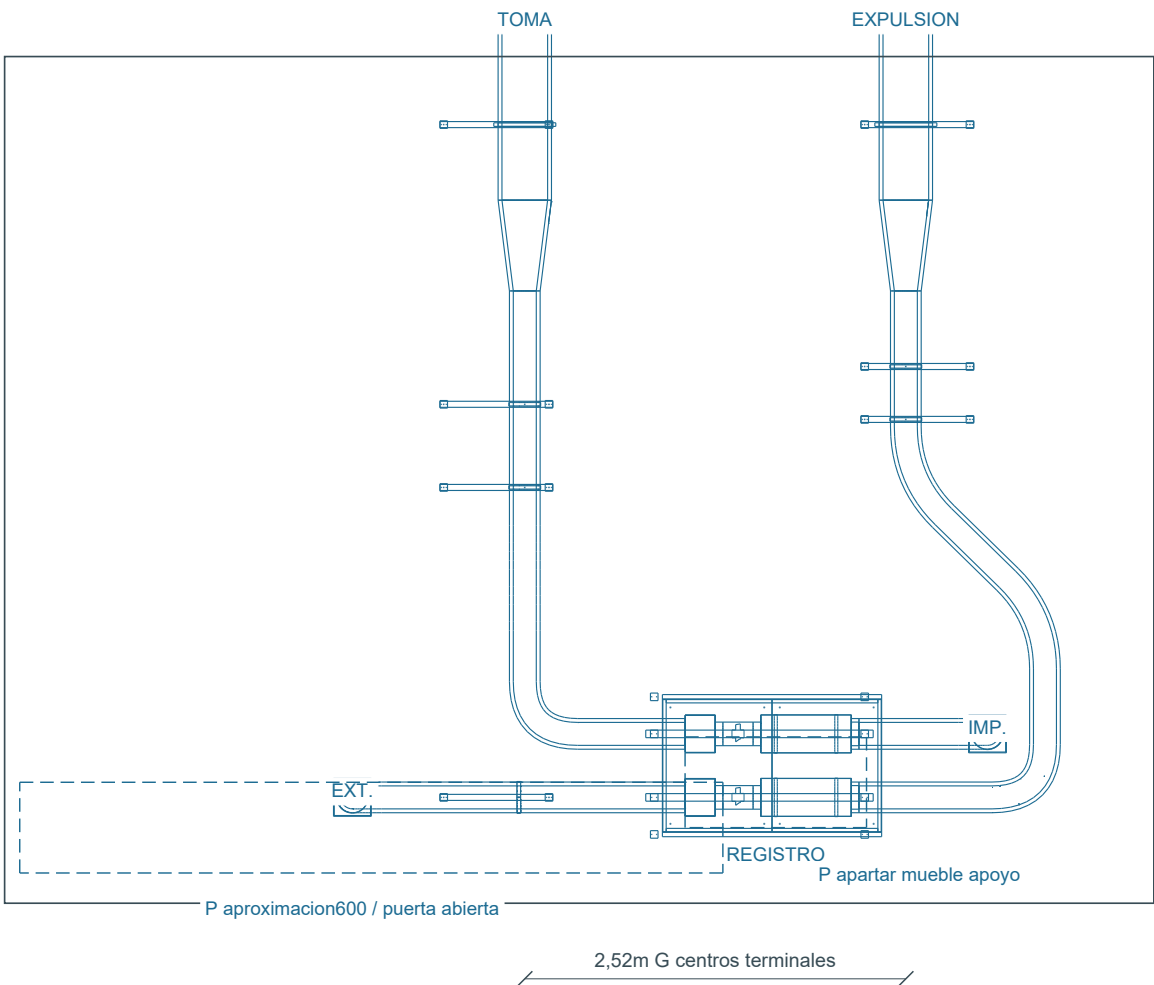


P retro: tapas; filtro por abajo; fan con dos flexibles; silenciador con acoples, abrazaderas y sus dos colgantes. El otro circuito y los bastidores permanecen. No se desmontan nubes.


18 Equipo / corte Z4,68 | 1:10

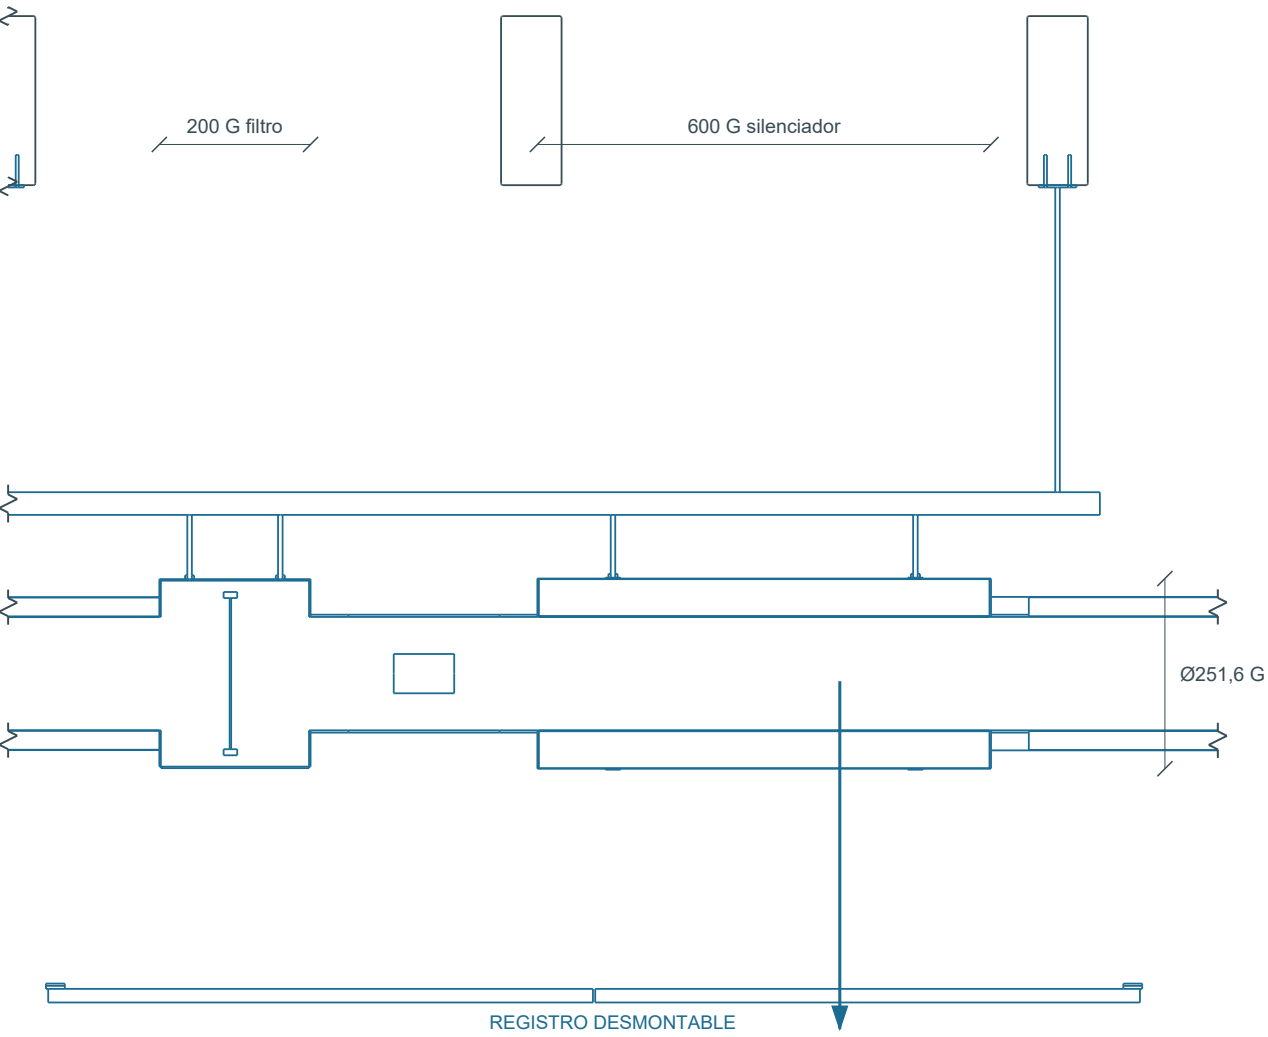

19 Acceso / X19,40 + P | 1:25

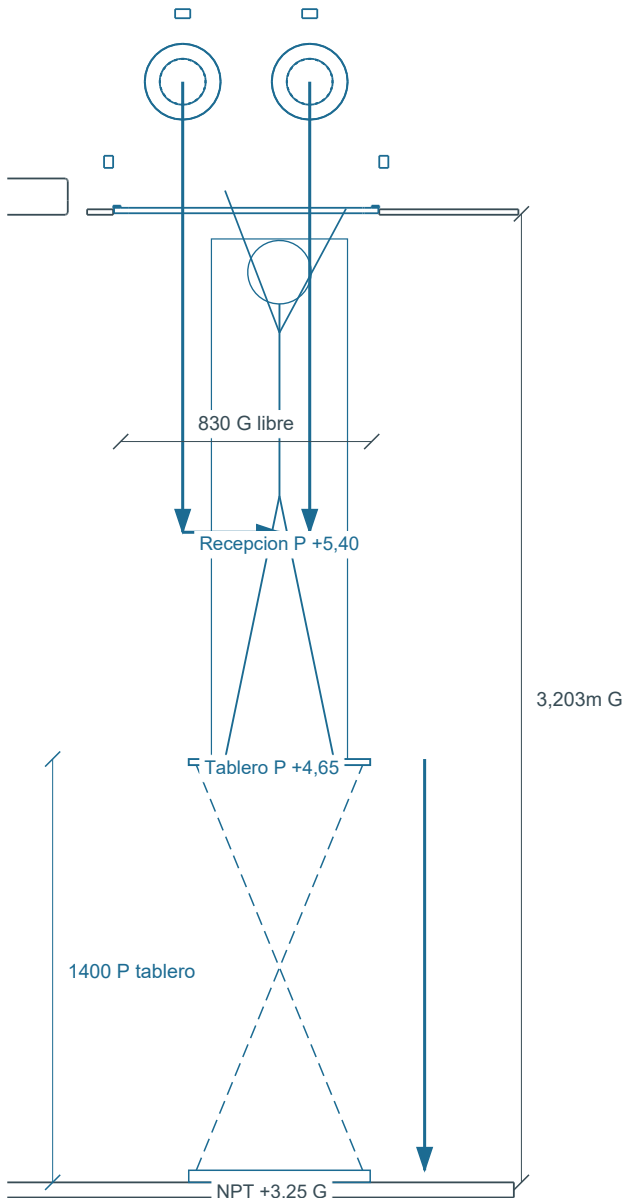


17 Axonometria de montaje / sin escala

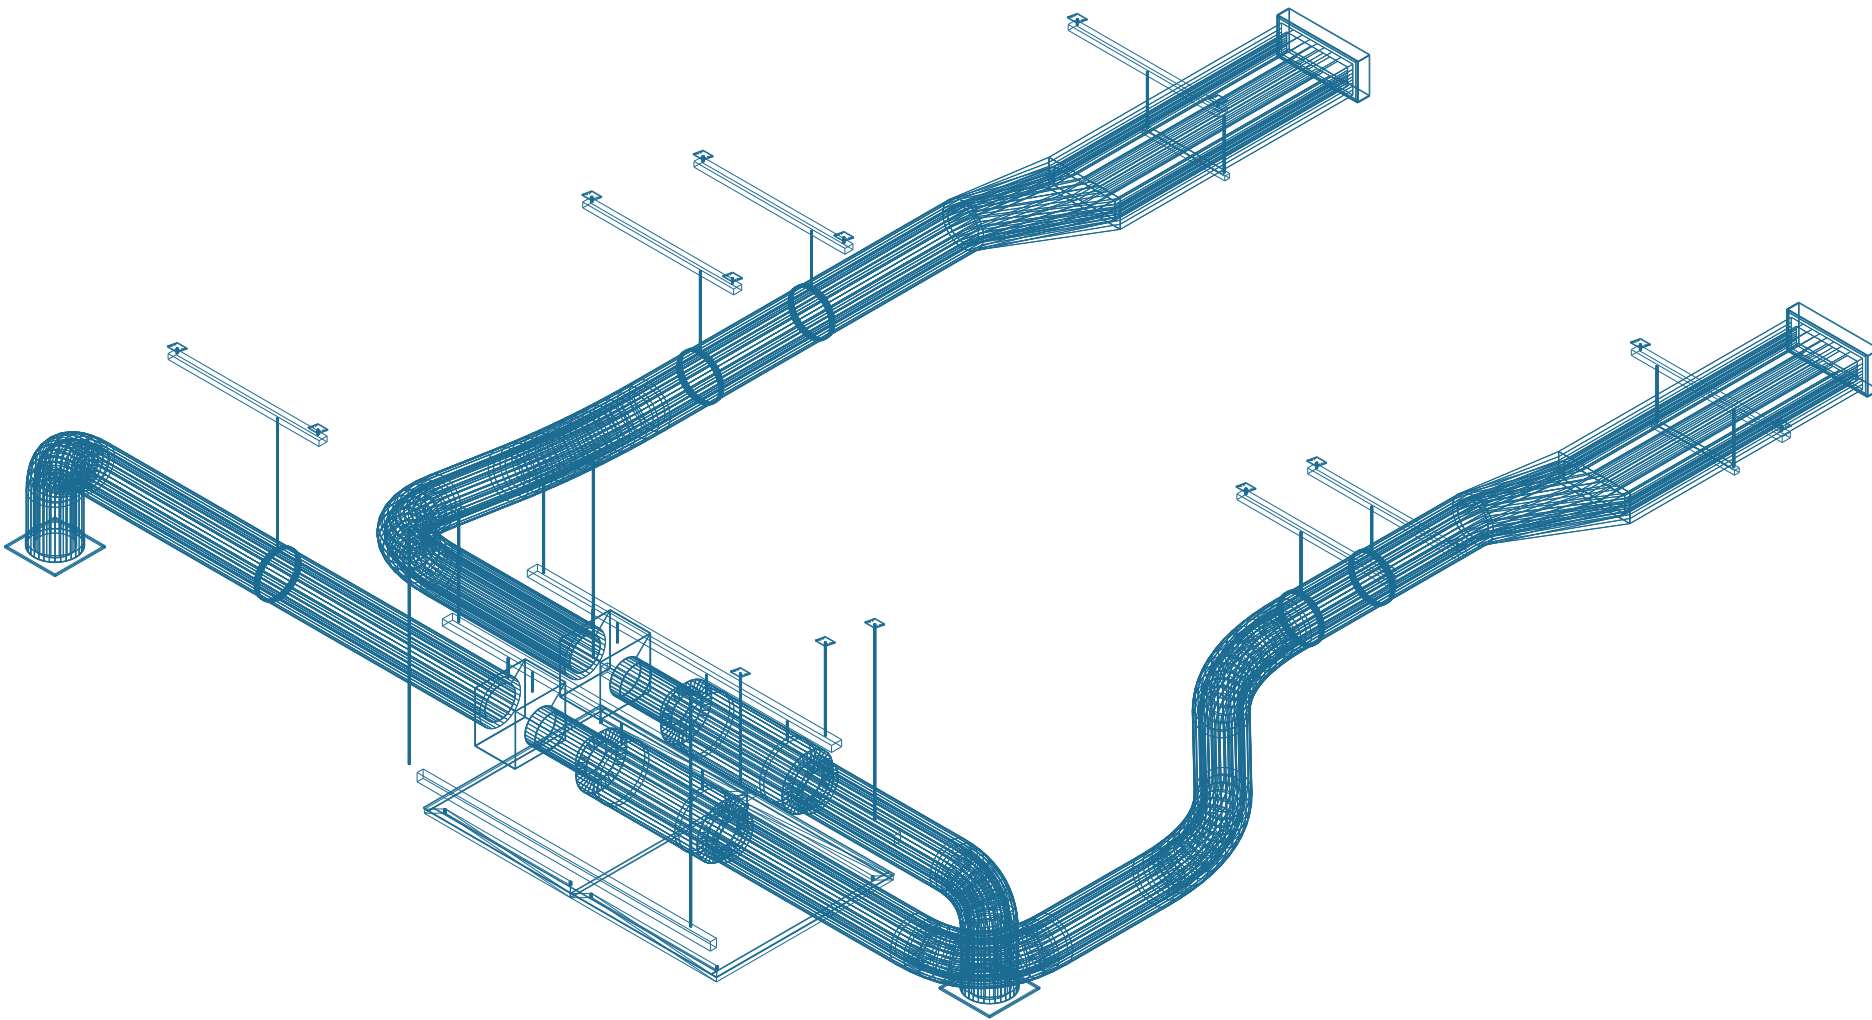

P medio auxiliar no modelado: plataforma elevadora 1200x600, tablero +4,65; cuerpo 450x1720, cabeza +6,37. Apartar mueble apoyo y 4 patas. Retirar a +5,40; trasladar sobre tablero y descender al piso. Operario cambia X segun modulo; seleccionar equipo, alcance, herramienta y capacidad.

20 Frente / corte X17,64 | 1:20

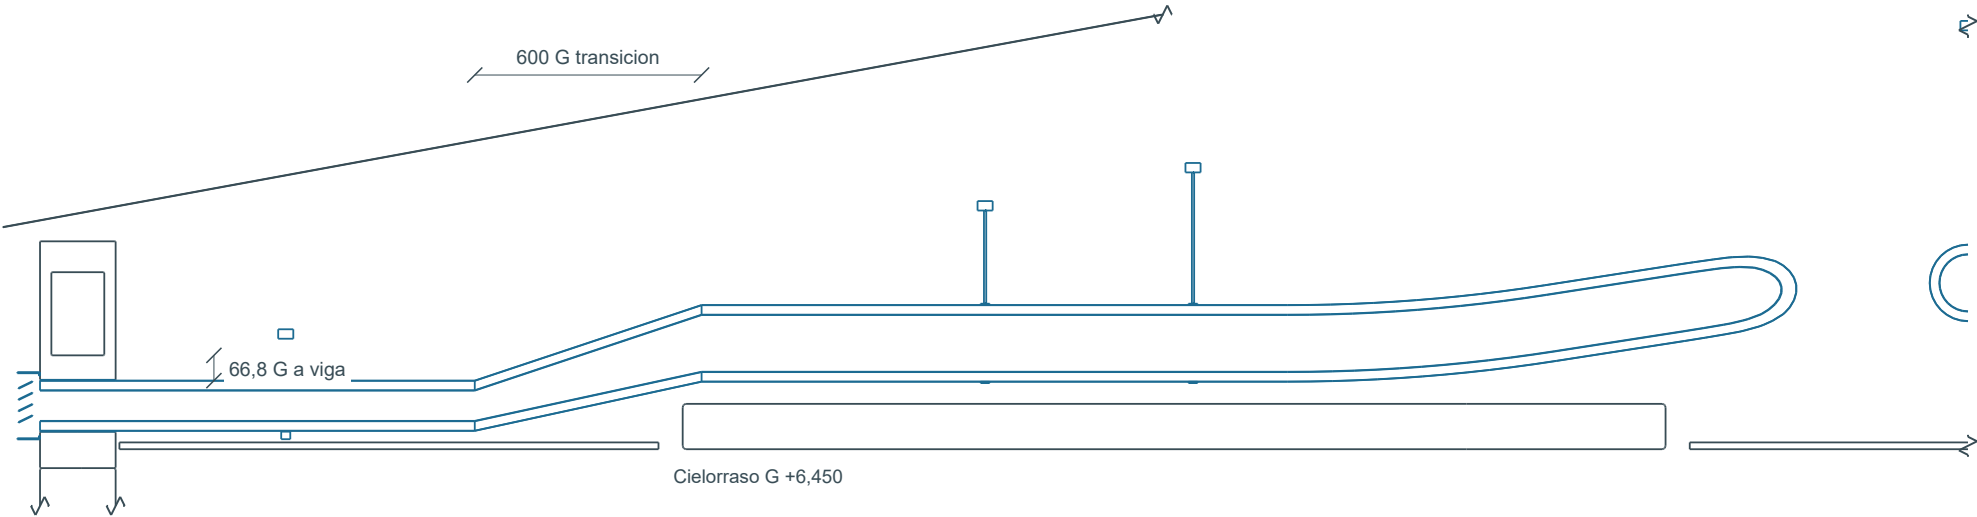


G seccion rectangular 300x80; area 0,024m2. Chapa 1 + aislacion 25 + camisa 0,5; exterior 353x133. P seleccion, caudal, ruido, condensacion y fijaciones pendientes de proyecto.

G = medido / gris

P = propuesta dimensional / azul

Todas las cotas en mm salvo niveles en m


18 Transicion humedo-seco / geometria G | 1:5

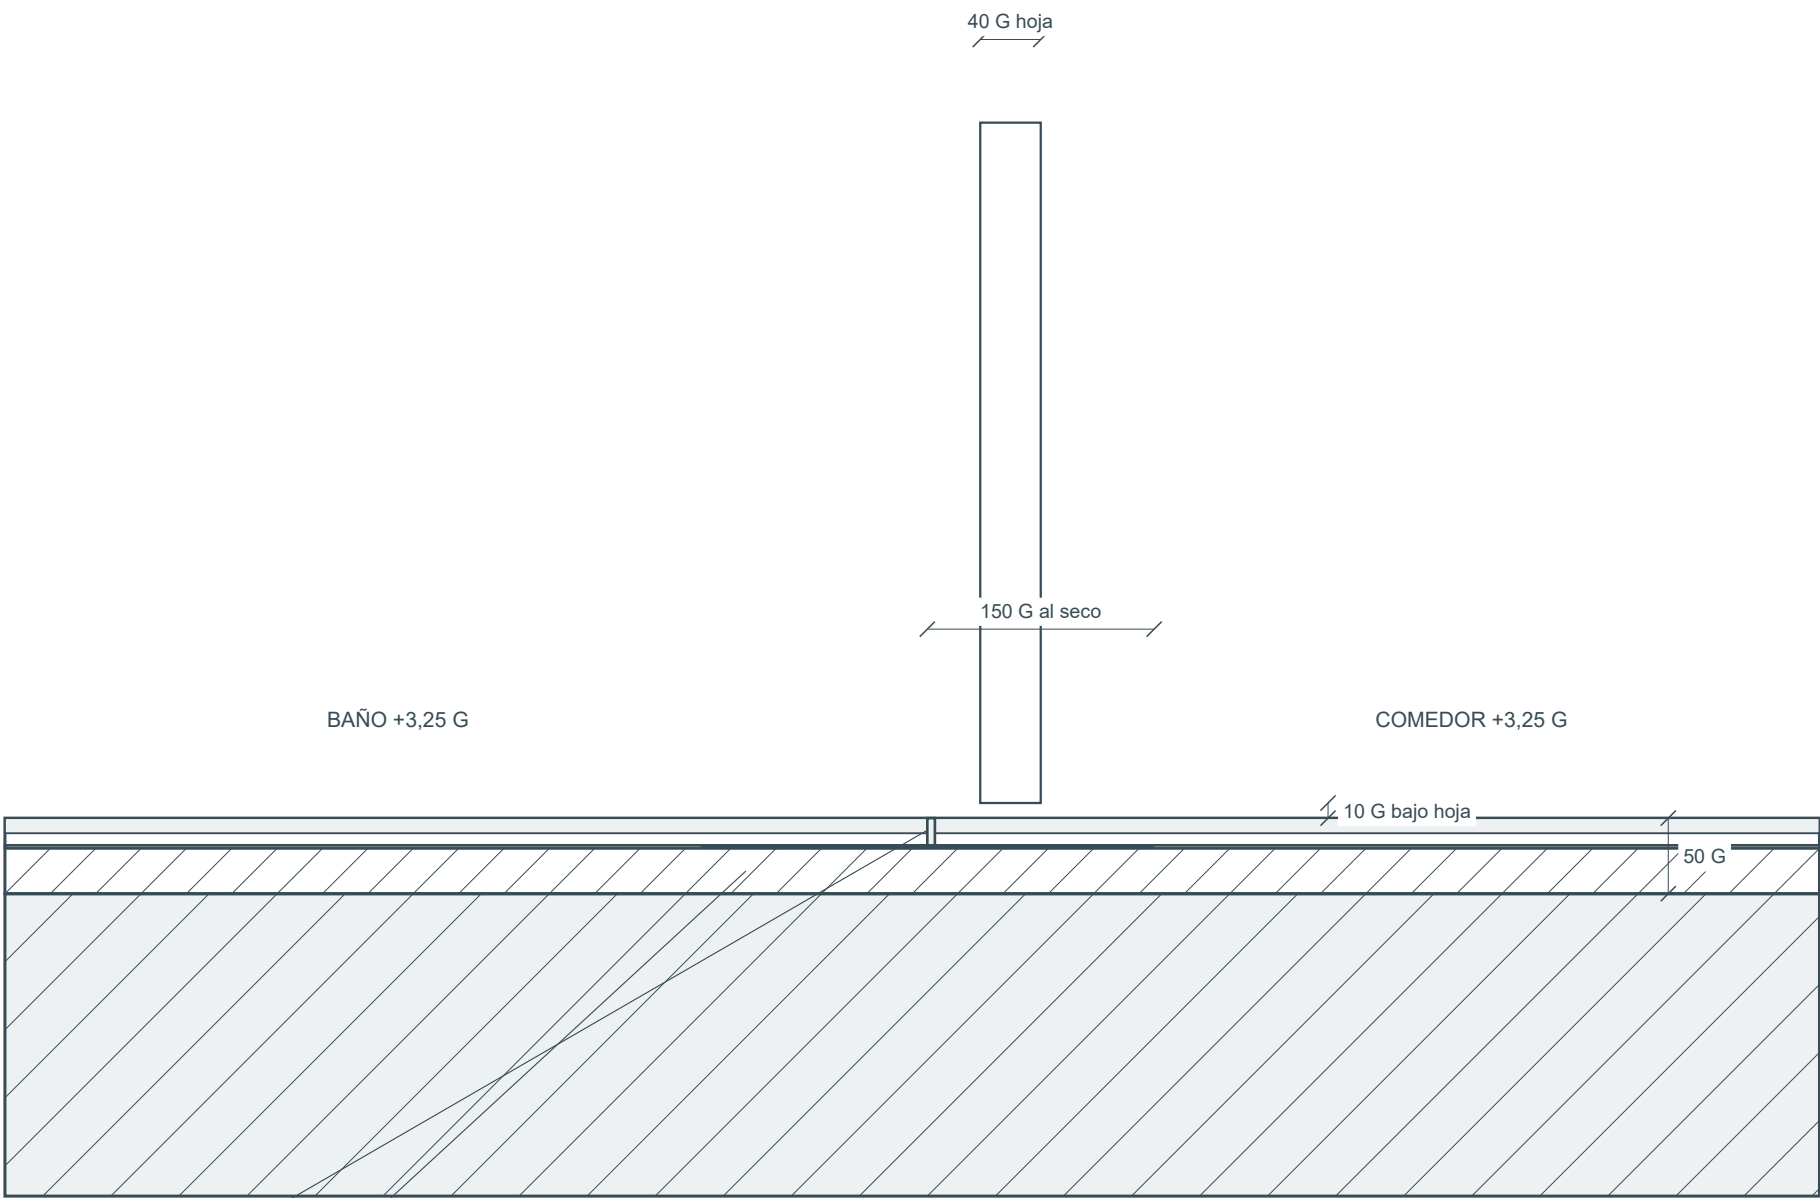

G junta elastica5 en terminacion; banda flexible bajo baldosa, prolongacion150 al lado seco y retorno en jambas. El paso queda sin resalto.

G composicion dentro de50: mortero30 + membrana2 + adhesivo8 + baldosa10. Verificar espesores del sistema elegido y soporte; no duplicar piso general bajo la zona humeda.

19 Corredera modelada / vista parcial G | 1:10

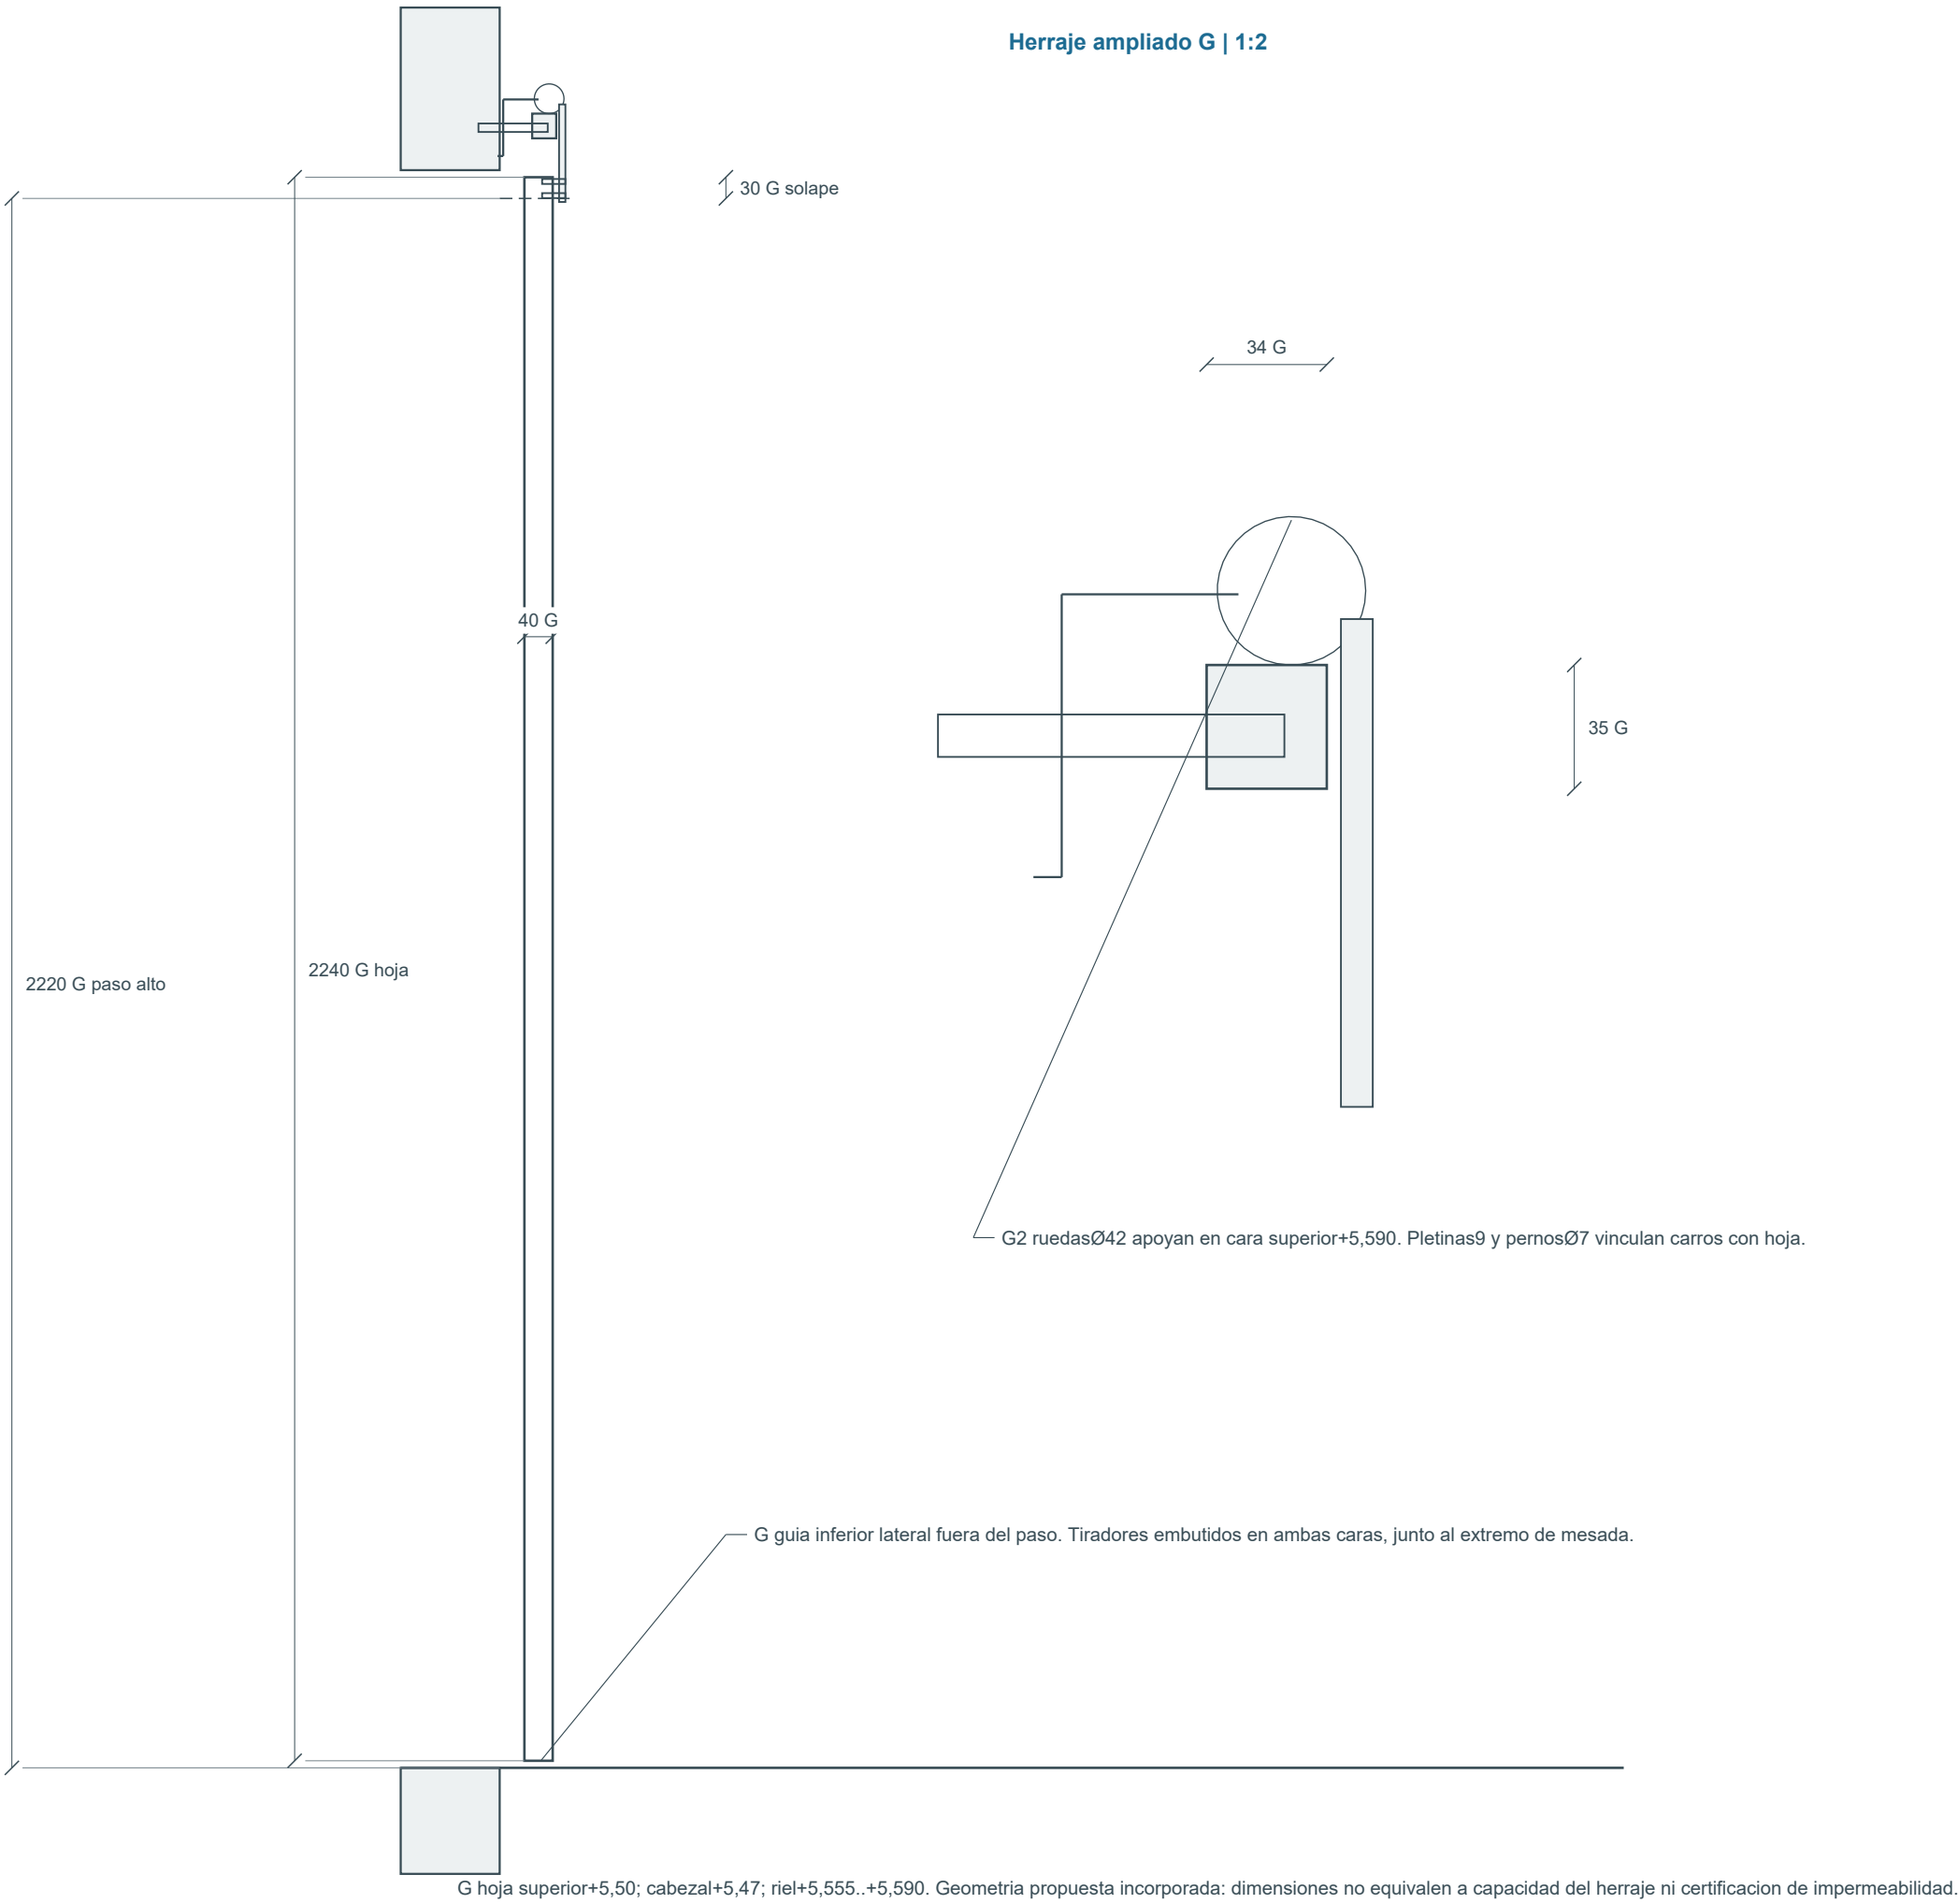

Herraje ampliado G | 1:2

R5 | Hilti: Base plates - design considerations

R8 EN REVISION / SIN APROBACION9,9 / SIN CALCULO DE CAPACIDAD

Base G: Casa_de_Campo_99_R8.blend / 60810e1945f53b33


G acredita geometria, no capacidad. P identifica propuestas; su presencia3D no valida prestaciones.

A2 / imprimir al 100 %


10 / 11-09-2026

G = medido / gris P = propuesta dimensional / azul Todas las cotas en mm salvo niveles en m


20 Rodadura / corte exacto de la geometria | 1:2

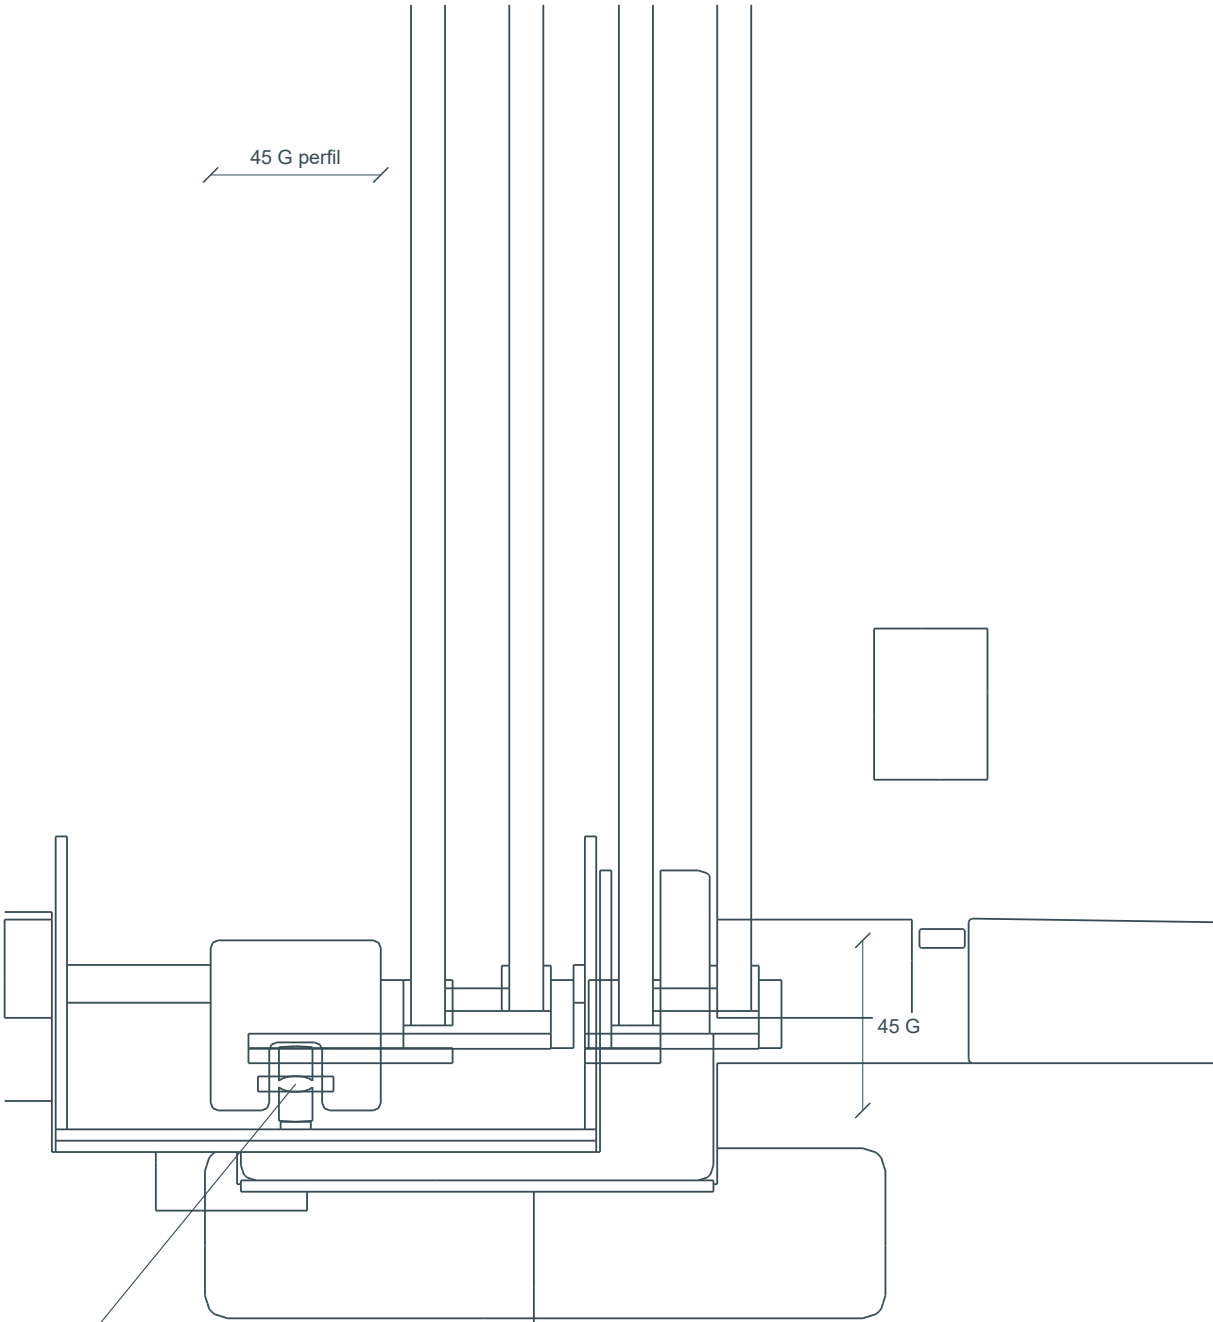


22 Guía superior / corte G | 1:2

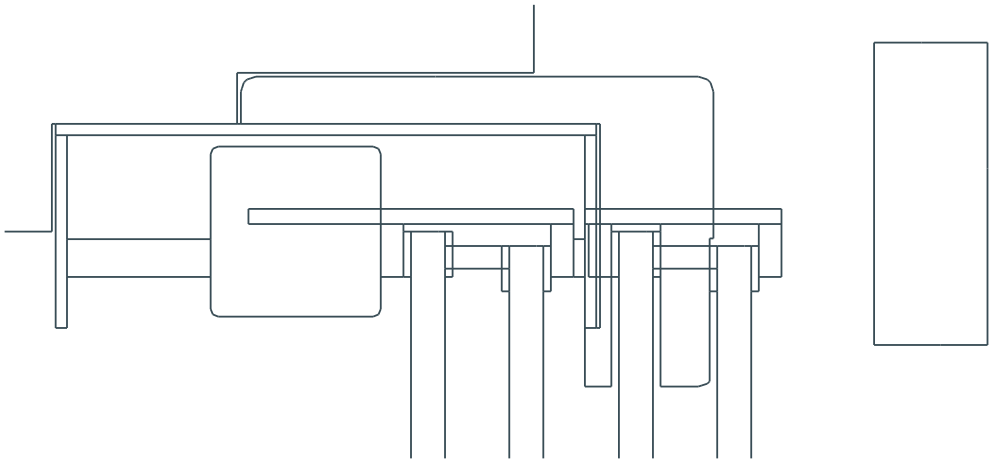

21 Acristalamiento / corte por tacos | 1:2

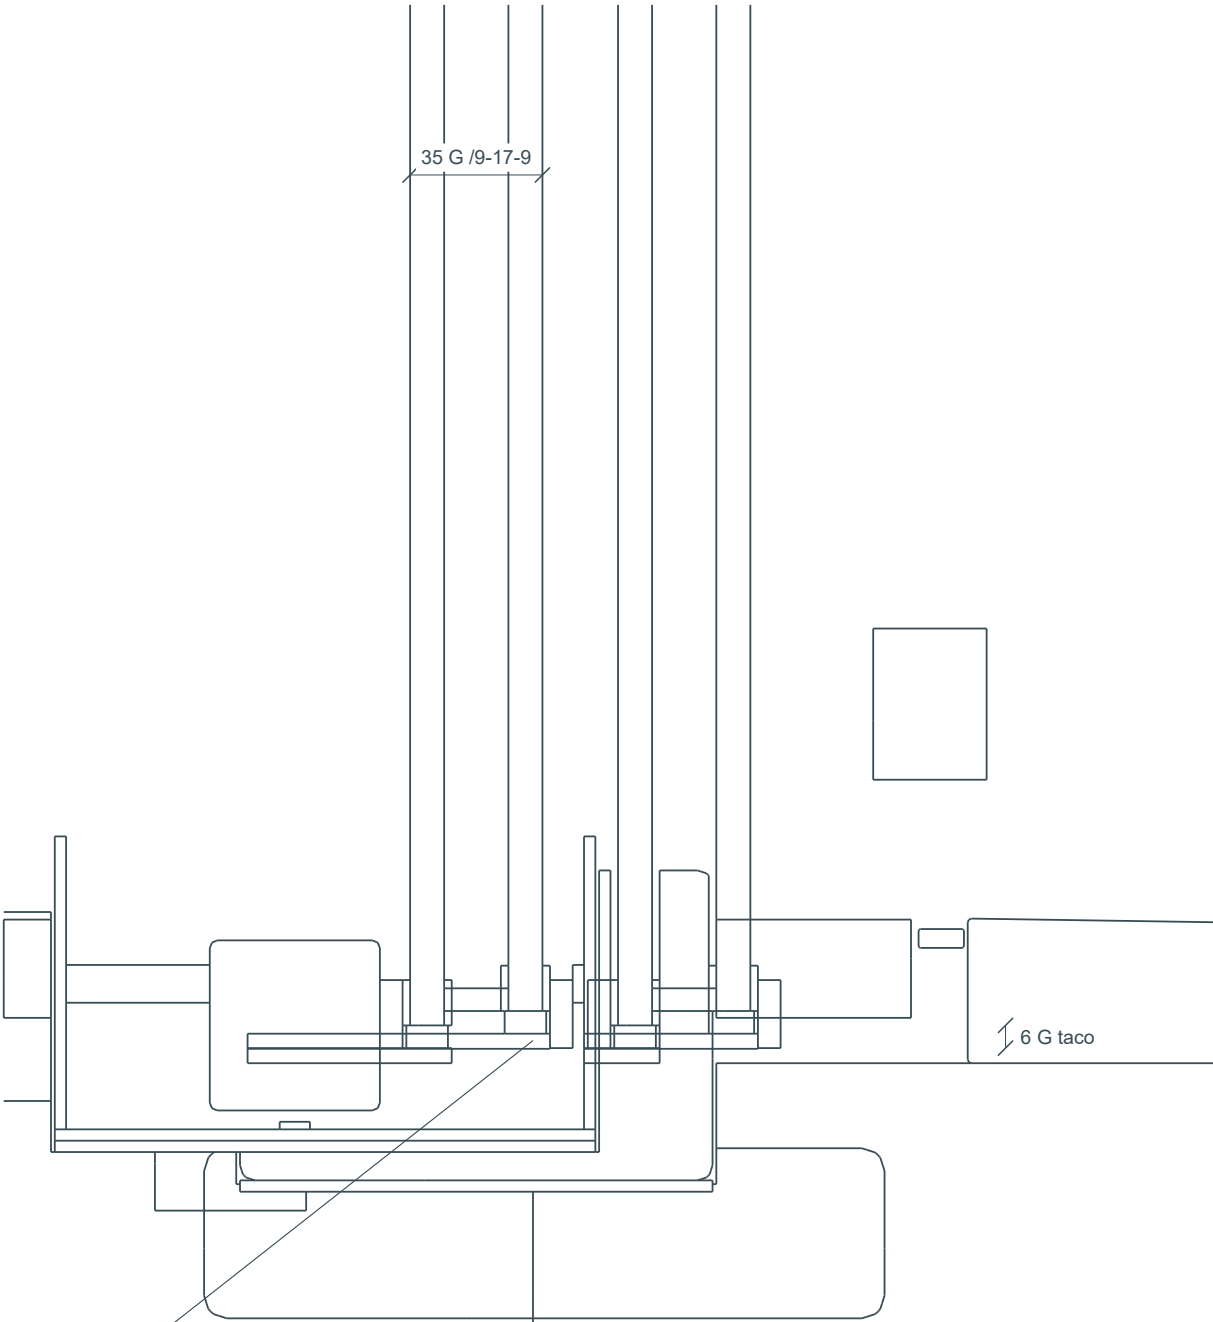

23 Drenaje al borde / corte G | 1:10

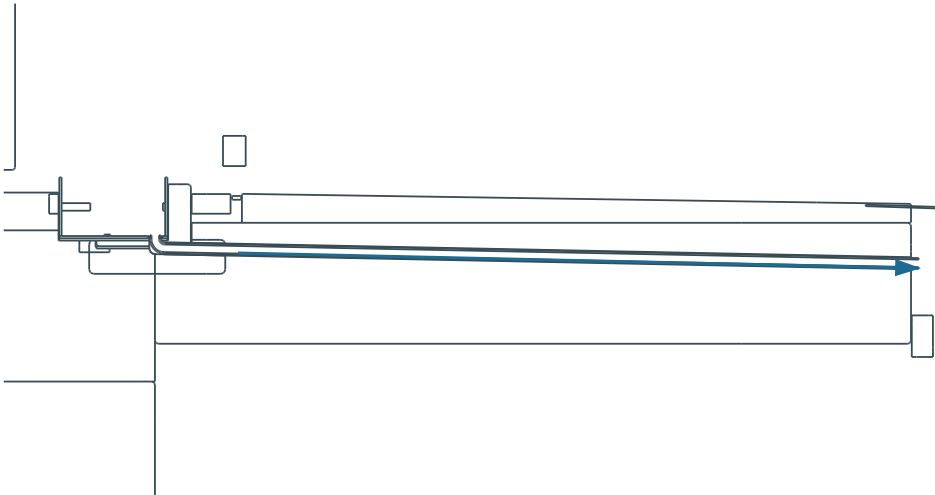

GEOMETRIA / LIMITES

G conserva 13 rigs, carrera y dimensiones de vidrios. Se vaciaron galces y perfiles; no se movieron los vanos.

Holgura nominal 3mm al contorno movil terminado; 2mm en galce de vidrio. Felpas y EPDM son geometria propuesta, sin ensayo de estanqueidad.

Rodillos y tacos son una propuesta de montaje. No hay capacidad, durabilidad ni especificacion de producto validada.


Rebajes de losas y dinteles, y perforaciones Ø16 para tubos Ø14, requieren coordinacion con armado y calculo. No se declara aptitud resistente.

G = medido / gris

P = propuesta dimensional / azul

Todas las cotas en mm salvo niveles en m

24 Ducha PB / planta | 1:10

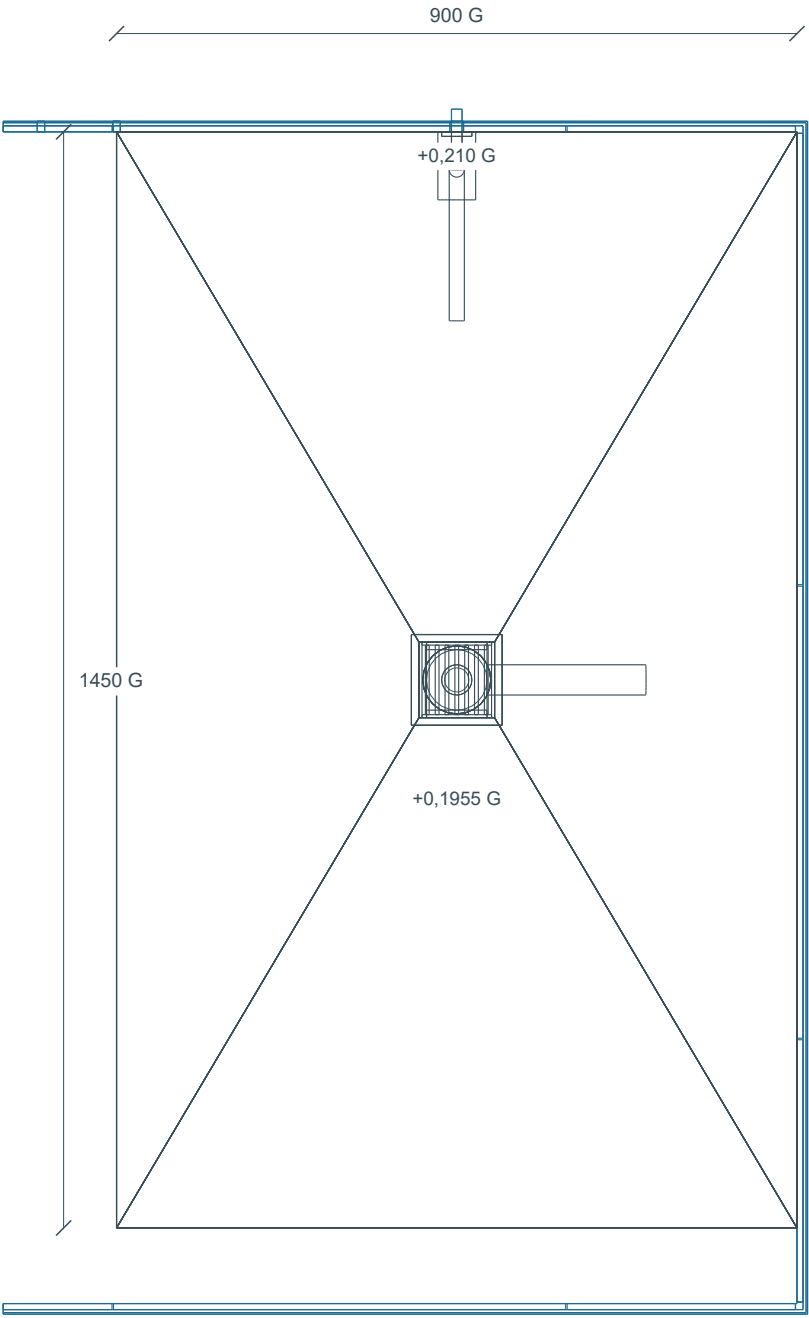


G ducha a piso: rejilla100x100 y caída14,5mm; pendientes2,15% /3,63% hasta el borde del desagüe.

24a Junta pasante / X21,35 | 1:1




P modulo600x300; juntas2x8 y esquinas2. Compatibilidad y ensayo de estanqueidad pendientes.

25 Ducha PB / X21,35 | 1:10

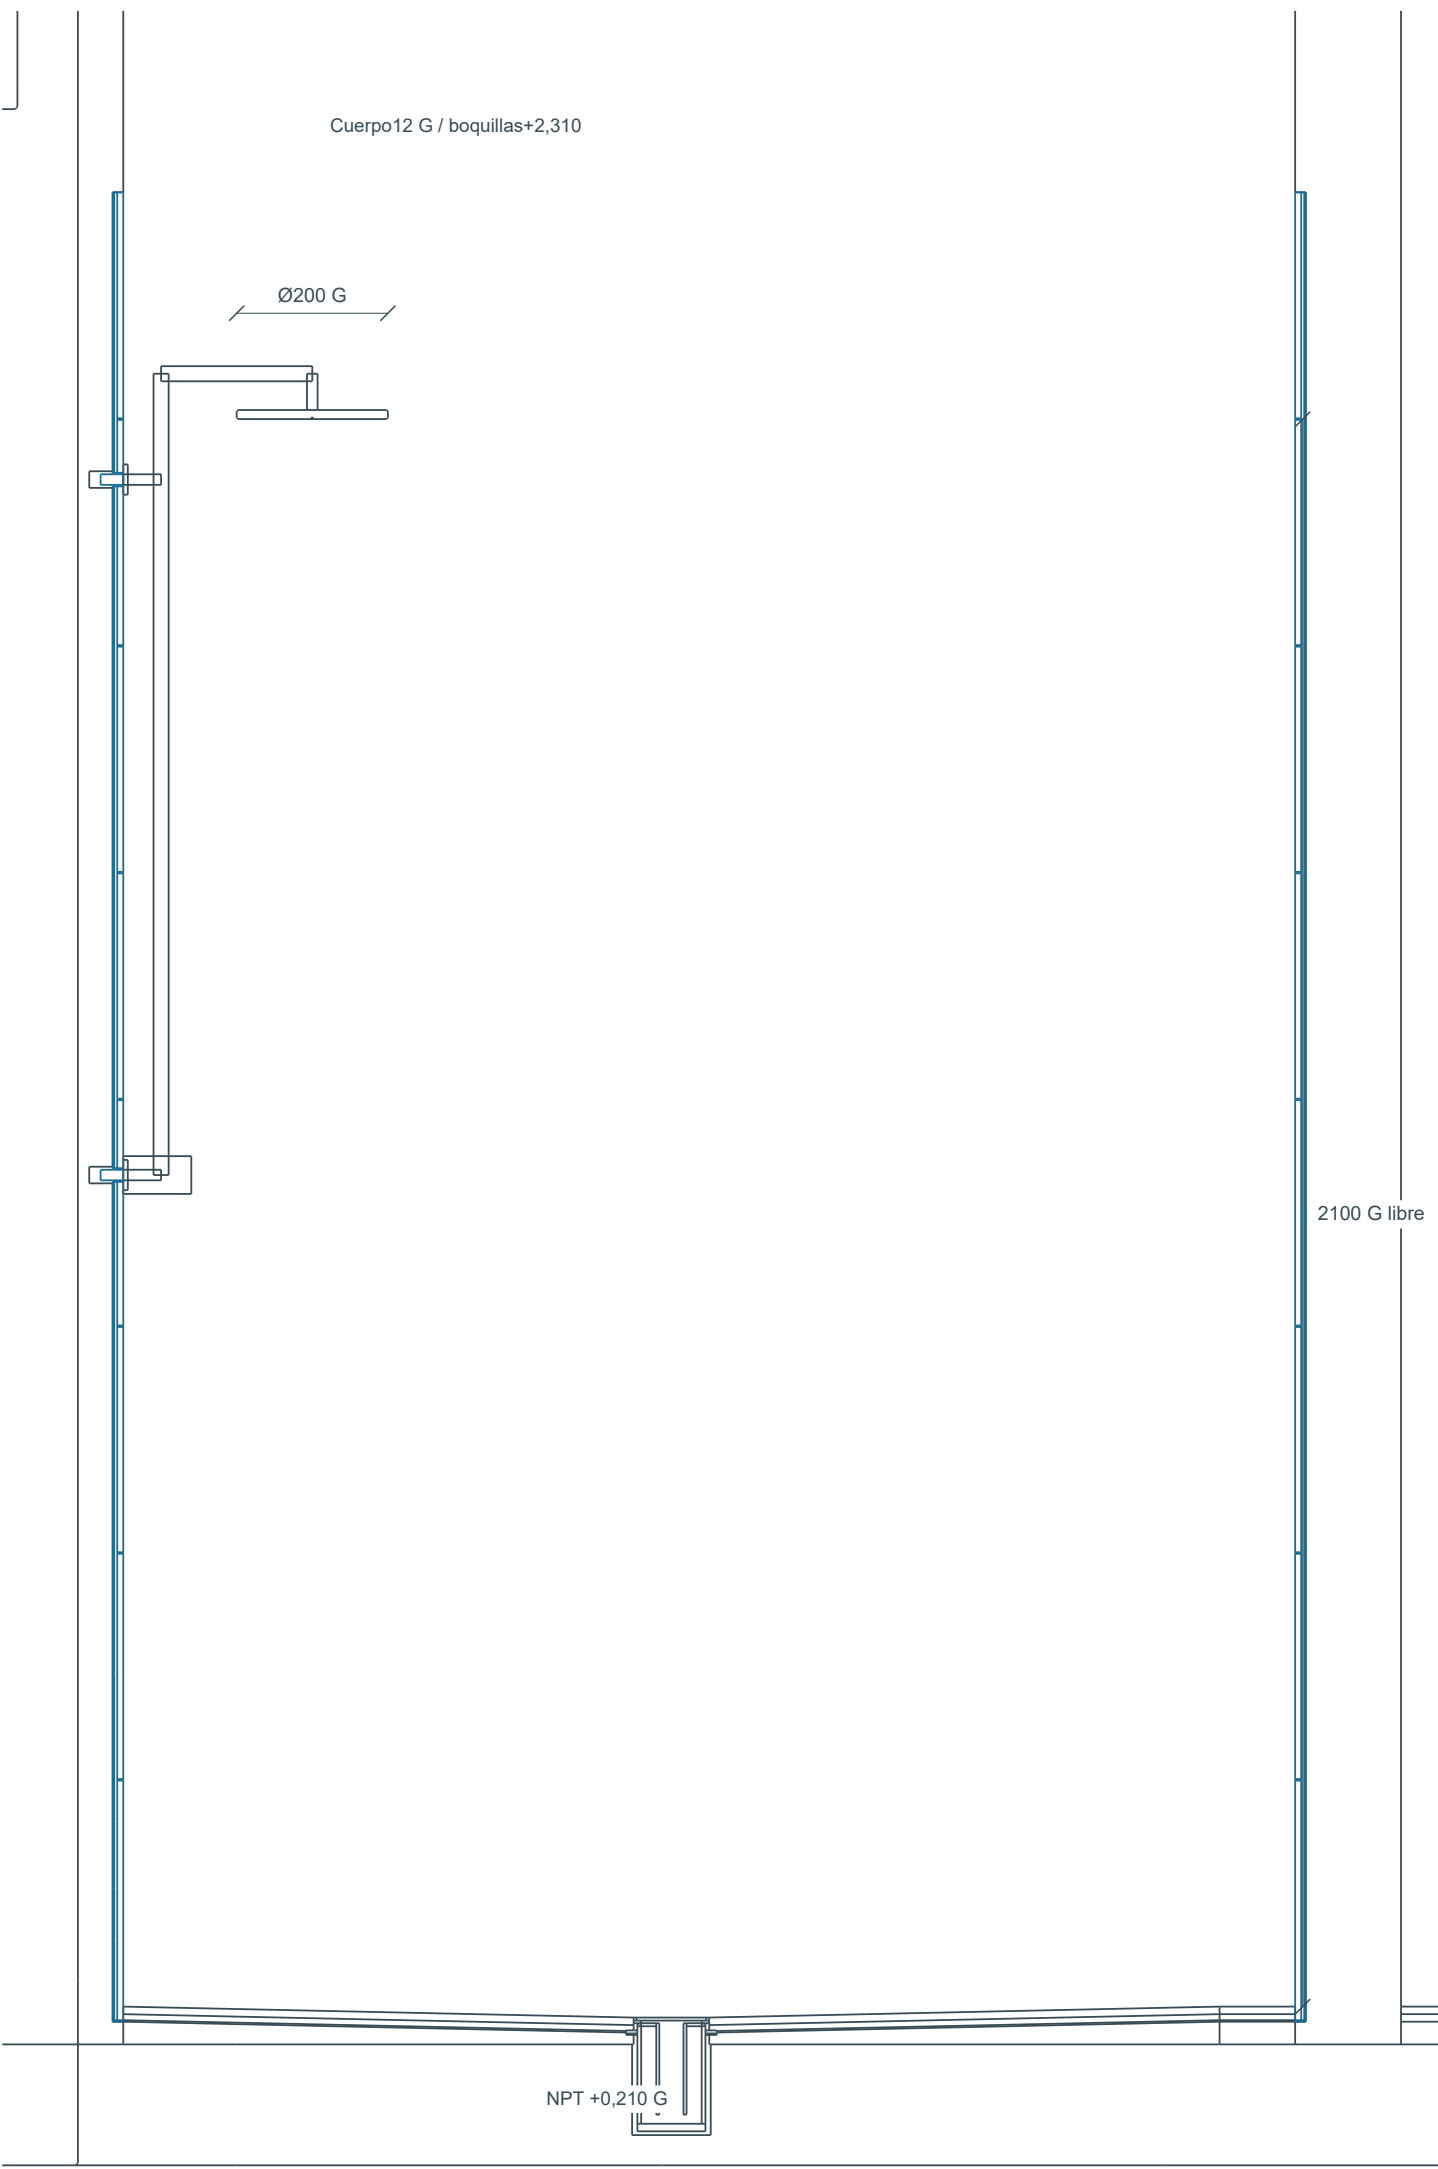


26 Griferia PA / X21,10 | 1:2

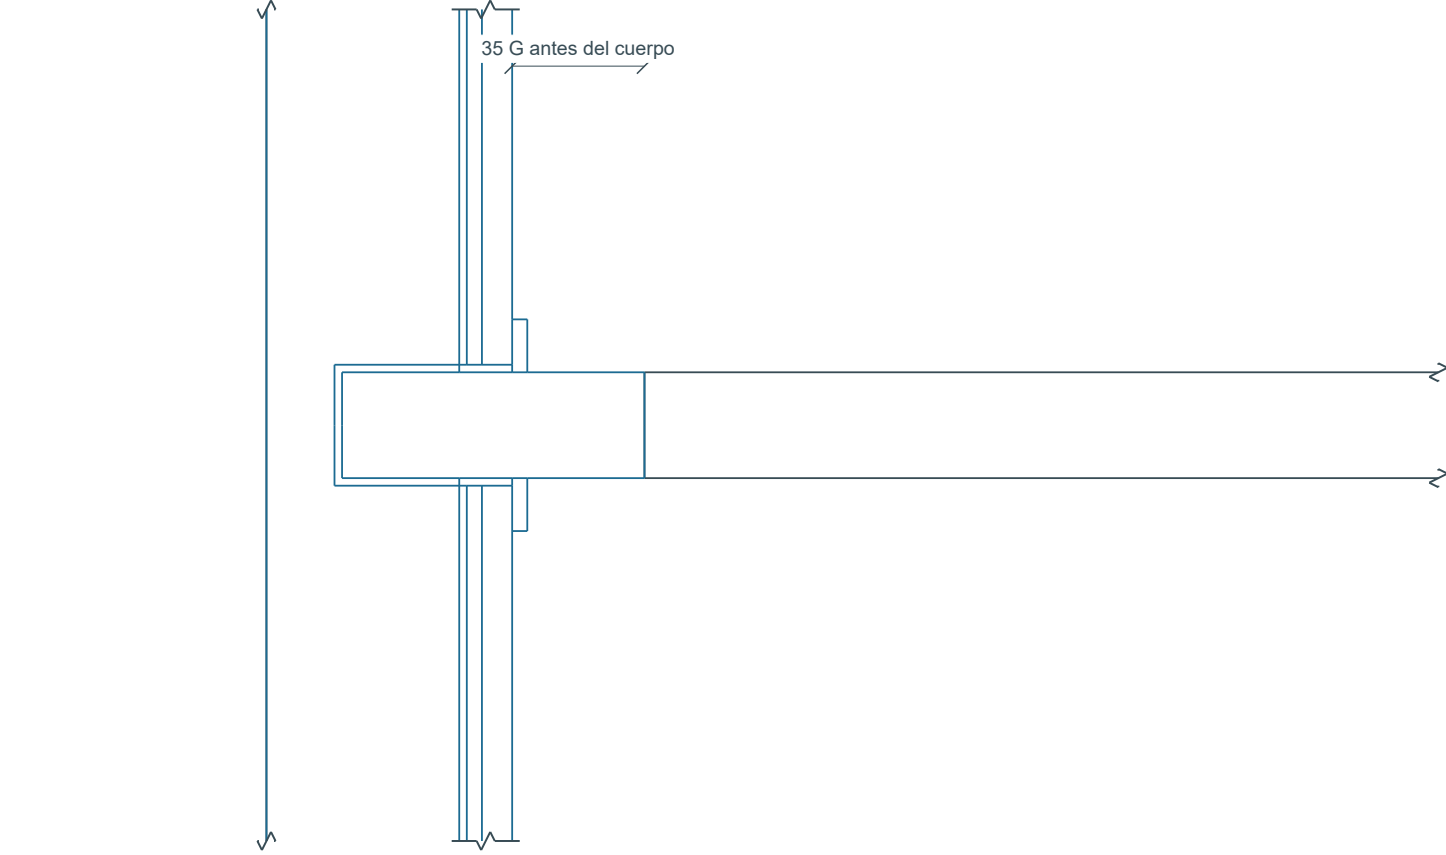


P vástago metálico hasta cuerpo empotrado, collar impermeable y roseta en cara terminada Z6,165; grifería conserva posición. Se conecta al sustrato, sin tubo flotante.

27 Piso-muro PB / Z1,40 | 1:2

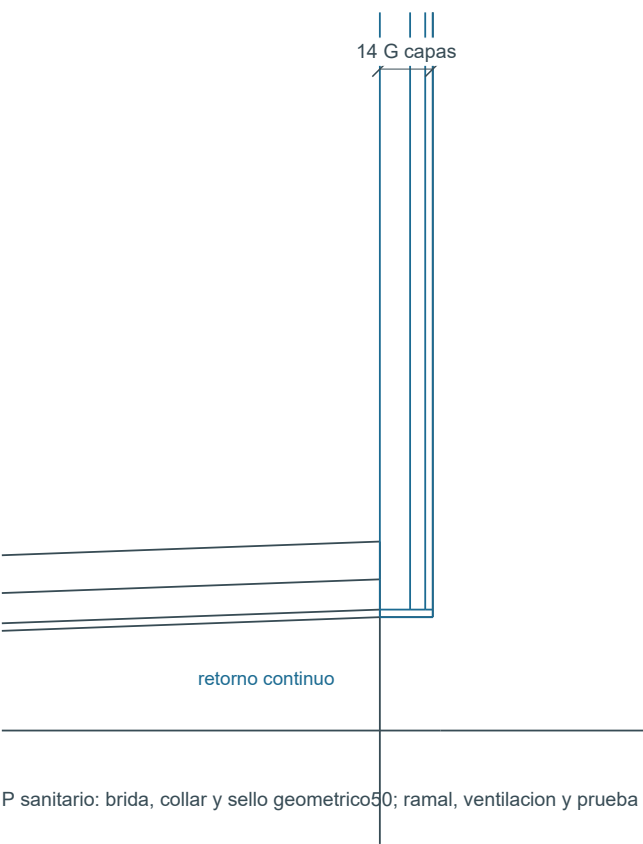

P sanitario: brida, collar y sello geométrico80; ramal, ventilación y prueba pendientes.

28 Sumidero PB / Z0,985 | 1:5

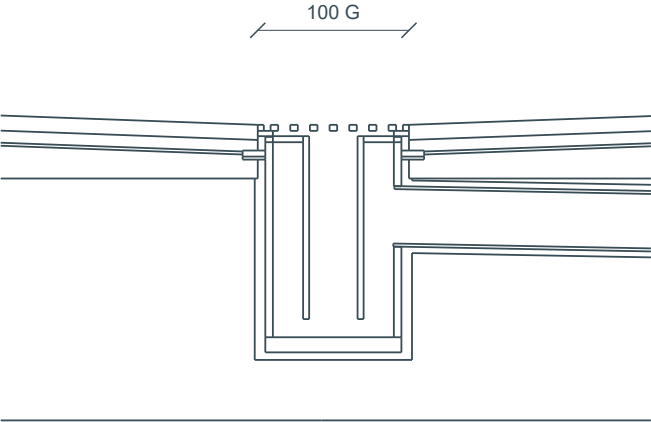


Todas las cotas en mm salvo niveles en m

COORDINACION DE USO

La evidencia de cuerpos y contactos corresponde a este SHA. No valida comodidad universal, resistencia ni producto comercial.




El montaje demuestra contacto y continuidad geometrica. No asigna capacidad, estabilidad, vibracion ni ajuste a todas las tallas.

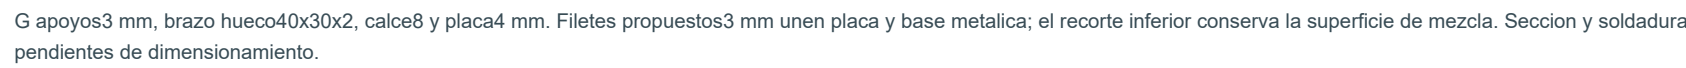

A2 / imprimir al 100 %

G = medido / gris P = propuesta dimensional / azul Todas las cotas en mm salvo niveles en m

29 Corte por plaza A / X16.35 | 1:10

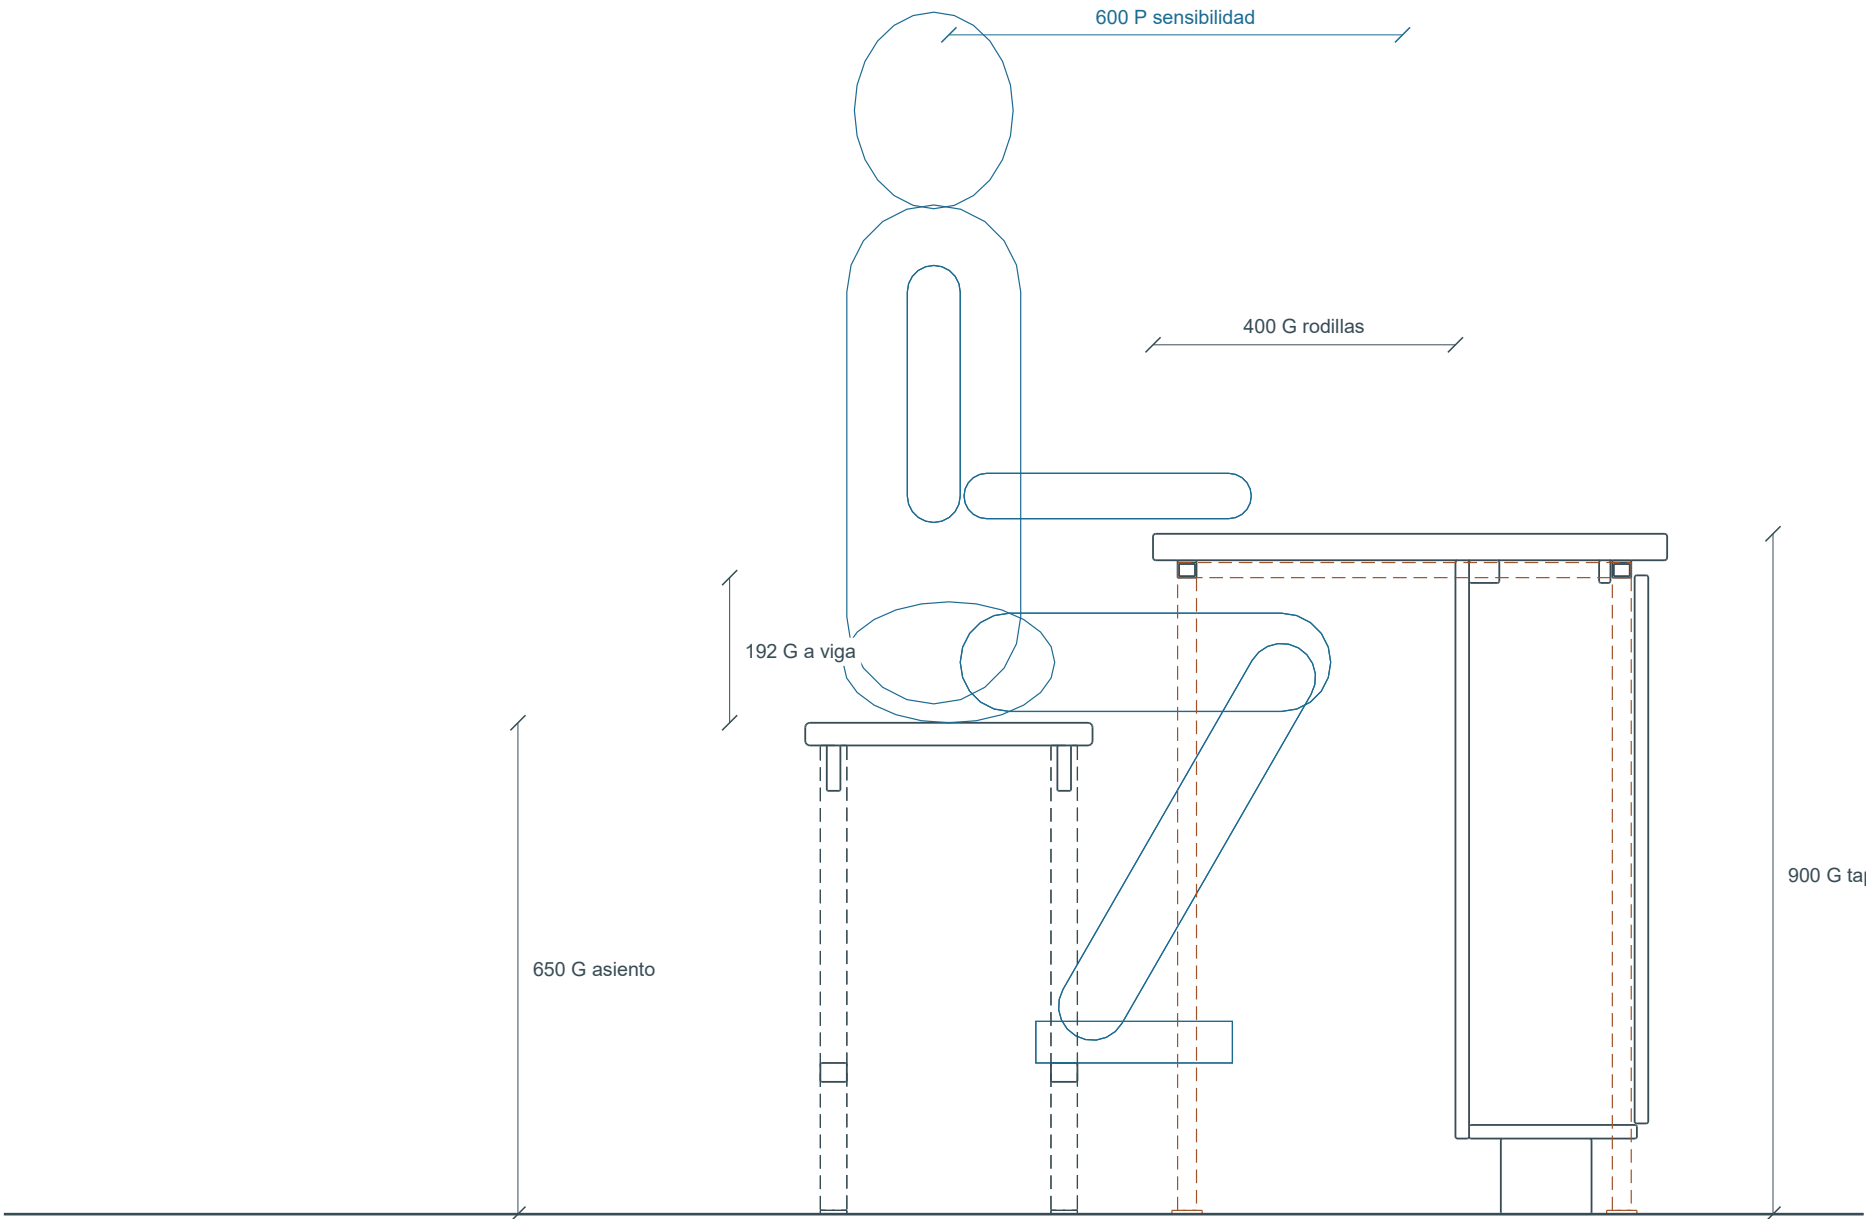

ESCENARIOS Y APOYOS

G patas fuera del corte: trazos grises. Ocre: portico lateral fuera de las bandas de rodilla. La tapa mantiene apoyos físicos hasta el piso.

P paso posterior con ambos comensales sentados. Retirada450 mm de cada taburete en21 poses, uno a la vez; acceso y salida en18 posiciones por el espacio central. Ocre en planta: asiento retirado, estado alternativo.

Los ensayos no simulan equilibrio, esfuerzo ni todos los gestos de sentarse. La referencia NKBA610x381 mm se toma como criterio de diseno, no como reglamento argentino.

U1 | NKBA Kitchen Planning Guidelines, Guideline9: seating

GEOMETRIA Y USO

G tapa 1720x680x35 mm; rodillas 400 mm. P dos bandas610 mm. Interior de almacenaje222 mm; pasillo de cocina conservado.

G taburetes: asiento 650 mm, huella380 mm y 305 mm entre patas delanteras. P cuerpos sentados con pies en travesanos; rodillas largas y recorridoØ450 mm comprobados para esta fuente.

G porticos25x25x2 y vigas25x20x2, elastomero3 mm bajo tapa. Resistencia, soldaduras y vinculacion requieren dimensionamiento; no se acredita capacidad.

30 Planta de huellas y maniobra / Cedro arriba | 1:20

