

LA PROPIEDAD COMPLETA, EN UNA MISMA VERSION

Plantas, fachadas, cortes y detalles extraídos del archivo Blender indicado en cada cartela. Las anotaciones distinguen fuente dimensional, geometría medida y propuestas pendientes.

Hoja	Contenido	Escala
A01	Implantacion, paisaje y perimetro	1:100 / 1:50
A02	Planta baja y vanos	1:50
A03	Planta alta, estudio y vivienda	1:50
A03b	Vivienda / uso y recorridos	1:25
A04	Cubiertas y coordinacion pluvial	1:50 / esquema
A05a / A05b	Cuatro fachadas	1:50
A06	Cortes generales A-A y B-B	1:50
A07	Escalera, descanso y acceso	1:20 / 1:5
A08	Pileta y bordes	1:25
A09	Banos: plantas y elevaciones	1:20 / 1:25
A10	Quincho y cocinas	1:25 / 1:50
A10b	Monoambiente: uso y cotas G	1:25 / 1:20
A11	Estudio y tratamiento acustico	1:25 / 1:50
A12	Carpinterias y herreria	Cuadros / 1:25
A13 / A13b	Encuentros de envolvente	1:5 / 1:10
A14	Estructura conceptual	1:50 / 1:10
A15	Instalaciones coordinadas	1:100 / esquemas
A16	Superficies, decisiones y trazabilidad	Cuadros
D01-D11	Suplemento G/P (incluye D05b)	1:1 a 1:50



COMO LEER ESTE JUEGO

- F - Fuente: cotas expresas del HTML original y decisiones del propietario.
- G - Geometria: medida derivada de la version Blender identificada por SHA256. No equivale a un relevamiento de obra.
- P - Propuesta: coordinacion o solucion grafica inferida. Validar antes de construir.
- Niveles referidos al cero del modelo. No hay relevamiento altimetrico ni mensura catastral.
- Ubicacion: Virrey del Pino, Partido de La Matanza, Buenos Aires. Norte orientativo segun propietario: con la calle arriba, abajo a la izquierda.
- Servicios de red disponibles segun propietario. Posiciones, cotas y condiciones exactas de acometida pendientes.
- Escalas fisicas para impresion al 100 %. DXF en metros; cada vista se separa horizontalmente en espacio modelo.

JERARQUIA GRAFICA

- 0,50 mm: contorno de piezas cortadas. Relleno gris: material seccionado.
- 0,18 / 0,13 mm: proyecciones, mobiliario y contexto.
- Azul: cotas, niveles, referencias y criterios de coordinacion.
- No constituye proyecto ejecutivo ni calculo estructural, sanitario, electrico o acustico.


01 Implantacion general | 1:100

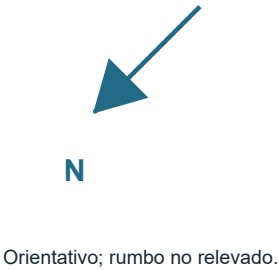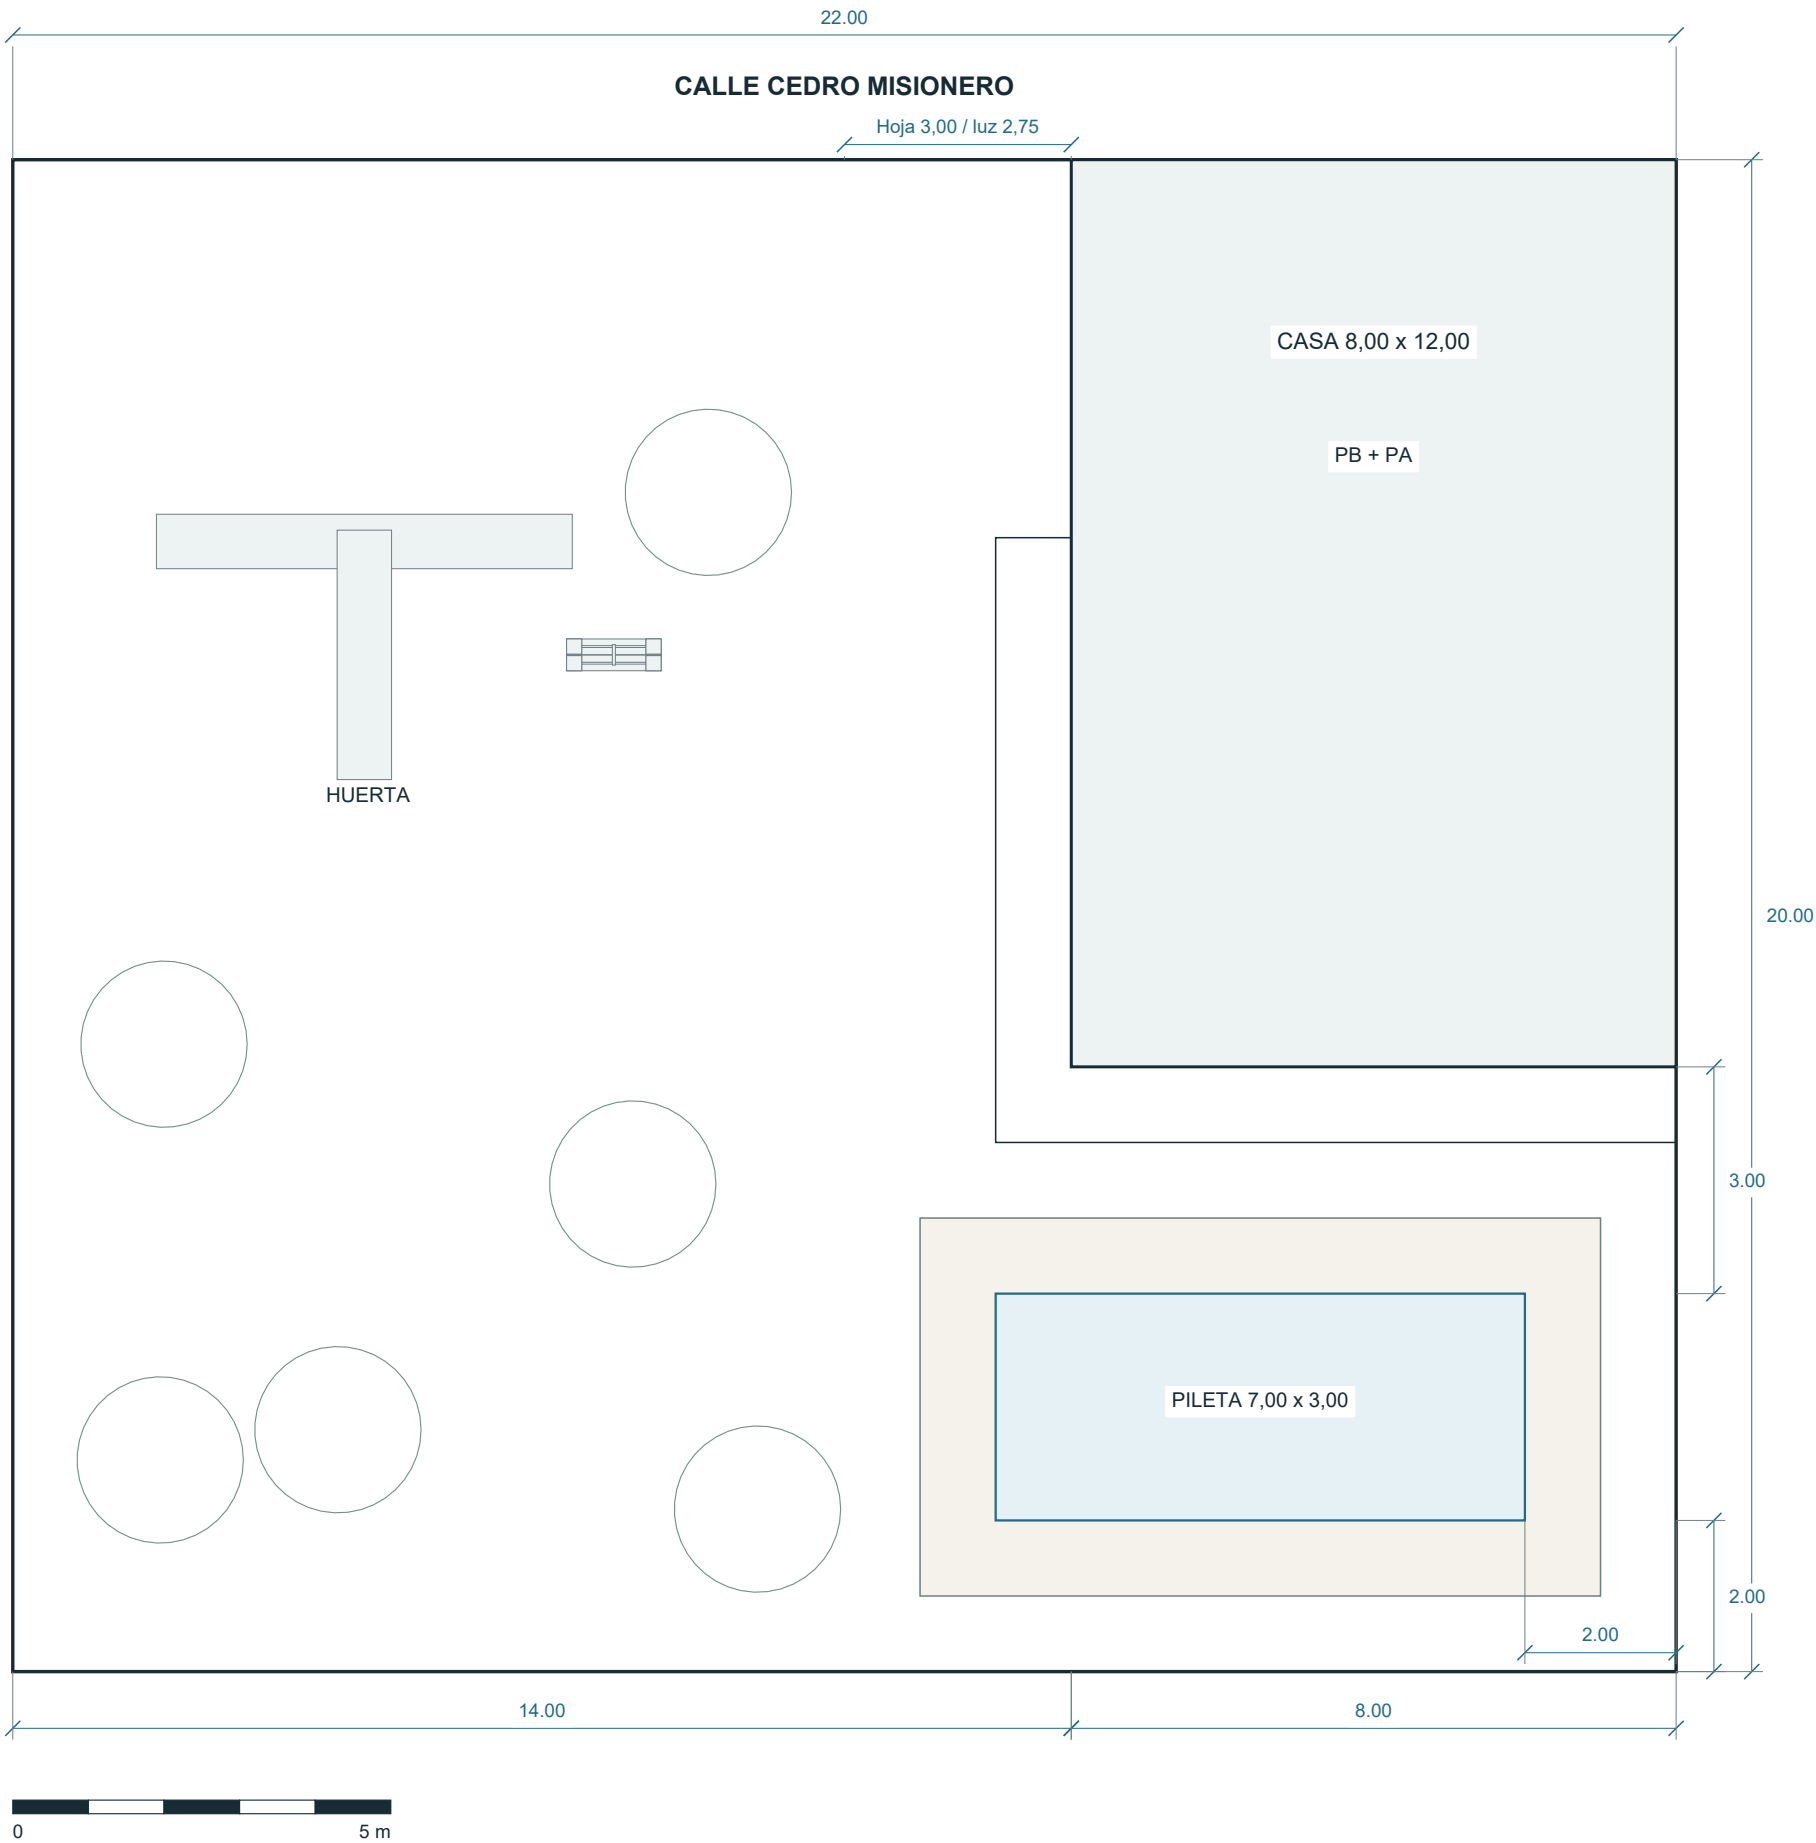

IMPLANTACION CONSERVADA


- F: lote nominal 22,00 x 20,00 m. Casa X=14,00; Z=0,00. Dos modulos de 6,00 m.
- F: pileta X=13,00; Z=15,00. Distancias nominales del vaso: 2,00 m al fondo y 2,00 m al lateral derecho.
- F: borde pavimentado de 1,00 m; huerta y centros de los seis arboles de fuente conservados.
- G: cotas de pavimentos se detallan en A02, A07 y A08. Rasante general del terreno por relevar.
- G: porton de hoja 3,00 m, luz entre pilares 2,75 m y carrera 3,05 m. No confundir hoja con paso libre.

02 Huerta y caminos | 1:50

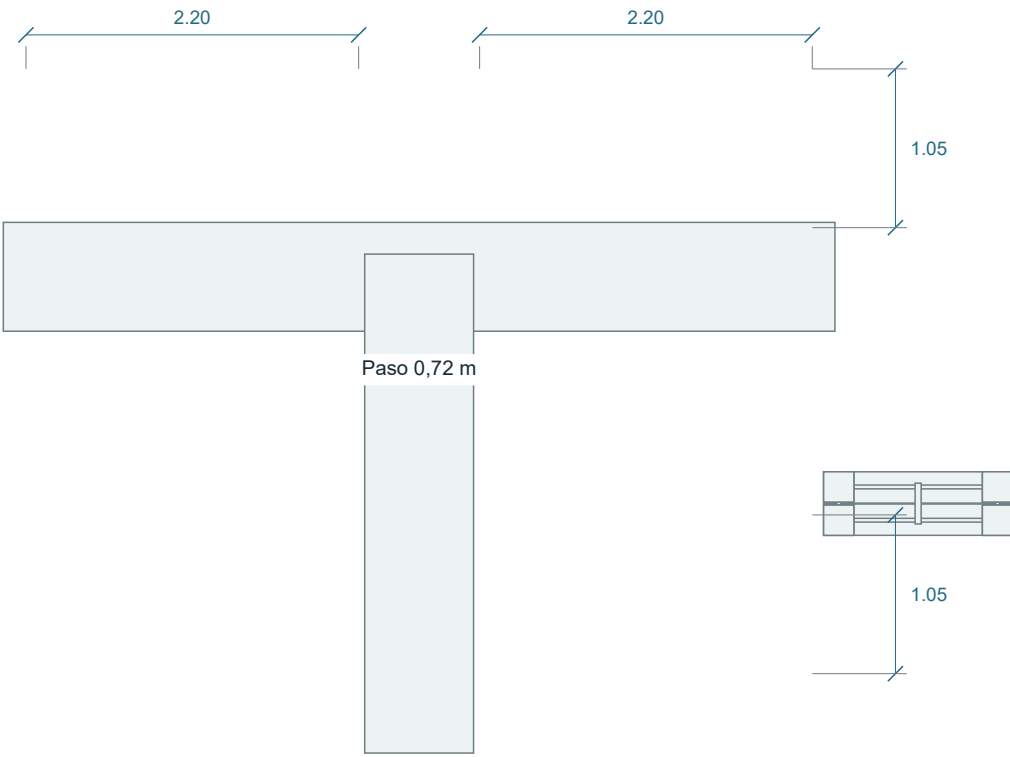

Perimetro y desniveles: confirmar mensura, cotas de terreno y drenajes exteriores. El norte grafico refleja la referencia del propietario y no un azimut topografico.

01 Planta baja amoblada | 1:50

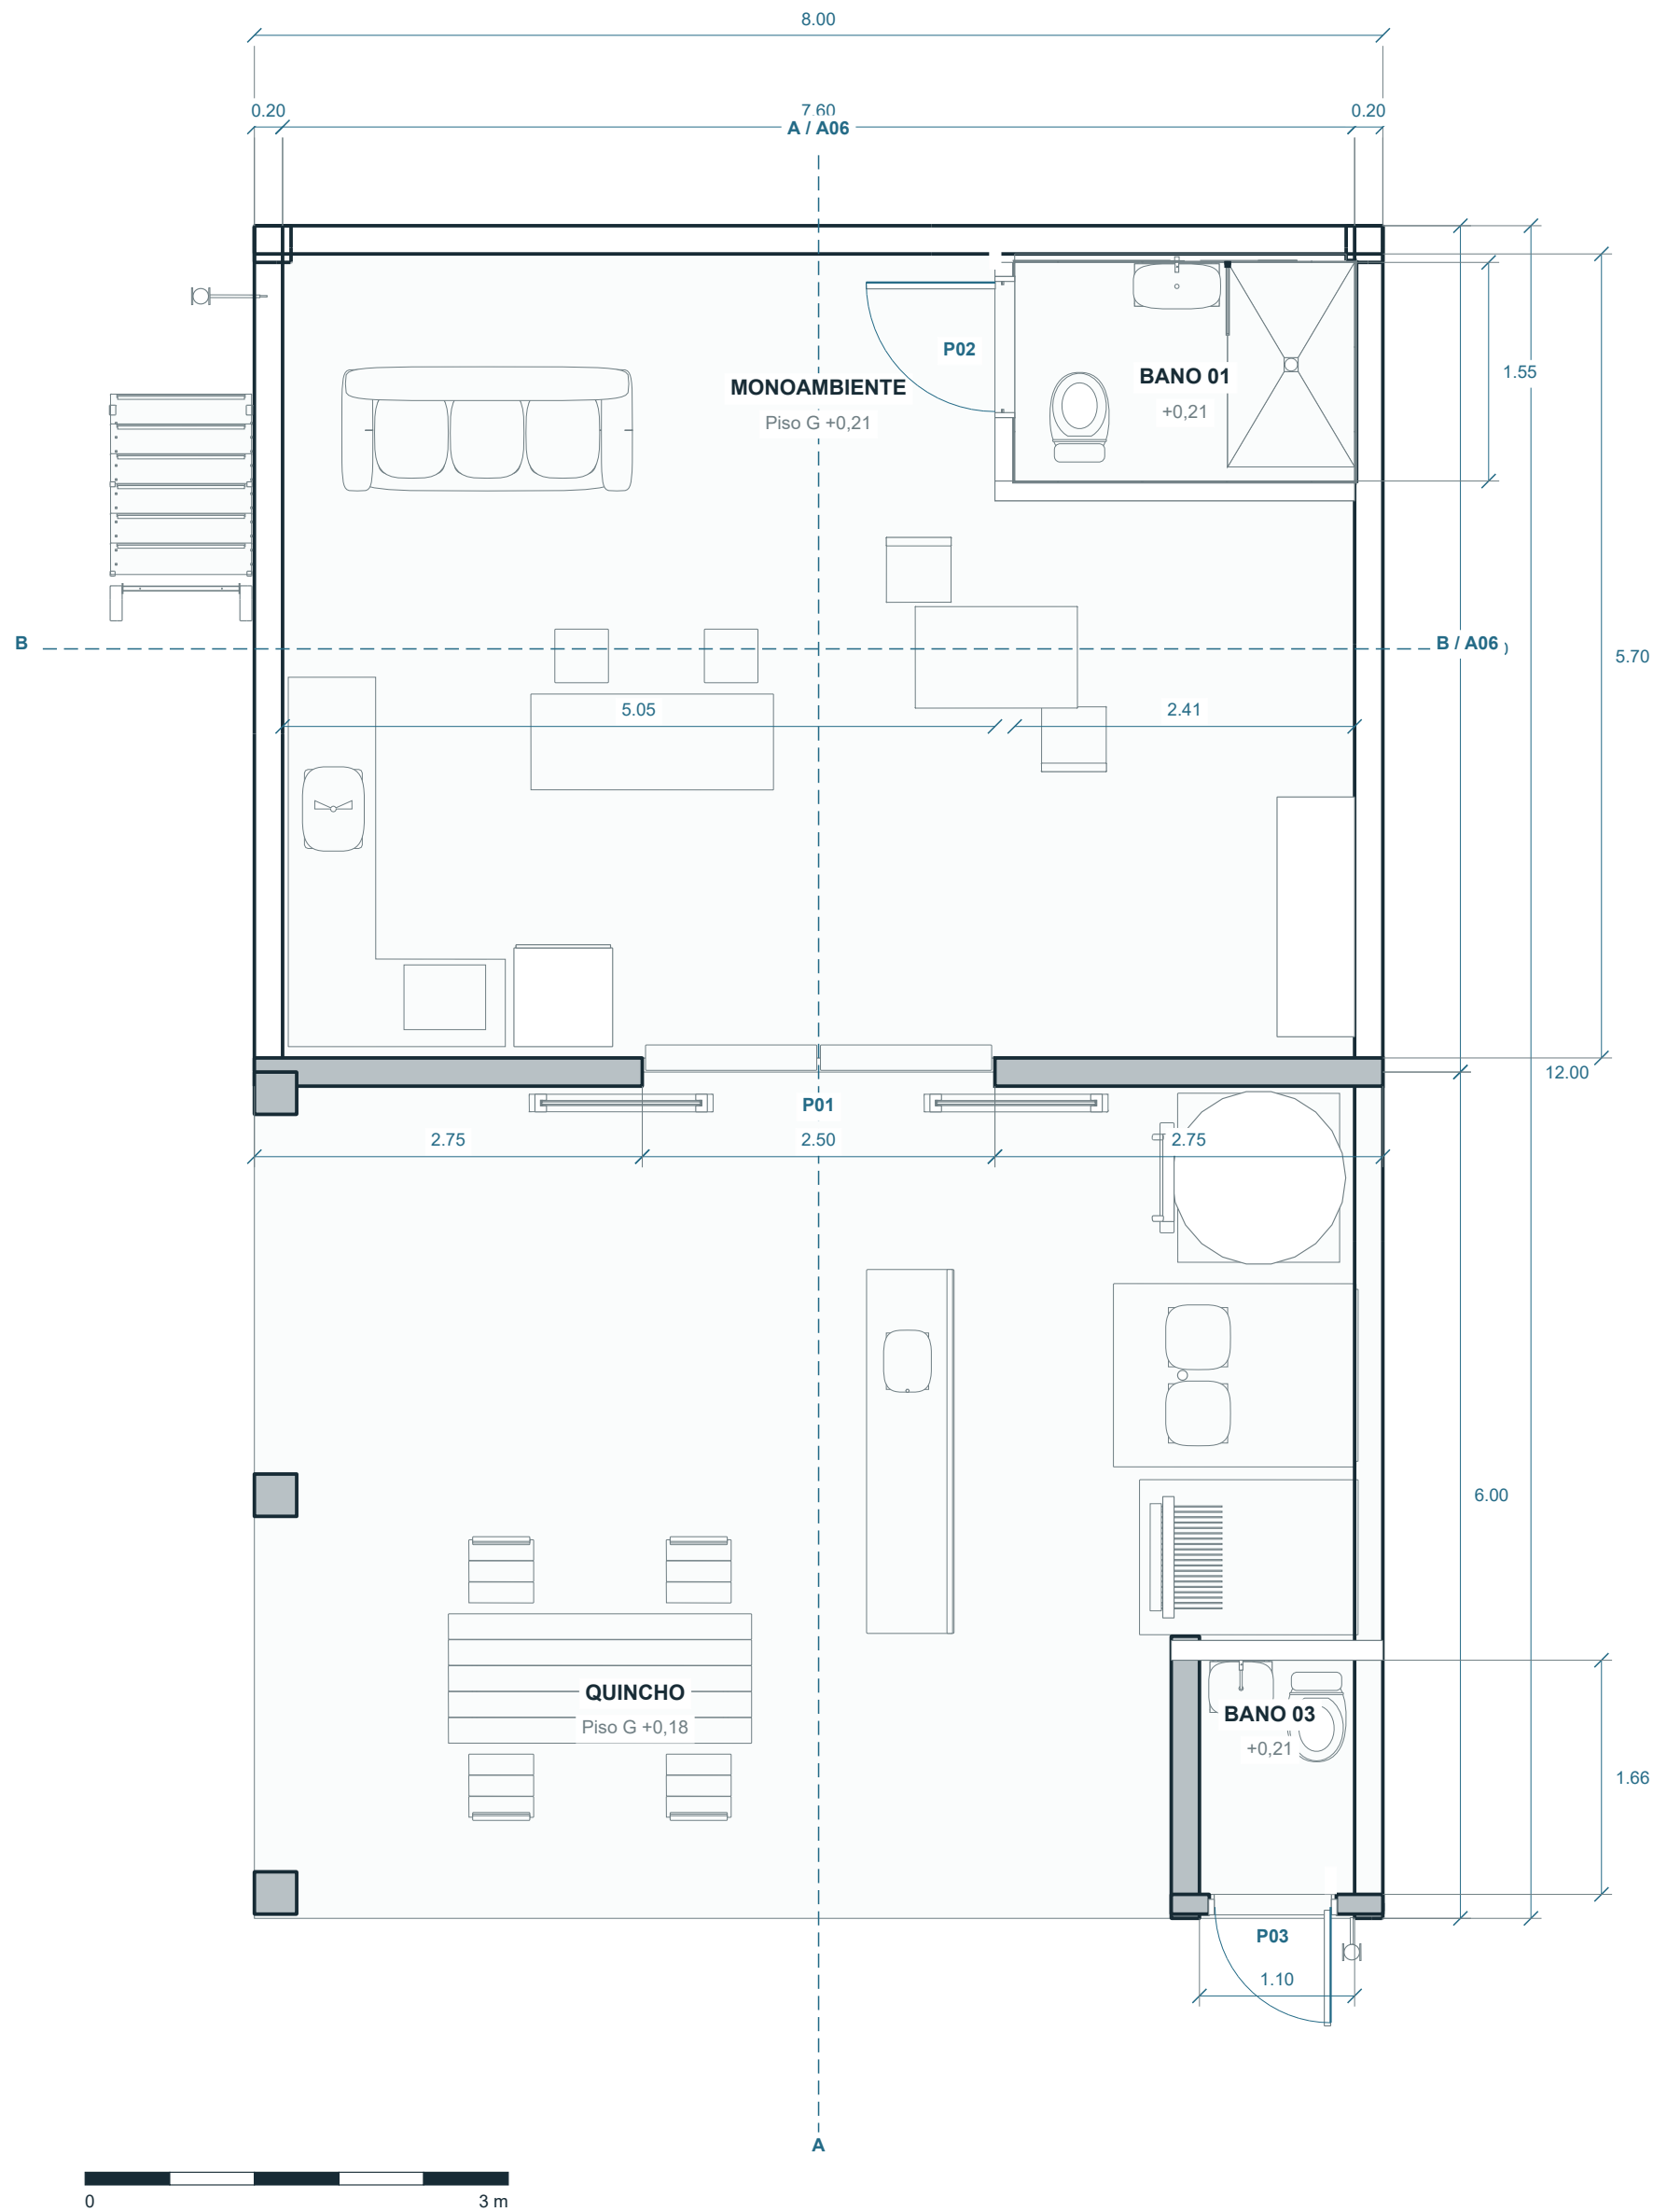

DIMENSIONES Y NIVELES


- F: envoltente nominal 8,00 x 12,00 m; espesor exterior 0,20 m. La geometría de piezas puede incluir juntas y salientes.
- G: piso monoambiente +0,21; quincho +0,18; ambos banos PB +0,21. Saltos entre acabados visibles: no se omiten.
- G: vano doble monoambiente 2,50 m entre jambas. Las hojas y rieles se describen en A12.
- G: baño mono en fachada Cedro y medianera: X19,39.21,80 / Z0,26..1,81. Luz entre acabados2,41 x1,55; tabique lateral0,14. Acceso por oeste.
- G: baño de pileta exterior con acceso desde jardín. Detalle acotado en A09.
- Barridos azules: pose de apertura esquemática de hojas; la ausencia de colision se audita en el modelo y no se presume por este símbolo.

LECTURA DE LOS EQUIPOS

- Cocina en L e isla del monoambiente: plantas y alturas de mesada en A10.
- Quincho: horno, bacha y parrilla mantienen la línea de fuente; extracciones independientes hacia patinillo. Ver A10 y A15.
- La circulación y los usos se muestran con el mobiliario actual. No se certifican accesibilidad ni condiciones reglamentarias locales.

Ref.	Ambito	Consultar
P01	Corredera PB	A12 carpinterías
P02 / P03	Banos PB / pileta	A09 locales
A-A / B-B	Secciones reales	A06 cortes generales

01 Planta alta amoblada | 1:50

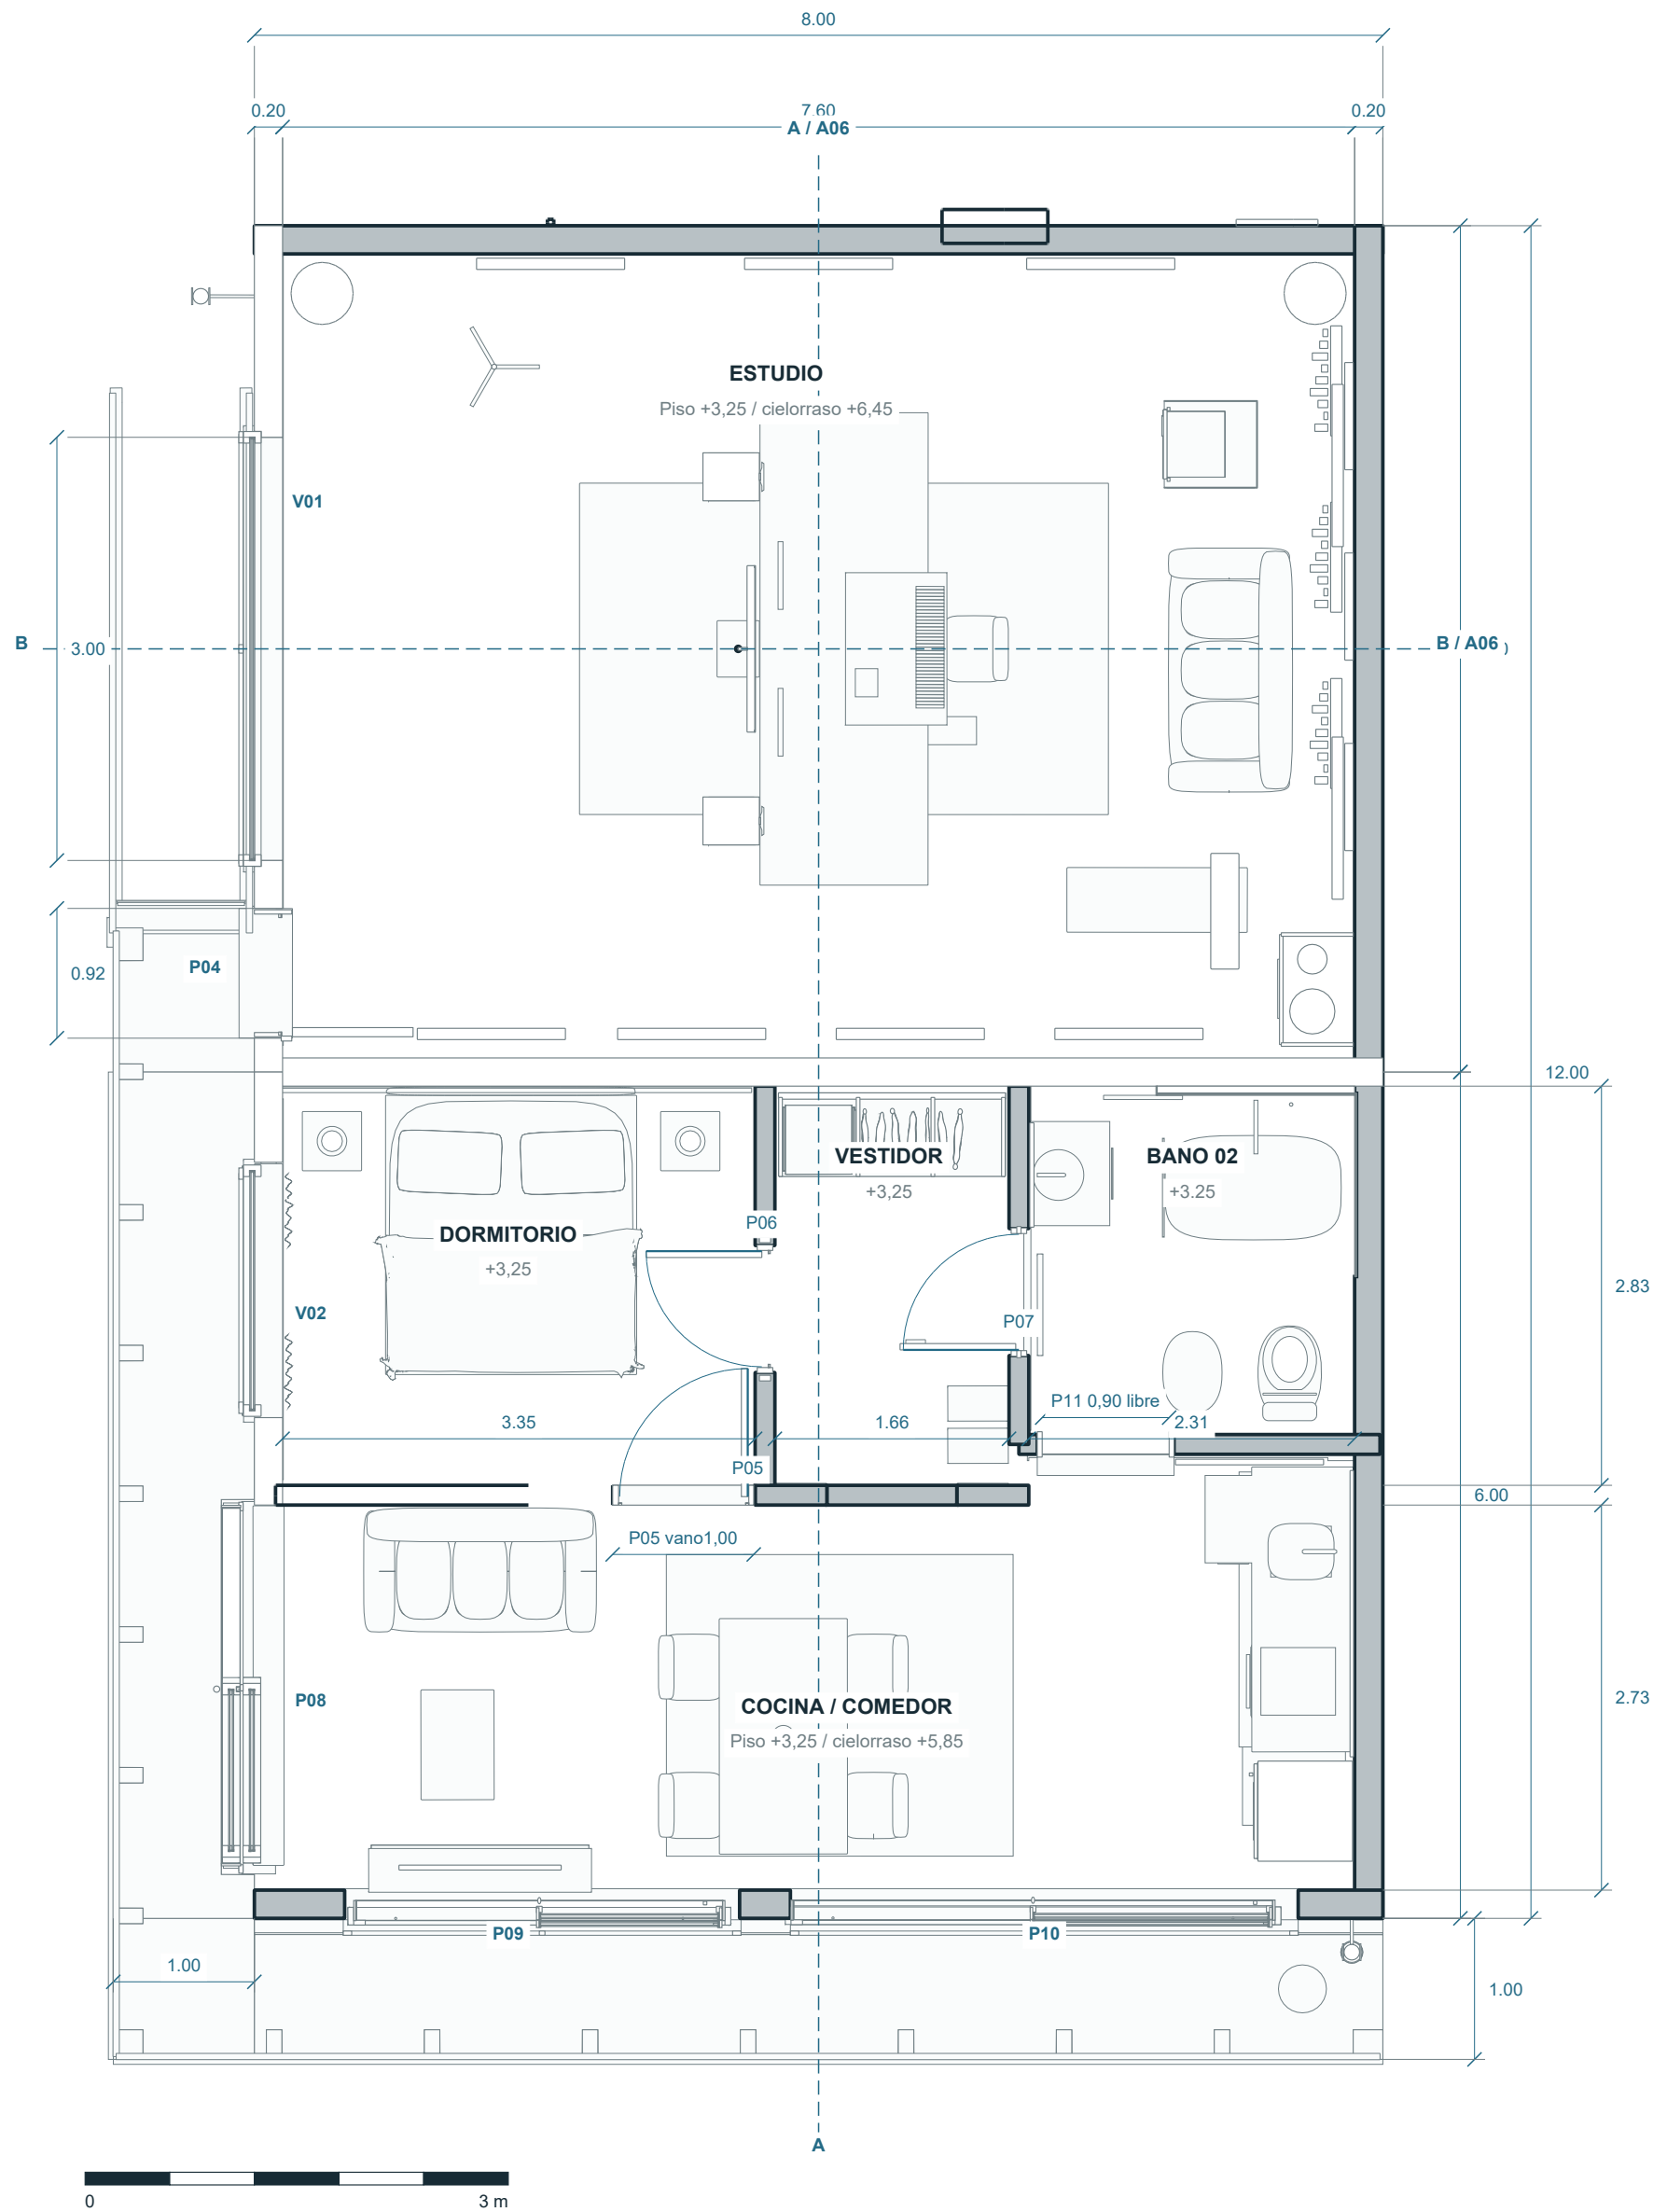

ALTURAS AUTORIZADAS

F/G: piso estudio +3,25; cara inferior del cielorraso +6,45 = 3,20 m libres.

F/G: piso vivienda +3,25; cielorraso general +5,85 = 2,60 m libres.

G: piso bano +3.25; cielorraso +5.85; altura libre 2.60 m. Transicion continua al comedor y corredora: suplemento D09.

G: losa entre plantas +3,00 a +3,20; espesor 0,20 m. Acabado general superior 0,05 m.

F: acceso exterior unico al nivel alto. Escalera y descanso 1,00 m nominal; detalle del umbral en A07.

CERRAMIENTOS Y VANOS


F: ventana del estudio 3,00 m. G: paños DVH y marco segun cuadro A12.

G: P05 conecta dormitorio con estar; P06 comunica dormitorio y vestidor; P07 vestidor y bano; P11 bano y comedor. Vestidor cerrado al estar.

G: balcon lateral 1,00 m y posterior 1,00 m nominal. Barandas y borde de losa en A12/A13.

Acustica, ventilacion y sellado: A11 y suplemento D06-D08. Prestaciones aun no calculadas.

01 Vivienda / accesos, mobiliario y huellas de uso | 1:25

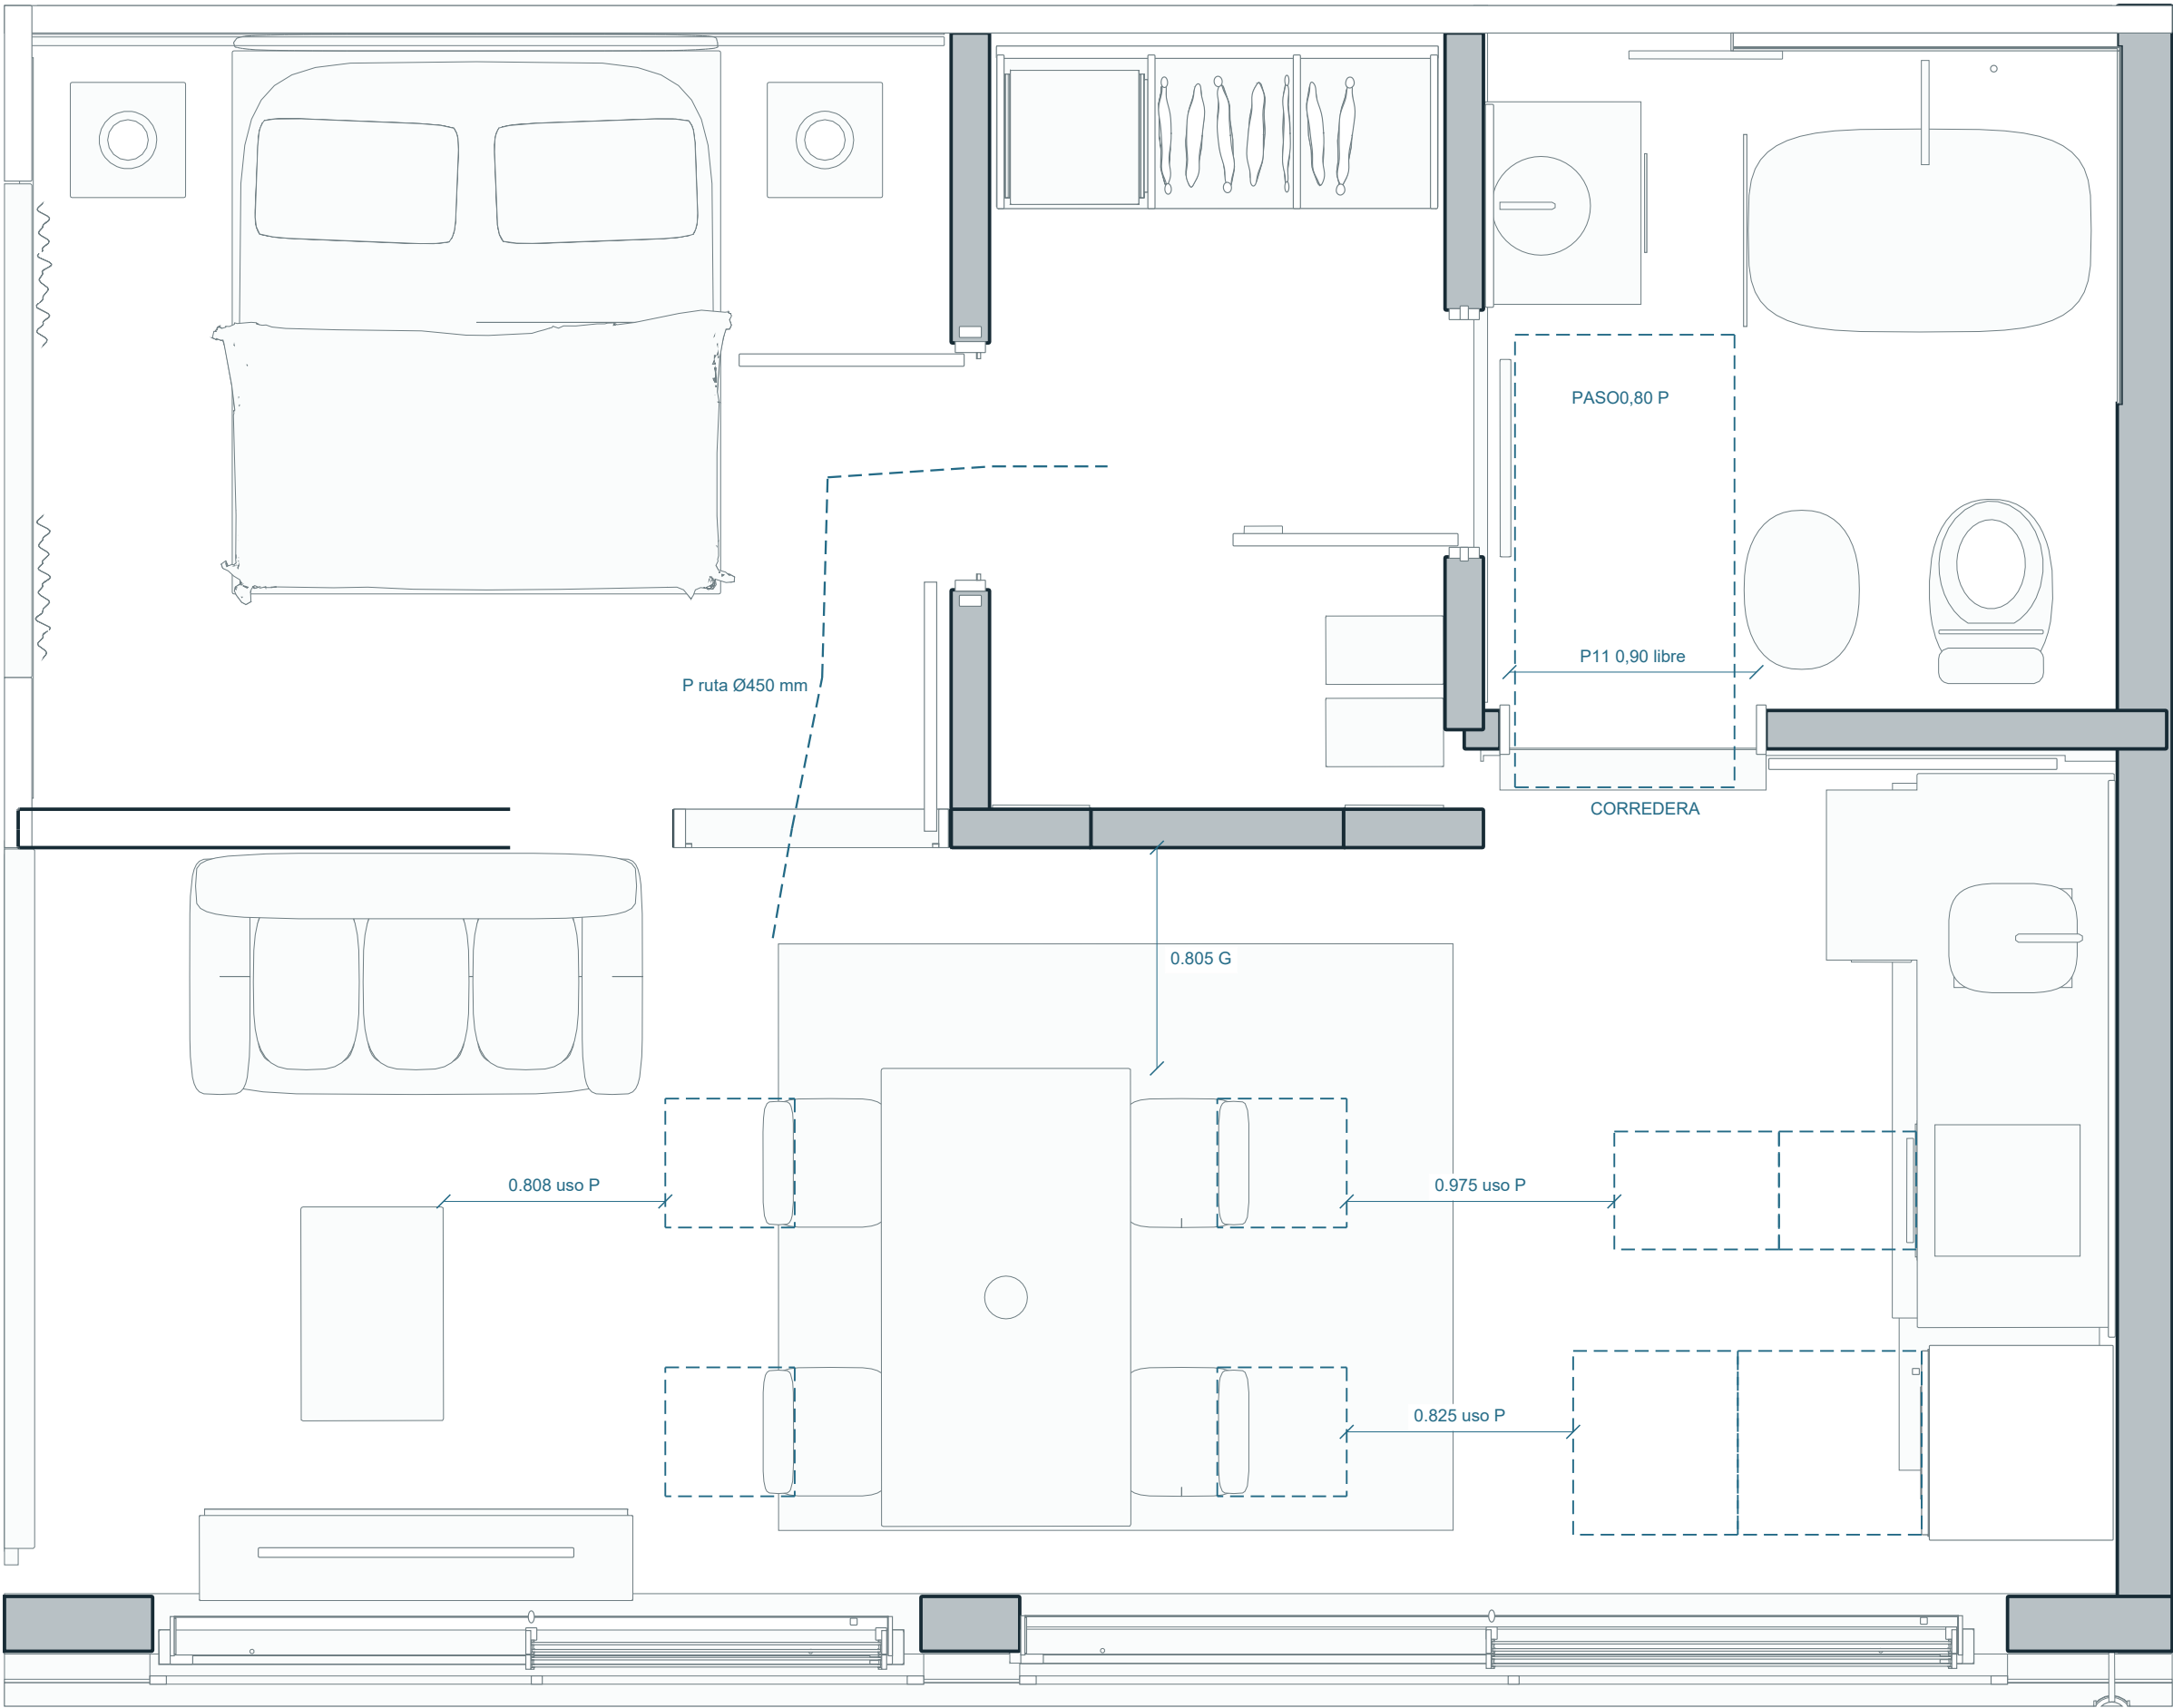

GEOMETRIA Y HUELLAS DE USO

G: muebles, mesadas y aparatos proceden del mismo modelo que esta cartela. Cotas a sus envolventes, no a centros.

P: cada silla se retira350 mm perpendicular al lado largo de la mesa. Se conserva su ancho y profundidad medidos.

P: profundidad de apertura de horno igual a altura de su frente; heladera igual a ancho de hoja. La abertura se dibuja como envolvente conservadora y requiere herraje real.

P: usuario de600 mm detras de hoja abierta. Estas huellas sirven para revisar simultaneidad; no acreditan accesibilidad normativa.

Caso simultaneo P	Paso m
Silla retirada / horno + usuario	0.975
Silla retirada / heladera + usuario	0.825
Silla oeste retirada / mesa baja	0.808

RECORRIDOS Y LECTURA


Estar -> dormitorio -> vestidor -> bano; P05 y P06 abren hacia dormitorio. P11 bano-comedor conservado; vestidor cerrado al estar.

G P05: paso conservador806mm: galce X16.6045 hasta manija X17.4105, hoja90°. Proyeccion sobre toda la profundidad de hoja; garganta848mm. A12.

Si muebles o herrajes cambian, recalcular estas envolventes; la ausencia de choque no sustituye la prueba de uso.

NPT vivienda y baño continuo +3,25. Se verifican trayectorias y espacios de uso como propuestas dimensionales; la evaluacion de confort y las aperturas finales se confirman sobre la nueva escena y los herrajes elegidos.

01 Cubiertas y captacion | 1:50

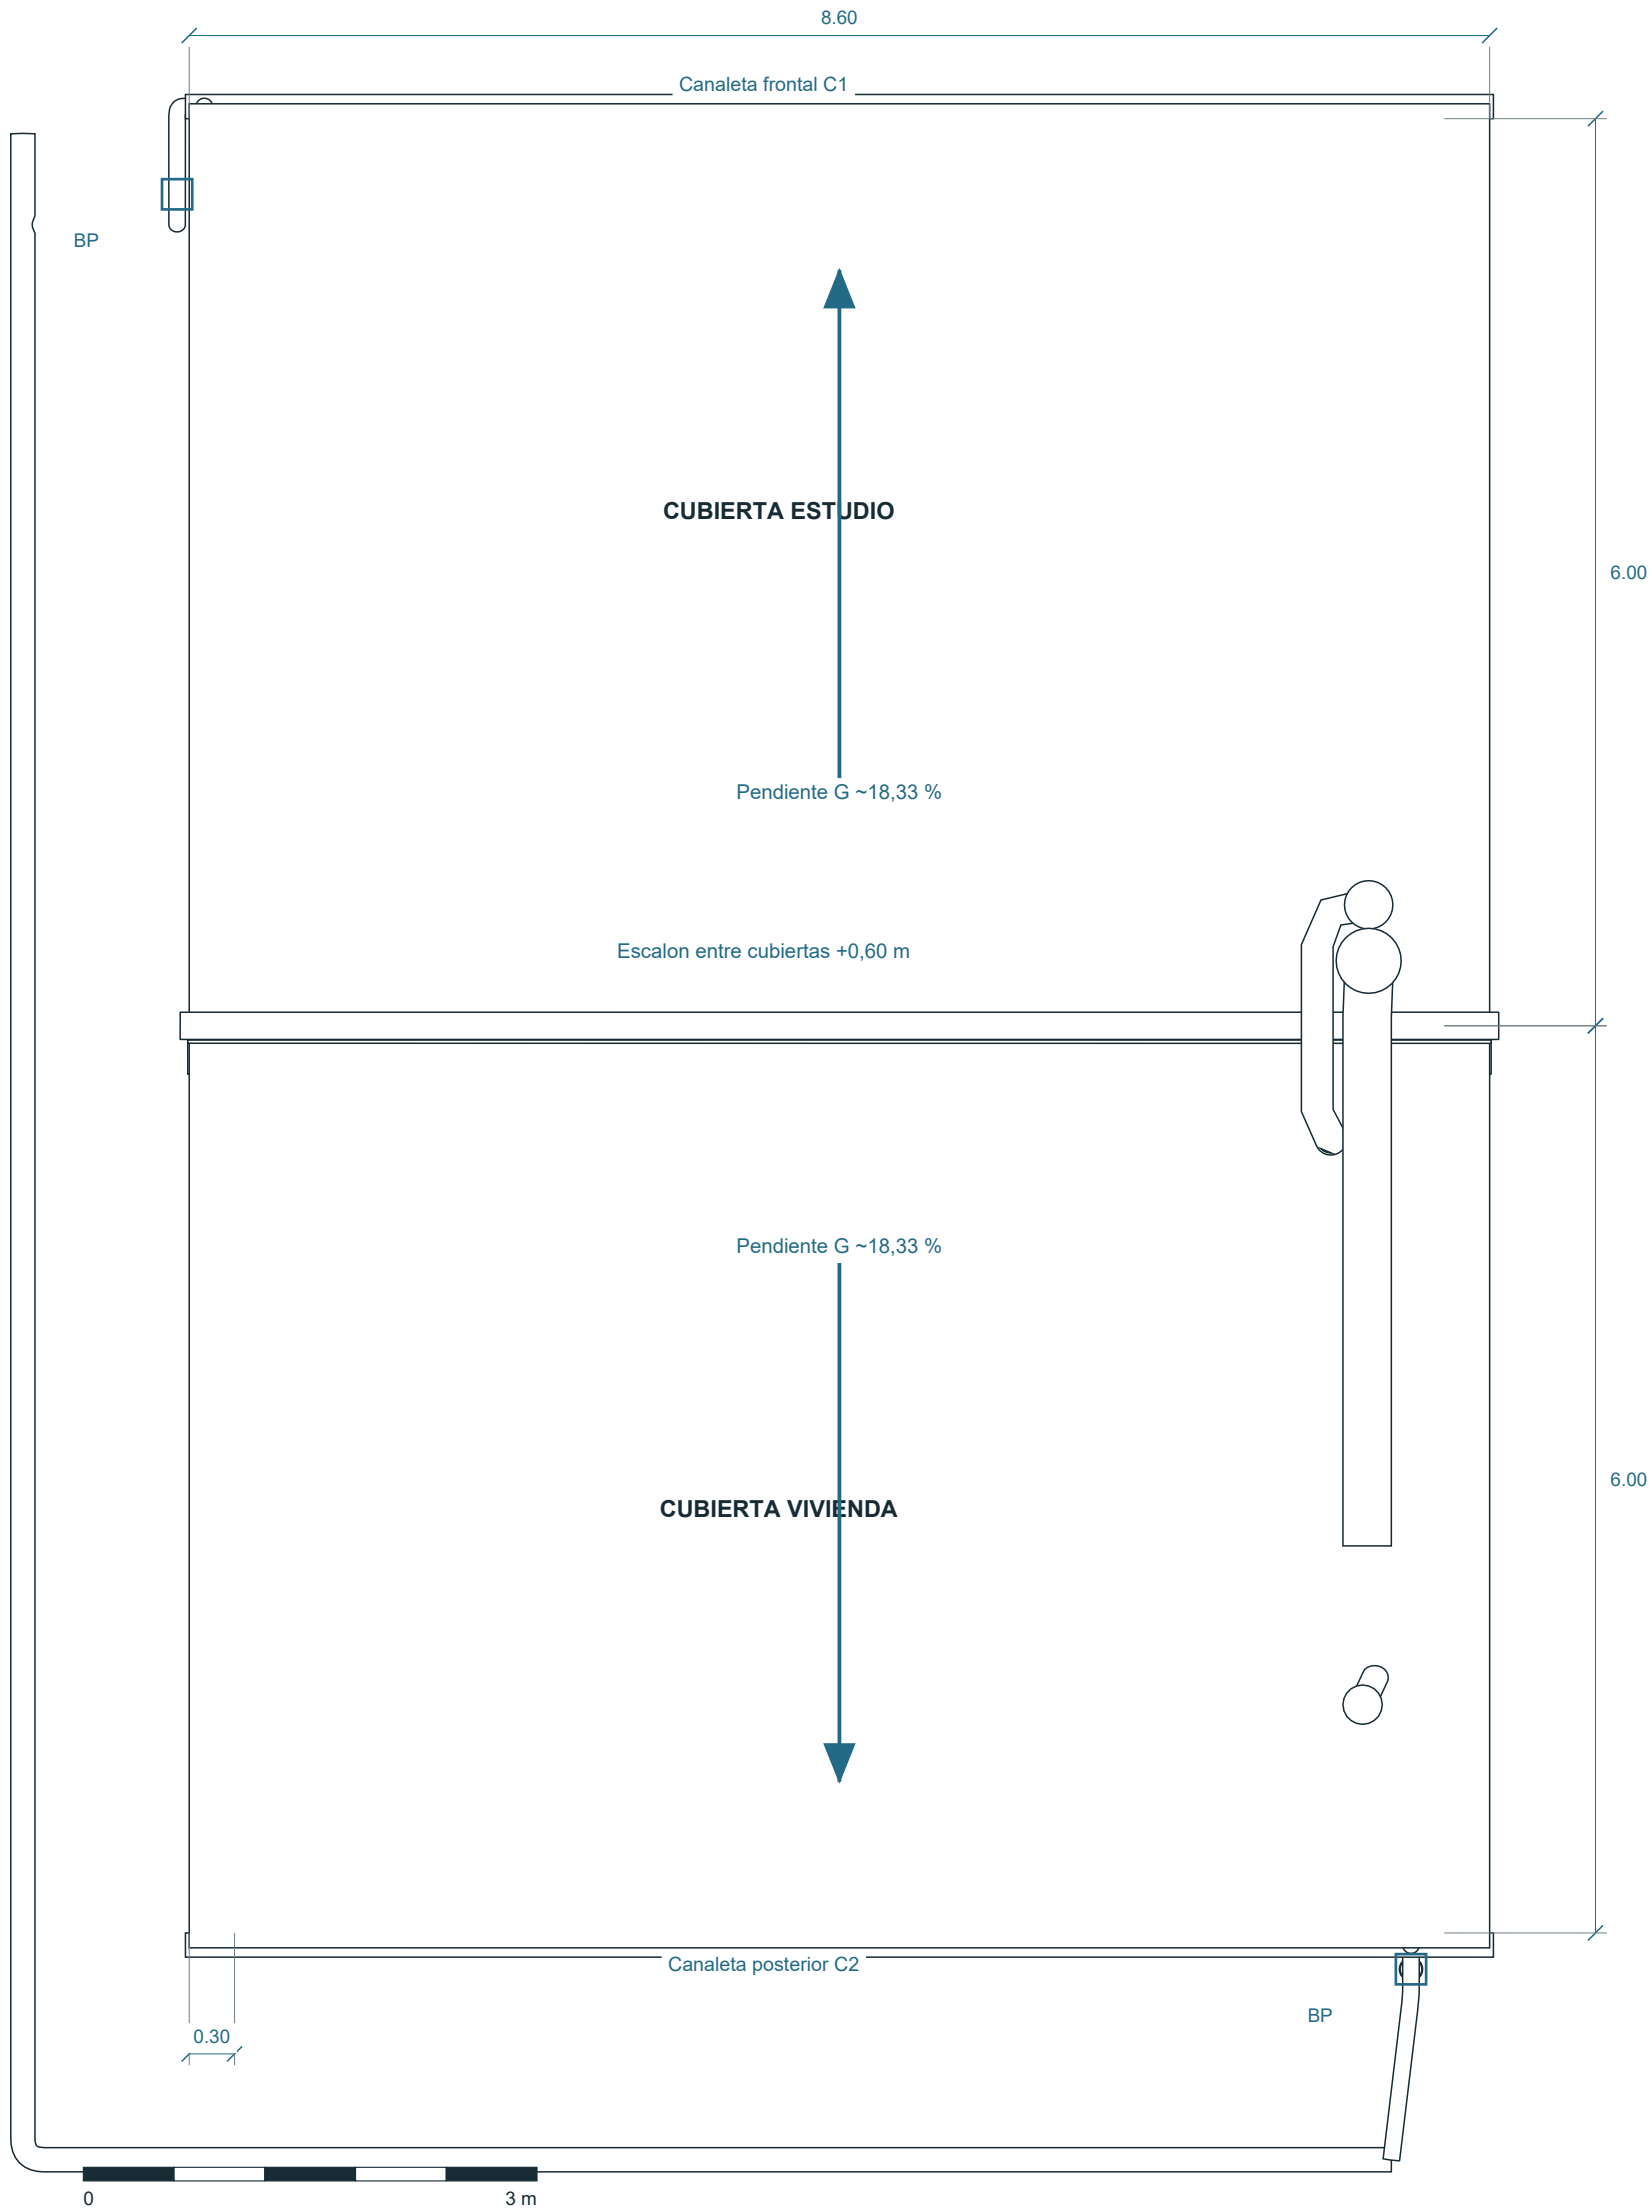

CONTINUIDAD DEL AGUA

G: pendientes principales conservadas, 1,10 m de subida en 6,00 m de desarrollo horizontal nominal (18,33 %). No es una pendiente pluvial de canería.


G: estudio elevado 0,60 m respecto de la cubierta de vivienda. Alero lateral nominal 0,30 m.

Captacion: revisar seccion abierta, embudo, codo y abrazaderas en el modelo de esta emision. El corte de abajo reproduce sus piezas reales.

P: conduccion de descarga hasta punto de red pluvial propuesto. Conexion, cota, caudal y diametros finales pendientes de datos de servicio y calculo.

No se presume que una bajada dibujada llega a una red existente. A15 identifica el limite de coordinacion.

02 Circuito frontal / proyeccion | 1:50

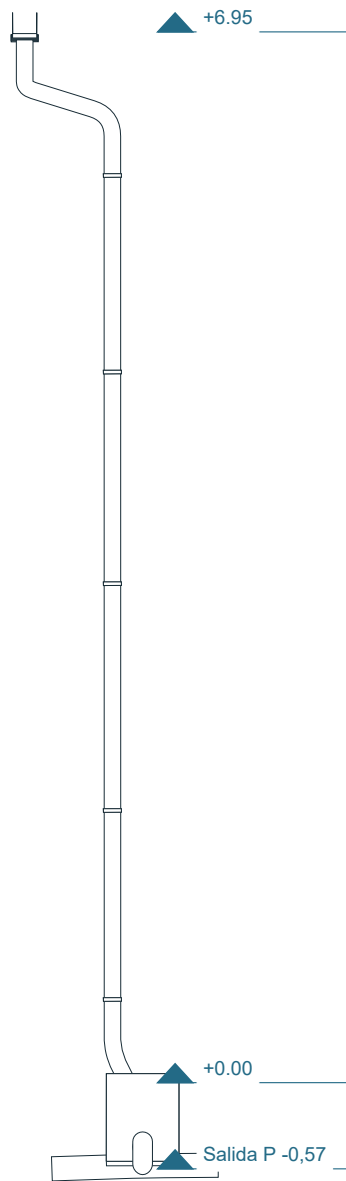


PUNTOS DE CONTROL

1. Cubierta hacia canaleta receptora.
2. Fondo de canaleta hacia salida.
3. Conexion estancia entre piezas.
4. Bajada continua y registrable.
5. Descarga con destino definido.

La continuidad fisica y la prueba de paso se documentan en la auditoria del modelo.

01 Frente / Cedro Misionero | 1:50

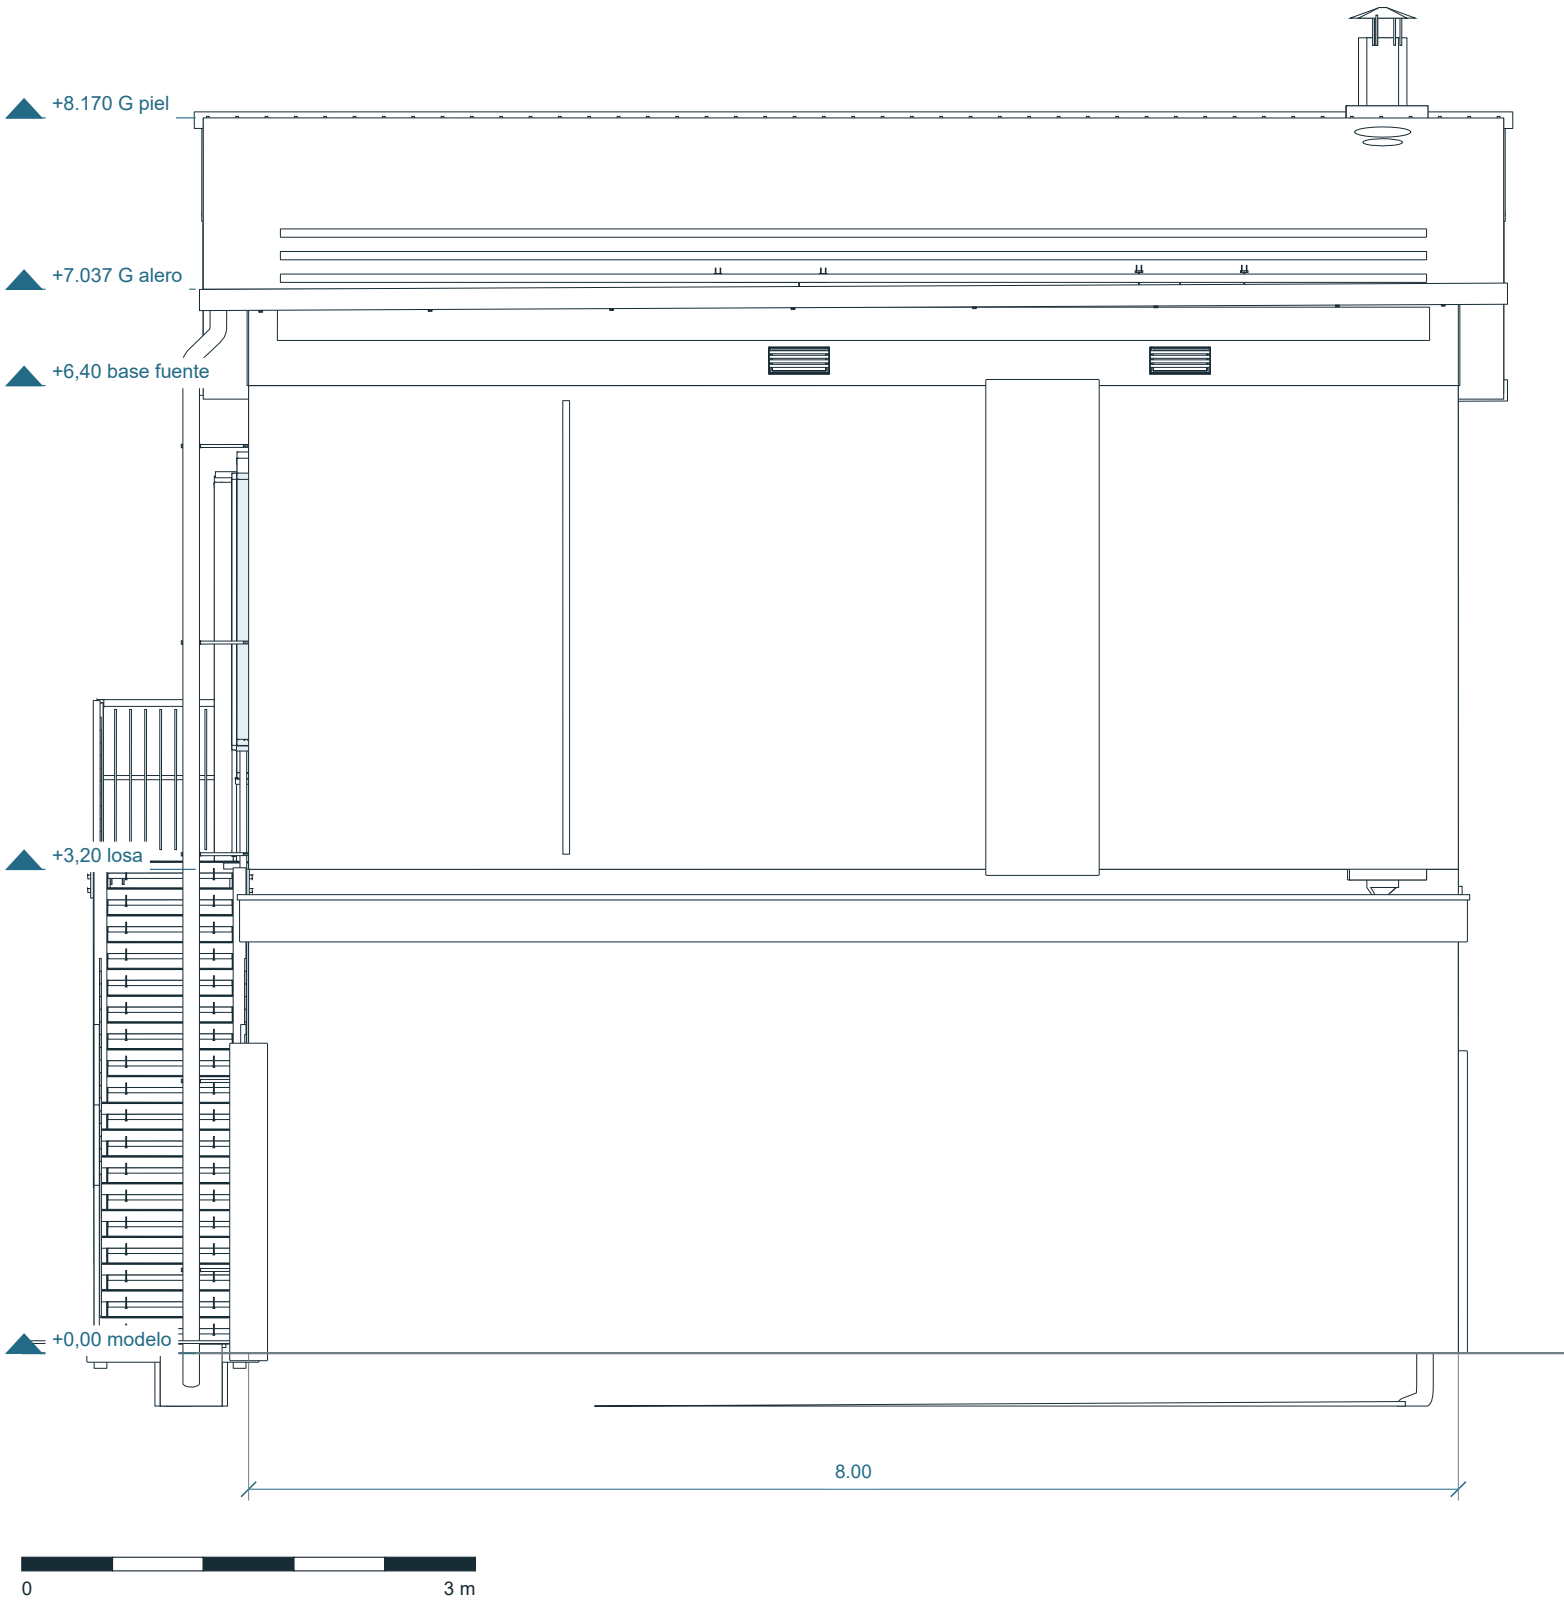

MATERIALIDAD REPRESENTADA


Ladrillo visto en cerramientos; hormigon en losas, pilares y vigas; cubierta metalica con encuentros y remates; DVH en carpinterias; herreria en balcones y escalera.

G cotas de piel exterior de cubierta extraidas de malla. F+7,00/+8,10 son referencias de fuente y no coronamiento terminado. A12/A13 y suplemento amplian hojas, capas y fijaciones; sin despiece certificado.


02 Contrafrente / pileta | 1:50



03 Lateral de acceso | 1:50

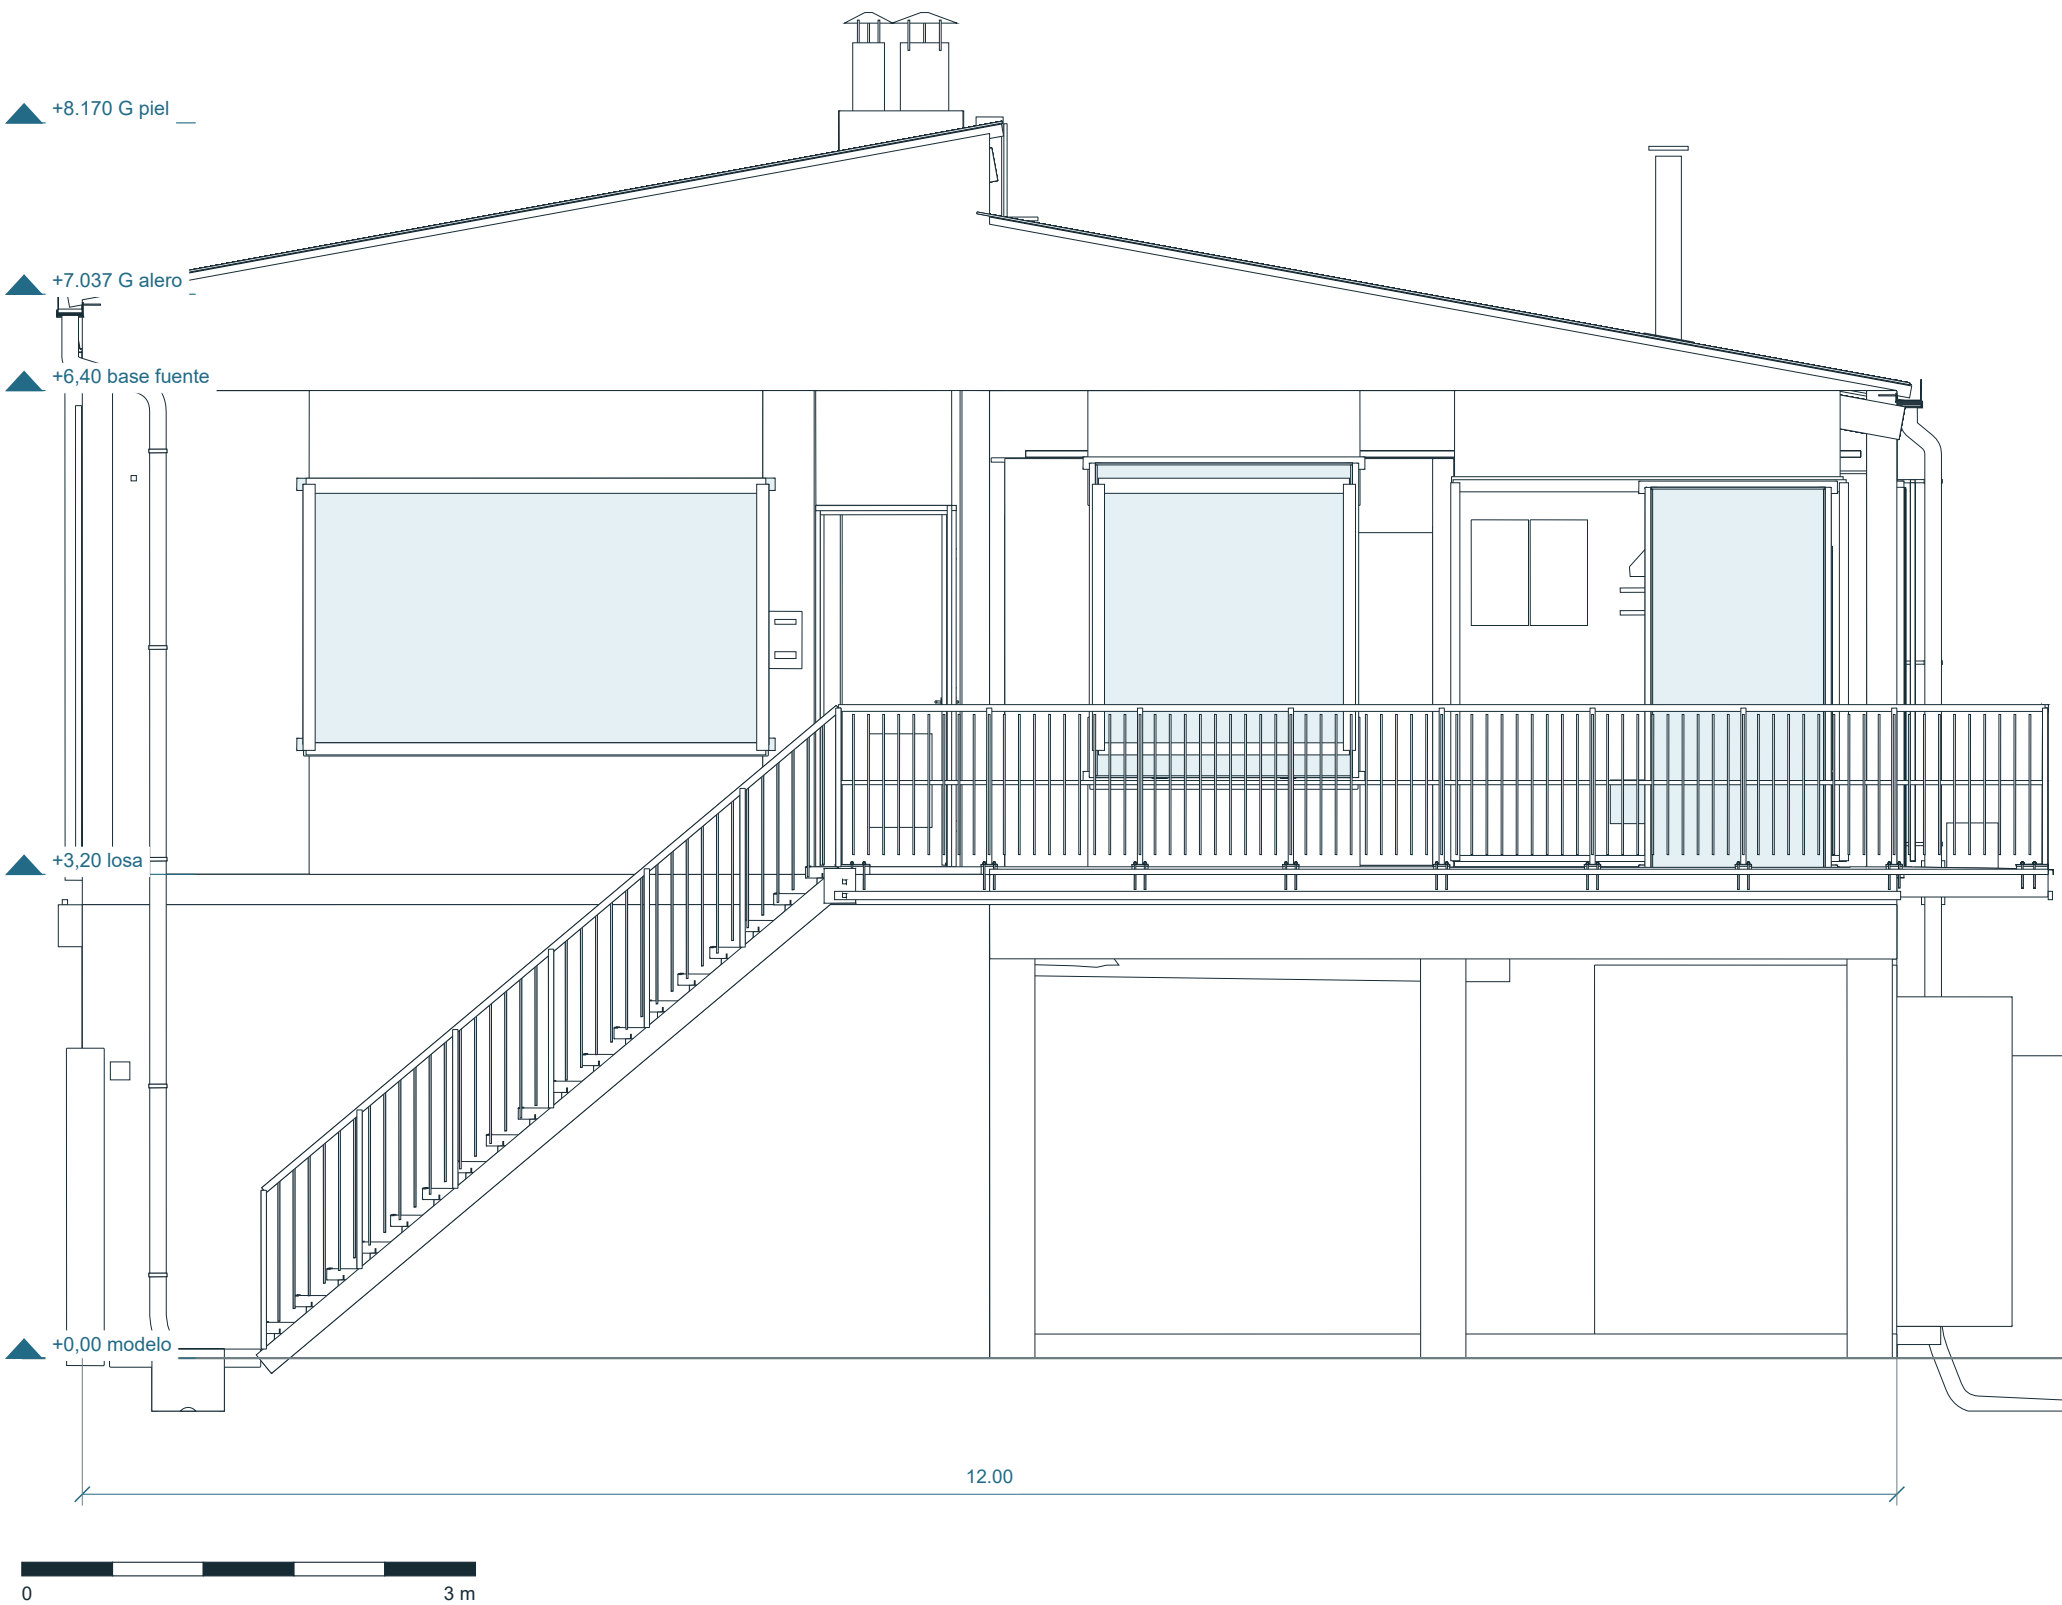

04 Medianera lateral | 1:50

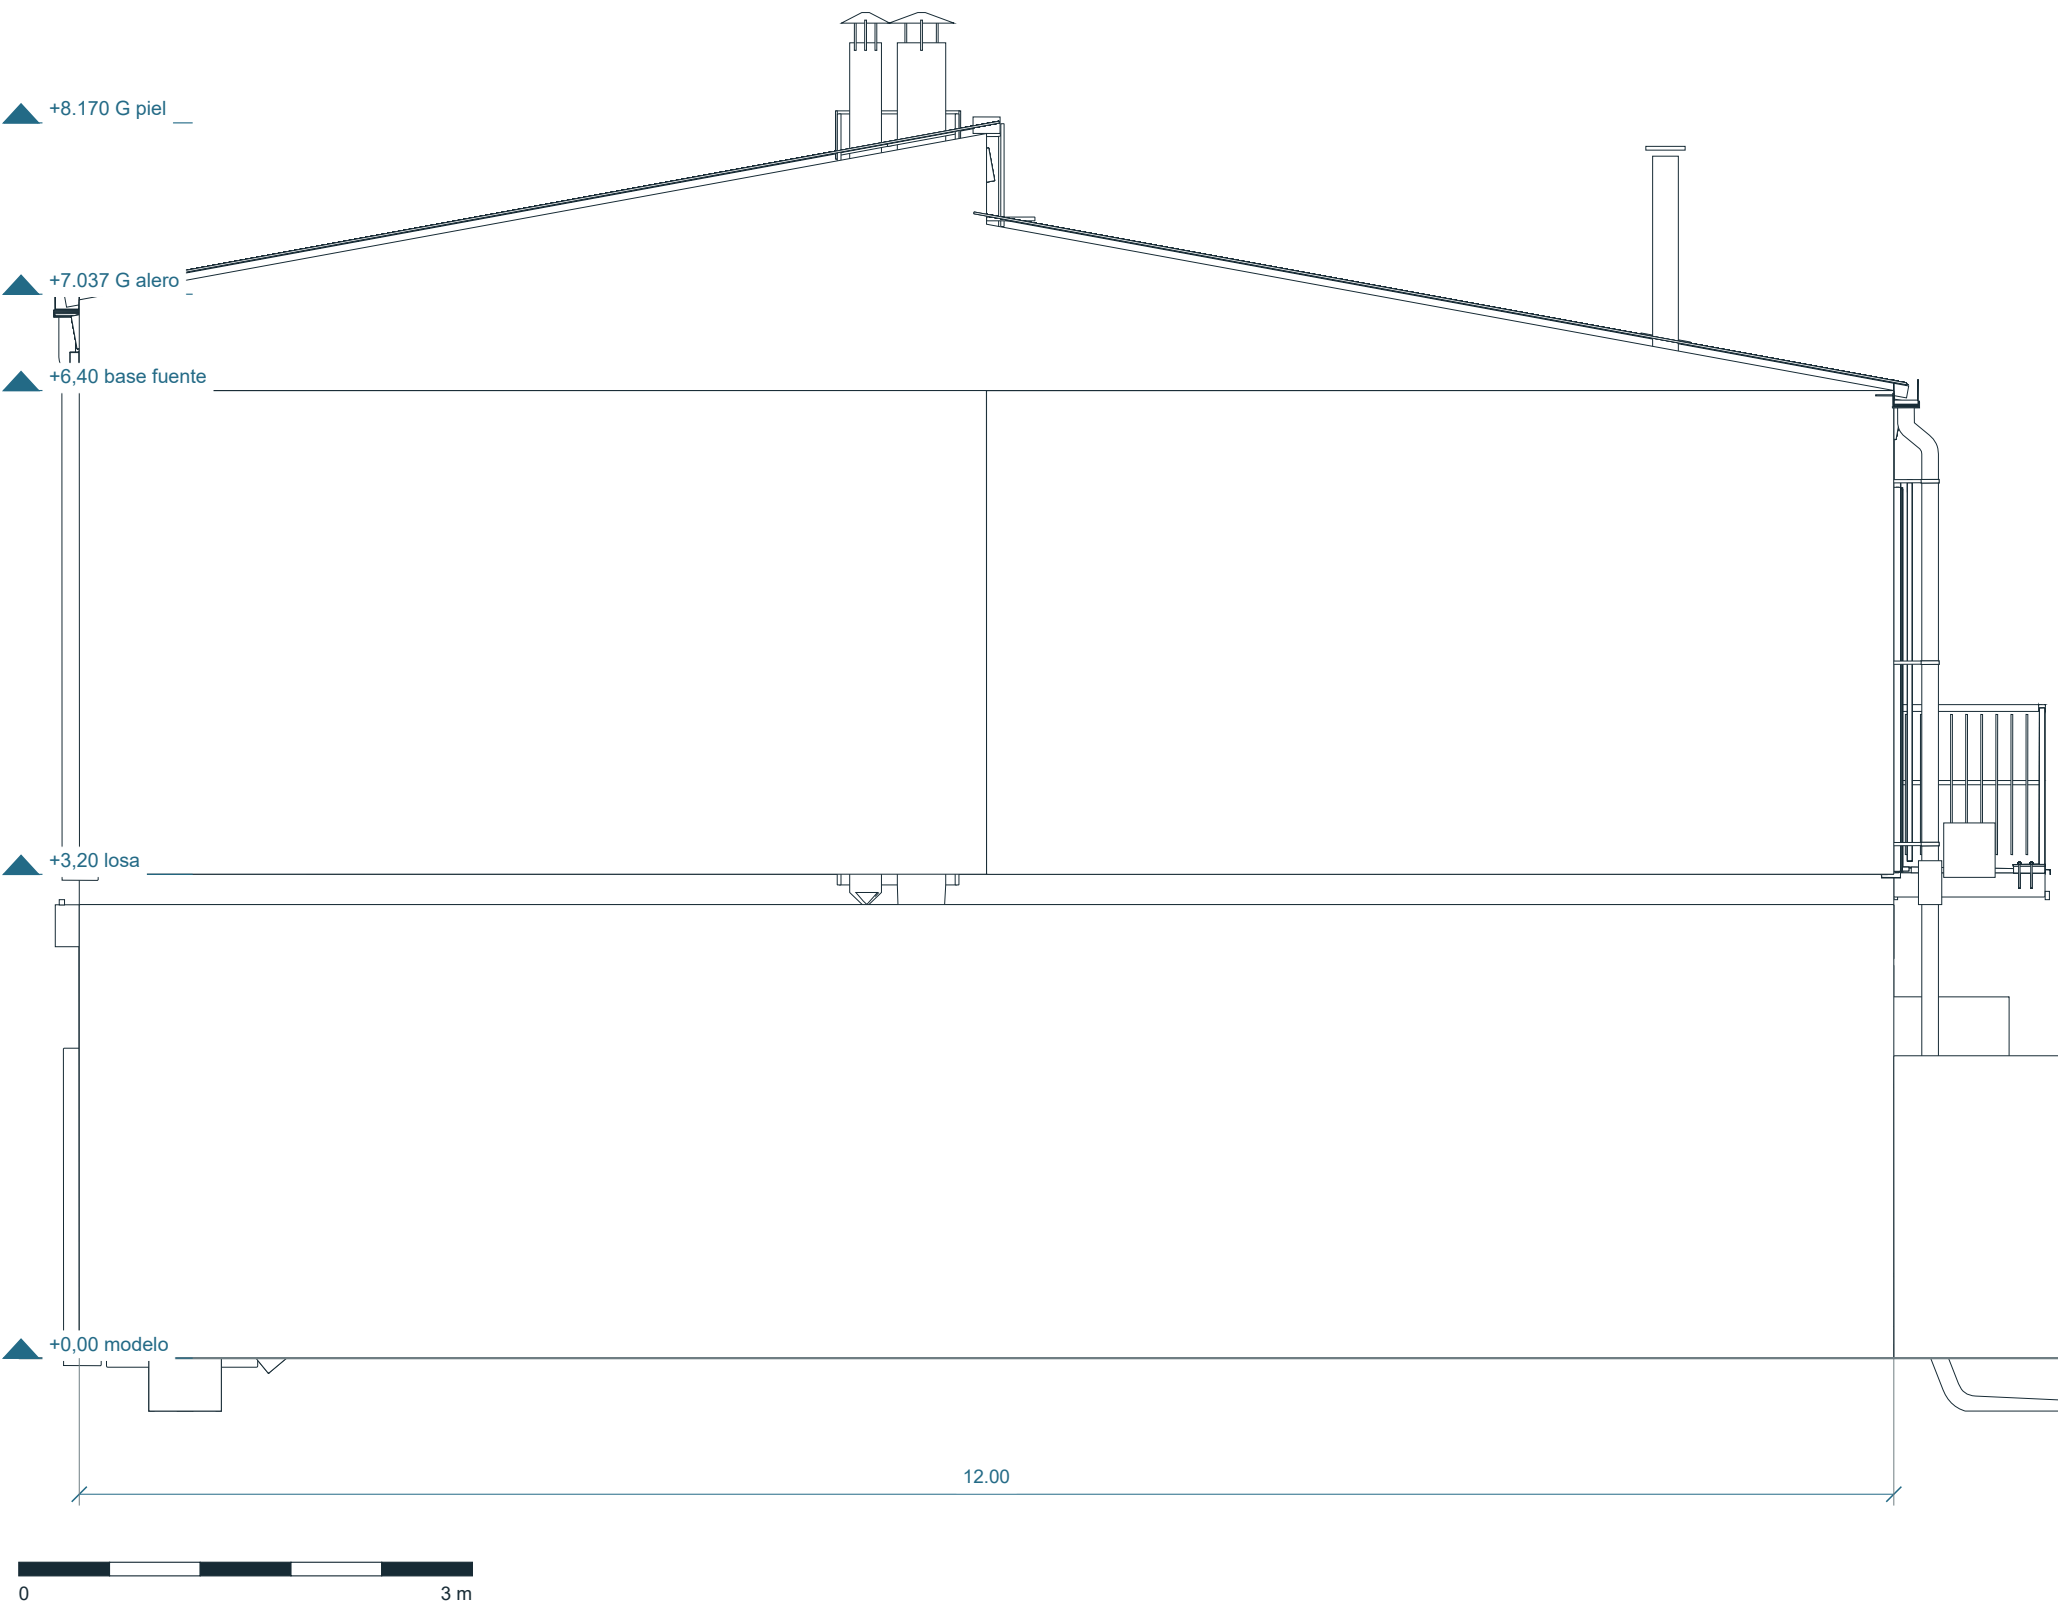


MATERIALIDAD REPRESENTADA


Ladrillo visto en cerramientos; hormigon en losas, pilares y vigas; cubierta metalica con encuentros y remates; DVH en carpinterias; herreria en balcones y escalera.

G cotas de piel exterior de cubierta extraidas de malla. F+7,00/+8,10 son referencias de fuente y no coronamiento terminado. A12/A13 y suplemento amplian hojas, capas y fijaciones; sin despiece certificado.

A-A Longitudinal por ambas alturas | 1:50

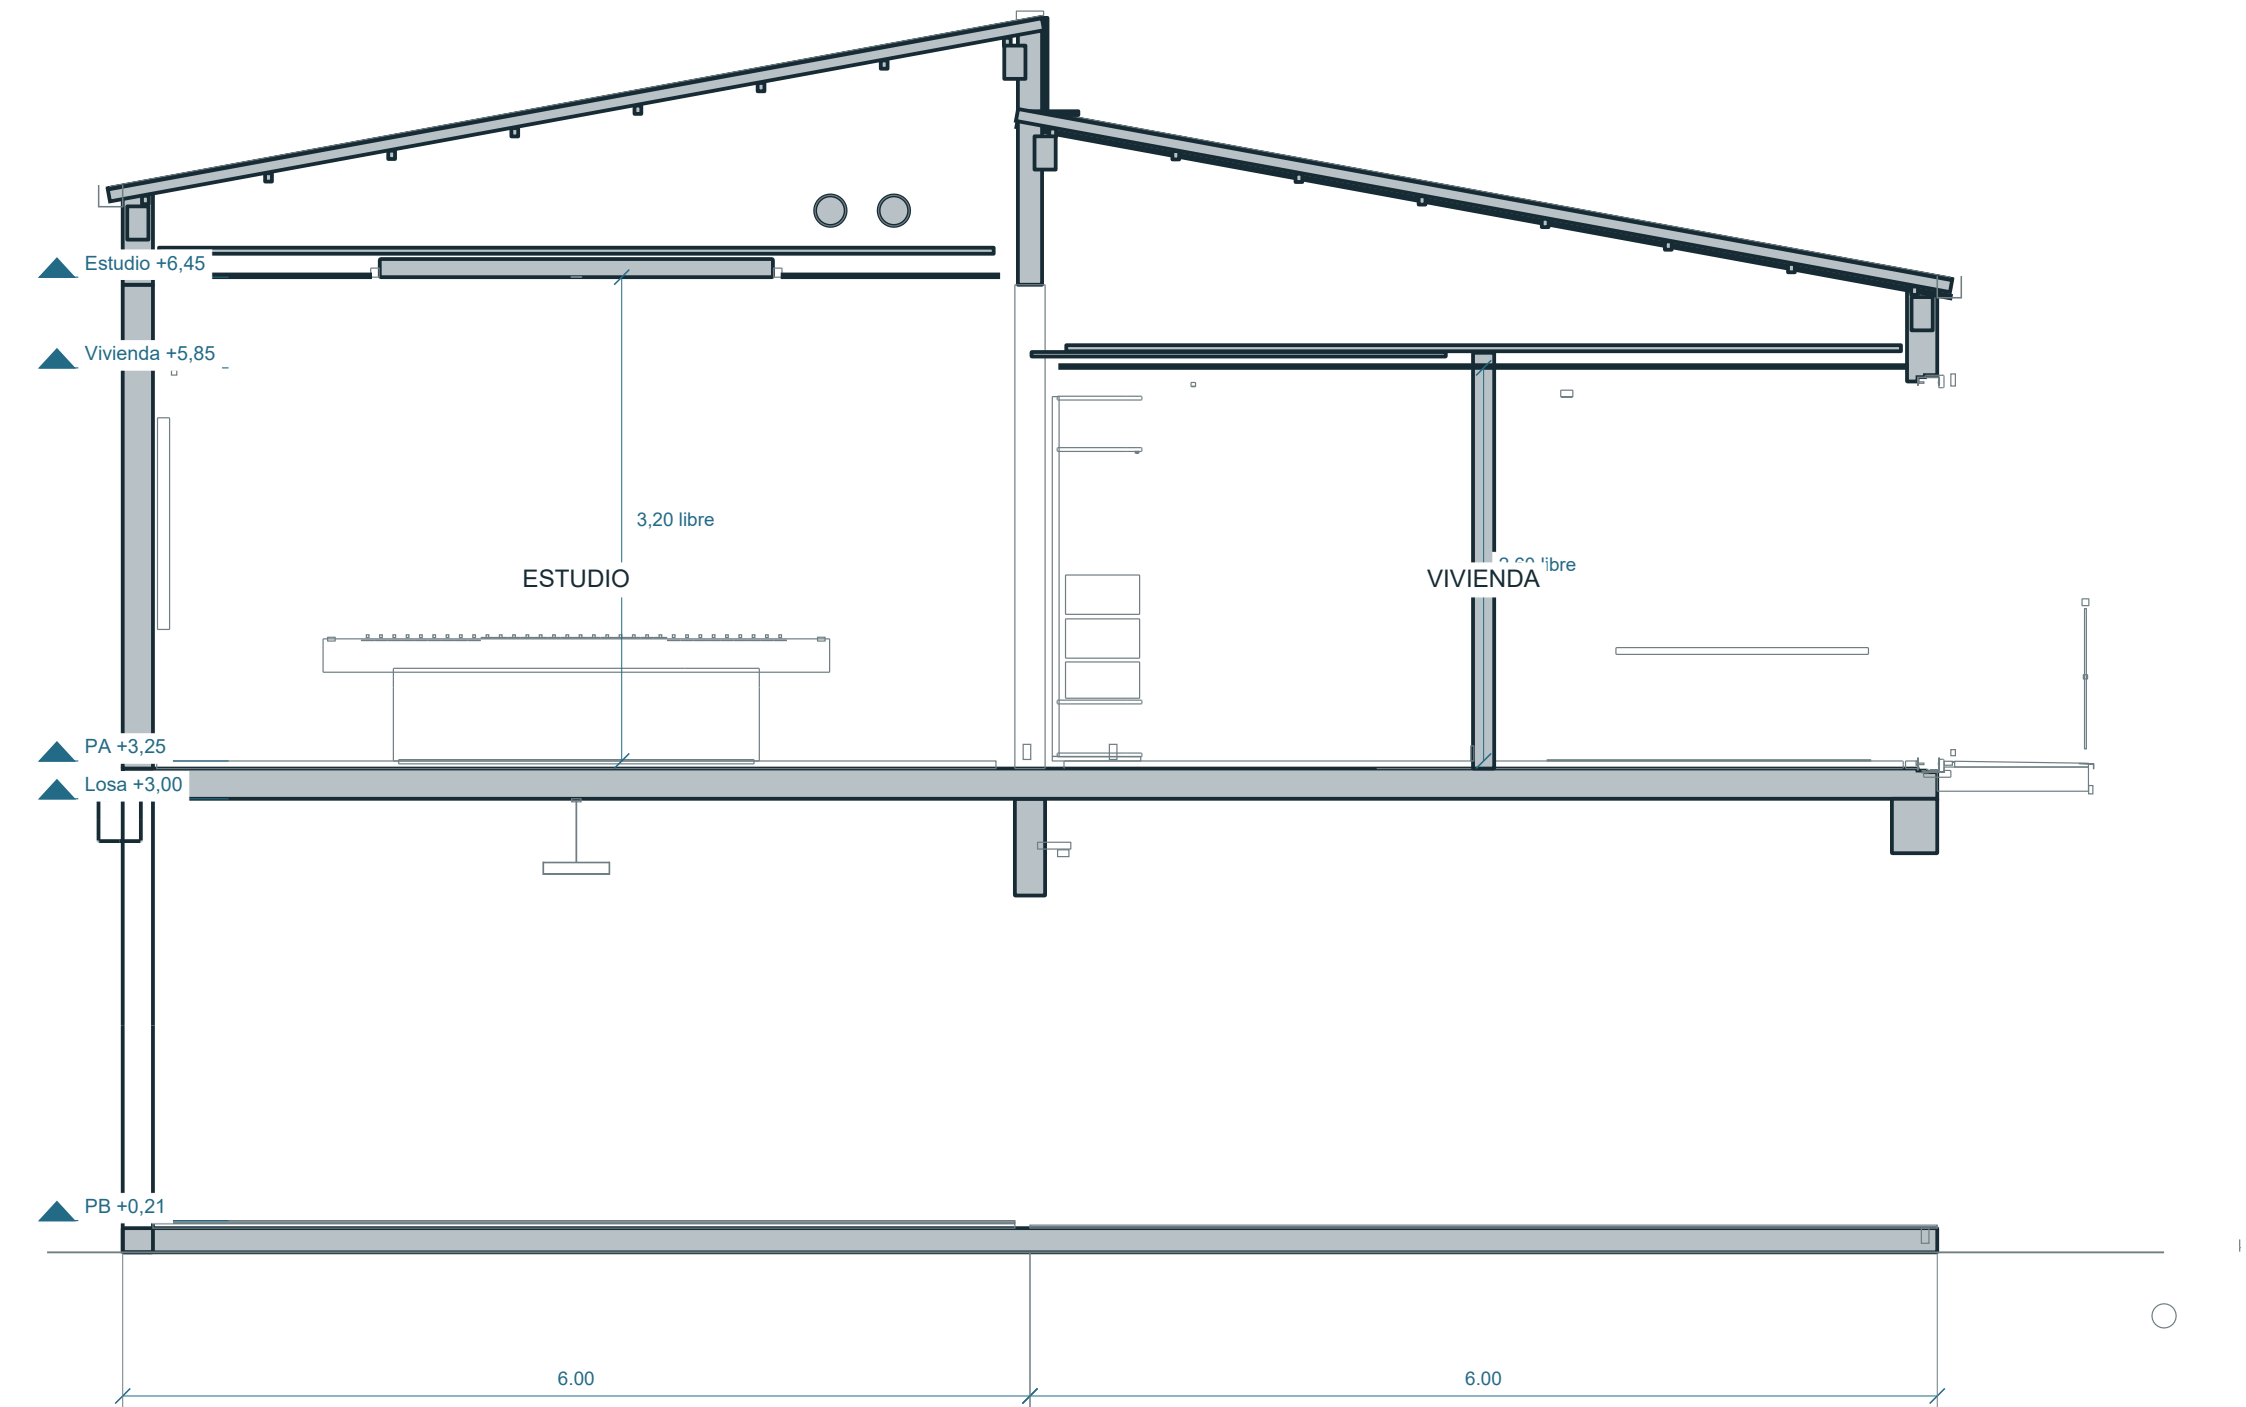

B-B Transversal por estudio | 1:50

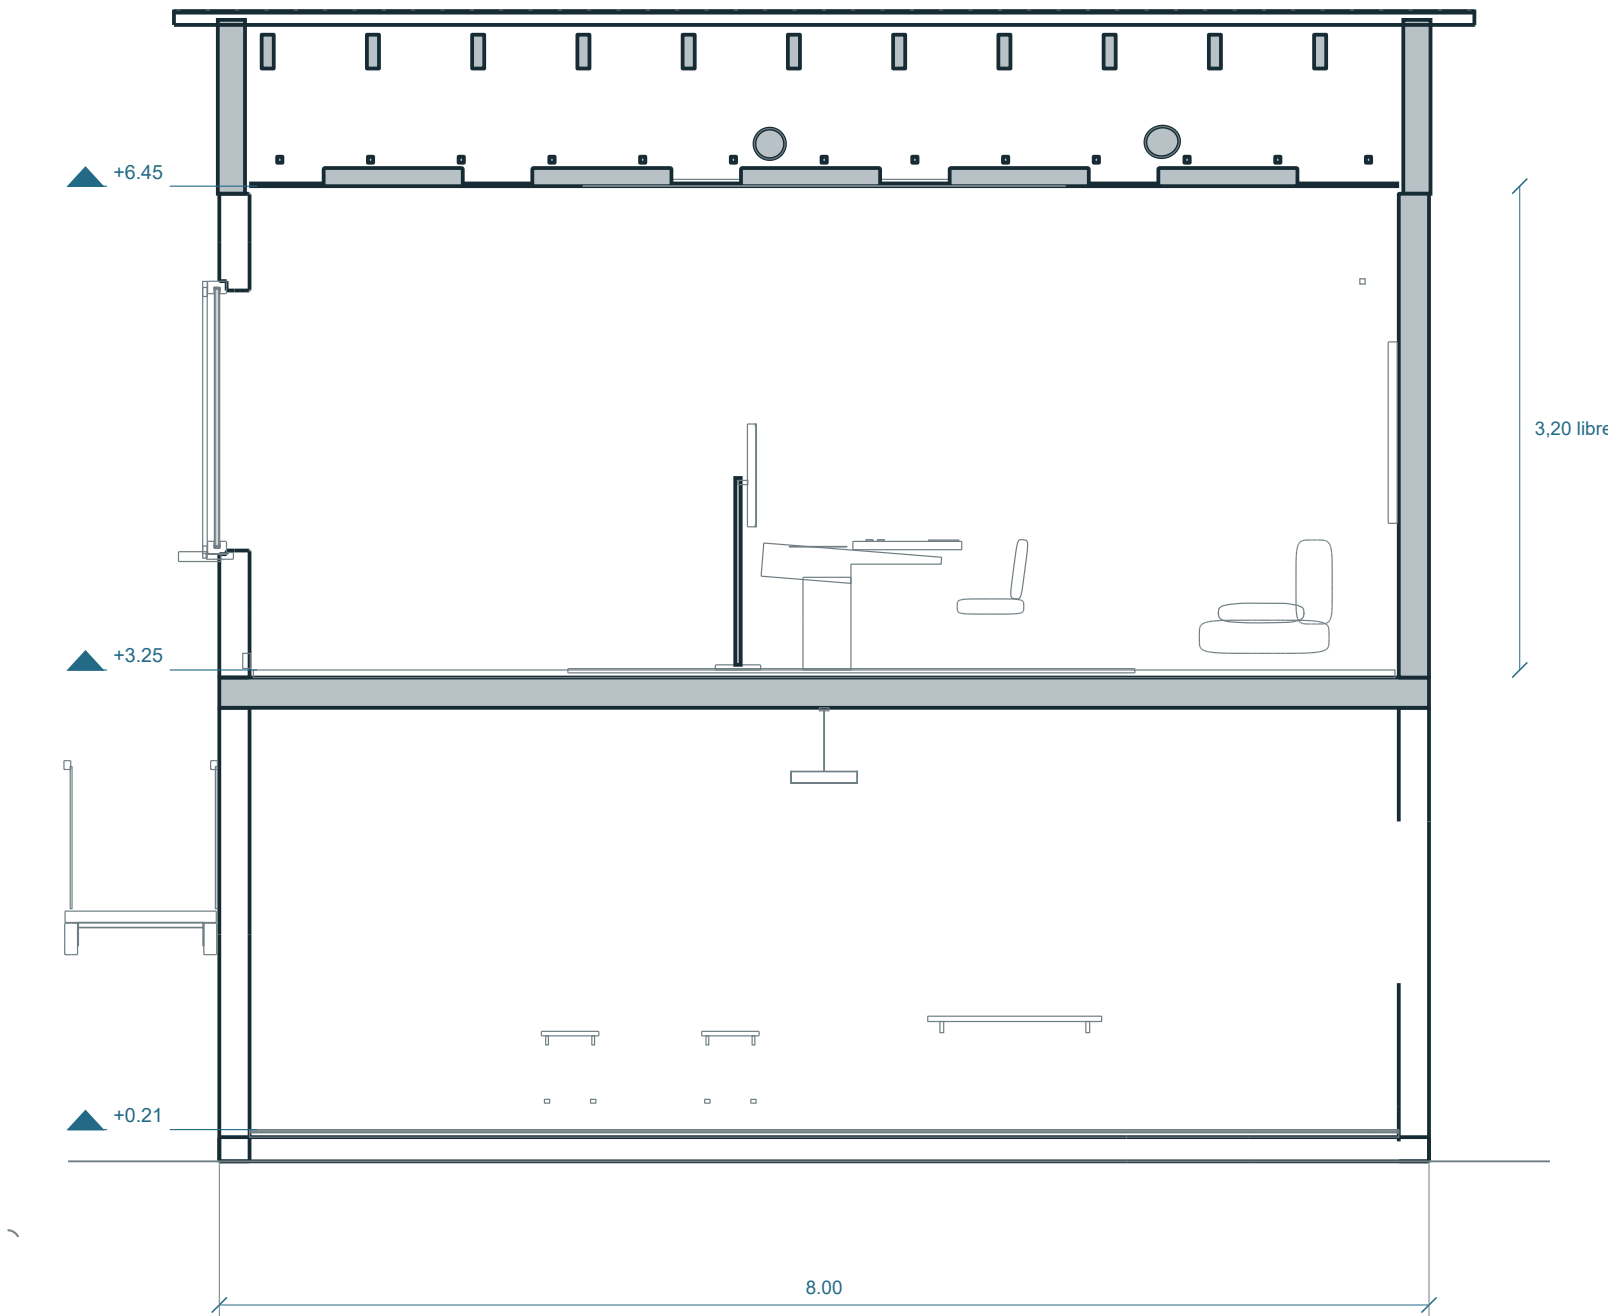


NIVELES Y CONSTRUCCION

G: losa entre plantas 0,20 m; piso general superior 0,05 m; cielorraso estudio +6,45 y vivienda +5,85. Corte A-A comprueba ambos volúmenes y el escalon exterior.


F: alturas libres autorizadas 3,20 / 2,60 m. La diferencia se conserva sin desplazar la implantación ni las huellas de los ambientes.

P: continuidad de cargas, fundaciones y conexiones por dimensionar. No hay estudio geotécnico ni verificación estructural; ver A14.


01 Planta / acceso | 1:20

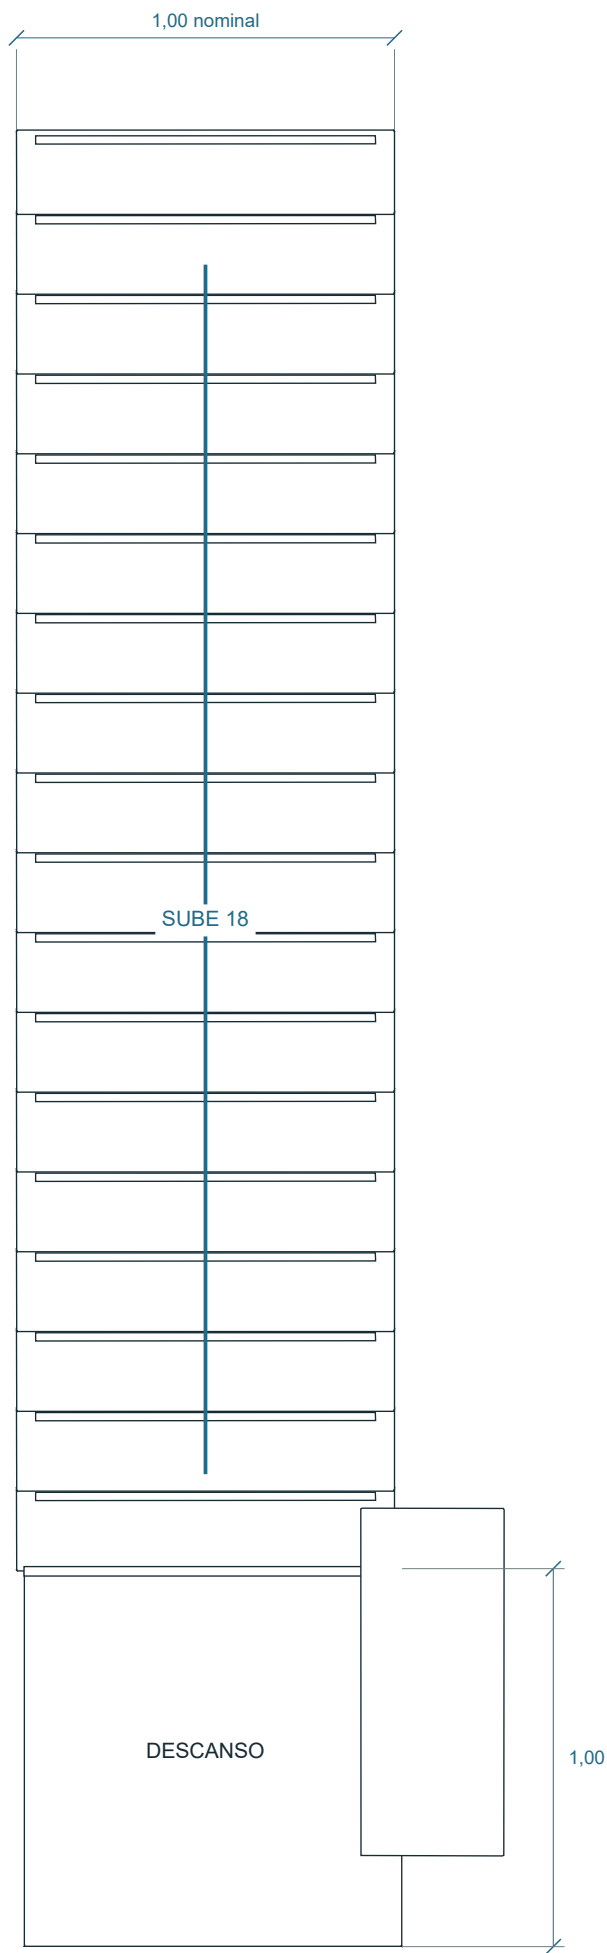

02 Seccion y proyeccion lateral | 1:20

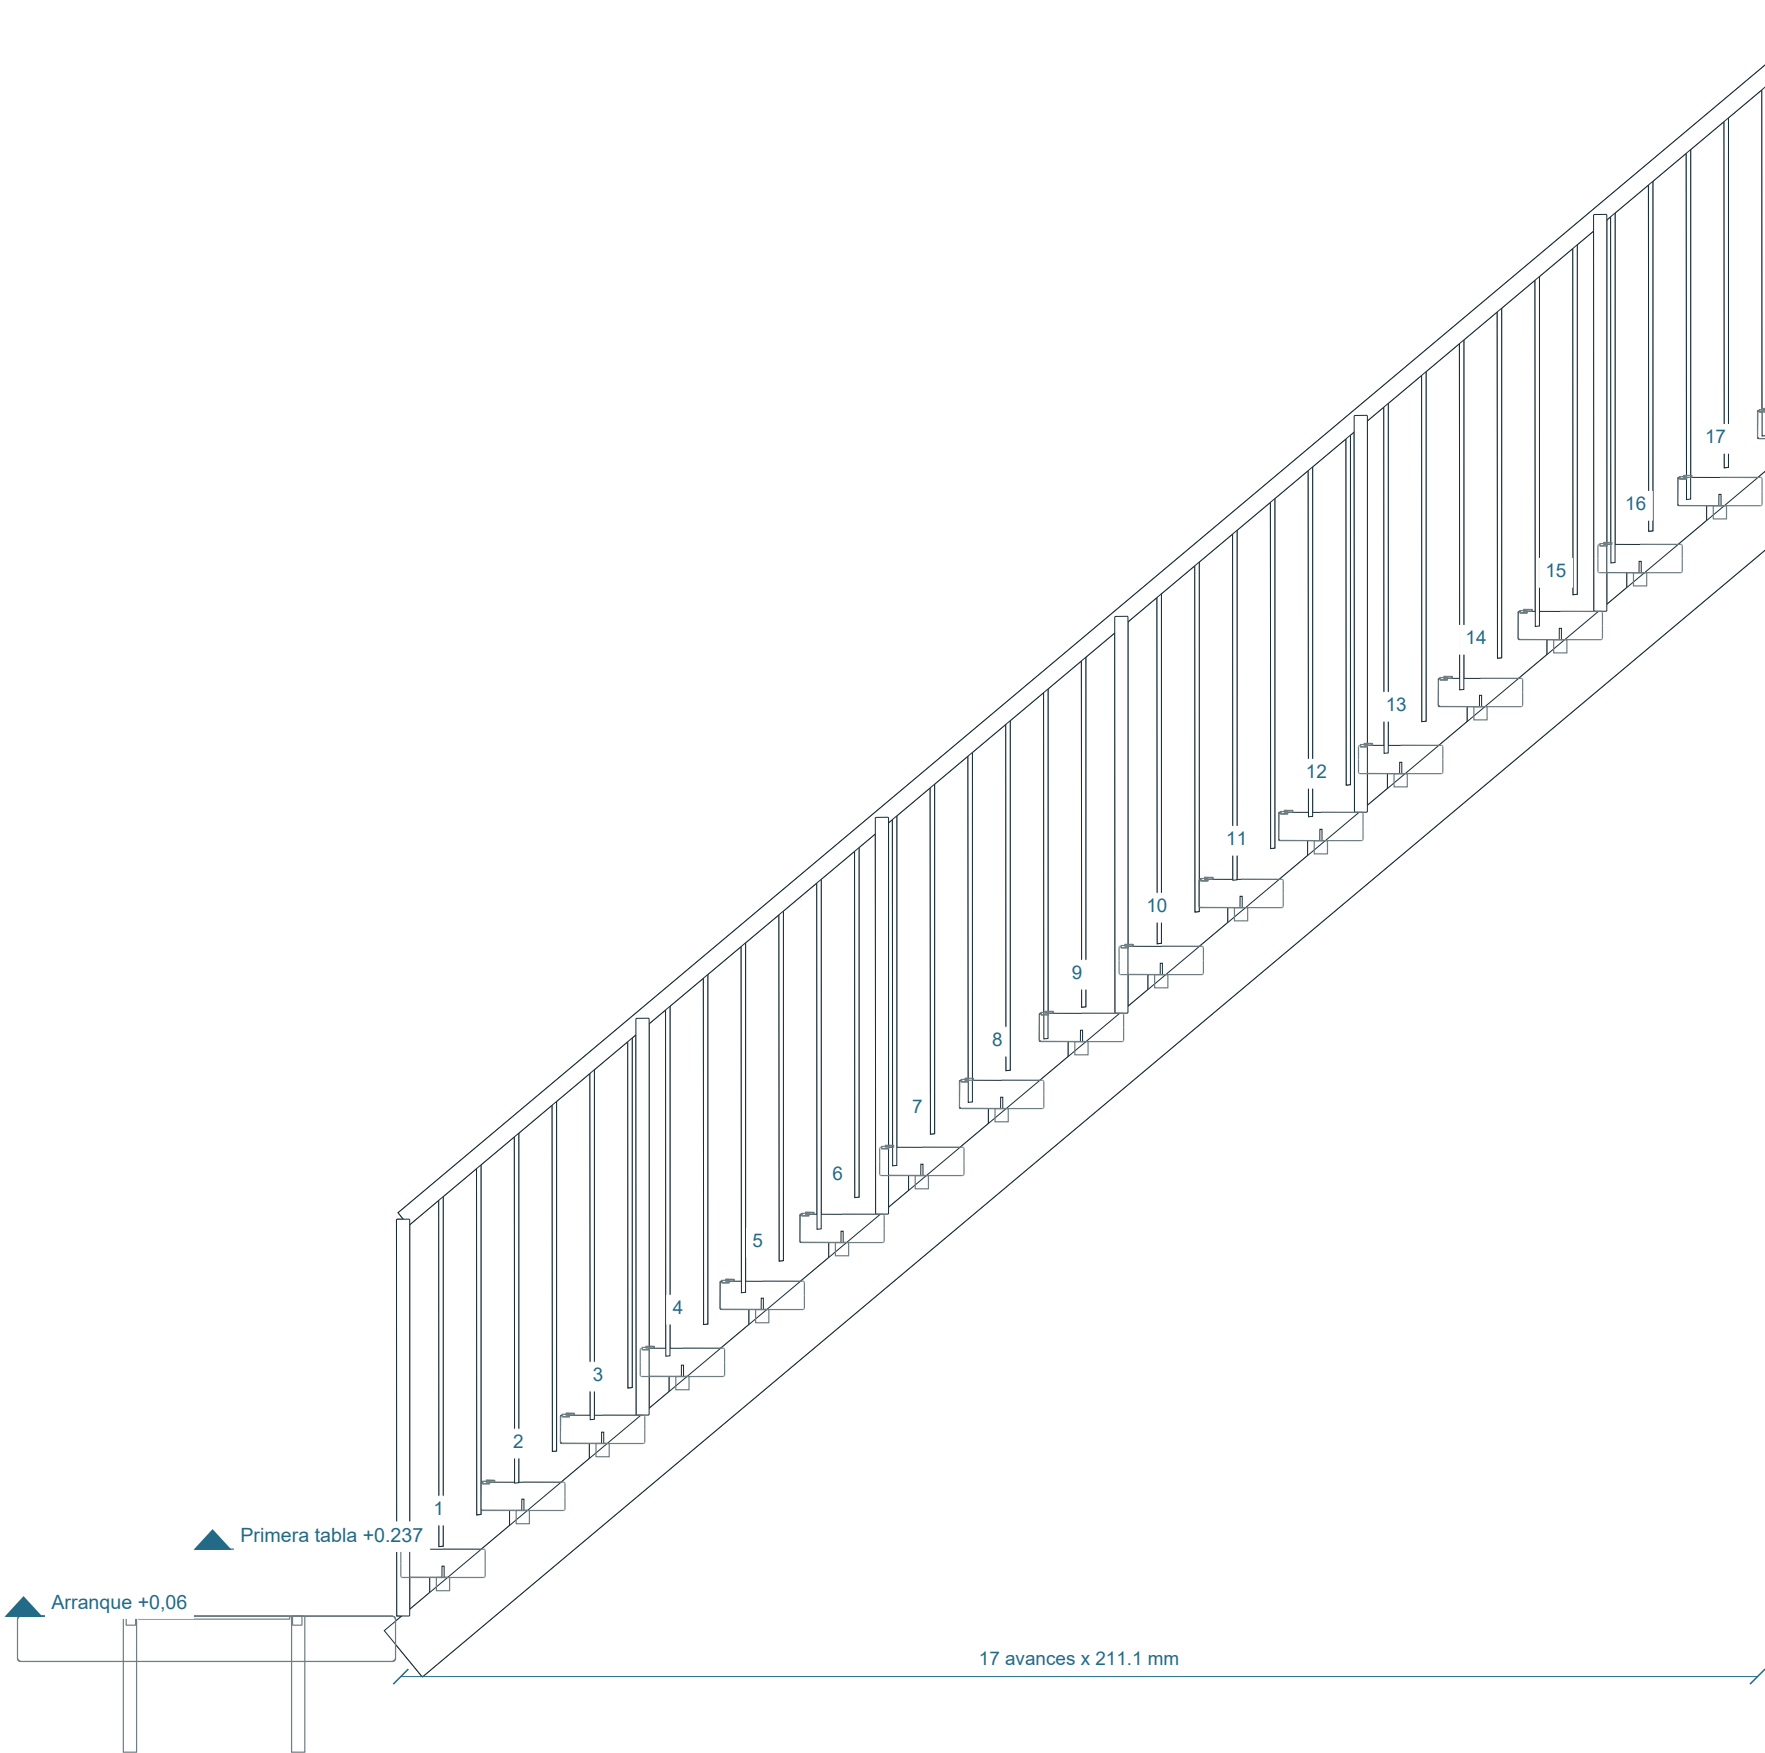

03 Umbral / corte Z=5,30 | 1:5

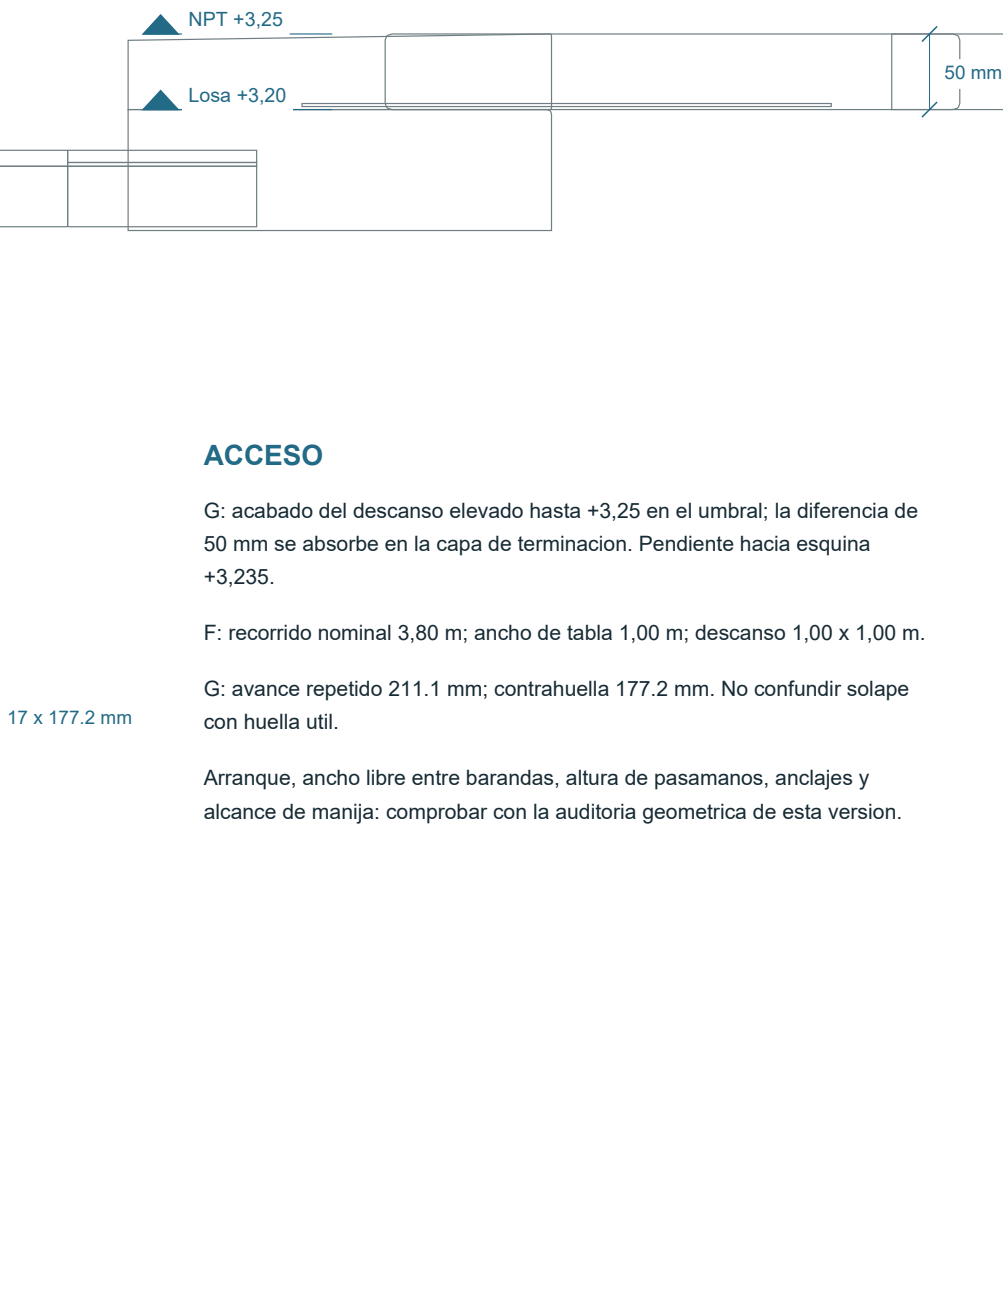

ACCESO

G: acabado del descanso elevado hasta +3,25 en el umbral; la diferencia de 50 mm se absorbe en la capa de terminacion. Pendiente hacia esquina +3,235.

F: recorrido nominal 3,80 m; ancho de tabla 1,00 m; descanso 1,00 x 1,00 m.


G: avance repetido 211.1 mm; contrahuella 177.2 mm. No confundir solape con huella util.

Arranque, ancho libre entre barandas, altura de pasamanos, anclajes y alcance de manija: comprobar con la auditoria geometrica de esta version.

COMPROBACIONES DE USO Y ANCLAJES

G soportes peldaños: tubo hueco35x35x3 sobre cartelas6 a zancas; narices embutidas4 y saliente2mm. Geometria de fijacion propuesta, capacidad pendiente. A14 y D05/D05b amplian apoyos.


01 Planta del vaso y playa humeda | 1:25



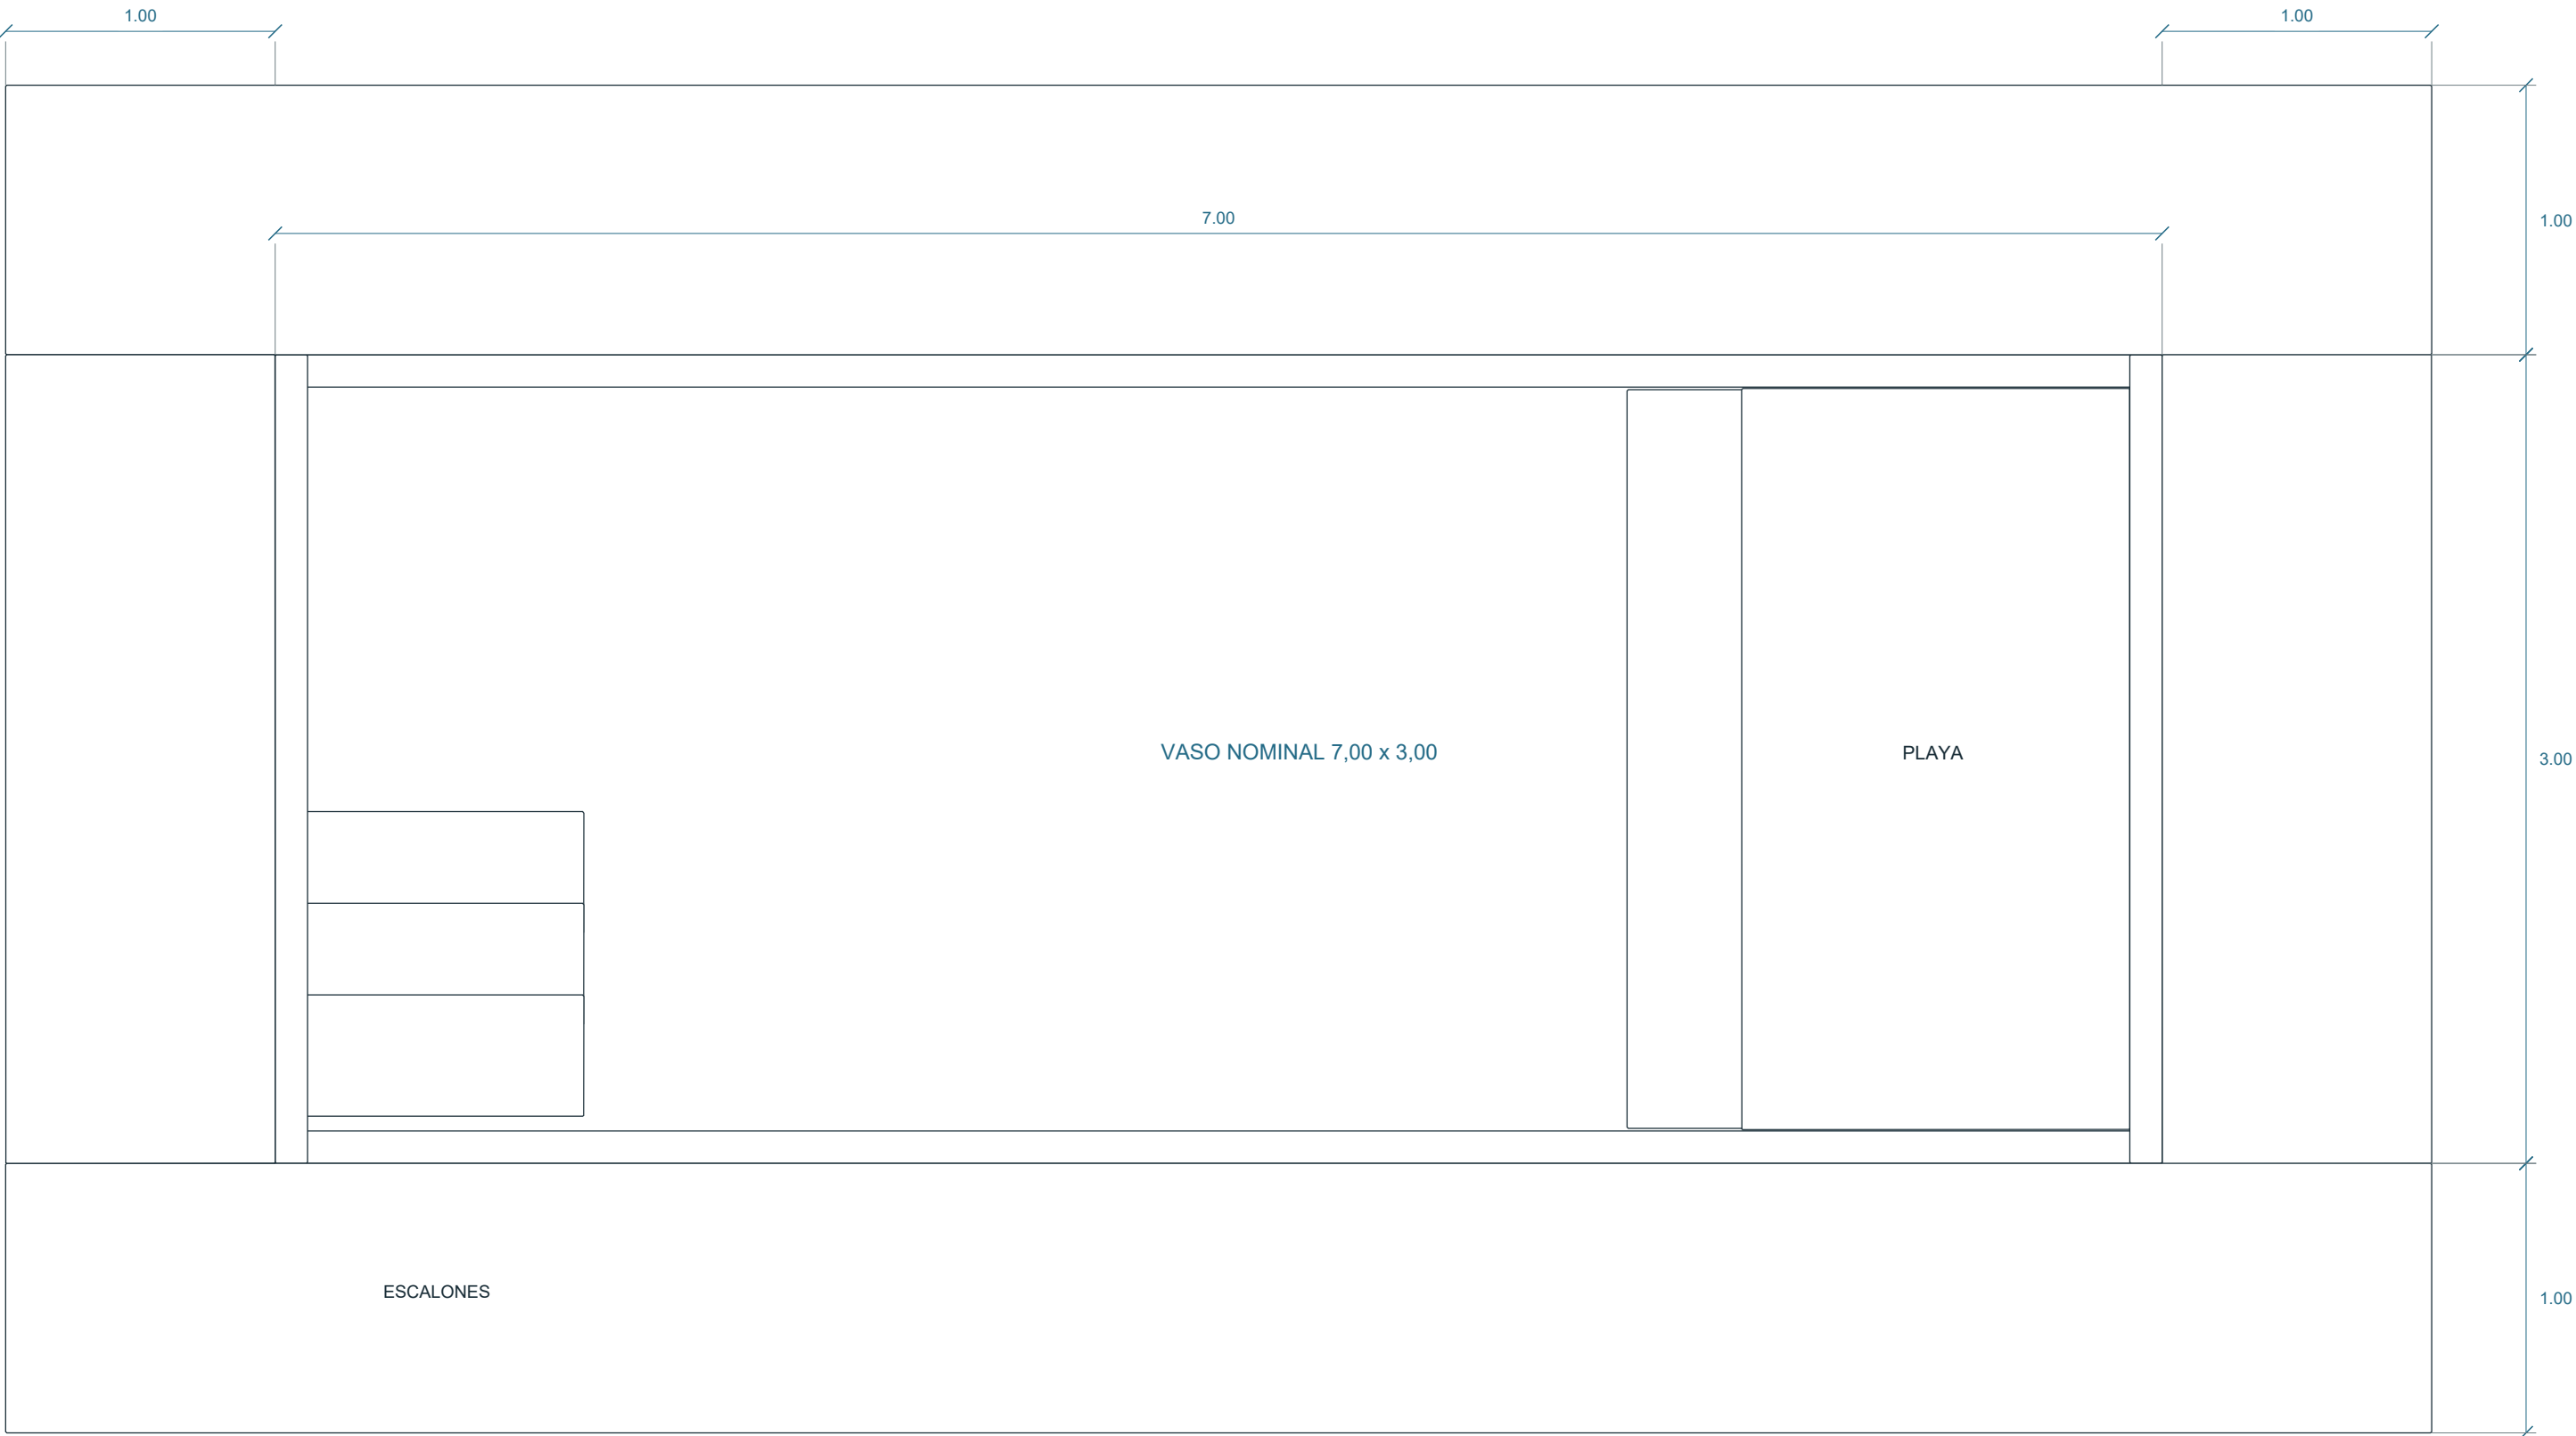


NIVELES DEL MODELO

- G: pavimento perimetral +0,09 m; borde vertical del vaso hasta +0,07 m.
- G: fondo del vaso entre -1,57 y -1,39 m; espesor representado 0,18 m.
- G: tres escalones con caras superiores -0,14 / -0,43 / -0,72 m.
- G: playa humeda -0,080 m; agua -0.030 m; profundidad actual 50 mm. Escalon intermedio -0,31 m.
- G cresta de agua -0.030 m; resguardo geometrico 100 mm al borde. P nivel operativo sujeto a proyecto hidraulico.
- G: agua recortada contra vaso, playa y escalones; fondo de agua -1.390 m, coincidente con cara superior del vaso. Proyecto hidraulico P pendiente.
- P: skimmer, retornos, filtrado y desague por dimensionar y coordinar. Esquema en A15.


02 Corte transversal al largo / Z=16,50 | 1:50

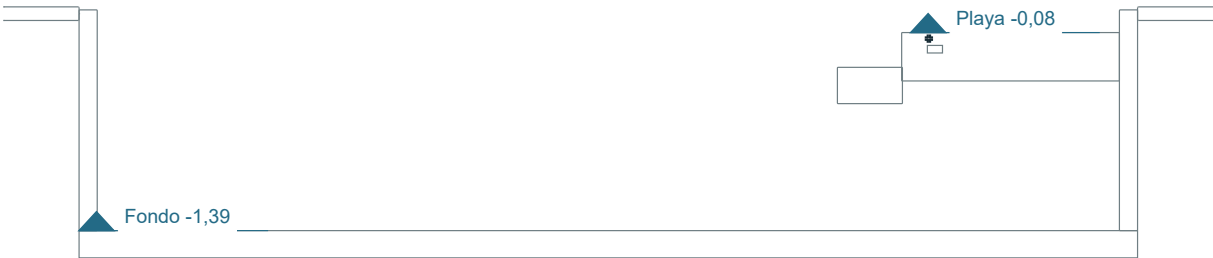

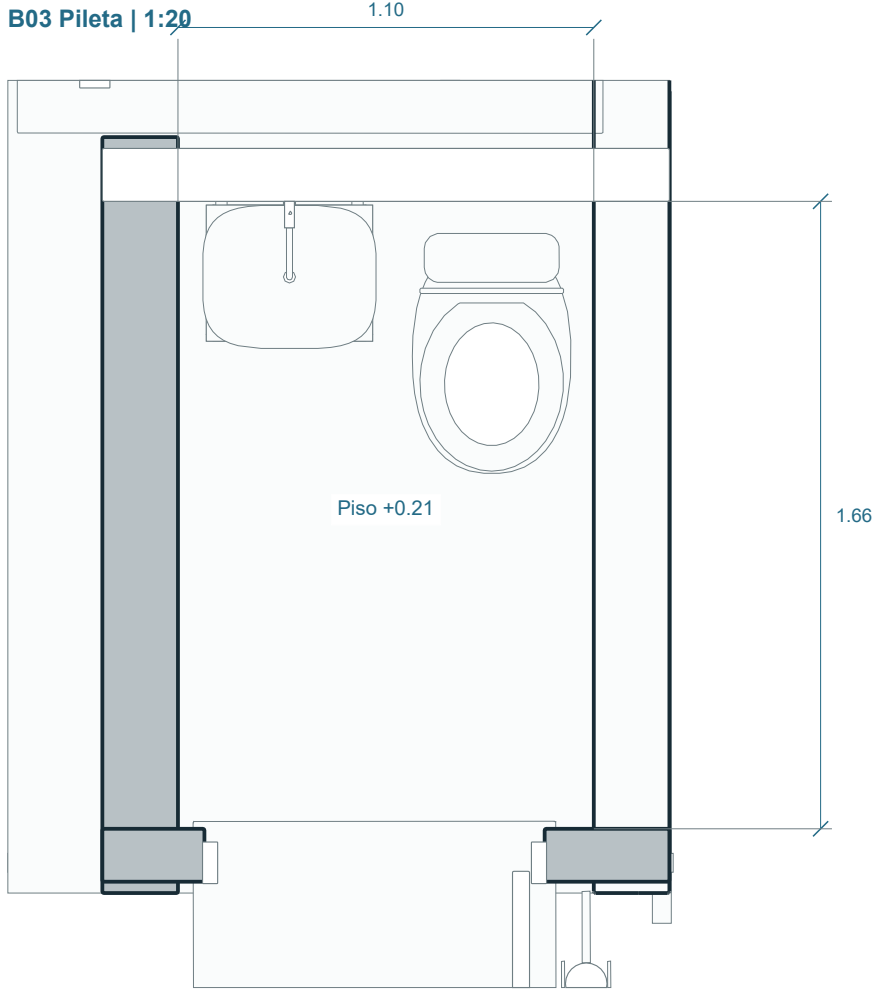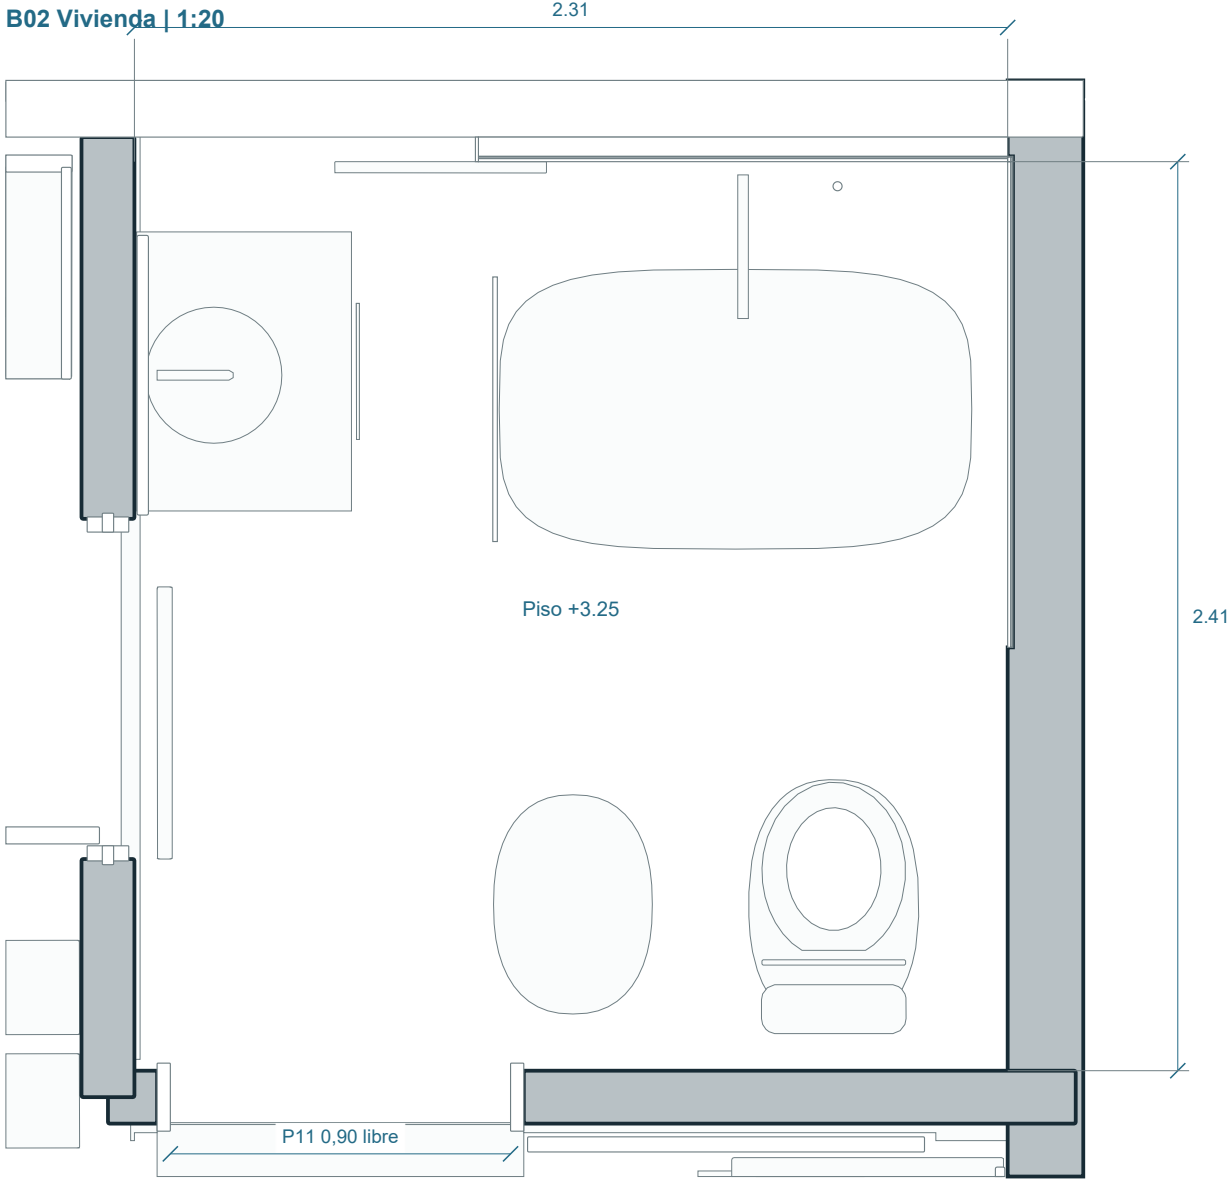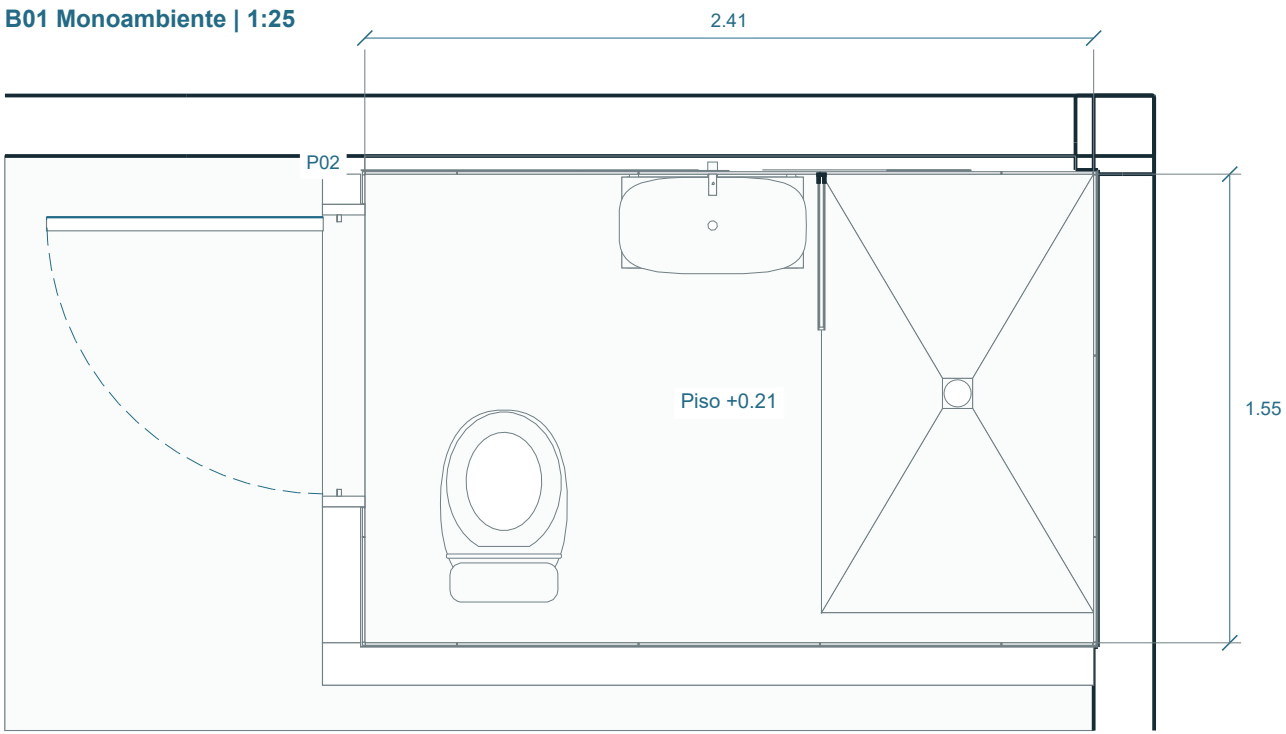


G: artefactos y mamparas de la malla actual; cotas interiores entre caras. D09 detalla piso continuo PA; D11 capas, sumidero y altura de ducha PB. Accesos de mantenimiento, productos y ensayos pendientes; hojas en A12.


Elevacion interior / artefactos | 1:25

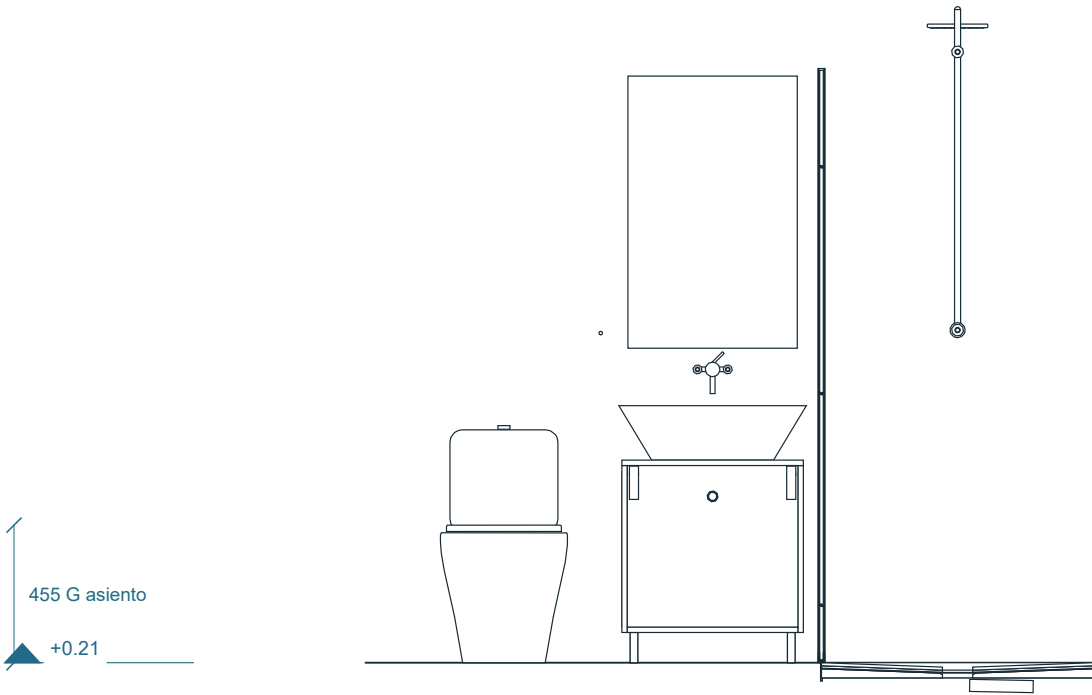


WC y bidet / hacia muro posterior | 1:20

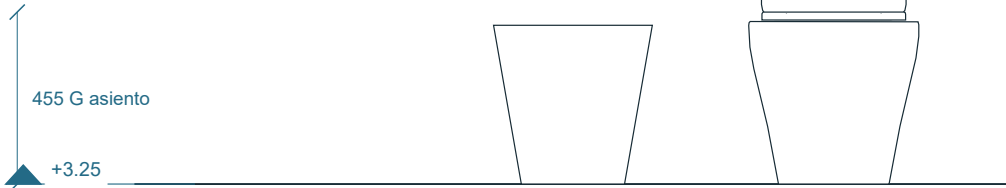

Elevacion interior / artefactos | 1:20

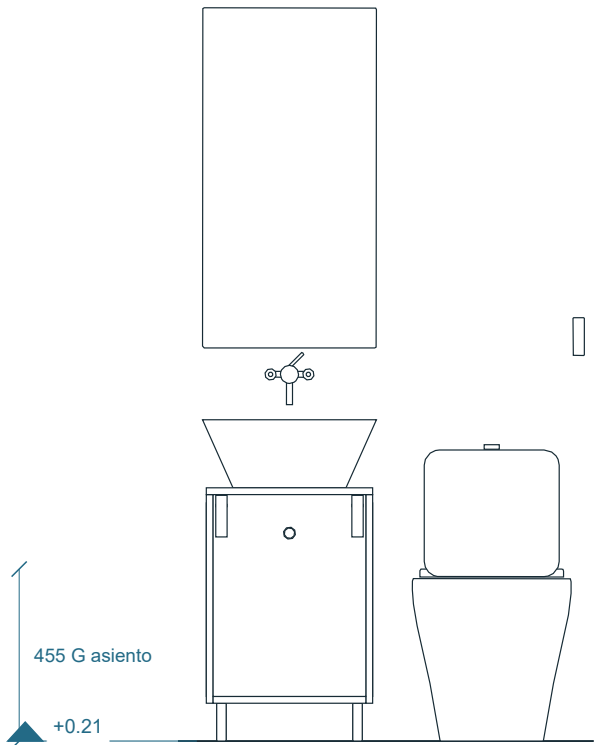

01 Línea del quincho | 1:25

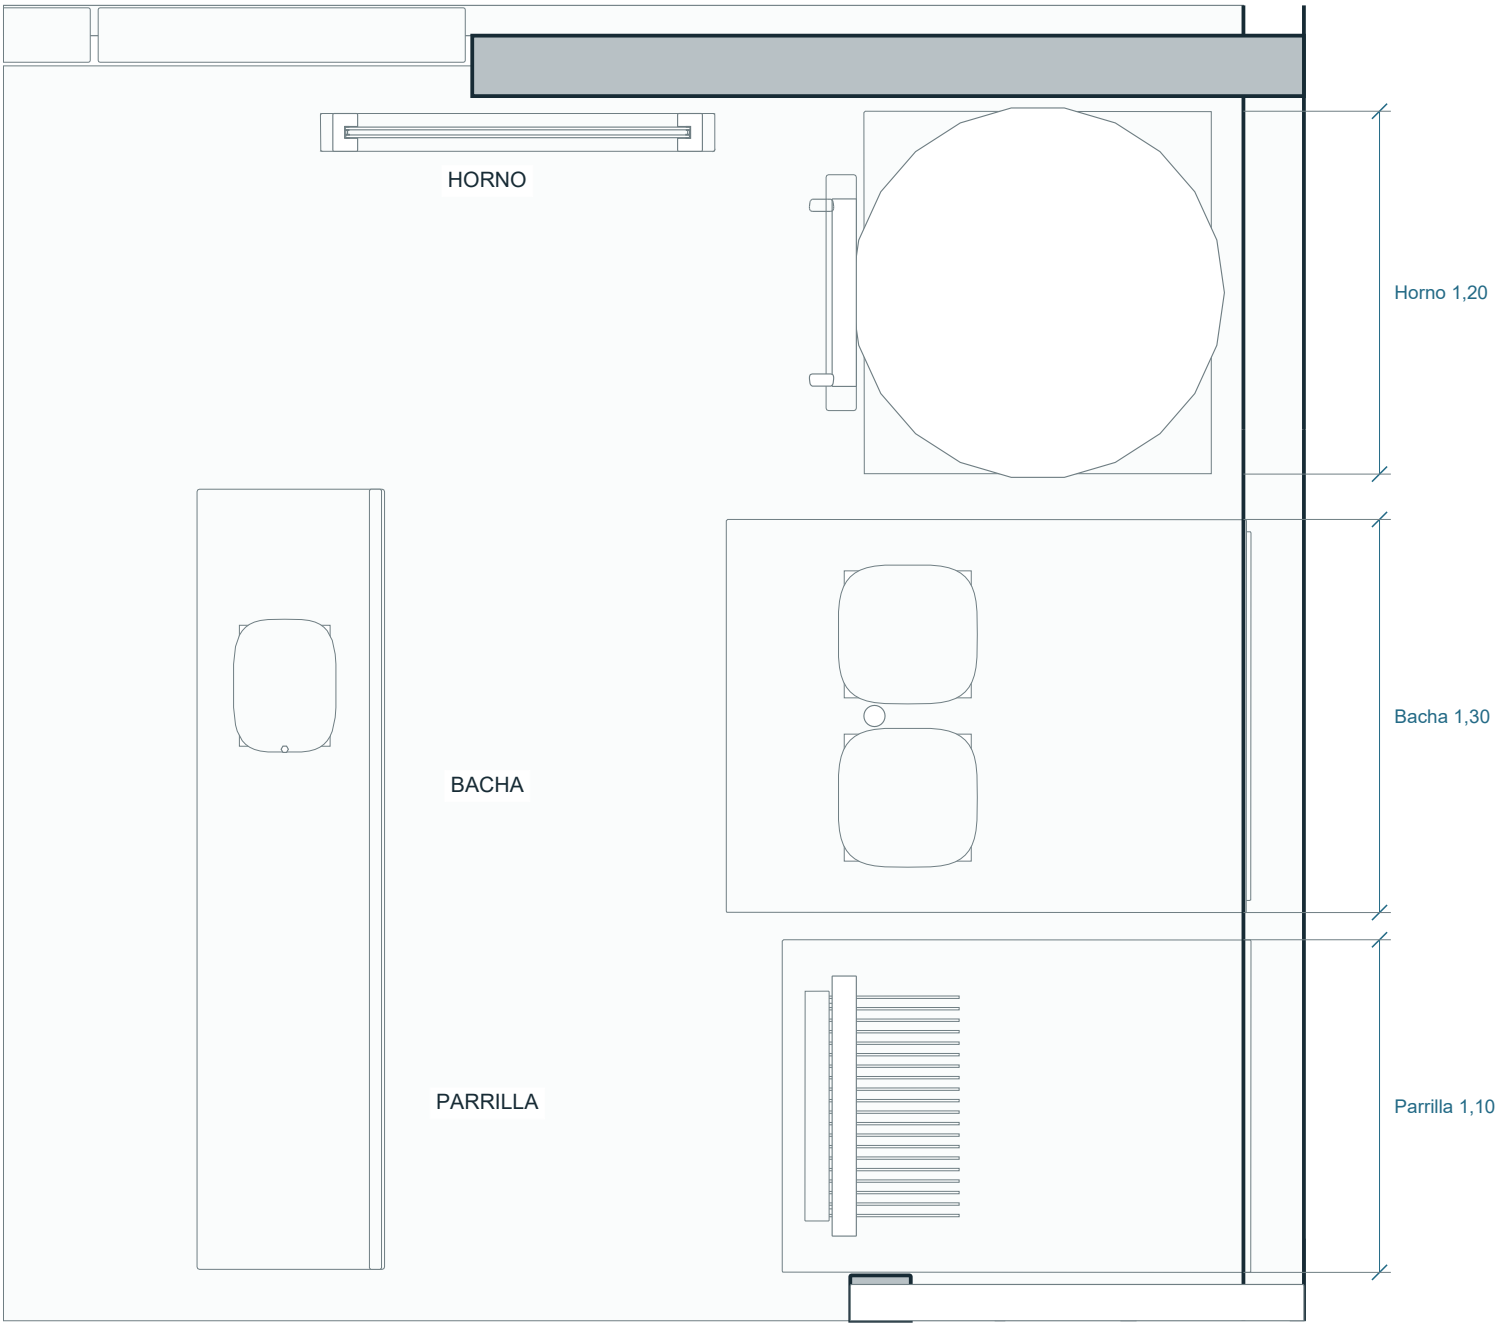


ALTURAS Y RELACION CON LOS LOCALES

G: cotas absolutas medidas de trabajo: mesa quincho +0.930; mesa comedor +4.000. No equivalen a altura desde el piso.


Comparar alturas de trabajo descontando el piso terminado de cada ambiente. No se confunden cotas absolutas con altura sobre piso.

La campana, el faldon y la boca de cada equipo se leen en los cortes del modelo. El tiro de combustion no esta certificado.

02 Cocina mono / ver A10b | 1:50

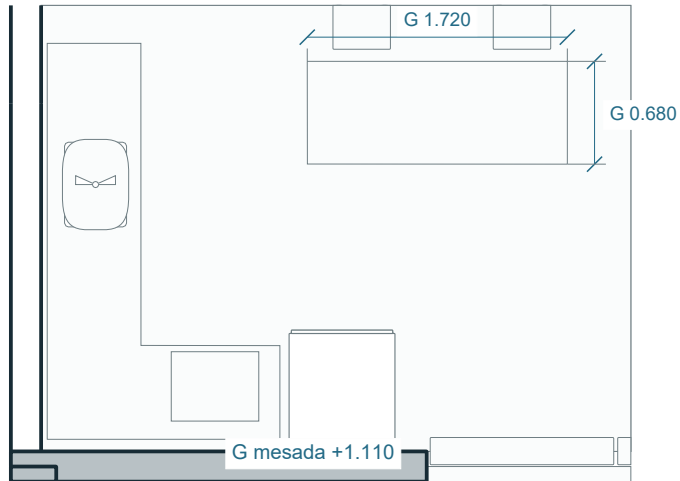

03 Cocina vivienda | 1:25

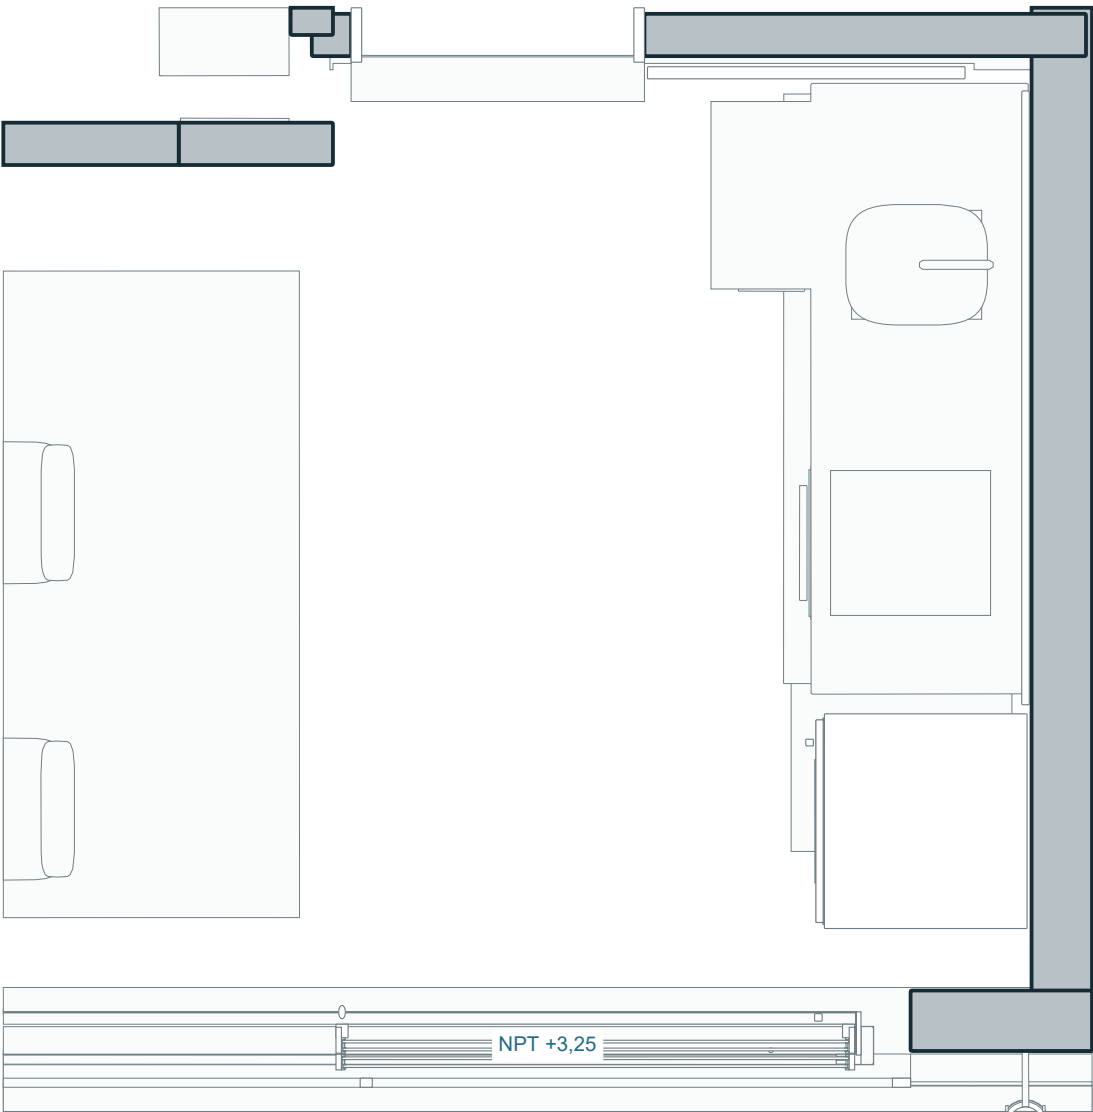

EXTRACCION Y MANTENIMIENTO

G: horno y parrilla con conductos independientes hacia el patinillo junto al estudio; cocina vivienda con salida independiente.


G: diametros representados de horno / parrilla ~0,21 / 0,32 m; son dimensiones de malla, no resultado de calculo.

P: verificar longitud desarrollada, radios, caudal, reposicion de aire, temperatura, aislamiento, registro y limpieza.

P: conexiones sanitarias de bachas y lavatorios, llaves de corte y sifones requieren detalle de instalacion. A15 ubica los puntos de coordinacion.

El patinillo comparte proximidad con el estudio. A11 identifica control termico, vibratorio y acustico pendiente.

01 Planta completa / piso +0,21 | 1:25

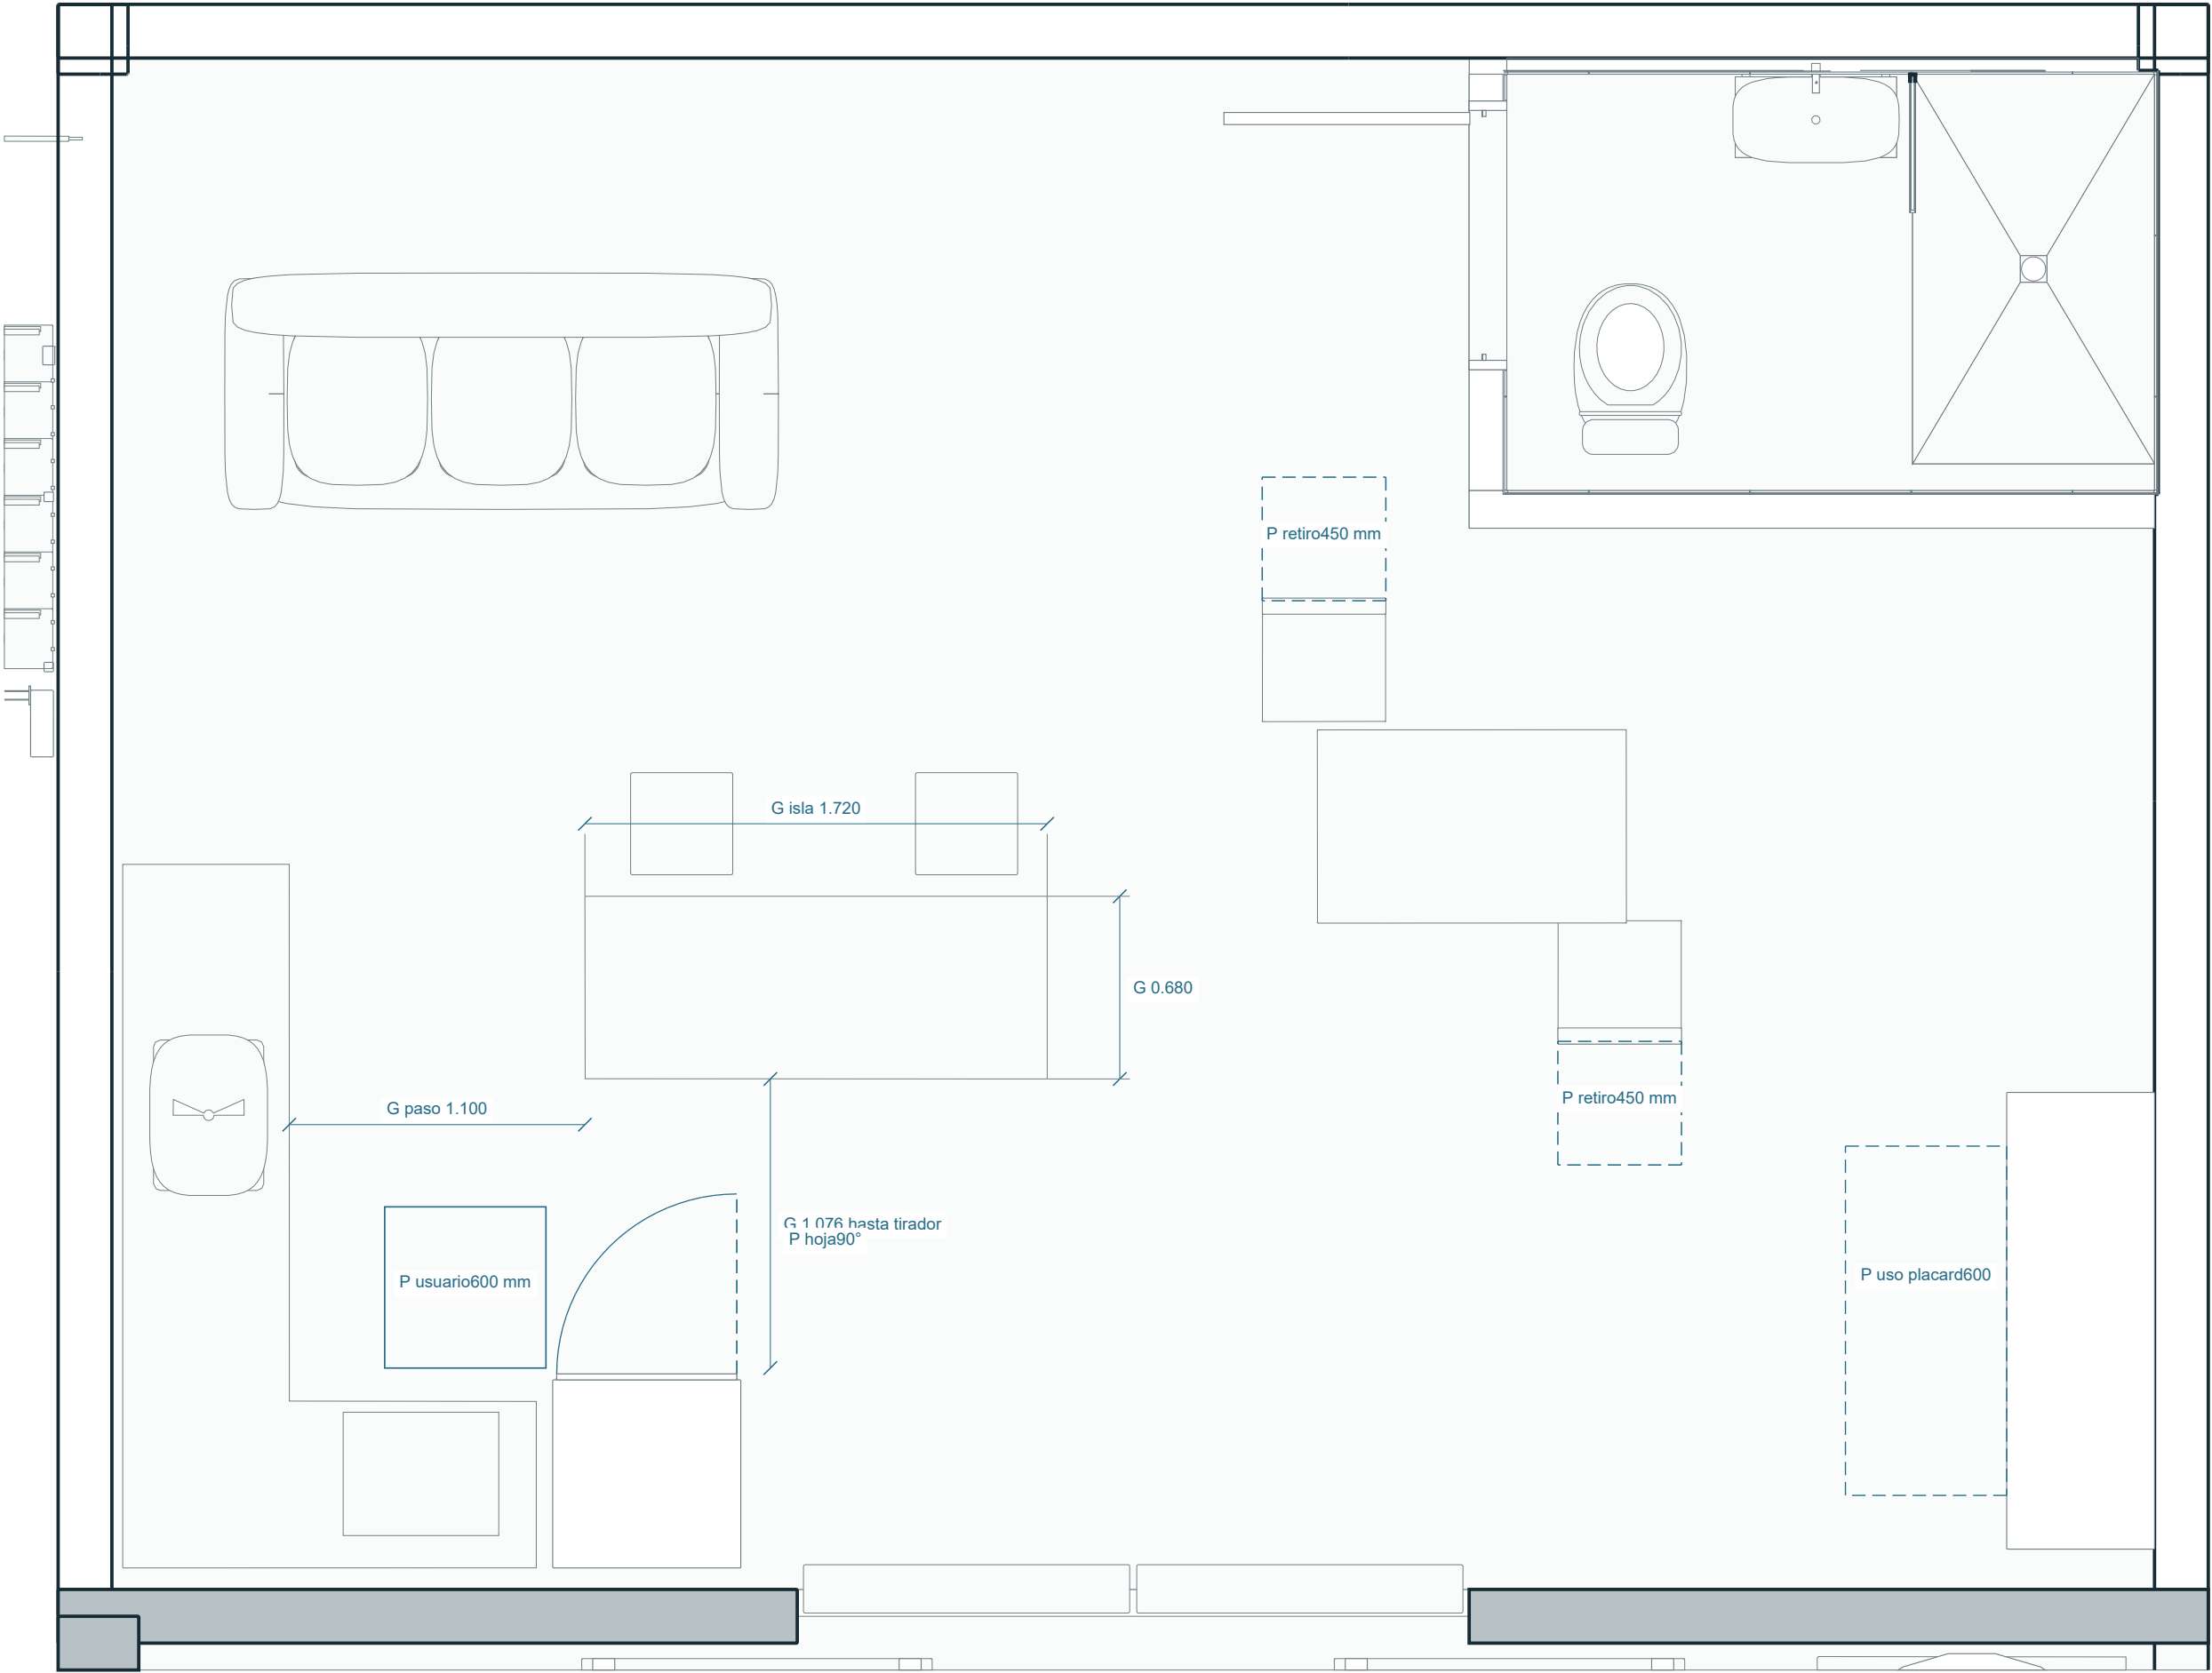

G: cotas tomadas del modelo, incluyendo el tirador que reduce el paso a la heladera. P: huella de uso y criterios de coordinacion. No se sustituyen medidas por dimensiones nominales de catalogo.

Mesa / altura G	0.750 m
Asiento silla / G	0.460 m
Mesada-isla / G	0.900 m
Piso terminado / G	+0,210 m
Paso hasta tirador / G	1.076 m

ALCANCE DE LAS HUELLAS P


P: usuario600 mm al lado del barrido de heladera y hoja abierta90° con eje derecho propuesto por tirador izquierdo. La seleccion del equipo debe confirmar mano, carrera y acceso.

G: posicion de muebles y sanitarios del modelo. P: retiro450 mm de ambas sillas en trazo discontinuo; no es pose guardada. A09 y D11 amplian los banos.


Herrajes, electrodomesticos y muebles no tienen marca/producto confirmados. G documenta geometria, no conformidad del producto o accesibilidad.

Las dimensiones de obra, espesores y servicios necesitan replanteo y proyecto ejecutivo segun jurisdiccion.


02 Mesa y sillas / elevacion G | 1:20

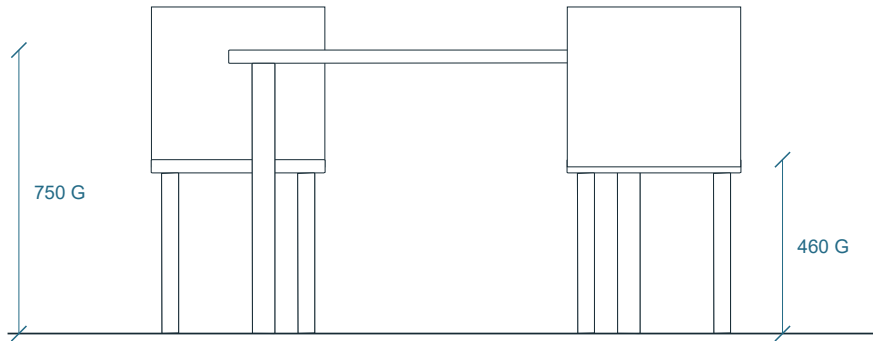

03 Mesada / Z3,60 | 1:20

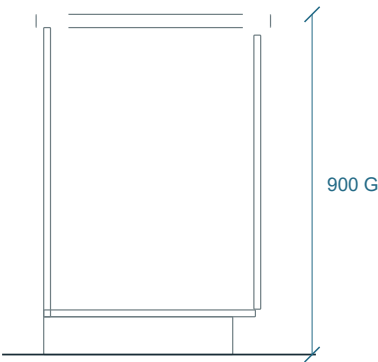

Alturas G sobre NPT +0,21. Aparatos y muebles genericos; sin producto ni capacidad certificados.

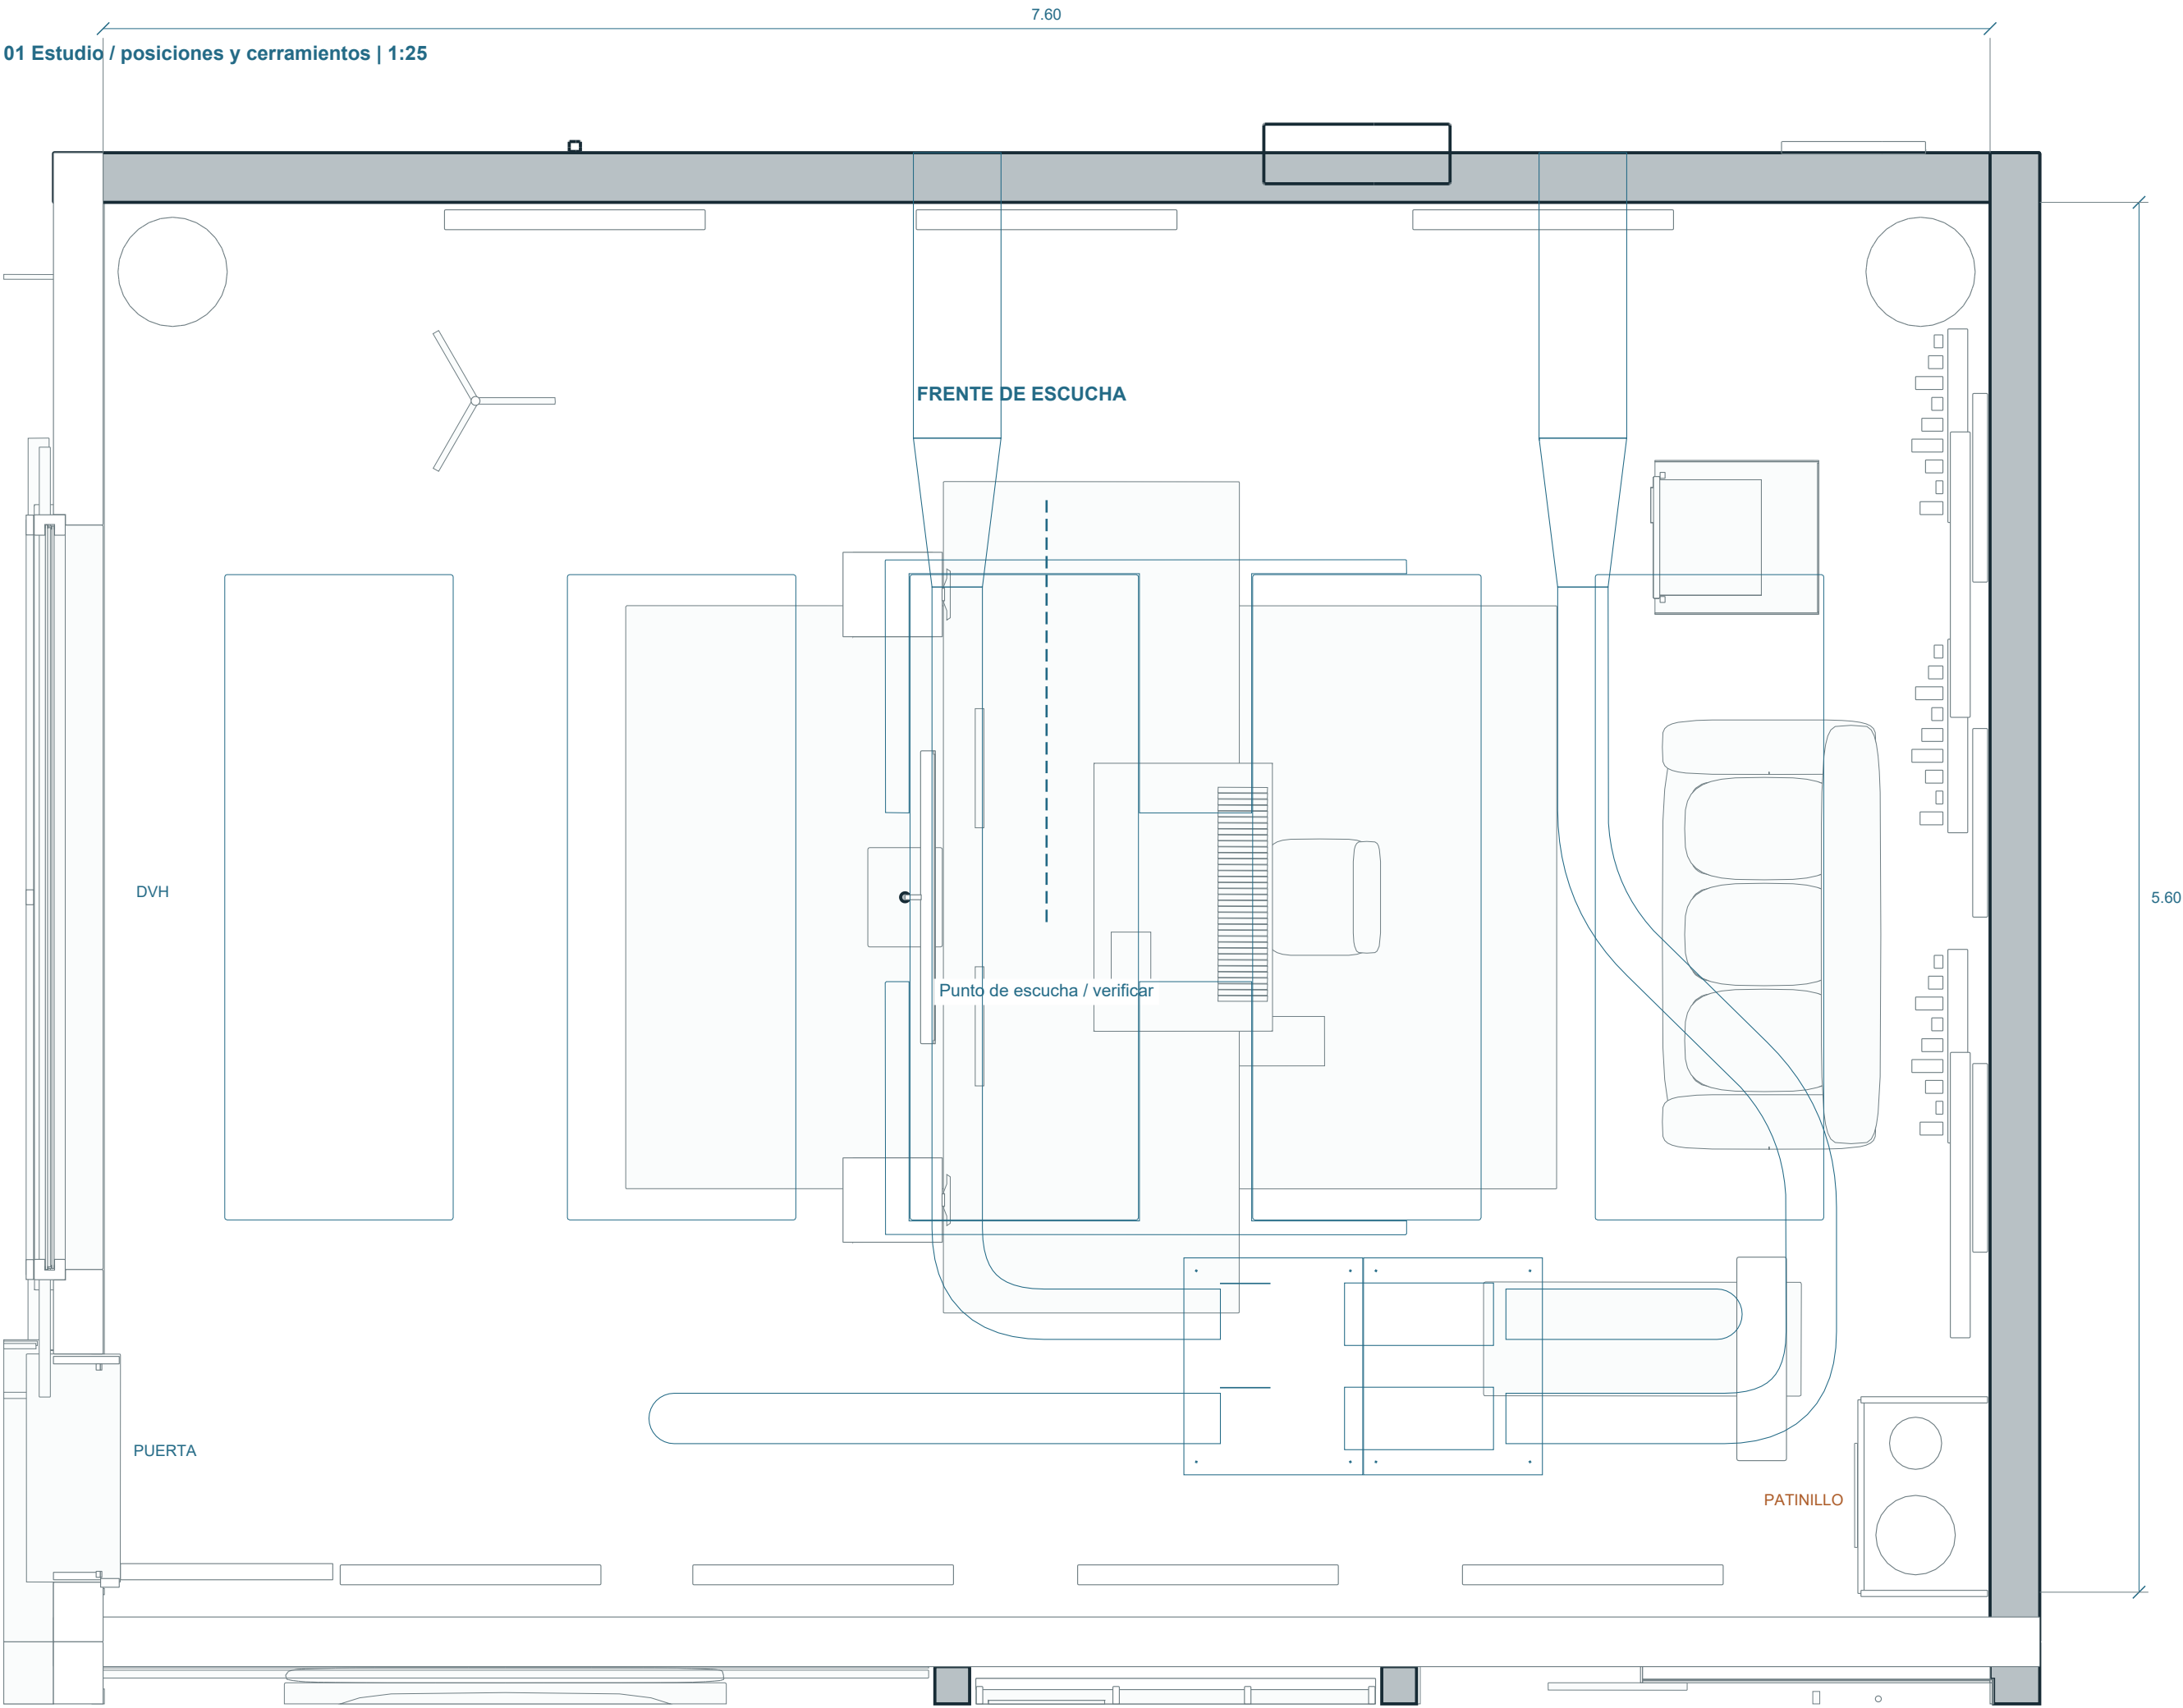

CRITERIO ACUSTICO PROPUESTO

- G: altura libre 3,20 m; cielorraso a +6,45. Paneles y nubes seccionados/coordinados con esa cota.
- P: identificar primeras reflexiones con posicion final de monitores y oidos. El trazado de escucha es una referencia grafica, no un calculo acustico.
- P: montaje dimensional, cierre hermetico y ventilacion en suplemento D06-D08; aislamiento, RT60 y ruido de fondo requieren calculo/medicion.
- P: sellado perimetral continuo en puerta, DVH y pasos; juntas elasticas y desacople donde el sistema constructivo lo requiera.
- P modelado:2 circuitos con filtros, ventiladores, silenciadores600 y ductosØ150; pasos frontales300x80. Registro1,40x0,83 y accesorios desde+6,453. D08 muestra montaje y retirada.
- P: patinillo de combustion: definir proteccion termica, separacion, juntas y acceso de limpieza sin comprometer el estudio.

VERIFICACION PENDIENTE

Medicion o simulacion acustica con absorcion real de materiales, volumen util, posiciones definitivas y ruido de instalaciones. No se asignan valores de dB ni tiempos de reverberacion sin evidencia.

Ref.	Pieza medida G	Ancho m	Alto m	Base	Tope
P01i	Corredera PB / vidrio	1.140	2.300	+0.270	+2.570
P01d	Corredera PB / vidrio	1.140	2.300	+0.270	+2.570
P02	Abatible bano mono	0.915	2.200	+0.220	+2.420
P03	Abatible bano piletá	0.820	2.180	+0.210	+2.390
P04	Acceso estudio	0.855	2.340	+3.260	+5.600
P05	Dormitorio / estar	0.908	2.200	+3.260	+5.460
P06	Dormitorio	0.820	2.170	+3.260	+5.430
P07	Bano vivienda	0.820	2.180	+3.250	+5.430
V01	DVH estudio / paño	3.000	1.720	+4.060	+5.780
V02	Lateral dormitorio / paño	1.700	2.080	+3.840	+5.920
P08a	Corredera lateral A / vidrio	1.150	2.540	+3.220	+5.760
P08b	Corredera lateral B / vidrio	1.150	2.540	+3.220	+5.760
P09	Corredera posterior A / vidrio	1.275	2.540	+3.220	+5.760
P10	Corredera posterior B / vidrio	1.675	2.540	+3.220	+5.760
H01	Porton / hoja	3.000	2.000	+0.085	+2.085
P11	Corredera bano/comedor	1.050	2.240	+3.260	+5.500

LECTURA DEL CUADRO

Dimensiones de hoja o vidrio; no equivalen al vano. P11: luz entre jambas0,90; hoja1,05 y carrera1,02; ver A09 / suplemento D09.

G: P05 vano1000, hoja908, marco923mm; garganta848mm y paso conservador806mm con manija a90°. P02 vano1000 / marco930mm.

G: DVH con dos paños de vidrio; espesor y separacion segun modelo. Prestaciones y composicion final por especificar.

P08/P09/P10: correderas vivienda; replantear rieles, solapes, desagues y retenedores a partir del vano real.

Porton: hoja 3,00 m; paso libre 2,75 m; carrera 3,05 m. Paso medido entre caras de pilares.

01 P05 / jambas y hoja cerrada G | 1:10

Hoja908 x45 G; apertura en A03



923 G entre jambas

806 G conservador

HERRERIA Y PROTECCION

F: baranda nominal 1,05 m sobre nivel de balcon. G: eje pasamanos lateral +4.30; NPT alto +3.25; diferencia 1.05 m. Medir altura util donde cambie el acabado.

G: postes, barrotes y zancas representados. Separacion de barrotes, resistencia horizontal, soldaduras, placas y anclajes requieren validacion de proyecto.

Escalera: 18 tablas de 1,00 m; avance entre tablas ~211,1 mm. A07 muestra el recorrido y el encuentro de acceso; A14 las piezas de soporte.


Pendiente: cuadro de fabricacion definitivo con materiales, espesores, tratamientos, sellos, drenajes, tolerancias y accesorios del fabricante.

02 Cierre vestidor-estar / corte G | 1:10



Sin puerta ni paso al estar


01/A13 Alero estudio / X=17,80 | 1:5

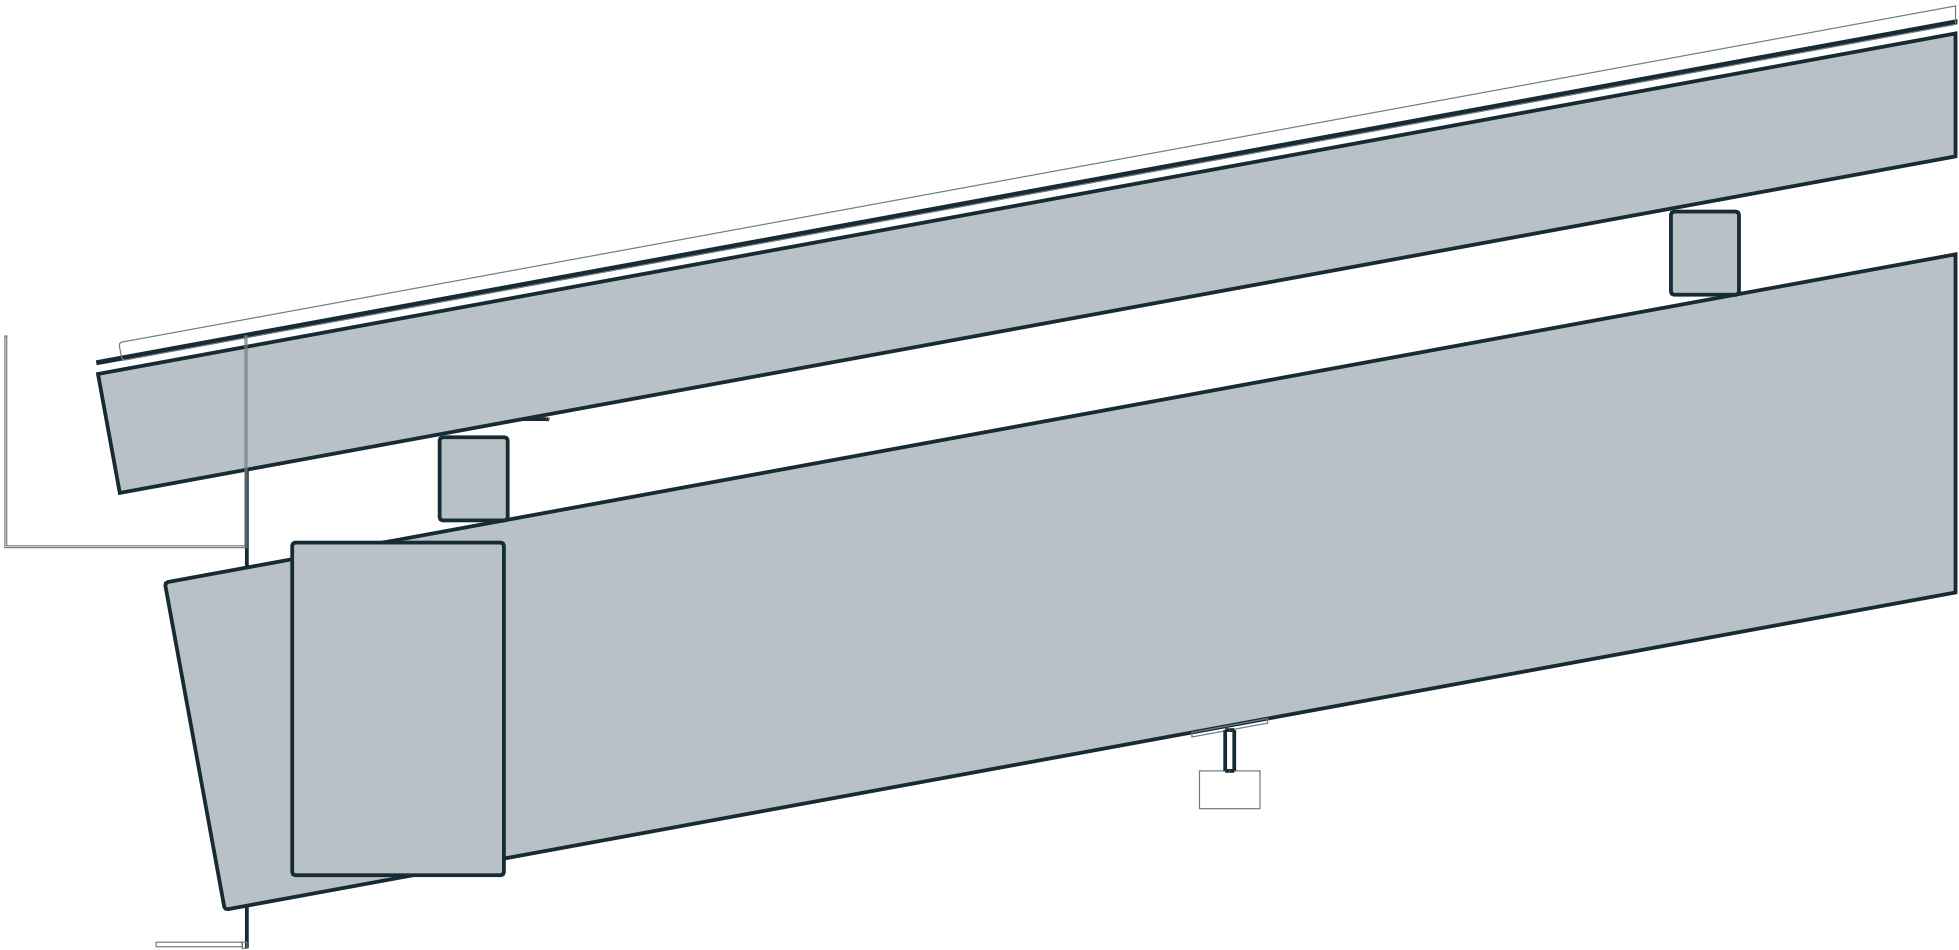

CAPAS Y GESTION DEL AGUA

- G: cubierta metalica, aislacion representada de 80 mm, revestimiento inferior y cabios/correas. La seccion corta las piezas de la malla a su escala real.
- G: chapa nominal0,8 mm. Suplemento D01 propone capas, goteron, solape150 y fijaciones selladas; compatibilidad y resistencia por verificar.
- P: babeta/contrababeta del salto, retorno de membrana y sellos alrededor de conductos desarrollados en suplemento D02; verificar frente a exposicion real.
- P: validar condensacion, viento, dilatacion y puentes termicos con datos climaticos y especificaciones definitivas.


02/A13 Escalon cubiertas / X=17,80 | 1:5

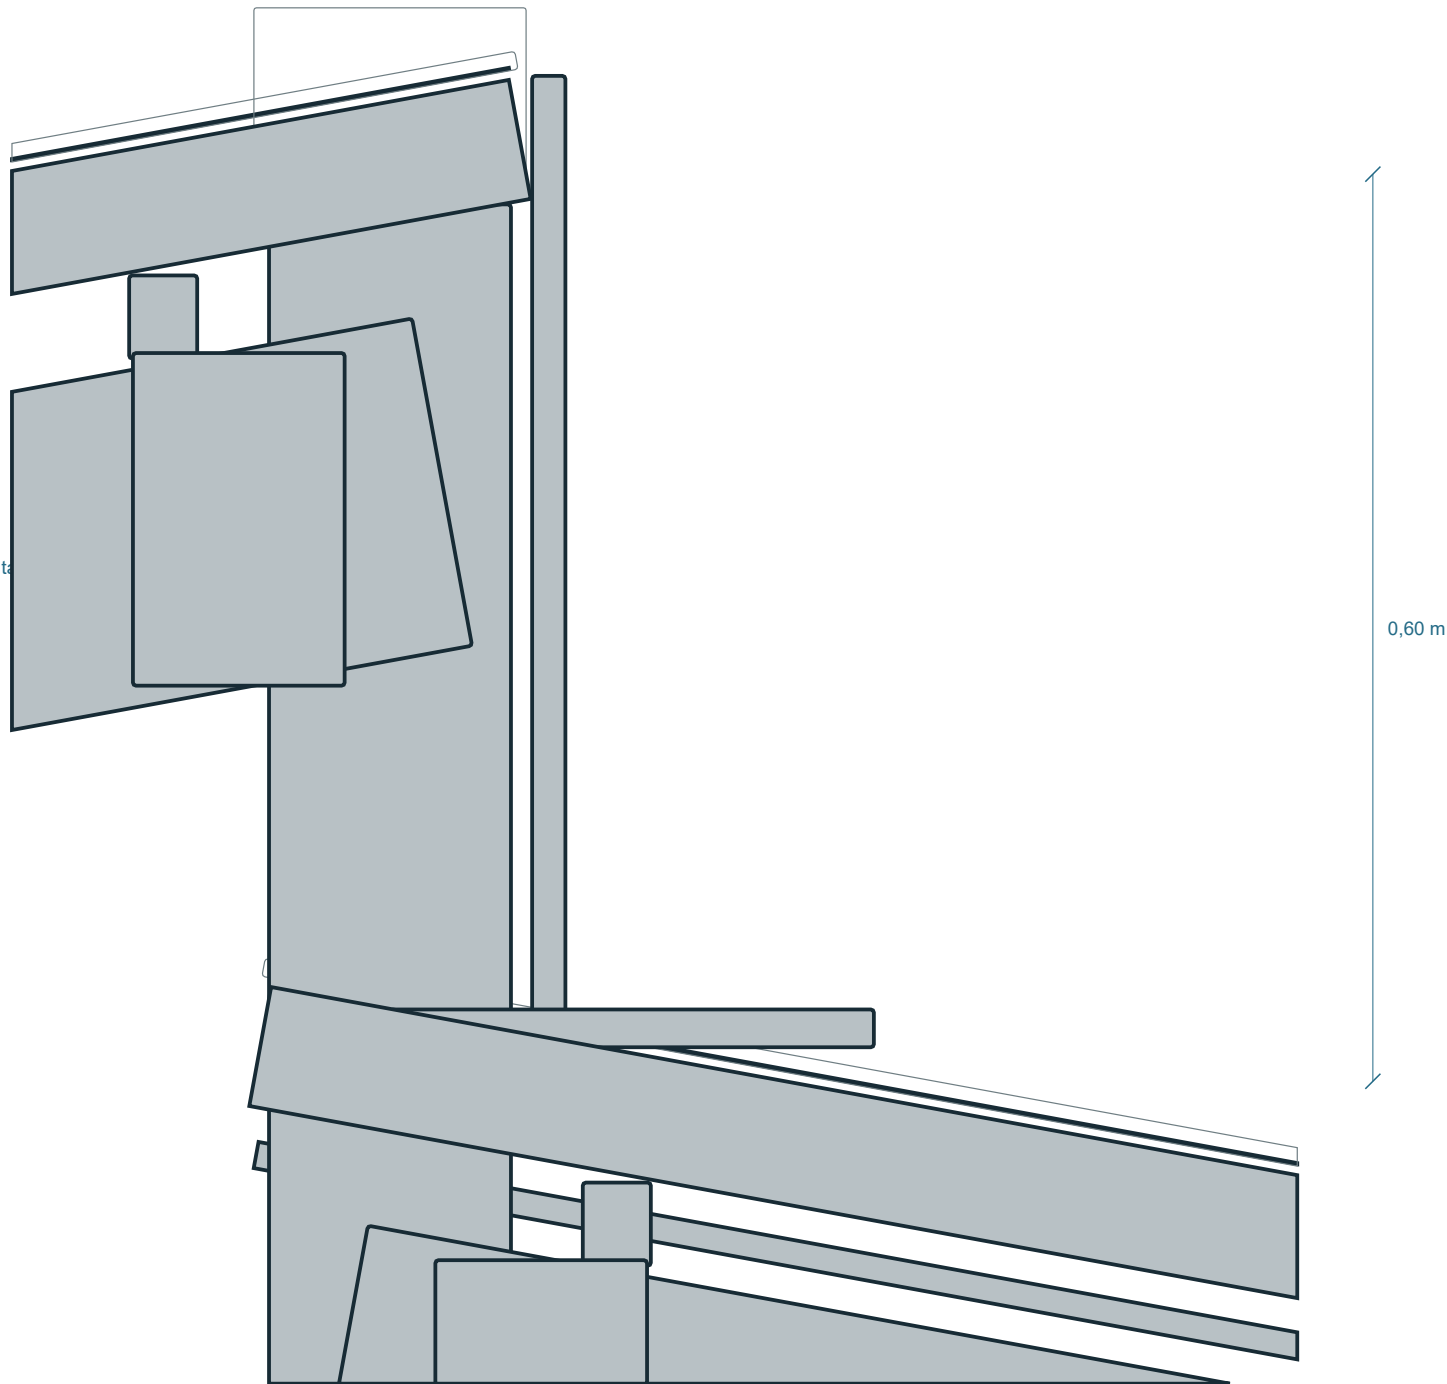

DVH, UMBRALES Y BALCON

- Encuentros generales: A07, A14 y A13b. Suplemento D01-D04 desarrolla capas, solapes, sellos y anclajes con cotas en mm.
- P: junta perimetral con respaldo y sello compatible; apoyo y calzos de vidrio, drenaje del marco, continuidad de aislacion e impermeabilizacion.
- El suplemento distingue las piezas G de las propuestas P; las especificaciones finales dependen del sistema y fabricante seleccionados.

05/A13b Canaleta abierta / X=14,00 | 1:2

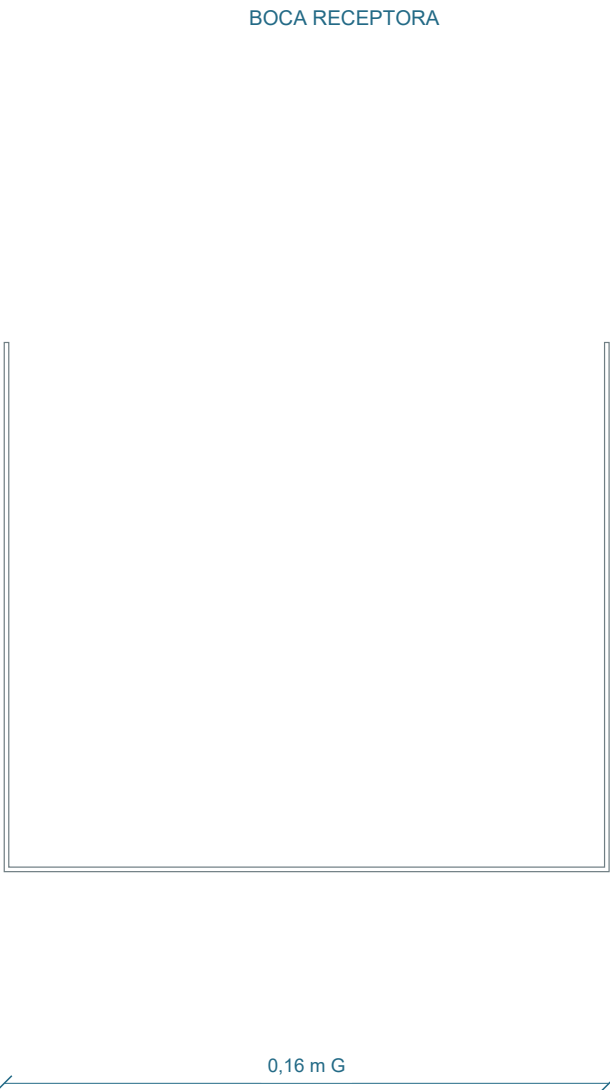


05/A13b CAPTACION / FIJACION

G: seccion de canaleta recortada directamente de la malla. Verificar apertura superior, fondo, salida lateral y continuidad en la prueba del modelo.

P: pendiente longitudinal, caudal, fijacion y sellos requieren dimensionado; el ancho grafico no certifica capacidad pluvial.

06/A13b DVH / antepecho / Z=3,00 | 1:5

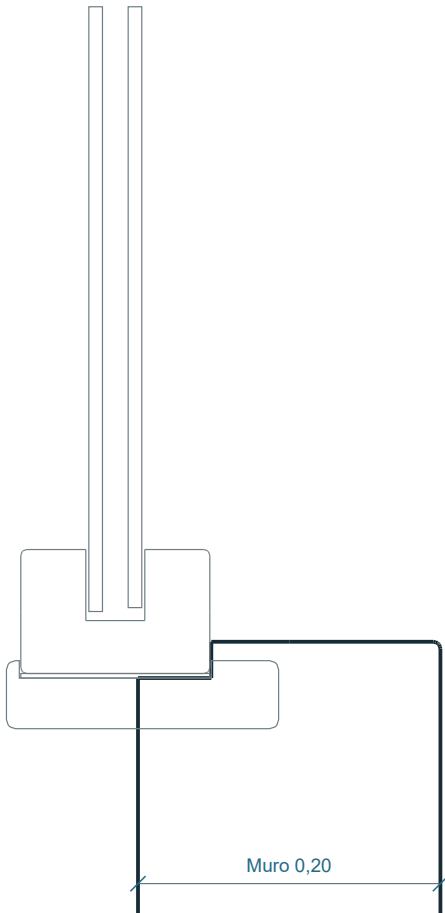


06/A13b ENCUENTRO DE VENTANA

G: dos paños, marco, antepecho y alféizar representados. La ampliacion permite revisar solapes y contacto.

P: apoyo, sellos, drenaje del marco y conexion de aislacion desarrollados a1:5 en suplemento D03.

Ver A12 para anchos, alturas y cotas de cada pieza.

07/A13b Paso de conductos / X=21,50 | 1:5

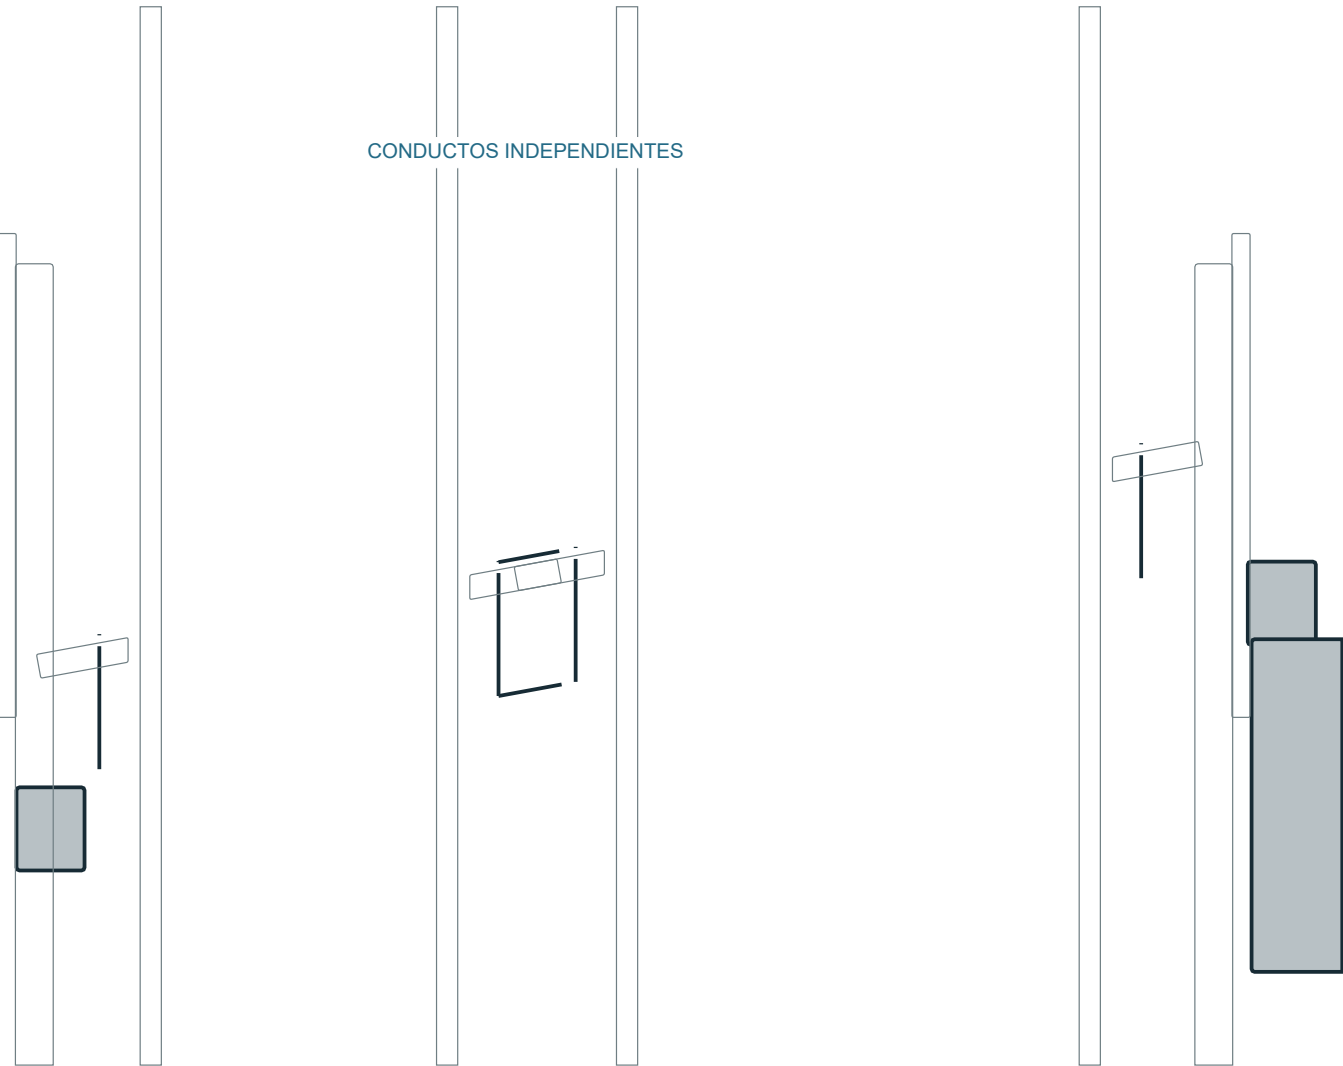


07/A13b PENETRACION / PATINILLO

G: conductos independientes, babetas perforadas y remate de patinillo. Se muestra la interseccion con cubierta.

P: continuidad de membrana, cuello y contrababetas, dilataciones, aislamiento termico y acceso de limpieza por especificar.

No se asignan distancias reglamentarias a combustibles ni caudales sin proyecto de combustion.


01 Planta de apoyos y líneas estructurales | 1:50

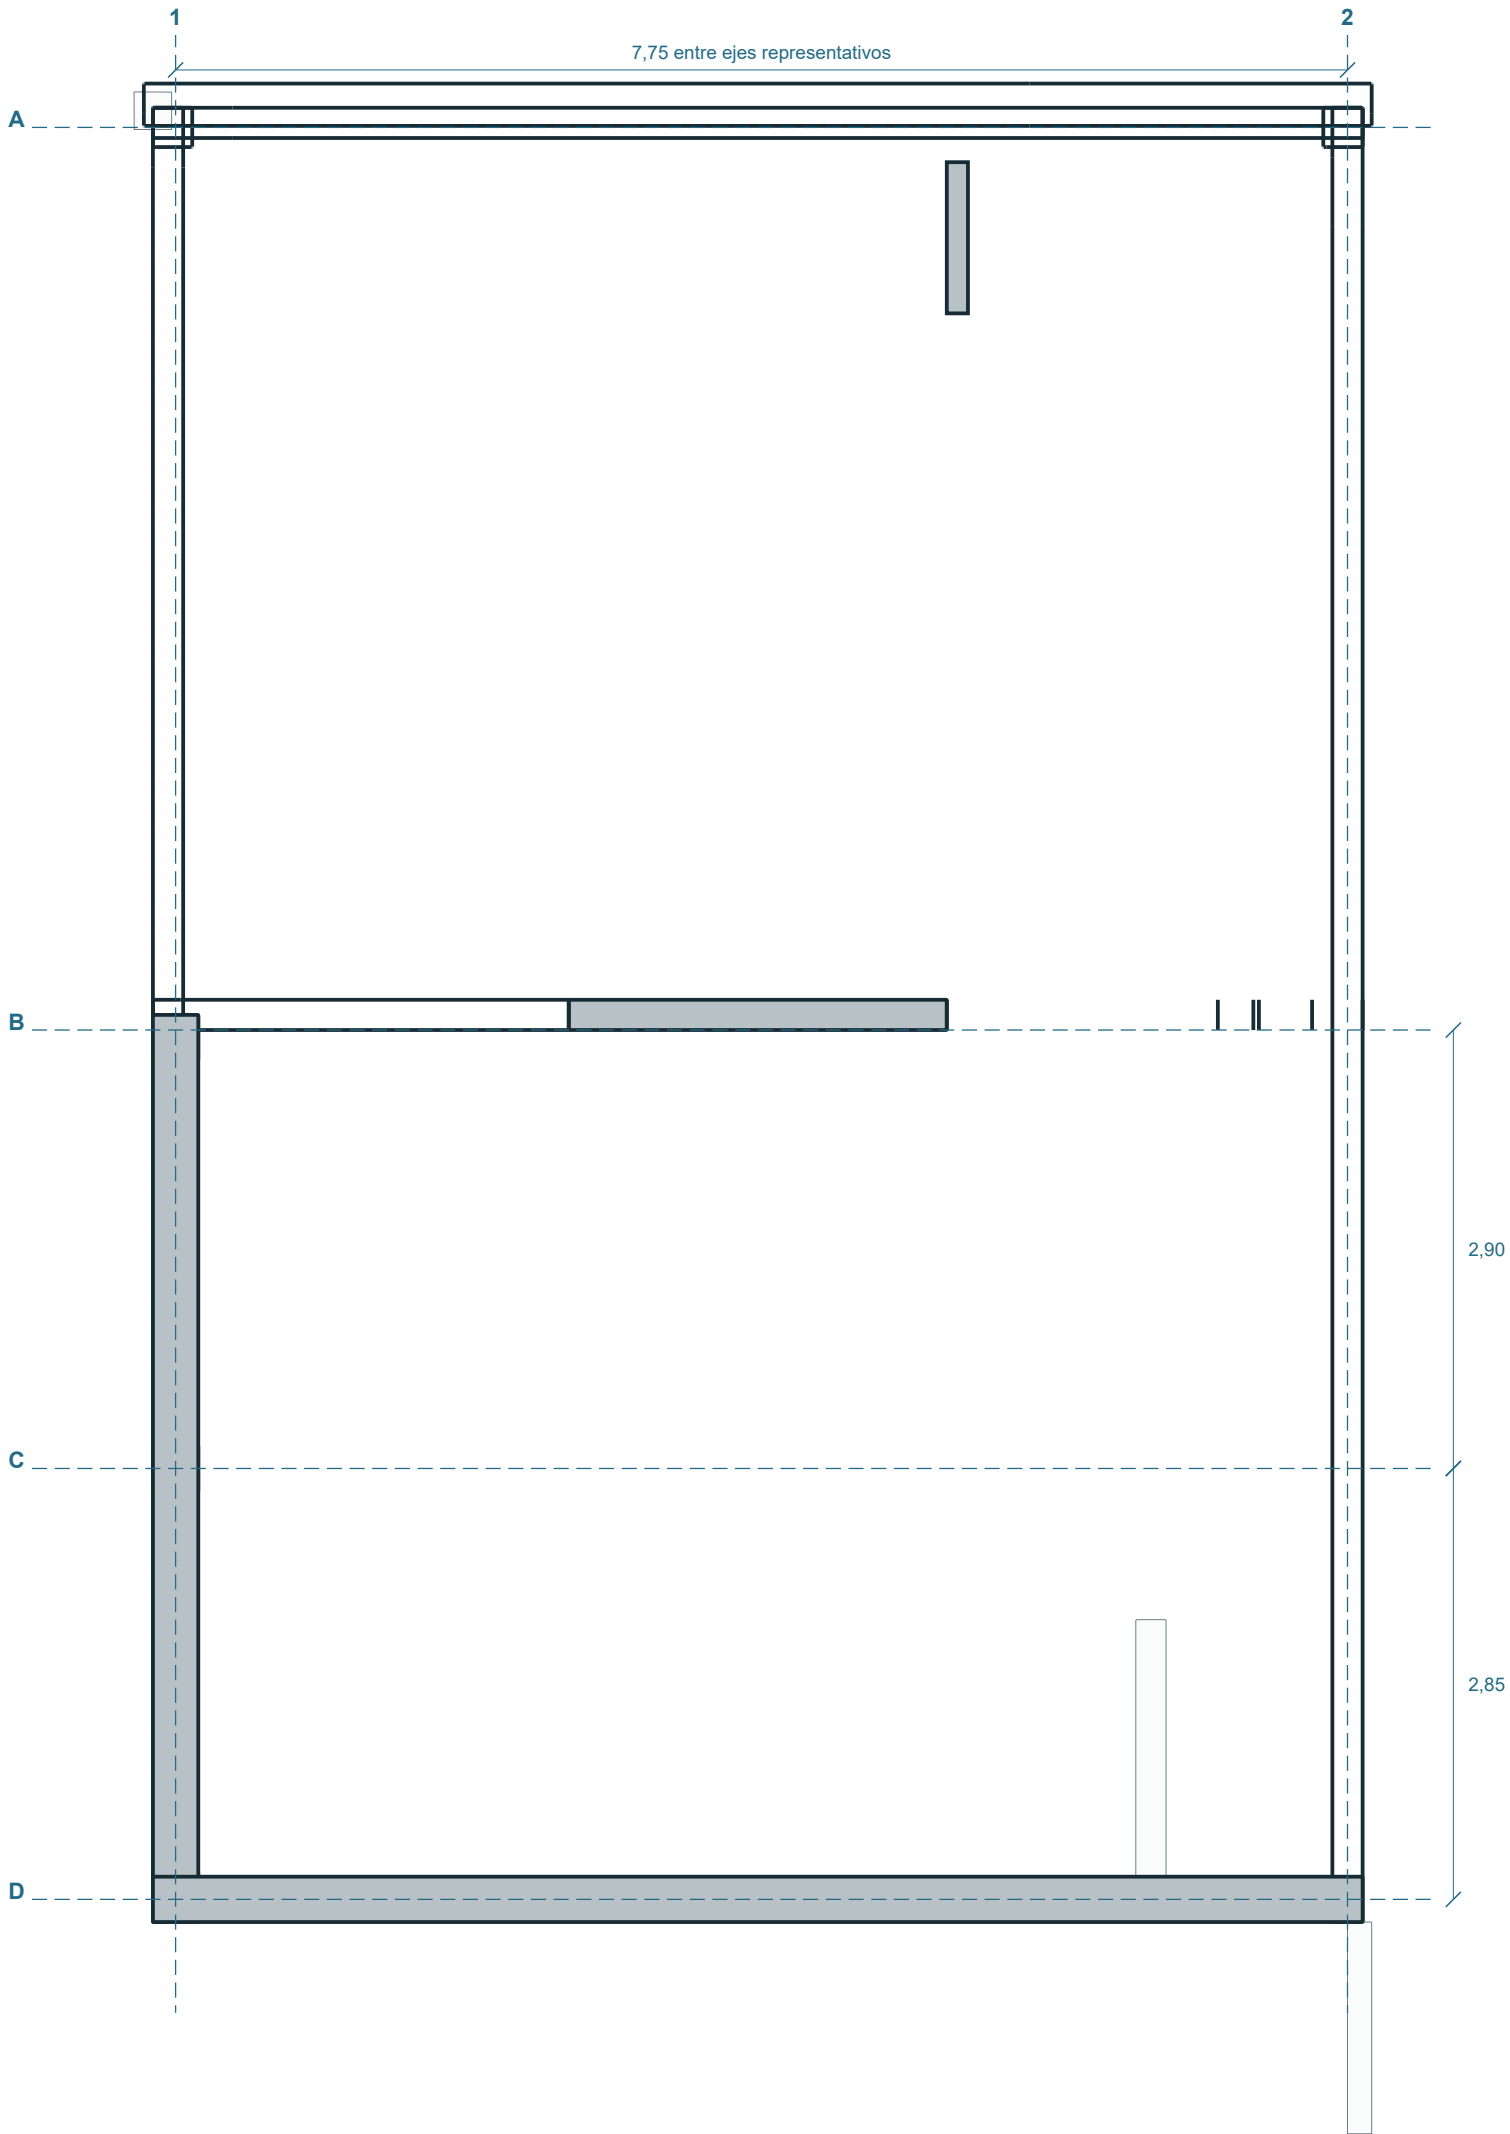

CAMINO DE CARGAS A VALIDAR

- Cubierta: chapa / aislacion -> correas -> cabios -> vigas de apoyo -> cerramientos / apoyos inferiores.
- Entrepiso: losa de 0,20 m -> muros y vigas / columnas representados -> fundacion por proyectar.
- Quincho: columnas 0,30 x 0,30 m y vigas de 0,30 x 0,36 m representadas. Son secciones de malla, no un dimensionado estructural.
- Balcones: proyeccion 1,00 m; verificar voladizo, continuidad y anclaje con la losa. No se infieren armaduras.
- Escalera: dos zancas; suplemento D05 dibuja cartelas, bulones y apoyo inferior P. Barandas: D04 muestra placas/anclajes G; capacidad pendiente.
- Fundaciones ausentes de la fuente: tipo, profundidad, armaduras y capacidad del terreno pendientes de estudio geotecnico y proyecto profesional.


04/A14 Balcon / baranda / Z=9,00 | 1:20

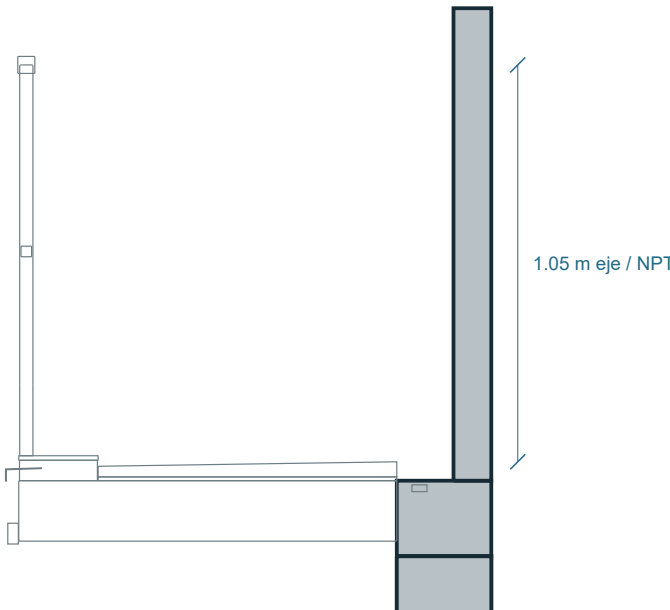

UNIONES

- El corte documenta las piezas presentes y sus apoyos aparentes.
- Los anclajes no se consideran resueltos por estar dibujados: validar sustrato, borde, profundidad y solicitudes.
- Acero/hormigon: especificar corrosion, drenajes y juntas.

01 Coordinacion general / PB | 1:100

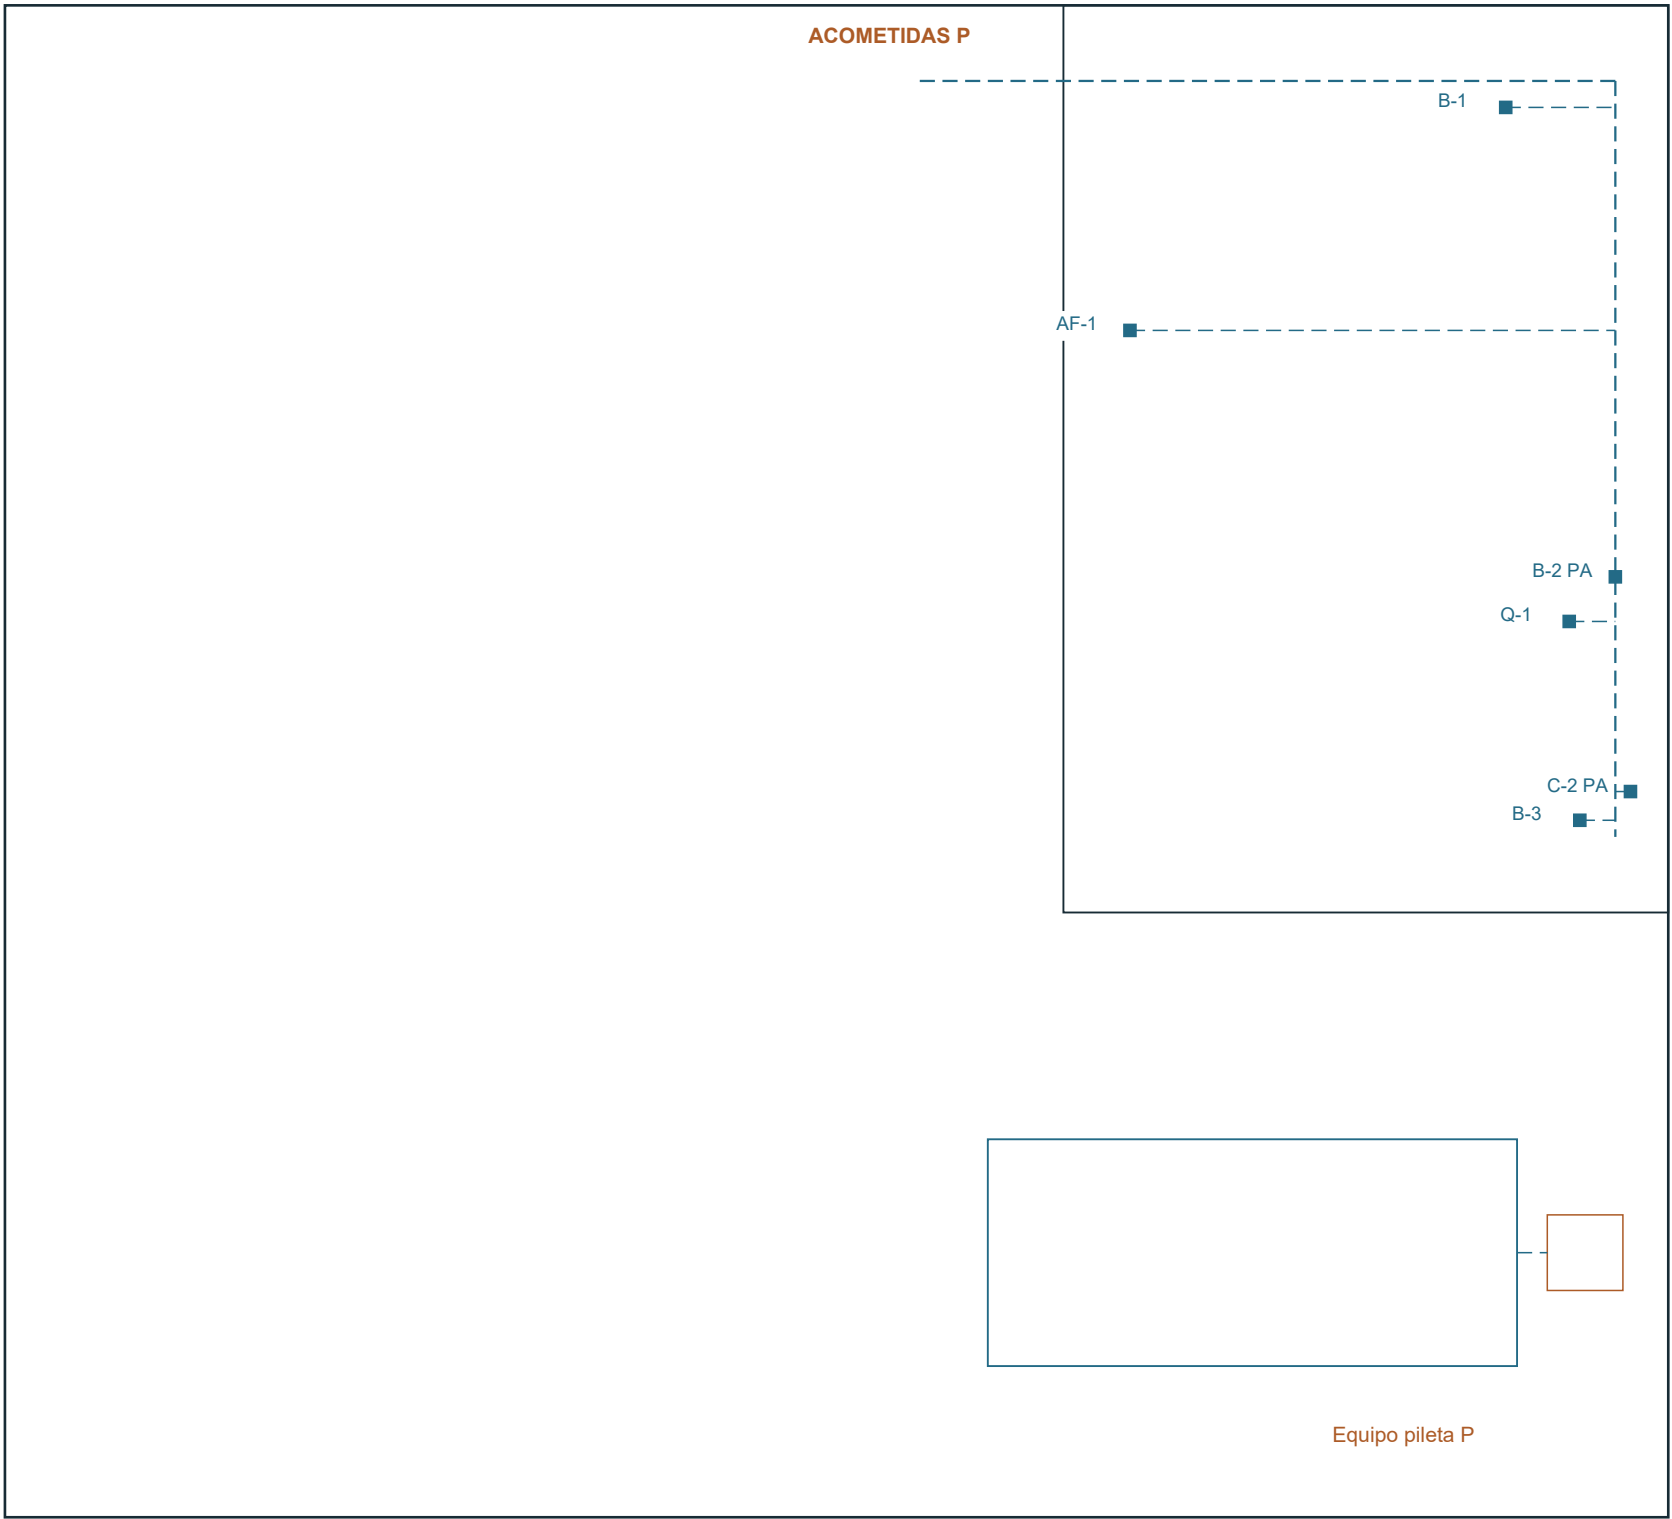

CRITERIO DE COORDINACION: localizar consumos y cruces antes de dimensionar redes. Sin cotas de servicio ni calculos no se presenta este esquema como instalacion completa o certificada.

AGUA / DESAGUE / PLUVIAL

AF-1 cocina mono; B-1 bano mono; Q-1 quincho; B-3 bano pileta; B-2 bano PA; C-2 cocina PA. Nodos sobre equipos reales del modelo.

Las líneas punteadas son relaciones funcionales, no tuberías ejecutivas. Recorridos, diámetros, pendientes, ventilaciones, registros y acometidas se definen con el proyecto sanitario.

Pluvial: captacion y bajadas en A04. Destino final de descarga propuesto; red y cota de conexion exactas pendientes.

Pileta P: skimmer / toma de fondo -> prefiltro / bomba -> filtro -> retornos. Prever valvulas, vaciado, renovacion y medidas de seguridad; equipo y tuberias por calcular.

ELECTRICIDAD / ILUMINACION / EXTRACCION

Servicios de red disponibles segun propietario. Tablero y medidor propuestos junto al acceso; ubicacion final segun prestador.

P: separar circuitos de iluminacion, tomas generales, cocinas, pileta y estudio. Definir potencias, protecciones, puesta a tierra y equipotencialidad.

G: luminarias representadas no equivalen a calculo luminotecnico ni conexion electrica.

G: conductos de horno, parrilla y cocina presentes. Ver A10: caudal, limpieza, aislamiento y reposicion de aire pendientes.

P modelado: D08 representa impulsion y extraccion independientes con soportes a cabios, registro, filtros y terminales separados2,52m. Caudales, productos y prestaciones pendientes.

Area / pieza	m2	Metodo / alcance
Lote nominal F	440.00	22,00 x 20,00; limites nominales
Huella casa F	96.00	8,00 x 12,00; incluye quincho
Dos niveles nominales F	192.00	192 m2 brutos geometricos; no computo legal
Vaso pileta F	21.00	7,00 x 3,00 nominal
Borde pavimentado F	24.00	Anillo de 1,00 m nominal
Piso estudio G	41.74	Proyeccion real de la pieza; puede solapar otras
Piso vivienda G	36.13	Proyeccion real de la pieza; puede solapar otras
Piso monoambiente G	38.86	Proyeccion real de la pieza; puede solapar otras
Piso baño mono G	2.42	Proyeccion real de la pieza; puede solapar otras
Piso baño vivienda G	5.61	Proyeccion real de la pieza; puede solapar otras
Piso quincho G	45.42	Proyeccion real de la pieza; puede solapar otras
Piso baño quincho G	1.81	Proyeccion real de la pieza; puede solapar otras
Balcón lateral G	6.00	Proyeccion real de la pieza; puede solapar otras
Balcón posterior G	8.98	Proyeccion real de la pieza; puede solapar otras
Descanso escalera G	1.00	Proyeccion real de la pieza; puede solapar otras

FUENTES Y REVISION

F: source/scene.json, configuracion y geometria original. Coordenadas fuente X / Z horizontal; Y altura. Blender X / -Z / Y.

F: docs/DECISIONES.md: estudio 3,20 m libres, vivienda 2,60 m y video pausado.

G: modelo Casa_de_Campo_99_R7D.blend; SHA256 9cf1a0e2f1b1a6063a289426...

G: extraccion de mallas evaluadas a cuadro 150, con puertas en su pose de documentacion. Los detalles omiten microgeometria menor para permitir lectura.

P: desarrollos constructivos y sistemas inferidos se identifican en sus hojas. No se presentan como verificacion profesional.

Las superficies de piezas no son utiles netas de recintos. Comprobar uniones y areas comunes antes de sumar; los pisos PB de banos se recortaron de las superficies generales.

PENDIENTES PARA EMISION FINAL

Mensura y topografia; servicios y cotas exactas; suelos; calculo de estructura, instalaciones, seguridad, clima y acustica.

Cierre de observaciones de la auditoria y coherencia con modelo / visor congelados. Umbral critico 9,9 e hiperrealismo siguen siendo condiciones de entrega.


ARCHIVOS: un PDF multipagina vectorial A2; un SVG y un DXF por lamina; geometria.json de extraccion; manifest.json de versiones; verification.json de controles. Los DXF contienen las vistas metricas separadas y cotas; la cartela completa se conserva en PDF/SVG.

G = medido / gris


P = propuesta dimensional / azul

Todas las cotas en mm salvo niveles en m

01 Alero propuesto sobre espesores G | 1:5

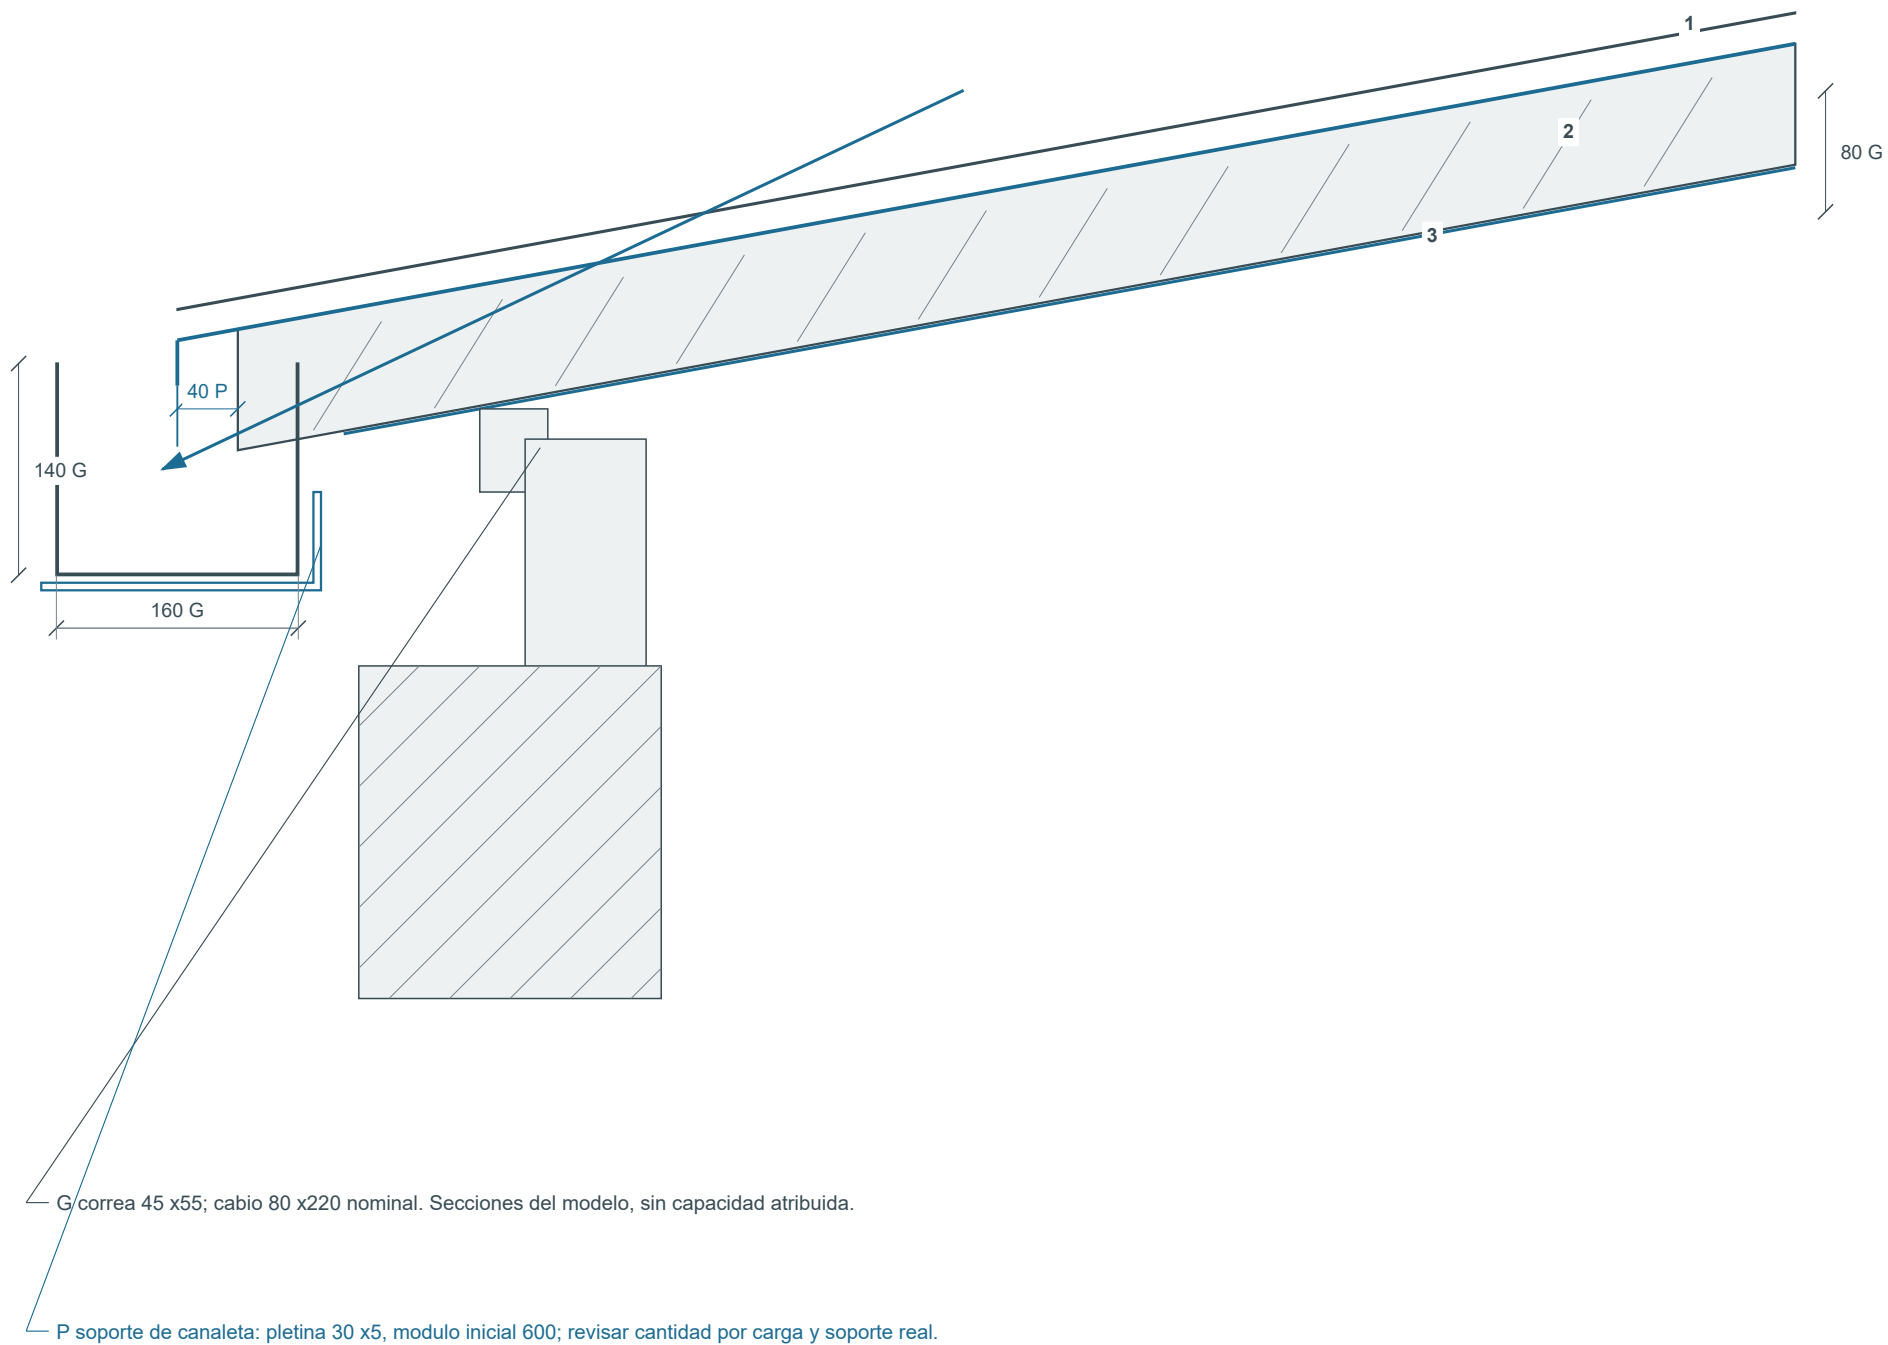

02 Solape de babetas / fijacion P | 1:5

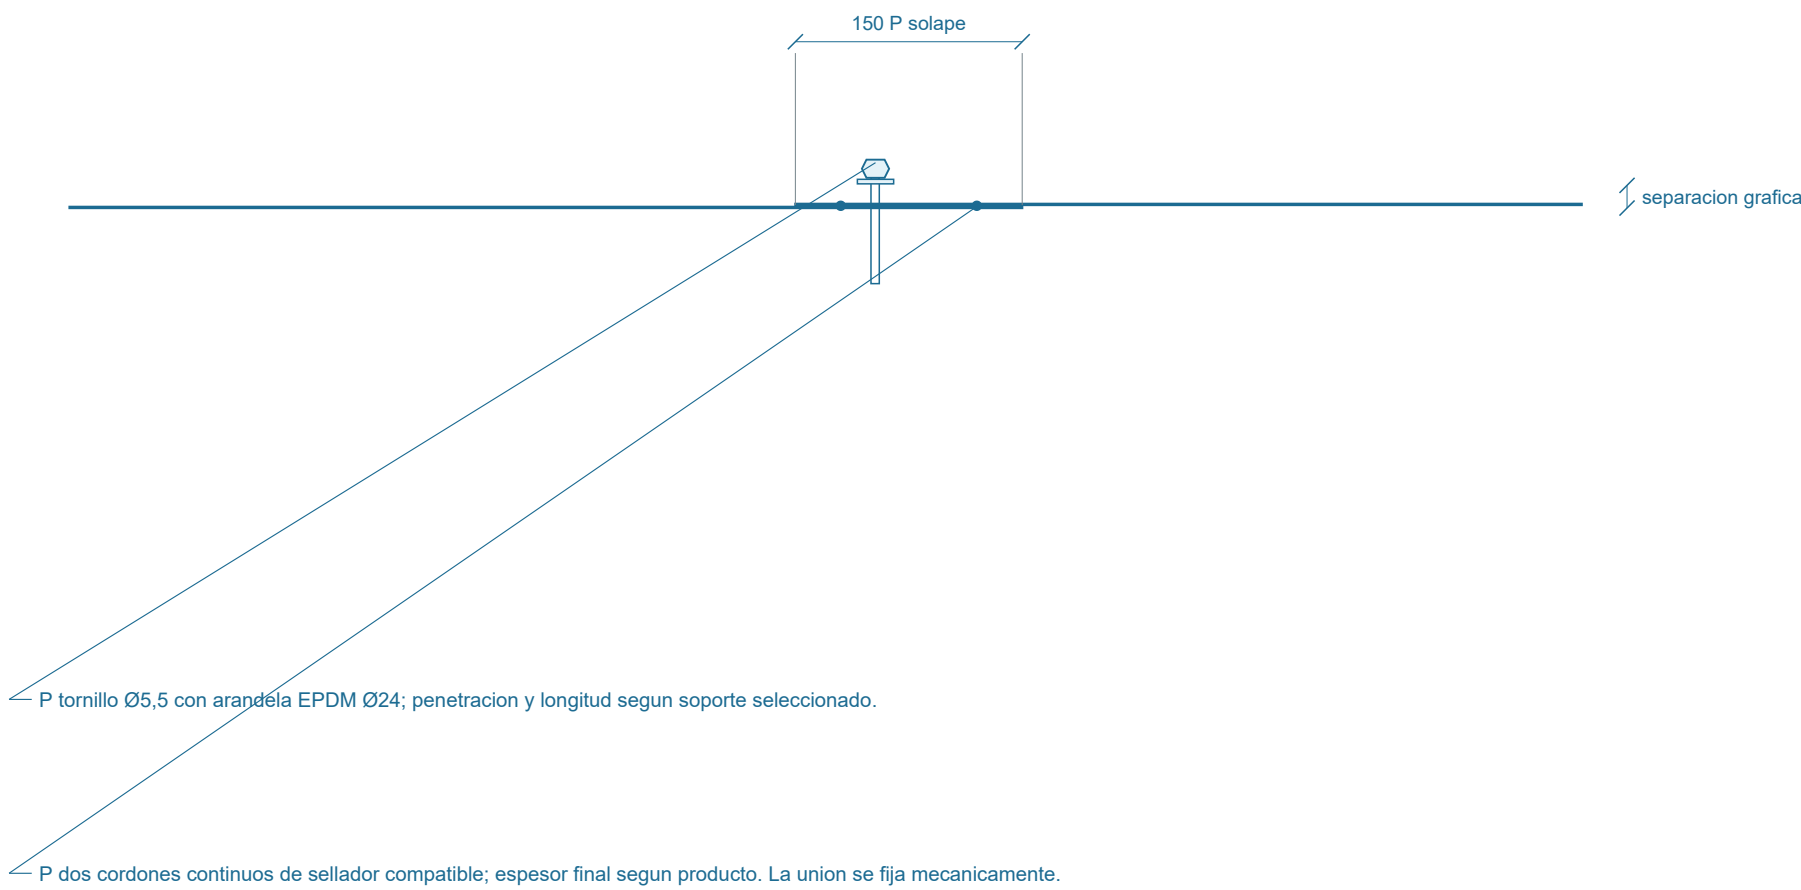

DECISION DIMENSIONAL P

Solape150 de remates; retorno20 de borde; sello neutro compatible; fijacion inicial cada300 en remate. No se traslada como tabla de fijacion de la chapa a correas

El detalle muestra orden de capas y salida del agua. Los espesores submilimetricos se dibujan con peso de linea legible, sin escalarlos como material mas grueso.

R1 | Lysaght: Roofing & Walling Installation Manual, §§7.9 y11

EN REVISION - PROPUESTAS DE COORDINACION, SIN CALCULO DE CAPACIDAD

A2 / imprimir al 100 %


Base G: Casa_de_Campo_99_R7D.blend / 9cf1a0e2f1b1a606

G acredita geometria, no capacidad. P identifica propuestas; su presencia3D no valida prestaciones

01 / 10-09-2026


G = medido / gris P = propuesta dimensional / azul Todas las cotas en mm salvo niveles en m

03 Encuentro escalonado / seccion P | 1:5

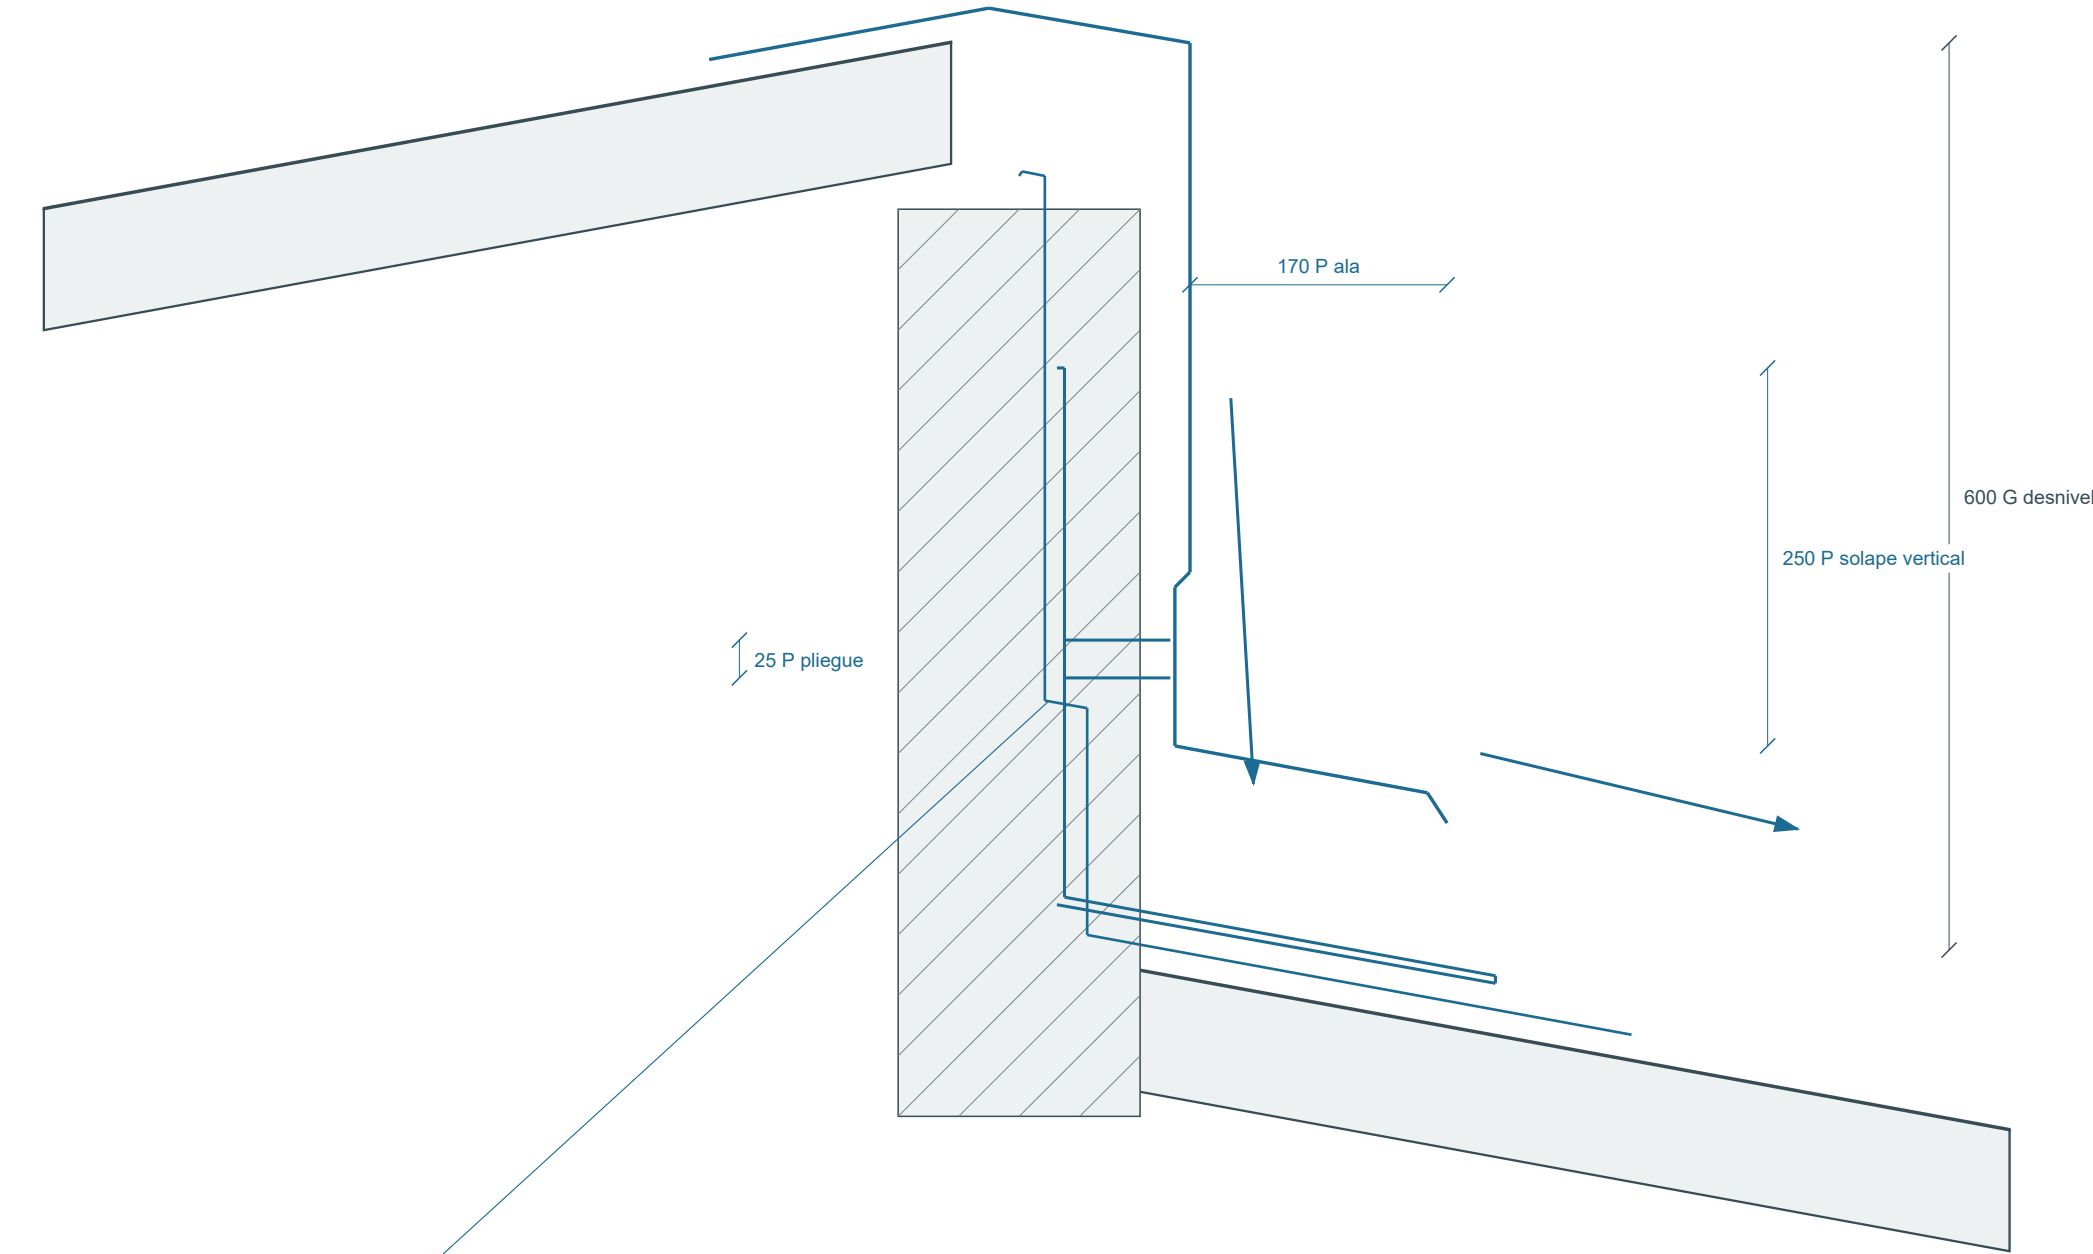

P membrana continua con pliegue flexible25; retorno vertical180 sobre faldon inferior. No puente rígido entre paños que impida dilatacion.

04 Paso de conducto / remate P | 1:5

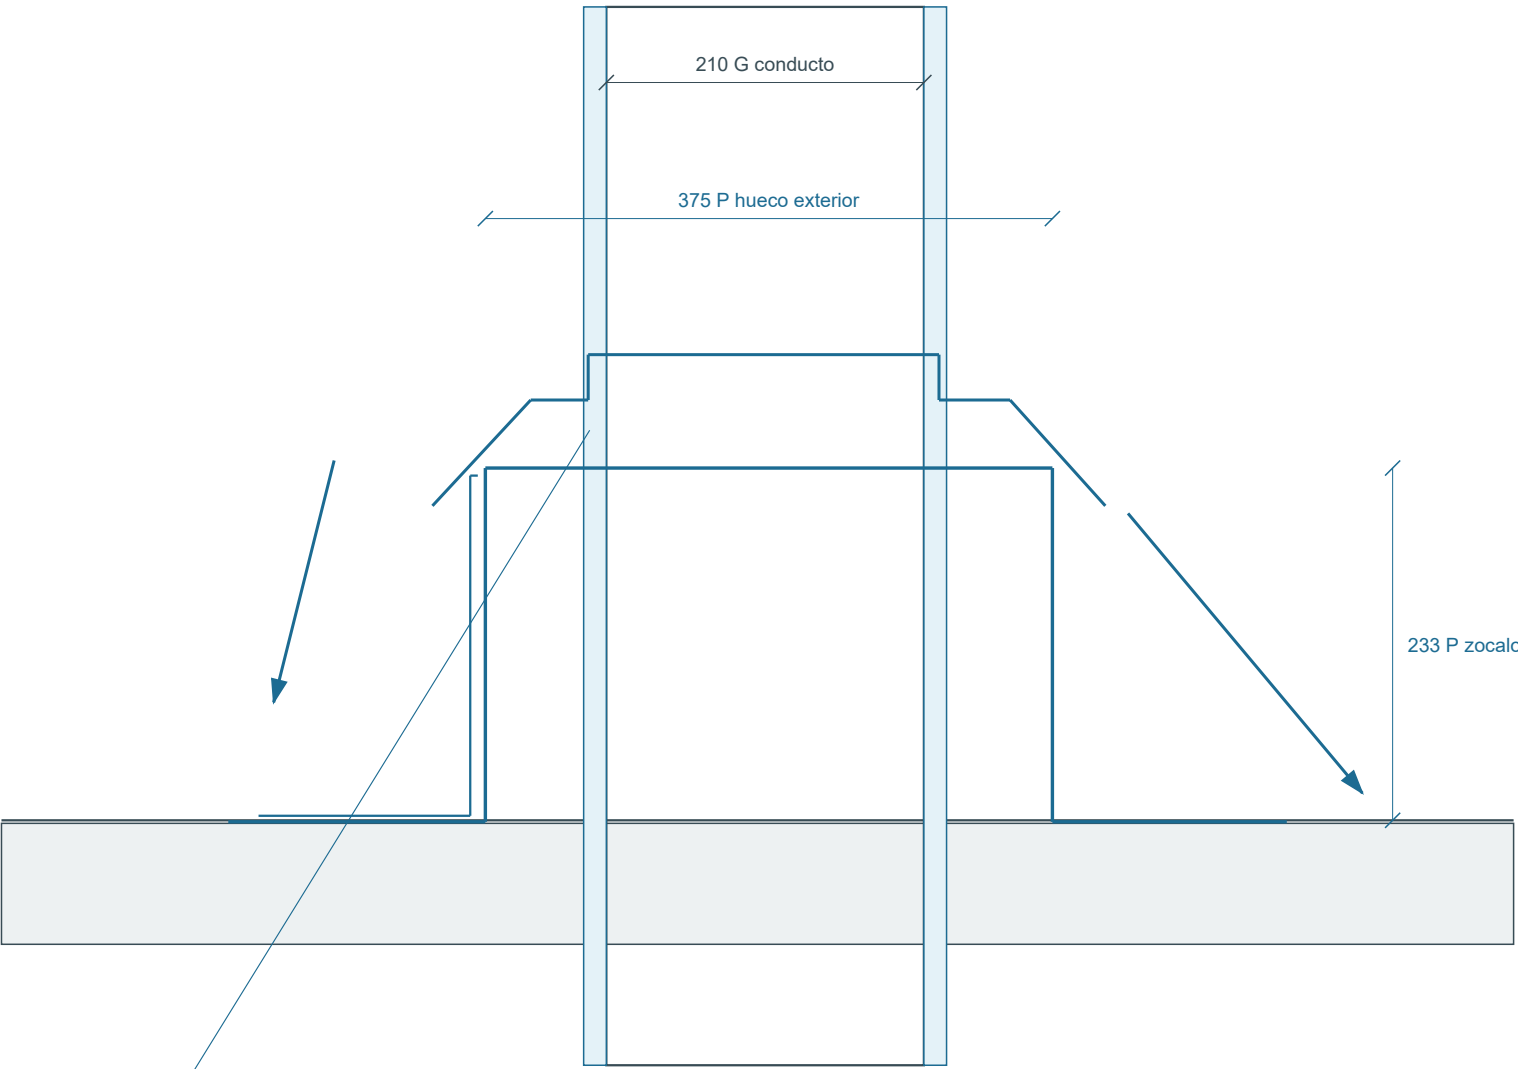

P collar partido desmontable, abrazadera y junta compatible con temperatura. Conducto aislado no queda rigidamente pegado a la babeta.

SERVICIO Y AGUA

P bandeja superior con desvio lateral; retorno200 contra cuello, solape150 en falda y goteron20. No obstruir canales del perfil.
P acceso desmontable de300 x300 al registro del patinillo. Aislamiento y distancias a combustibles requieren seleccion del sistema de combustion.


R1 | Lysaght: Roofing & Walling Installation Manual, §§7.9 y11

G = medido / gris

P = propuesta dimensional / azul

Todas las cotas en mm salvo niveles en m

05 Antepecho / corte real G | 1:2

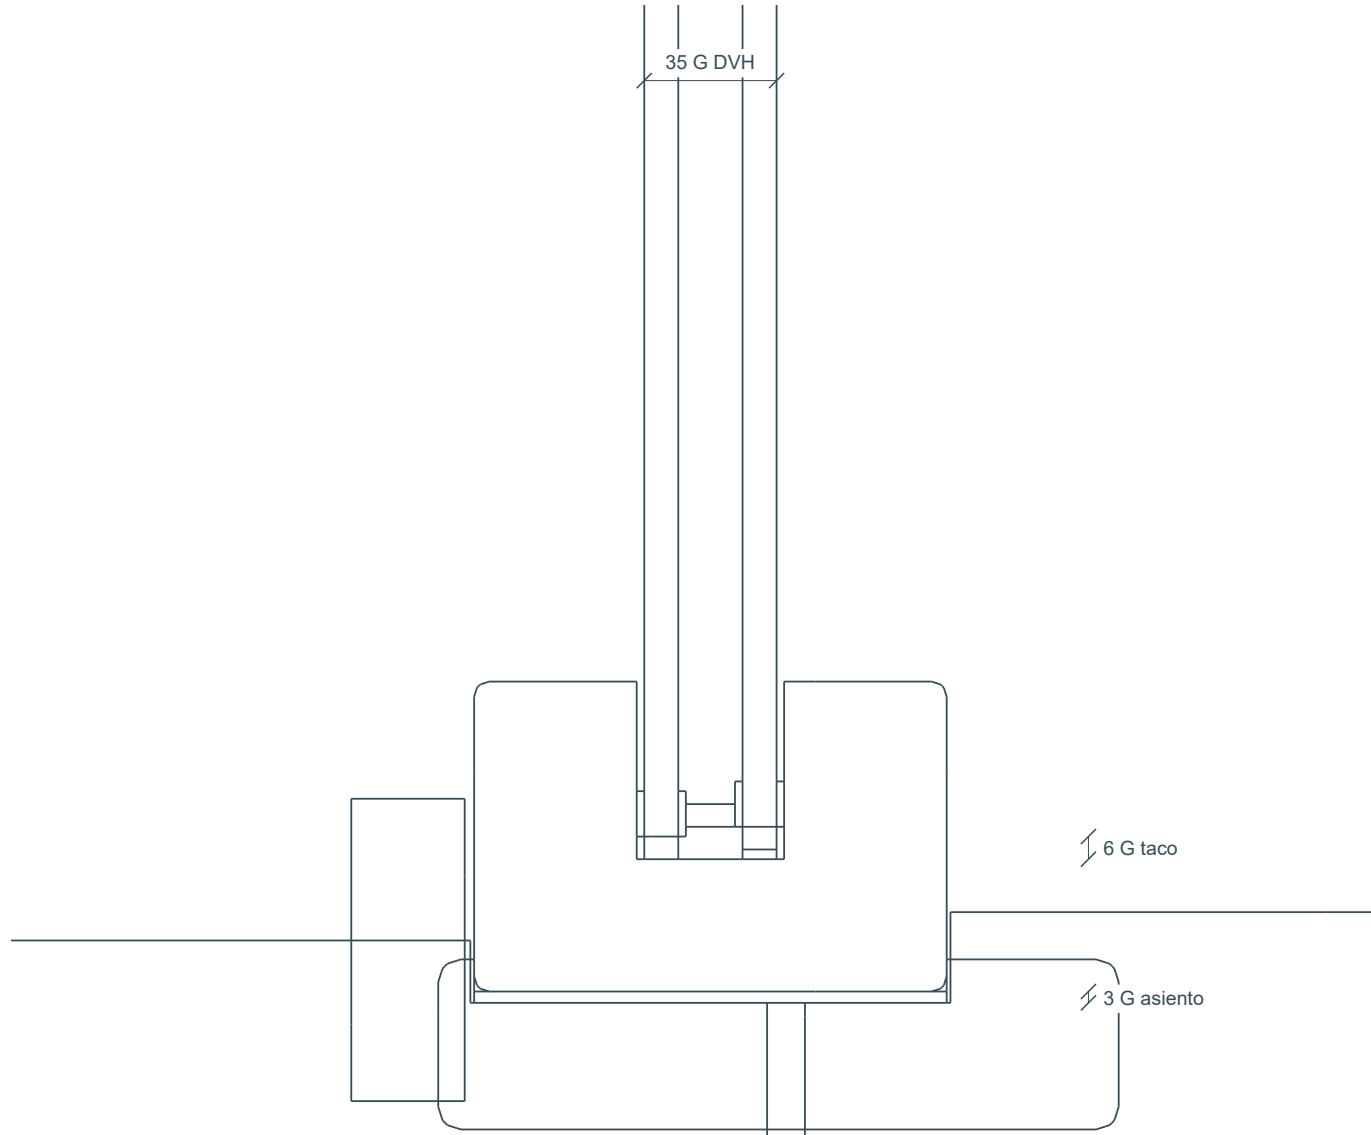


G galce comun39: paquete35 y2mm por cara exterior. Juntas elastomericas2mm a cada cara de los vidrios; toma12mm. El sellador de borde une ambas caras internas sin atravesar los vidrios.

G tacos100x6 por vidrio a1/4 y3/4 de luz; calzo conformado bajo el vidrio interior. Bajo el marco: apoyo continuo3 y juntas1 en rebaje local. Envolvente original conservada; sin carga sobre sello de cámara.


G se retiraron los 24 burletes metálicos macizos incompatibles. Las juntas nuevas son geometría P incorporada; no certifican hermeticidad, capacidad, térmica ni acústica. D10 amplía las correderas de balcón.

R2 | Vitro TD-140: Large Insulating Glass Units, p.4

06 Jamba / corte real G | 1:2

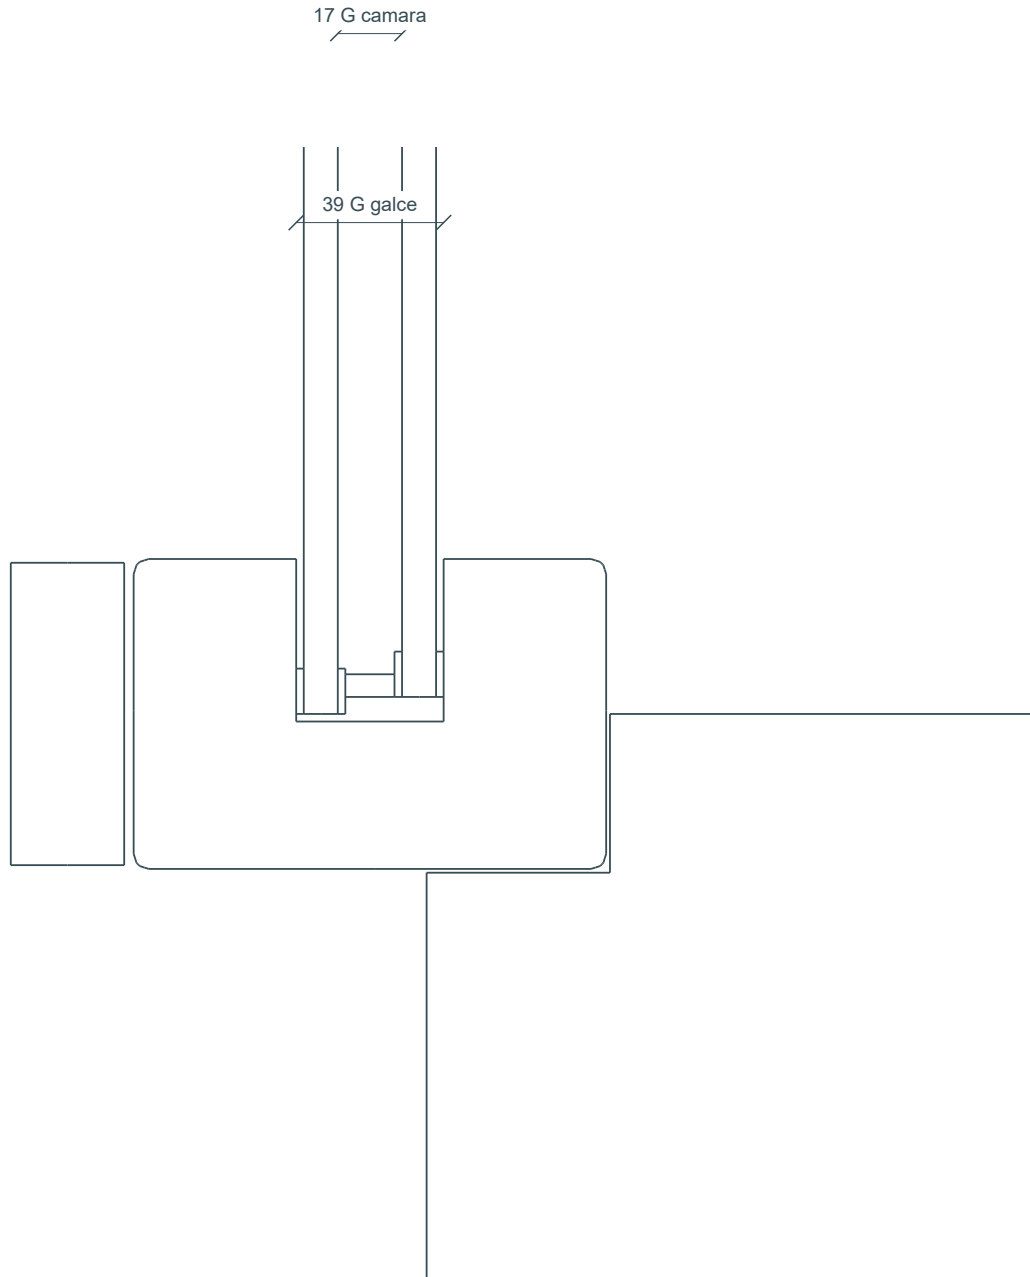

P Conexión del marco al soporte | 1:5

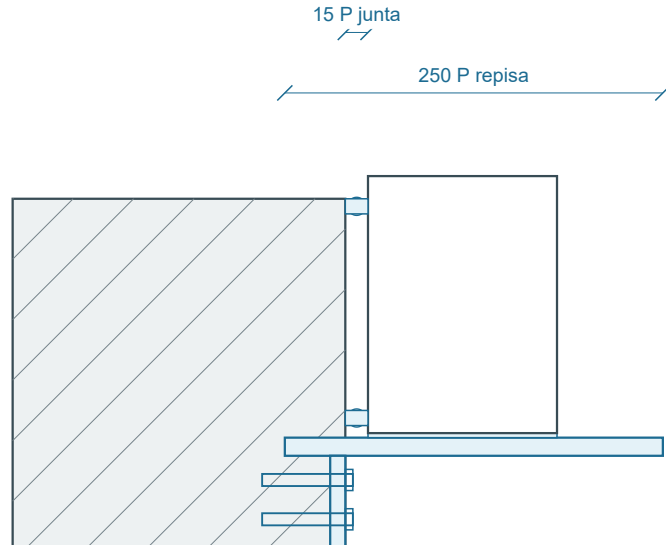

P apoyo continuo12 sobre escuadra10, fijacionesØ8 por dimensionar. Junta15 con respaldo y sellos; drenaje a exterior y compatibilidad del sistema pendientes de proyecto.

EN REVISION - PROPUESTAS DE COORDINACION, SIN CALCULO DE CAPACIDAD

A2 / imprimir al 100 %

Base G: Casa_de_Campo_99_R7D.blend / 9cf1a0e2f1b1a606

G acredita geometria, no capacidad. P identifica propuestas; su presencia3D no valida prestaciones.


03 / 10-09-2026

G = medido / gris

P = propuesta dimensional / azul

Todas las cotas en mm salvo niveles en m

07 Planta G / placa lateral regular | 1:5

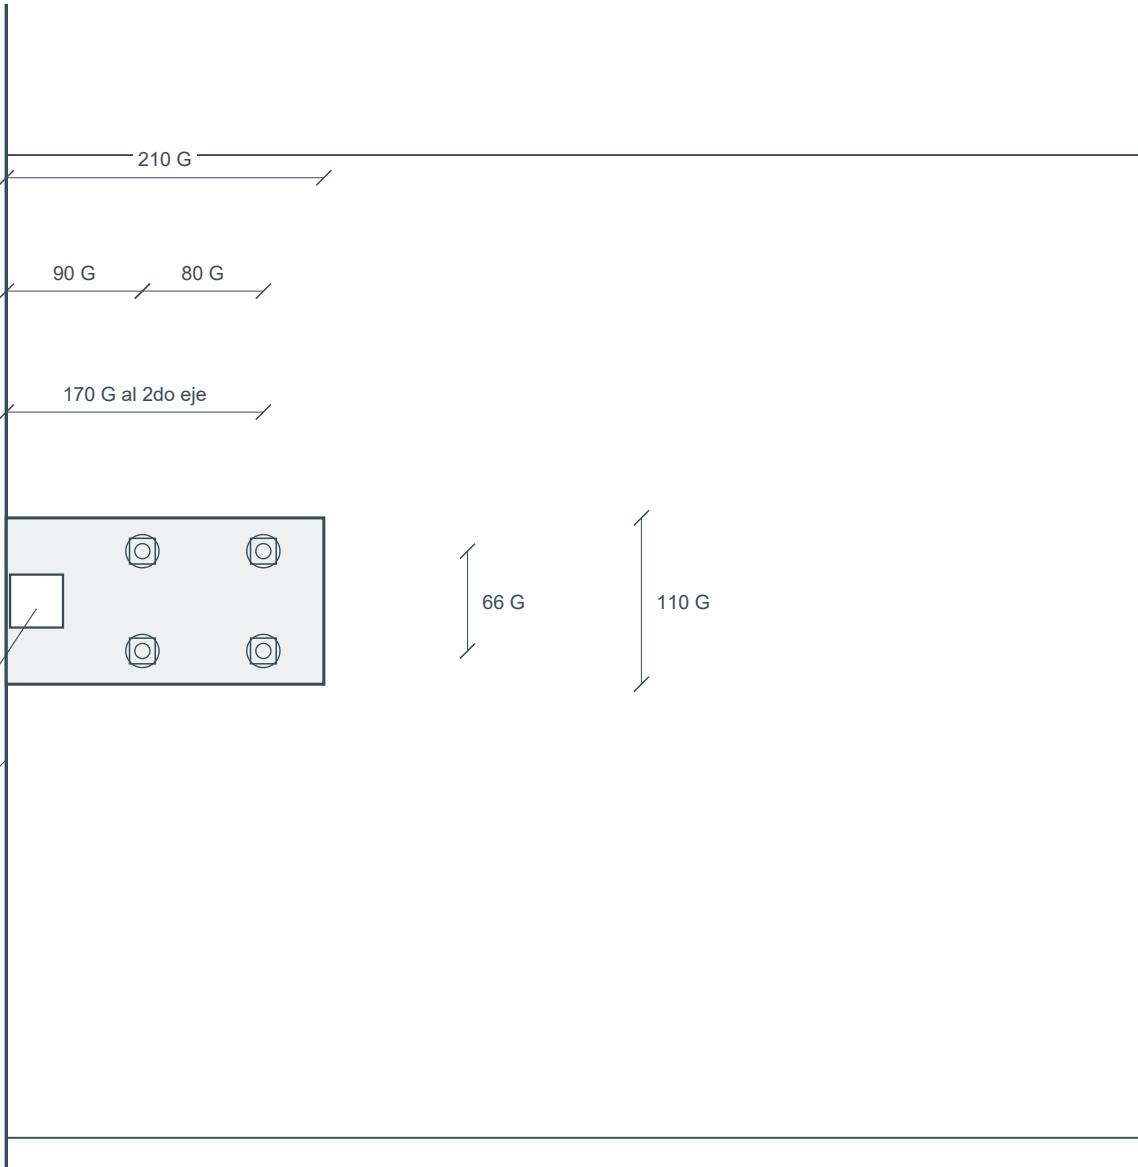

G canto de losa X=13,00. Ejes interiores a90 y170 mm. Reticula80 x66; cuatro vastagos continuos Ø10 por placa.


G poste 35 x 35, centro a 20 del canto. La placa 210 x 110 x 12 desarrolla el apoyo hacia el interior.

CASOS Y ALCANCE RESISTENTE

G17 postes unicos. Esquinas:210 x210; primera placa envolvente210 x232 por prolongacion al descanso. Capacidad de placa, soldadura, anclajes, borde y hormigon pendiente por cargas/armado [R5].

R5 | Hilti: Base plates - design considerations

08 Corte G / sustrato y anclaje continuo | 1:5

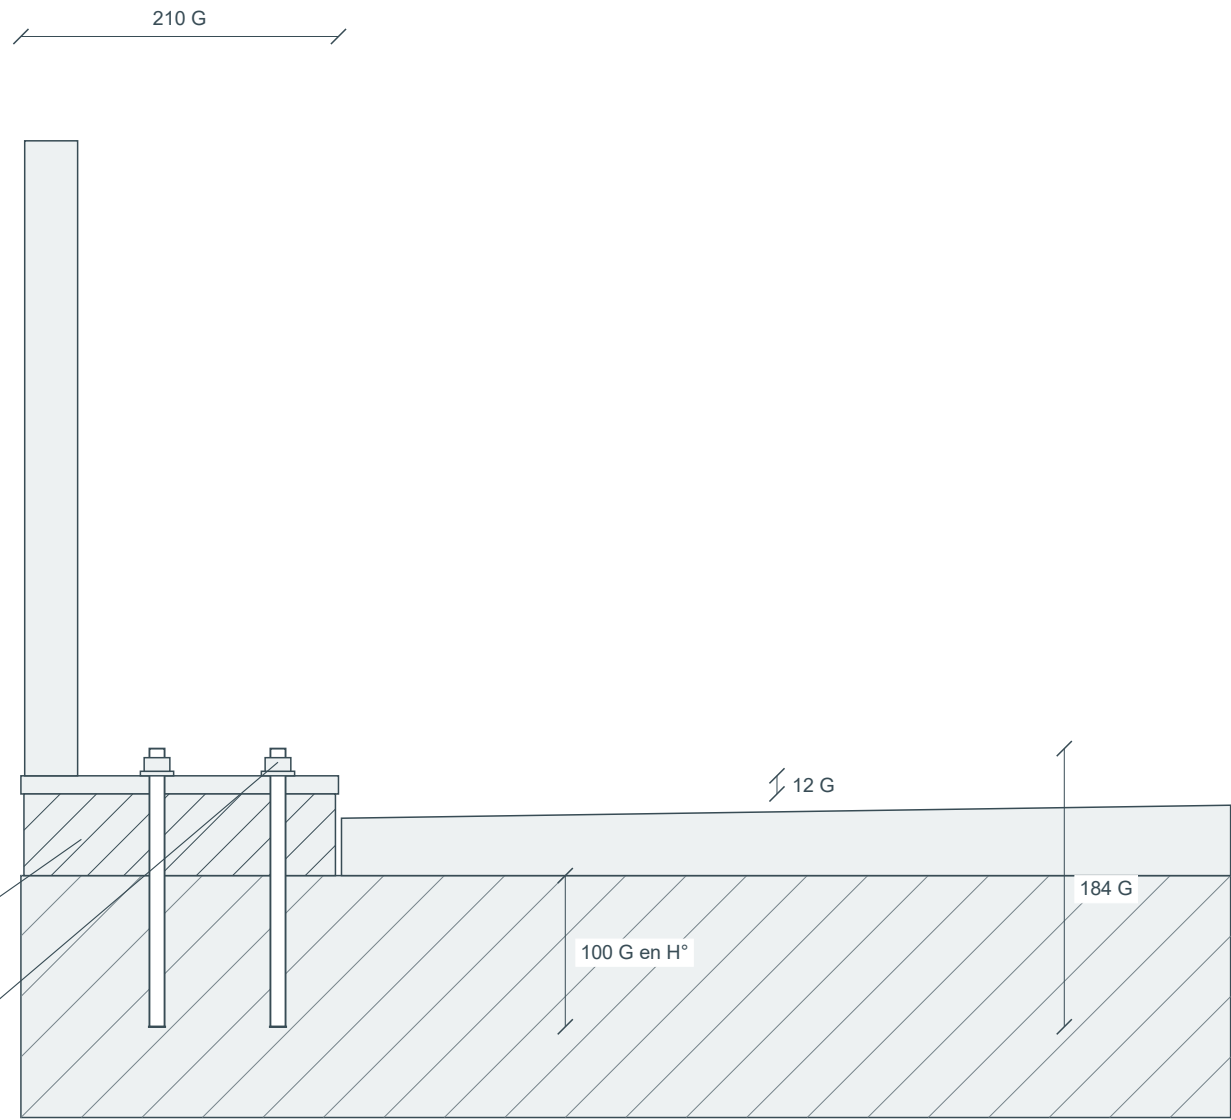


- G cajeado y grout conformado al H° real: 54 sobre +3,20; 44 sobre +3,21. En junta se adapta al escalon. Placa inferior +3,254.


- G arandelaØ22 x3, tuerca17 x17 x9 y vástagoØ10 hasta+3,284. Extremo inferior+3,10/+3,11:100 mm dentro de H°

G = medido / gris P = propuesta dimensional / azul Todas las cotas en mm salvo niveles en m

09 Union superior G / envoltentes reales | 1:5

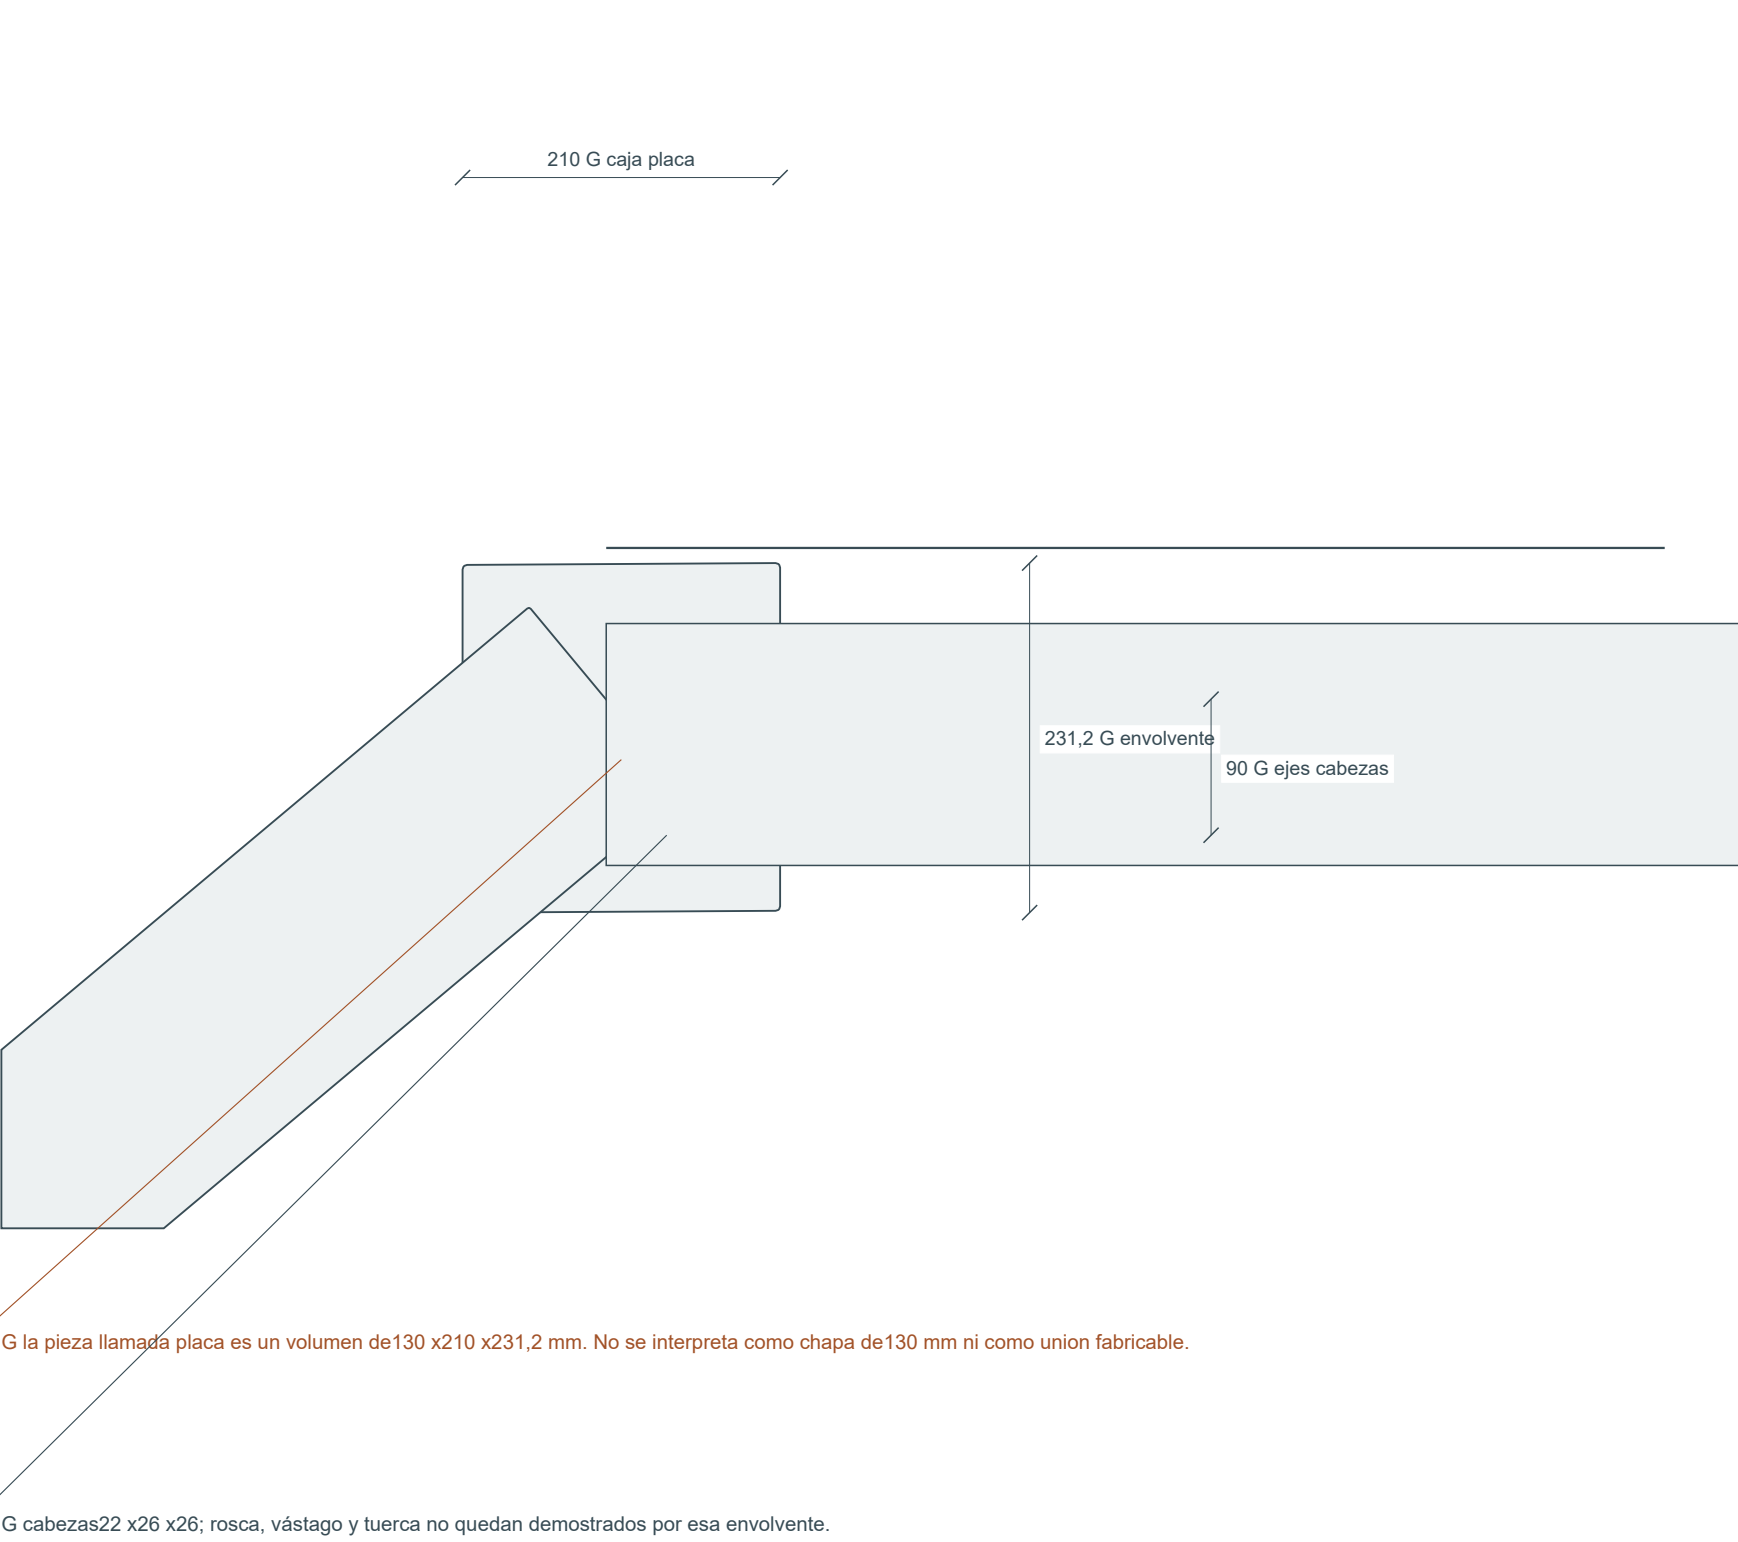

10 P doble cartela / seccion transversal | 1:5

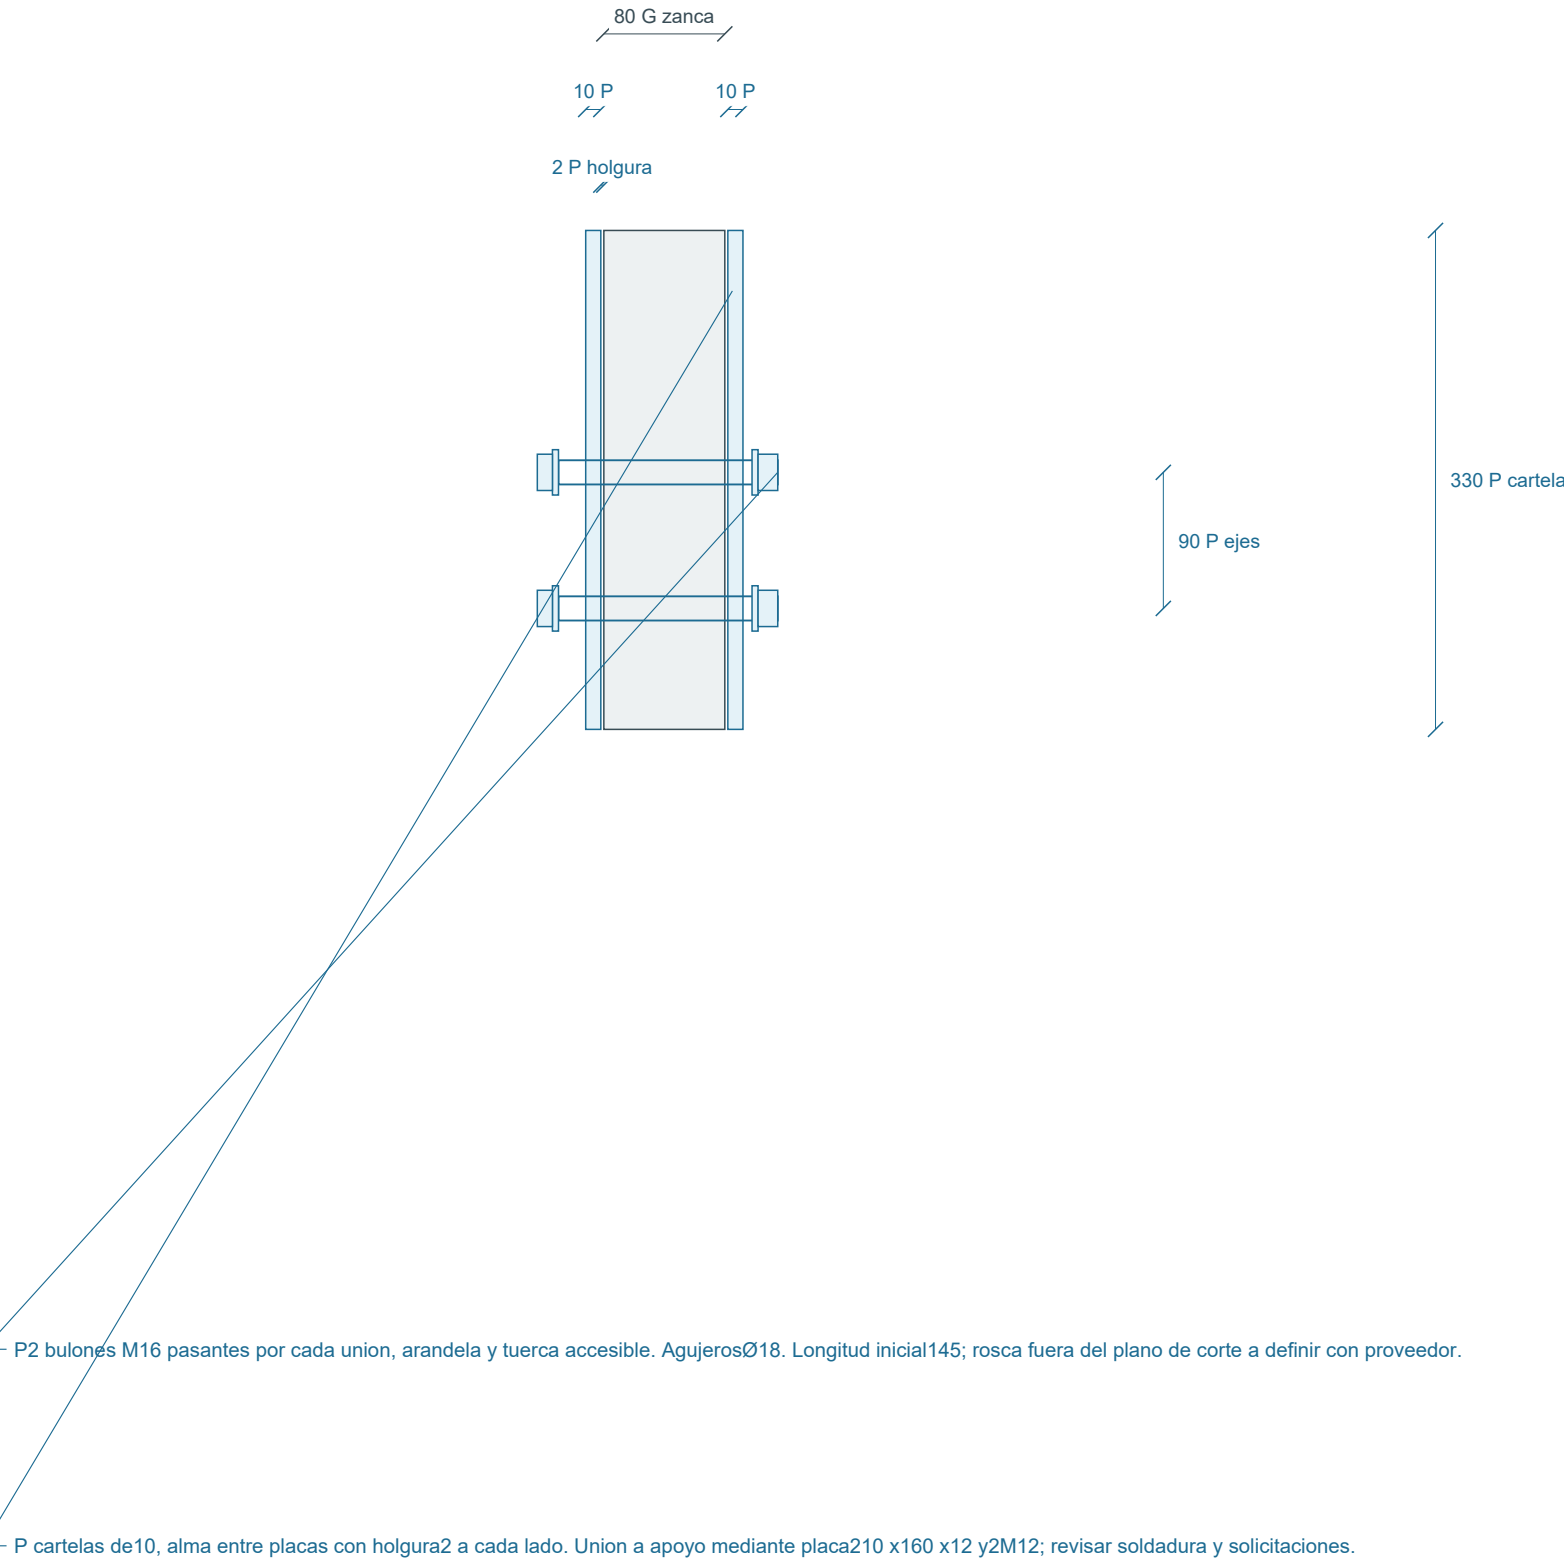


ARRANQUE PROPUESTO P

Placa inferior180 x160 x12 sobre grout20;2M12 ejes100 con empotramiento conceptual100 en dado300 x300 x250. Estos tamaños dibujan una reserva de coordinacion: suelo, fundacion, armado y resistencia no estan calculados.


R5 | Hilti: Base plates - design considerations

G = medido / gris P = propuesta dimensional / azul Todas las cotas en mm salvo niveles en m

11 Apoyo inferior / seccion P | 1:5

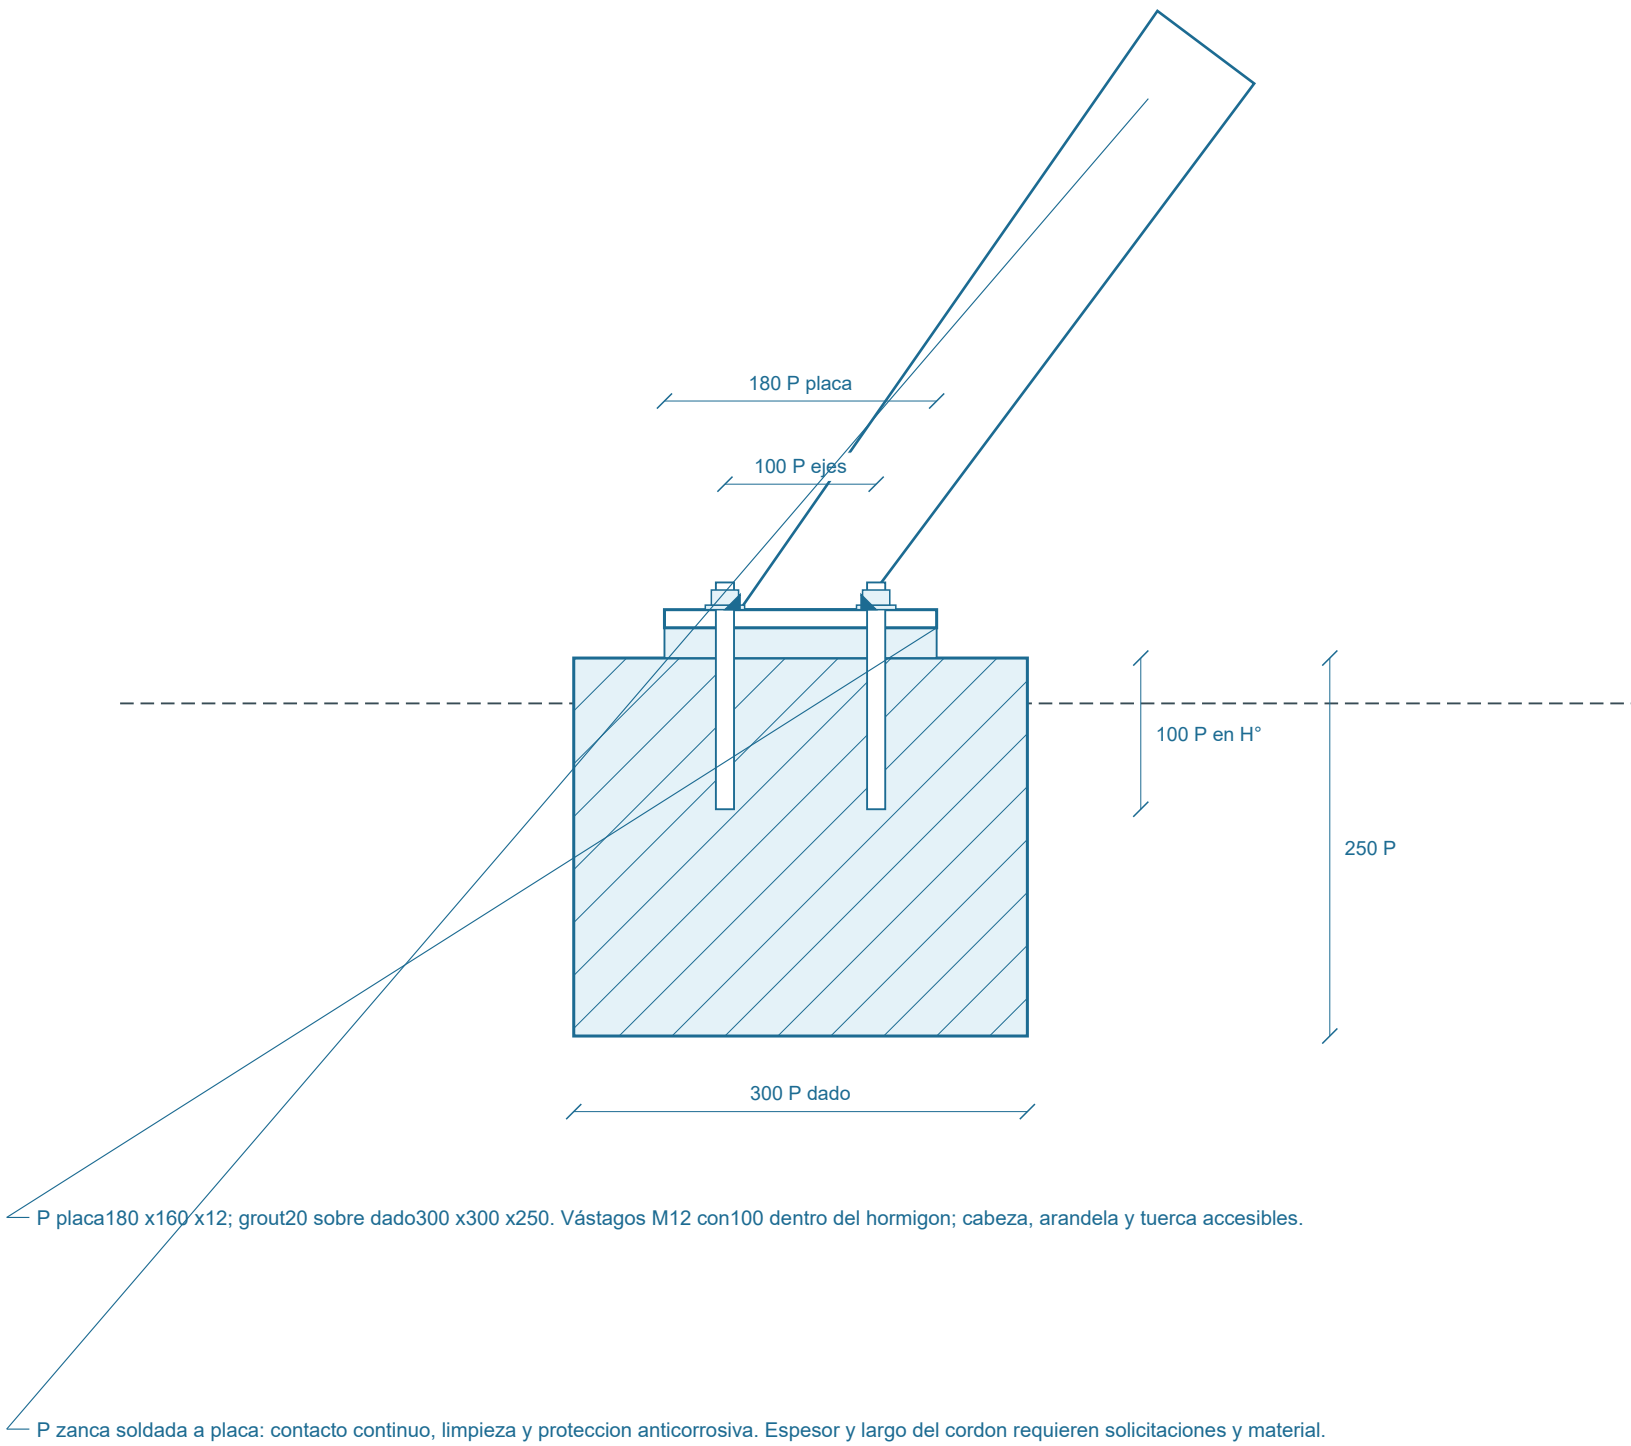

12 Plantilla de arranque / planta P | 1:5

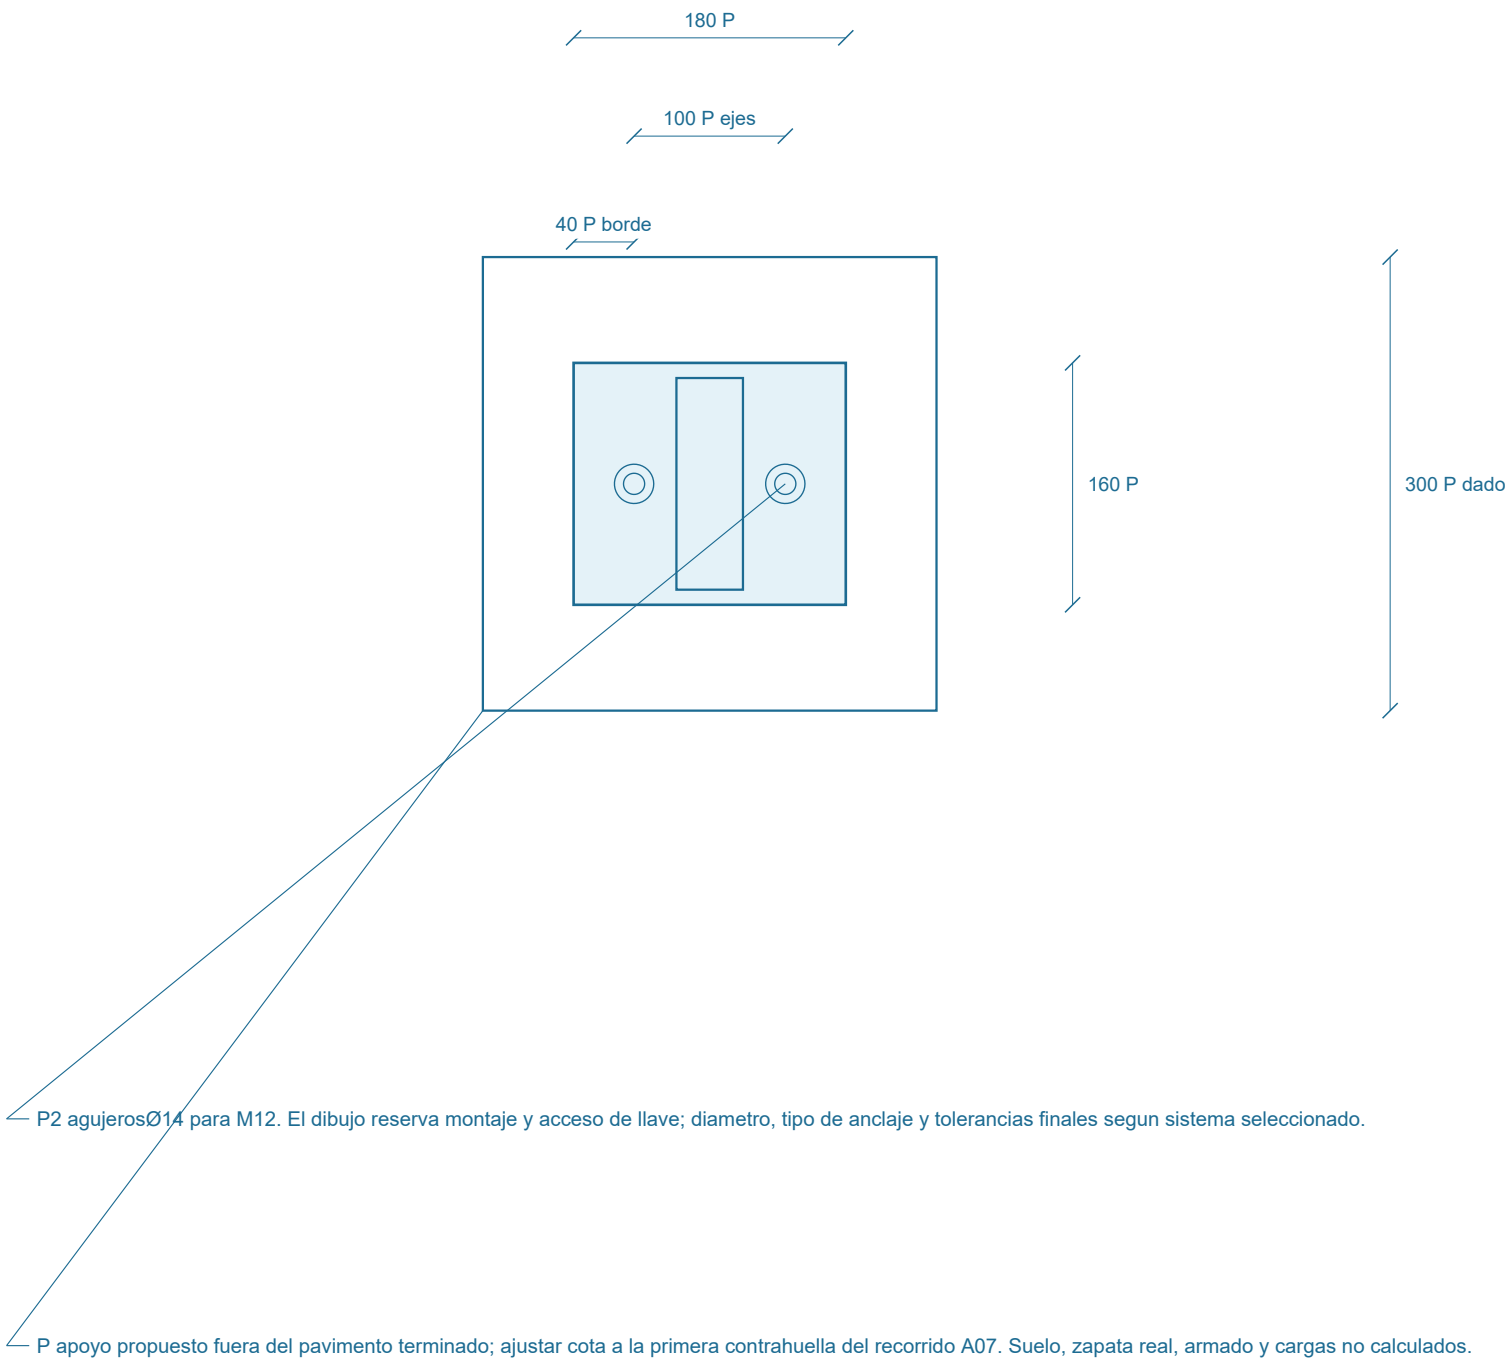


R5 | Hilti: Base plates - design considerations

G = medido / gris

P = propuesta dimensional / azul


Todas las cotas en mm salvo niveles en m

11 Panel de80 / montaje P dentro de huella | 1:5

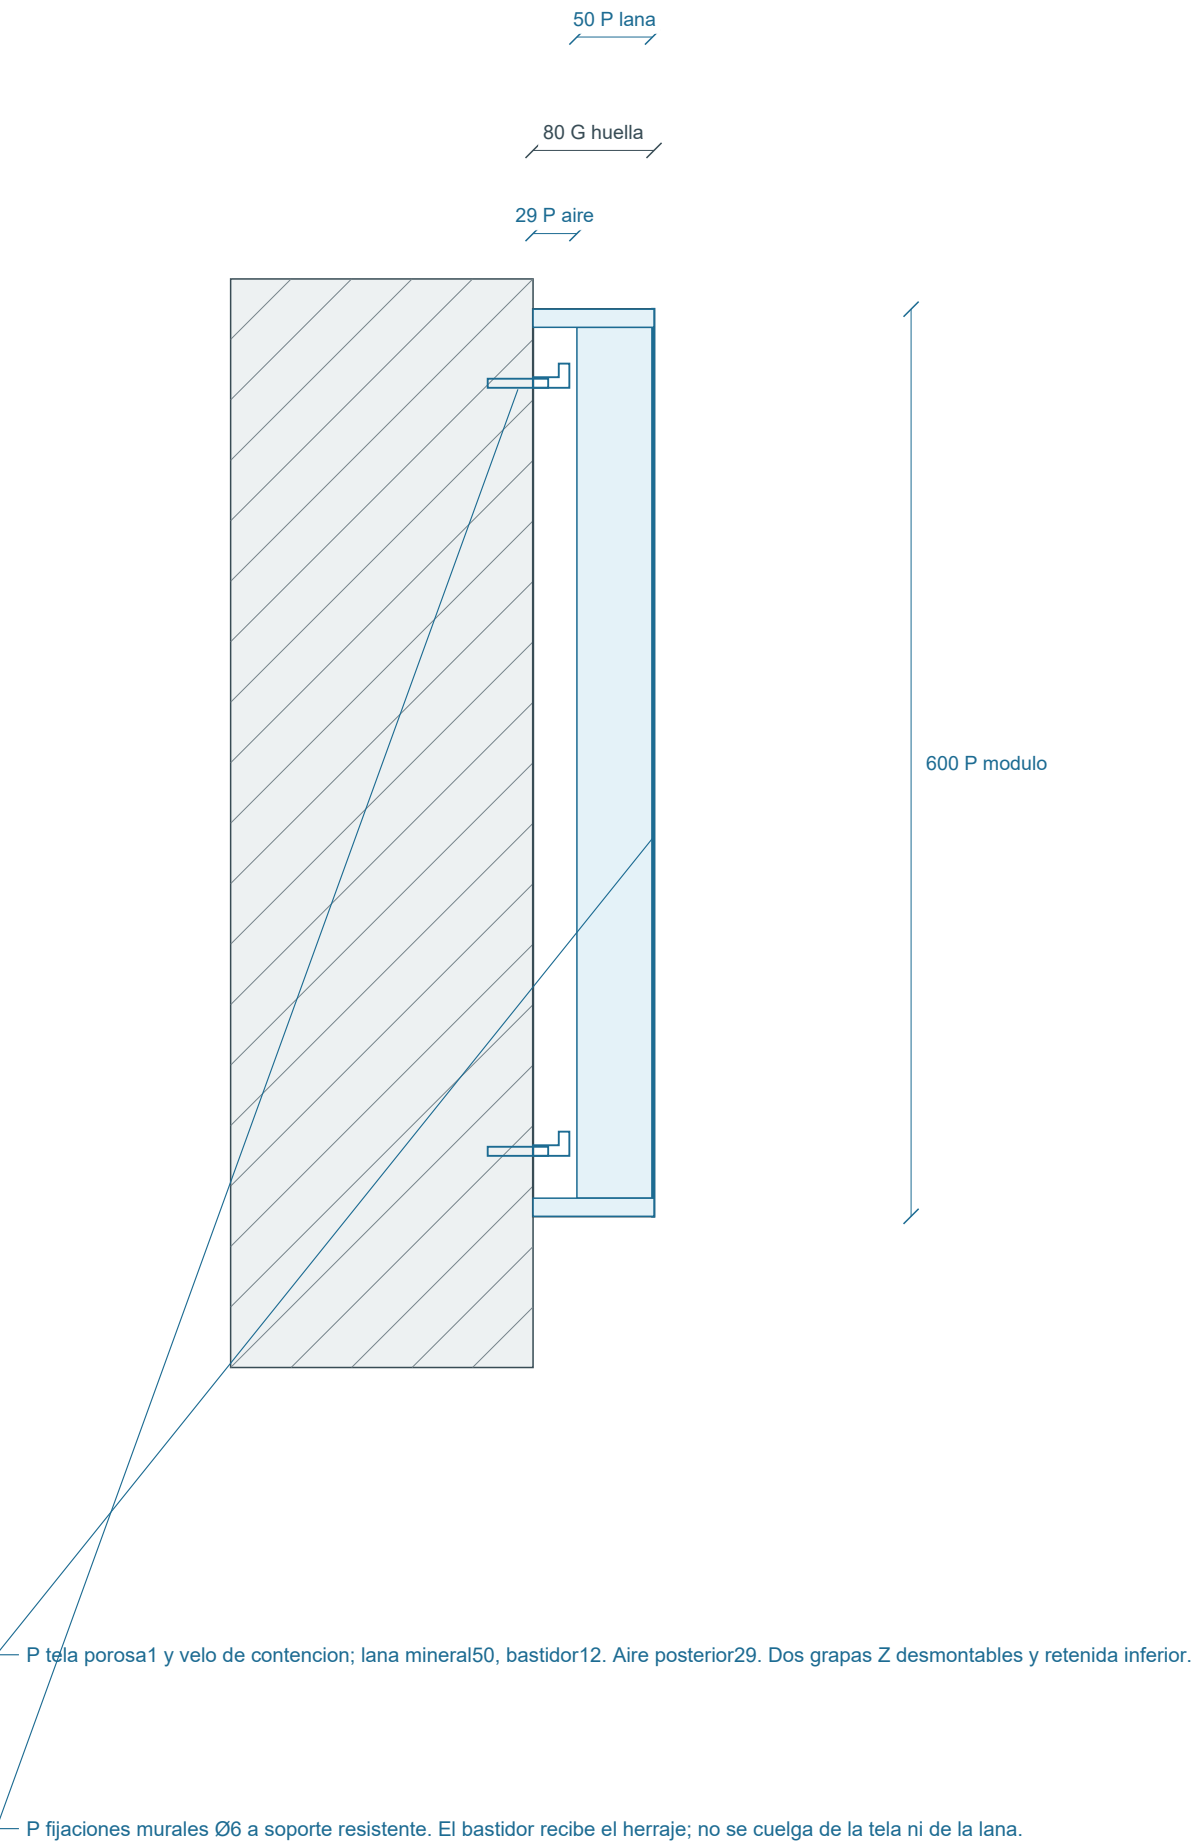

R3 | GIK Acoustics: How to Hang Acoustic Panels


Cielorraso P sobre baffle G / corte parcial | 1:5

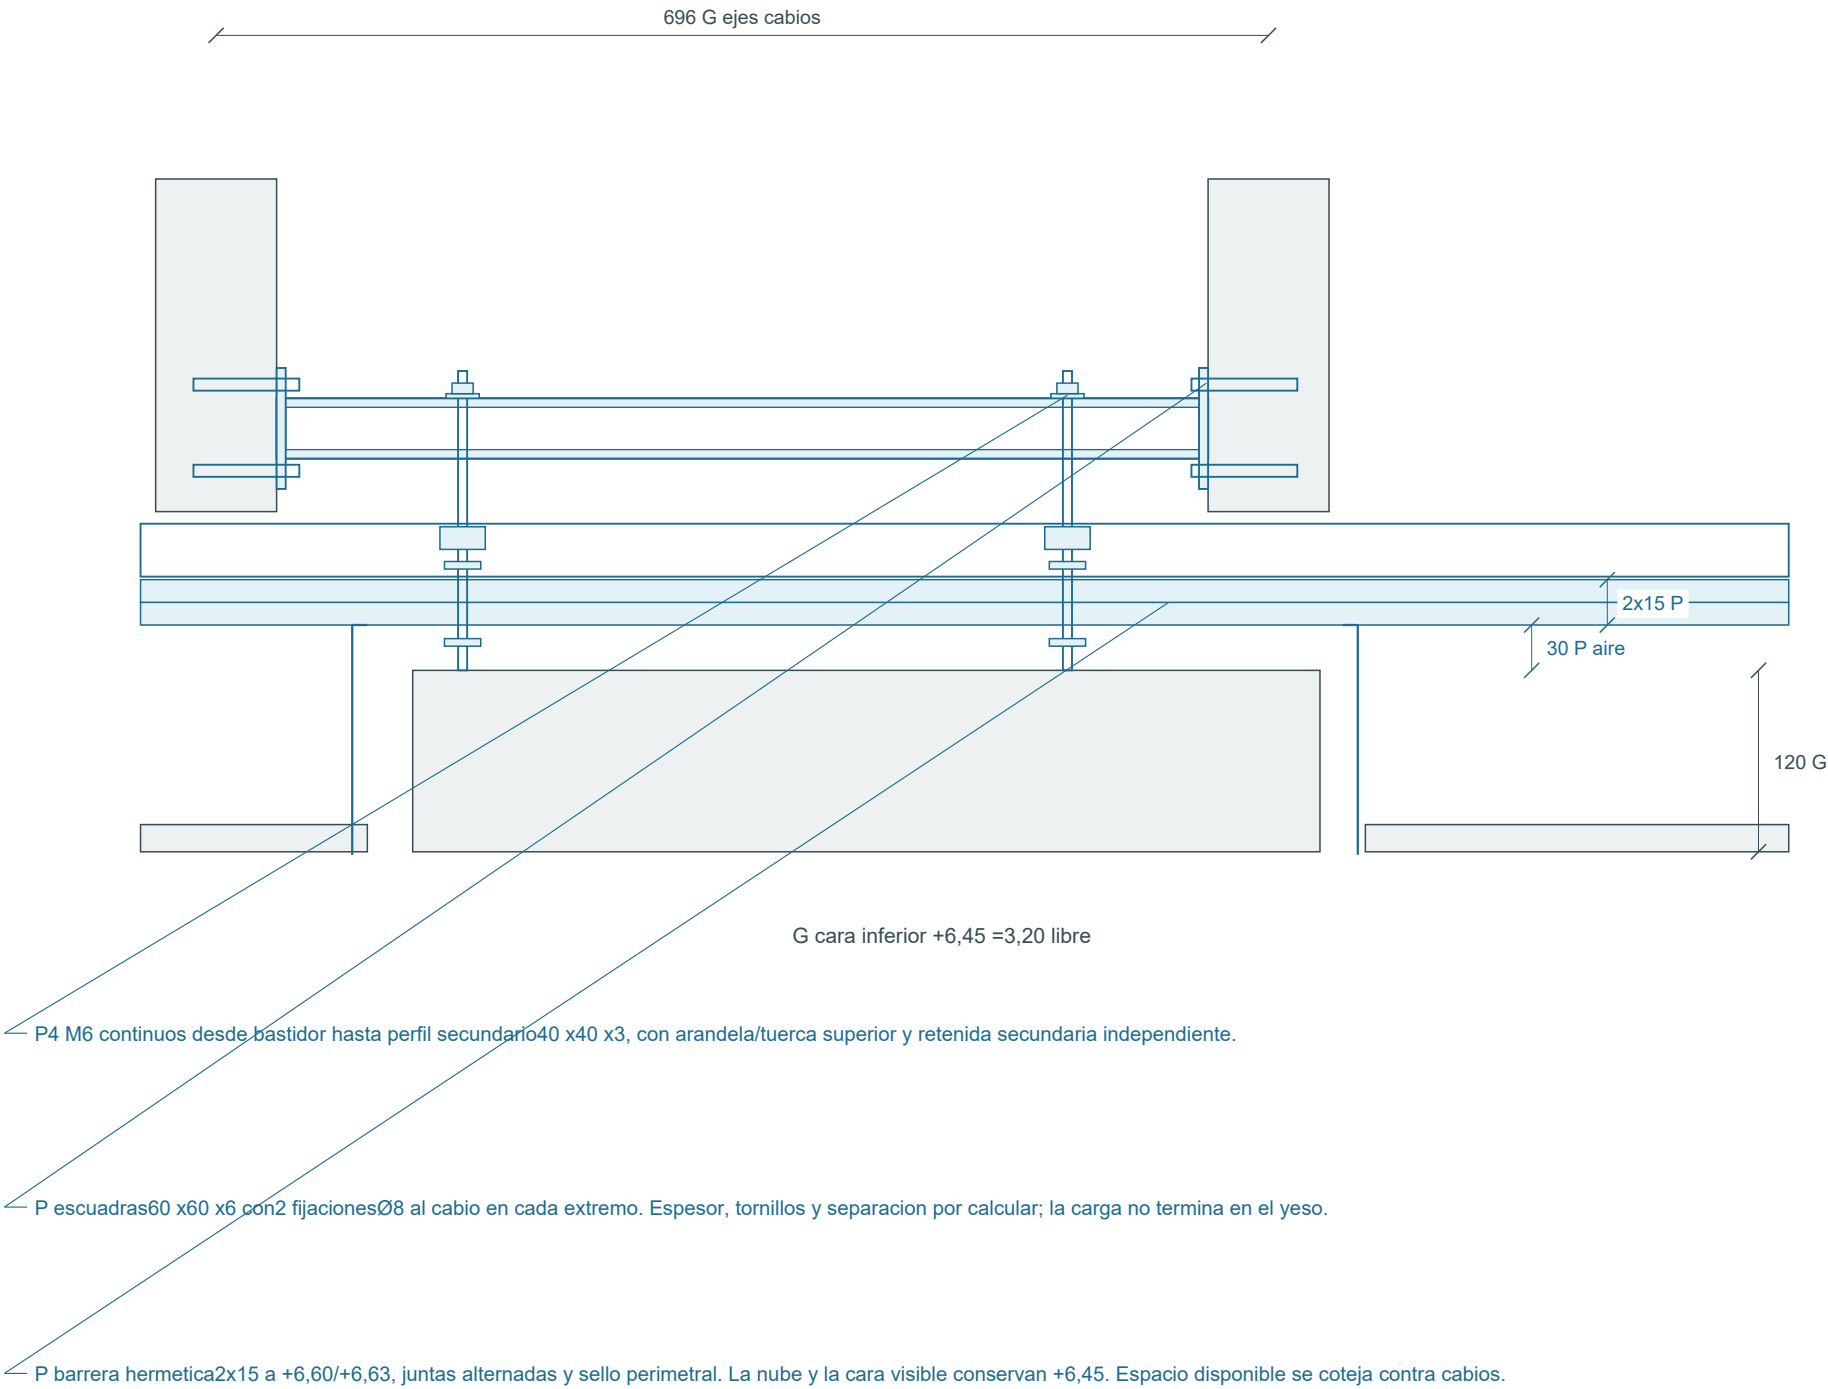

R6 | ROCKWOOL: Acoustic insulation - installation and flanking


G = medido / gris P = propuesta dimensional / azul Todas las cotas en mm salvo niveles en m

13 Puerta estudio / umbral y doble sello P | 1:5

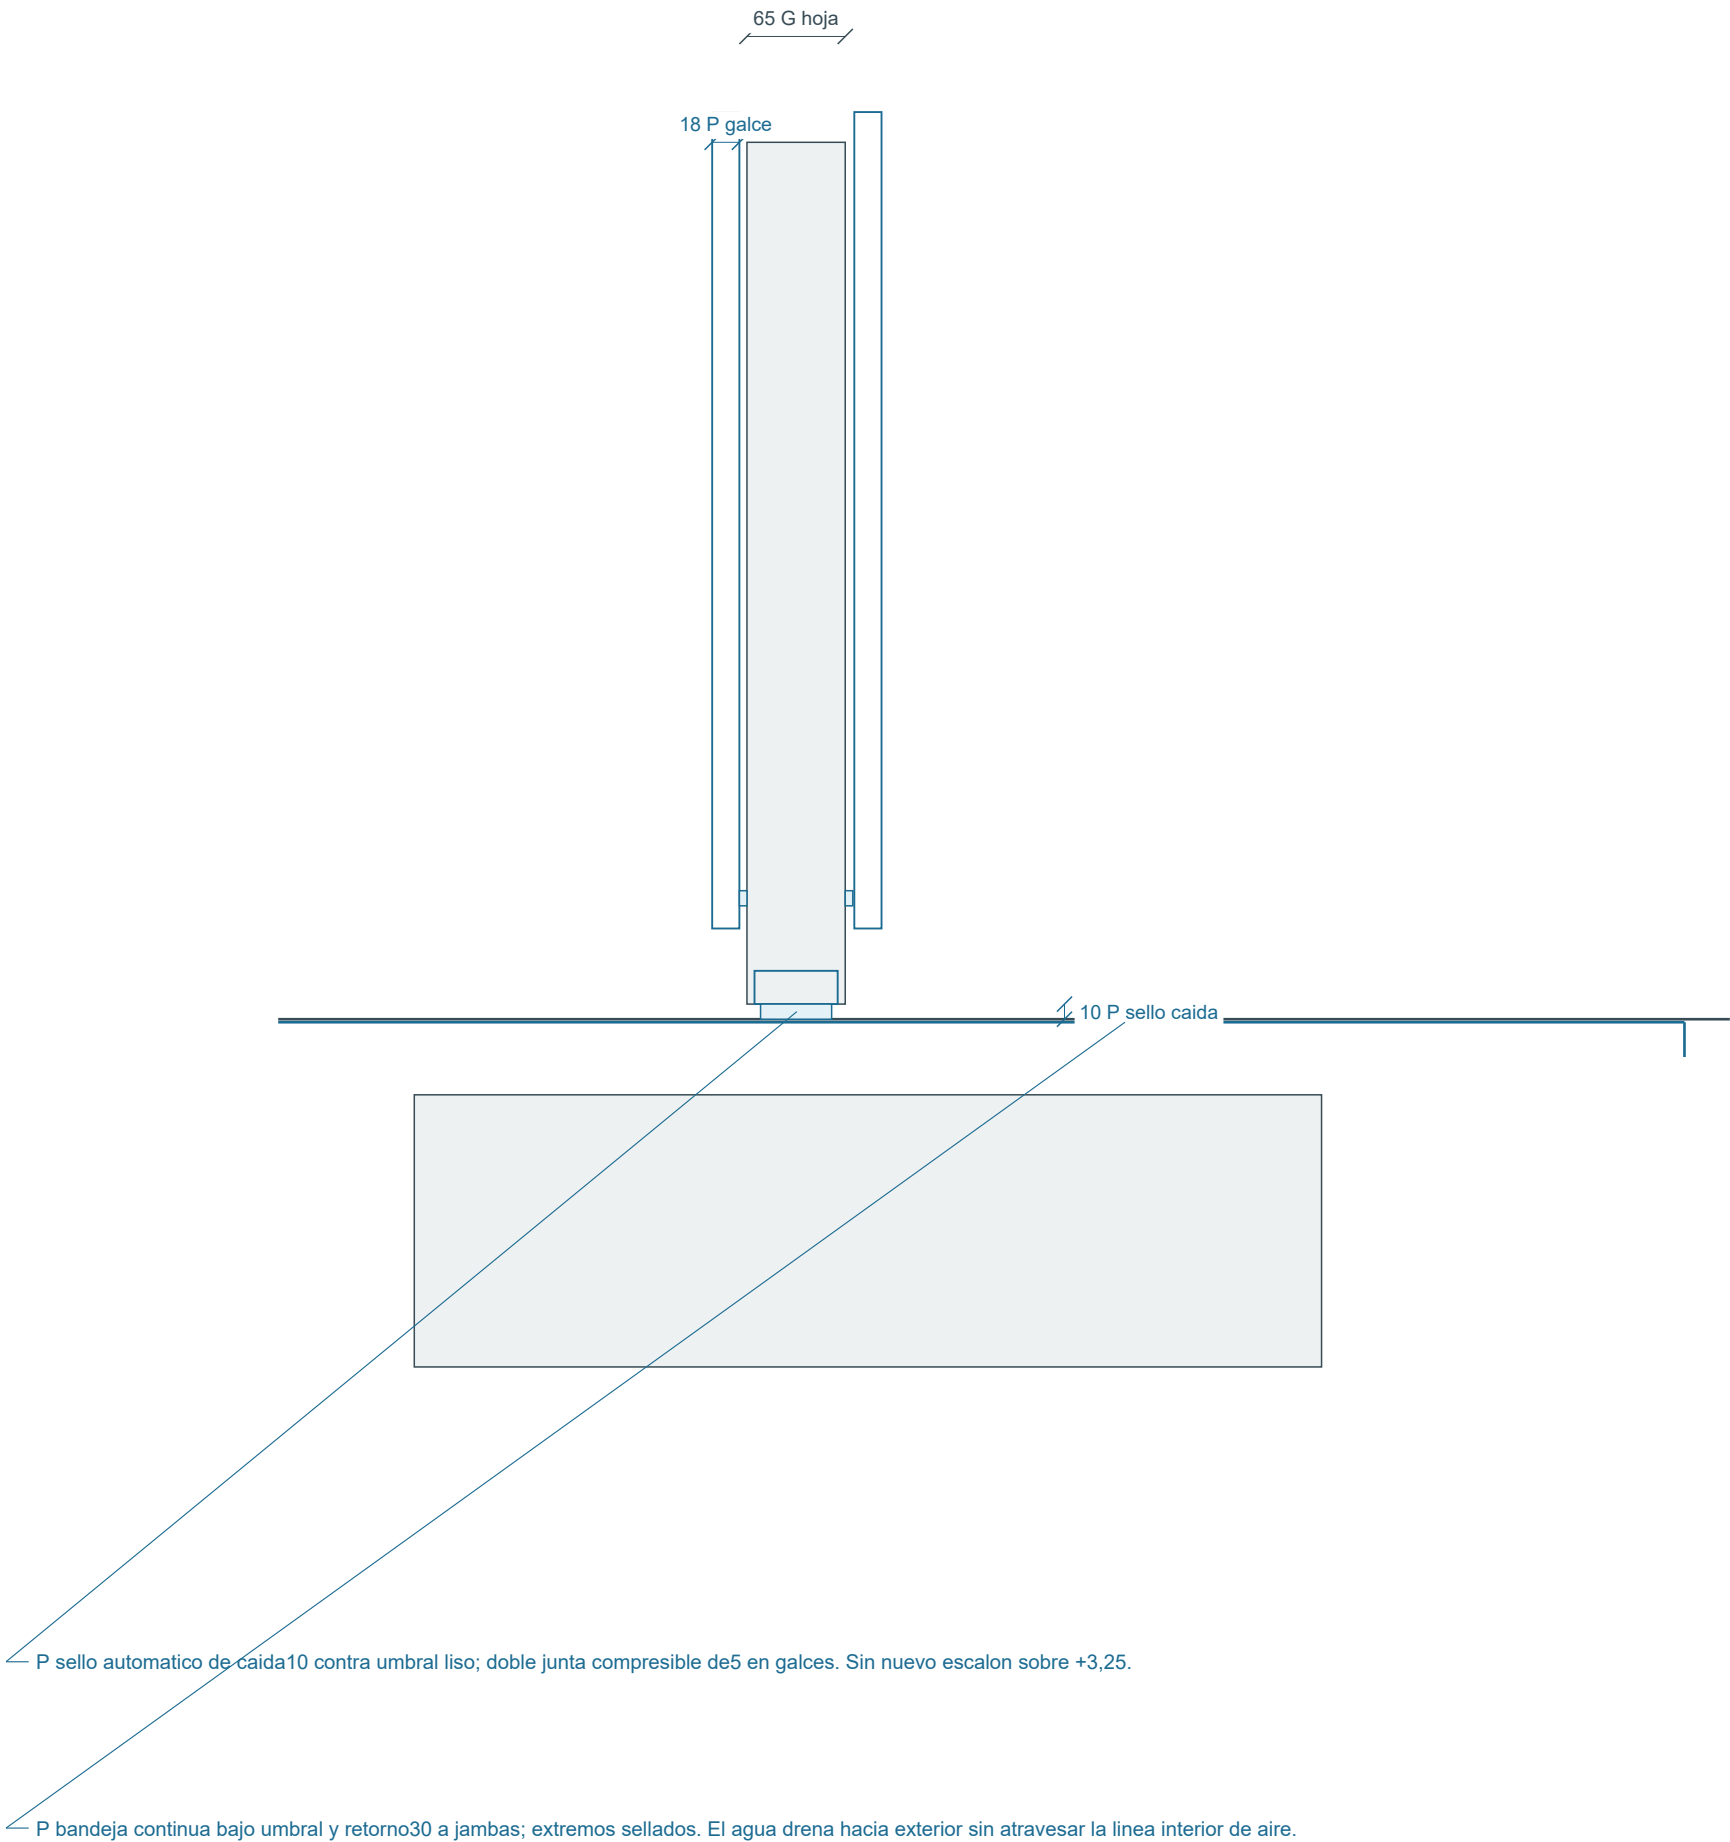


R6 | ROCKWOOL: Acoustic insulation - installation and flanking

14 Paso de servicio frio / sellado P | 1:5

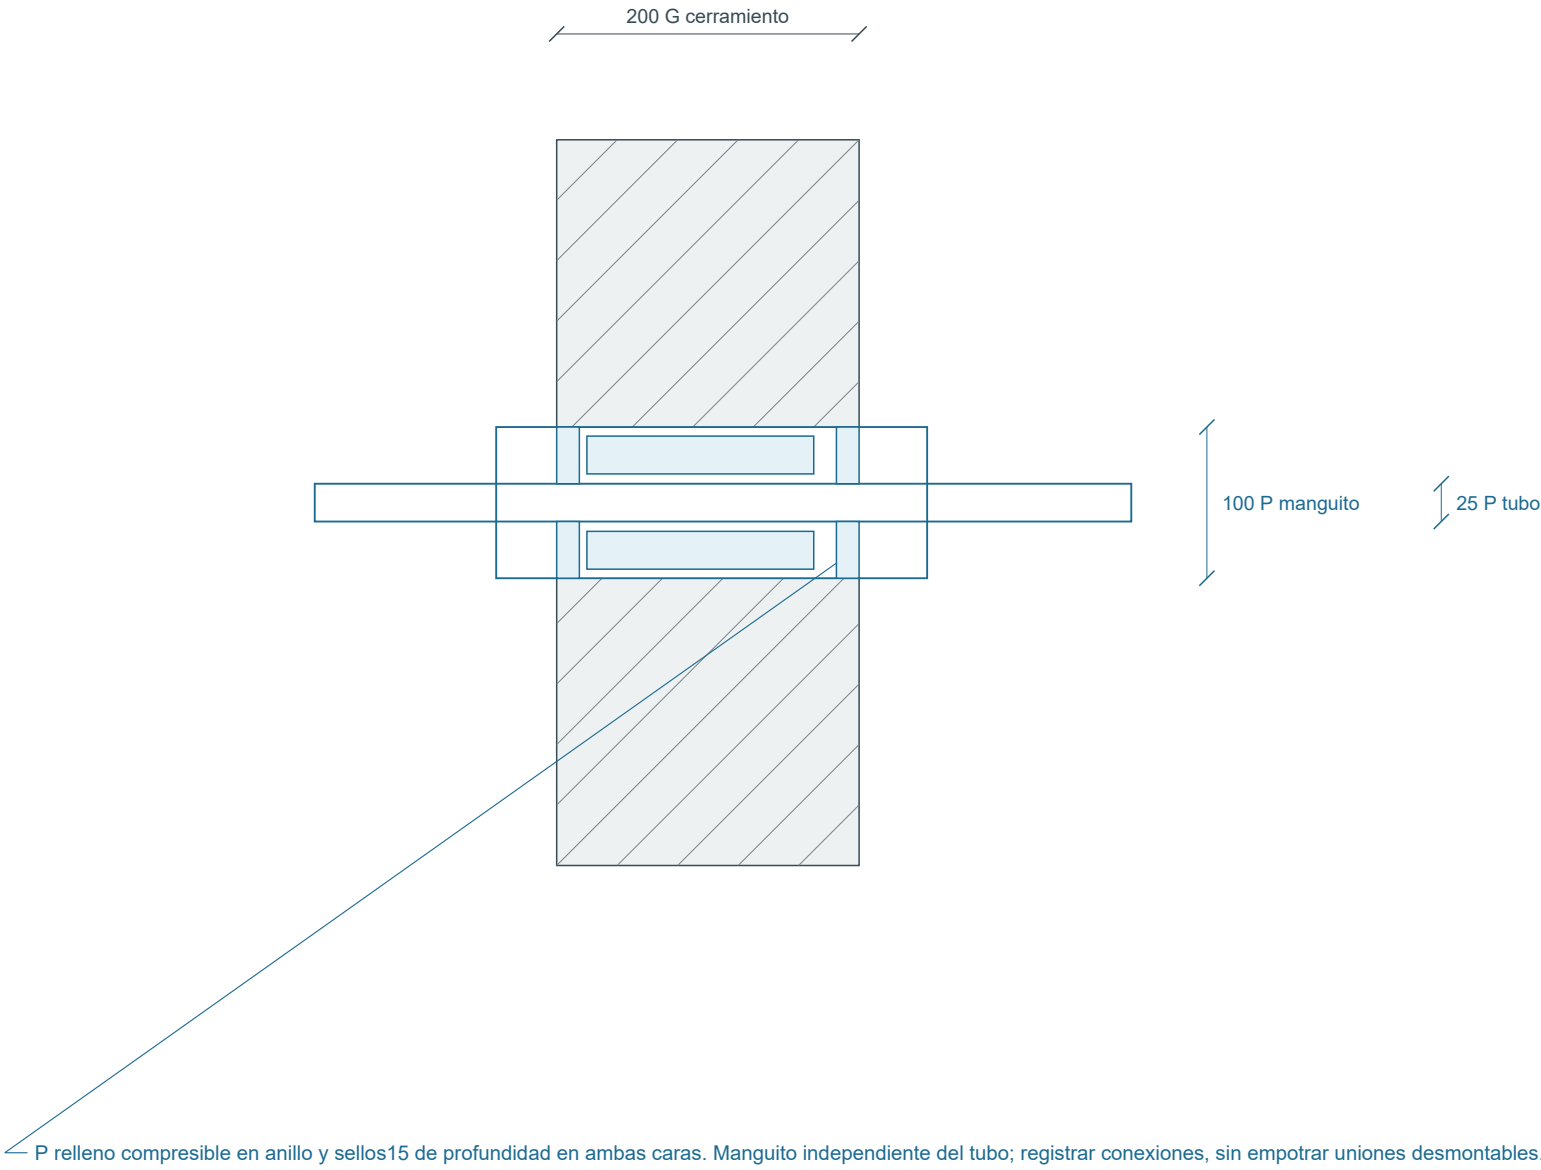

15 Relieve G / soporte posterior P | 1:5

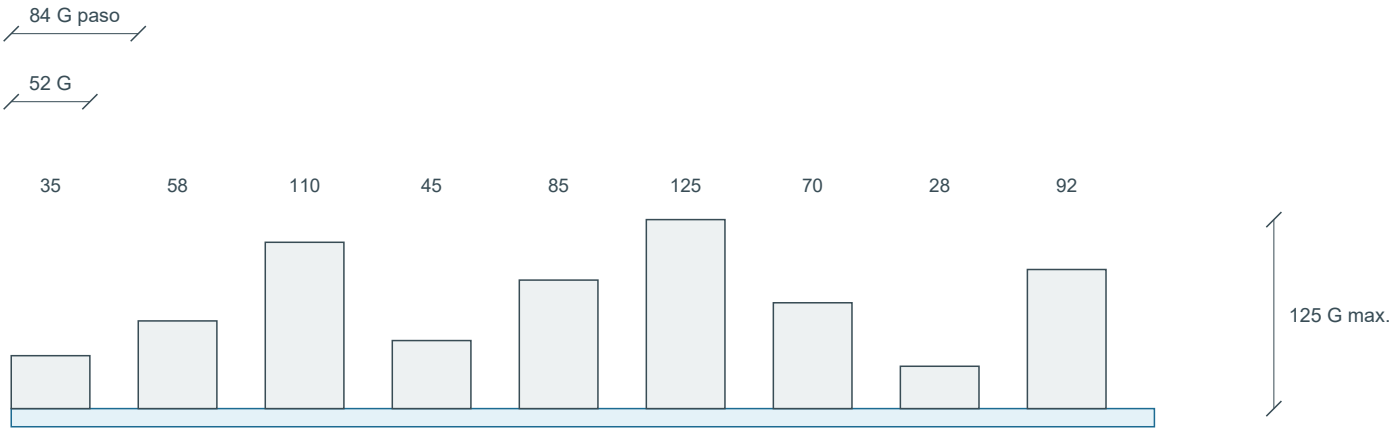


G relieve sin desempeño QRD demostrado. P respaldo12, grapa Z18 y retenida inferior; absorcion/difusion se verifican con sala terminada.

G = medido / gris

P = propuesta dimensional / azul


Todas las cotas en mm salvo niveles en m

16 Planta de cielorraso y plenum | 1:50

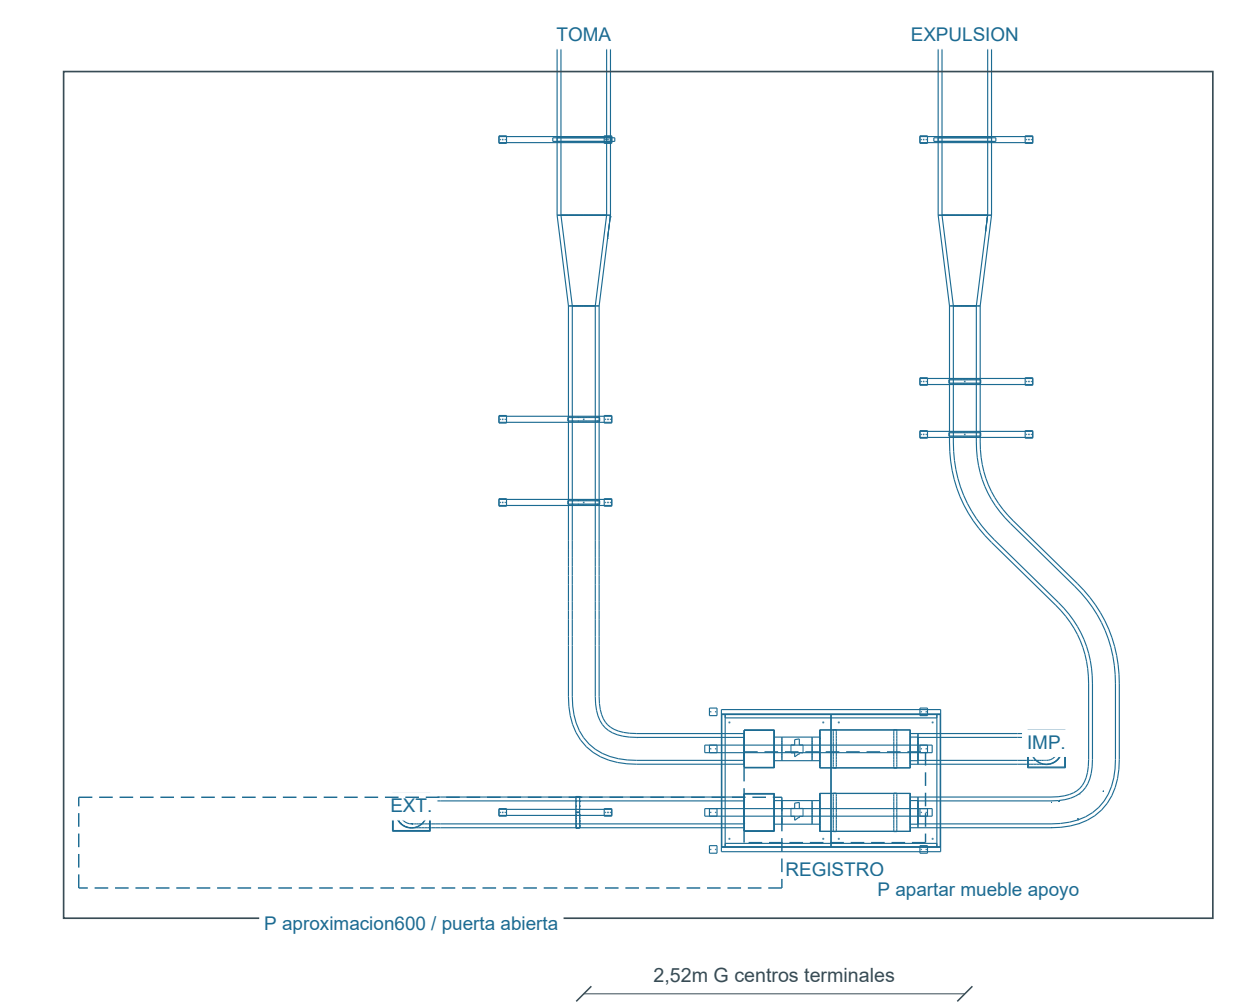


P retro: tapas; filtro por abajo; fan con dos flexibles; silenciador con acoples, abrazaderas y sus dos colgantes. El otro circuito y los bastidores permanecen. No se desmontan nubes.


18 Equipo / corte Z4,68 | 1:10

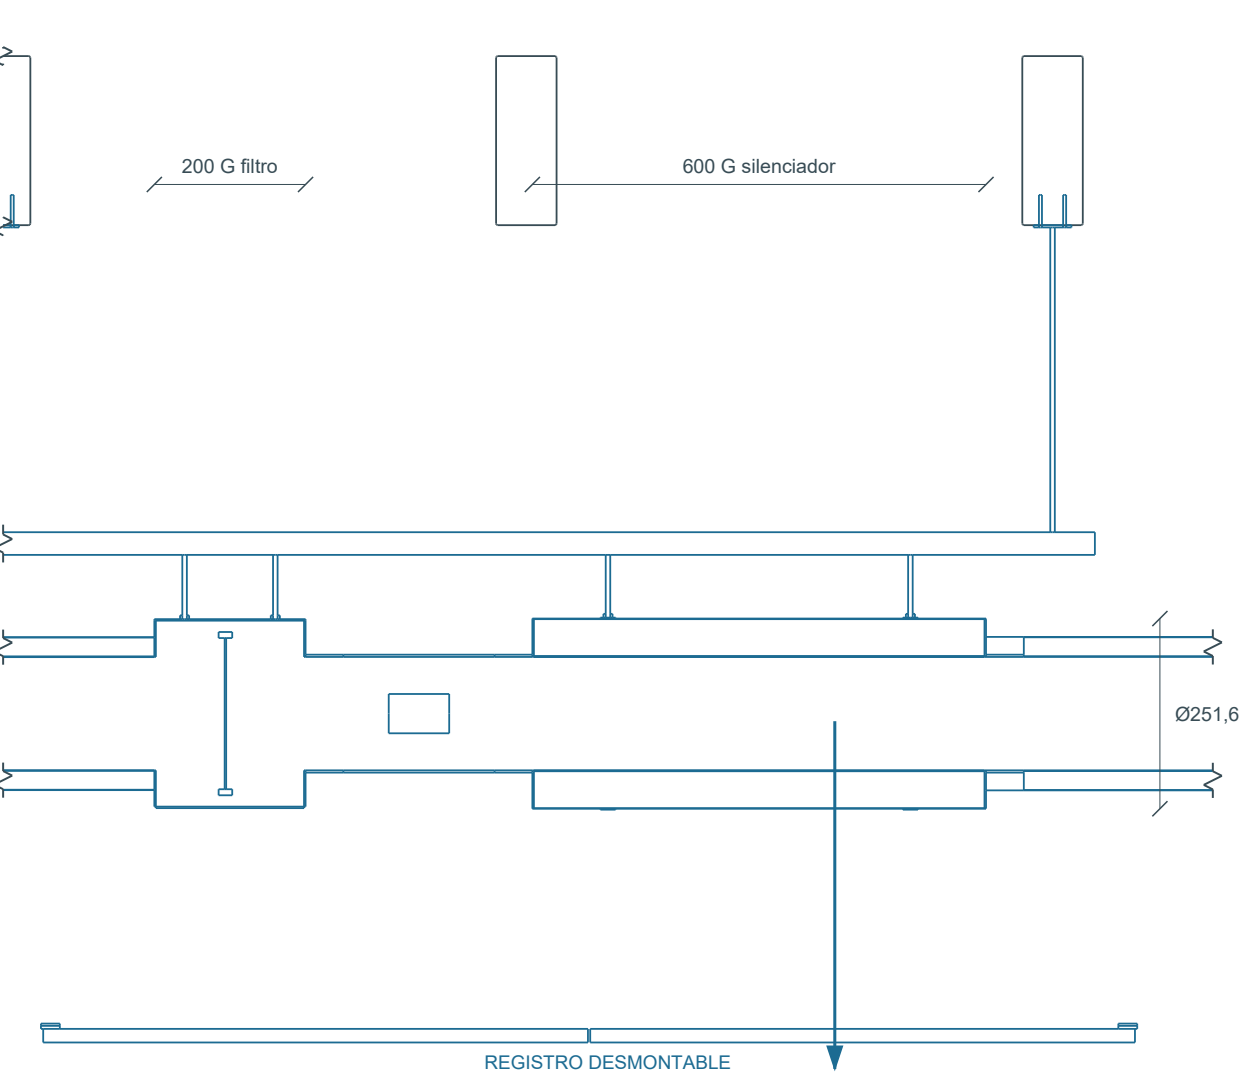

19 Acceso / X19,40 + P | 1:25

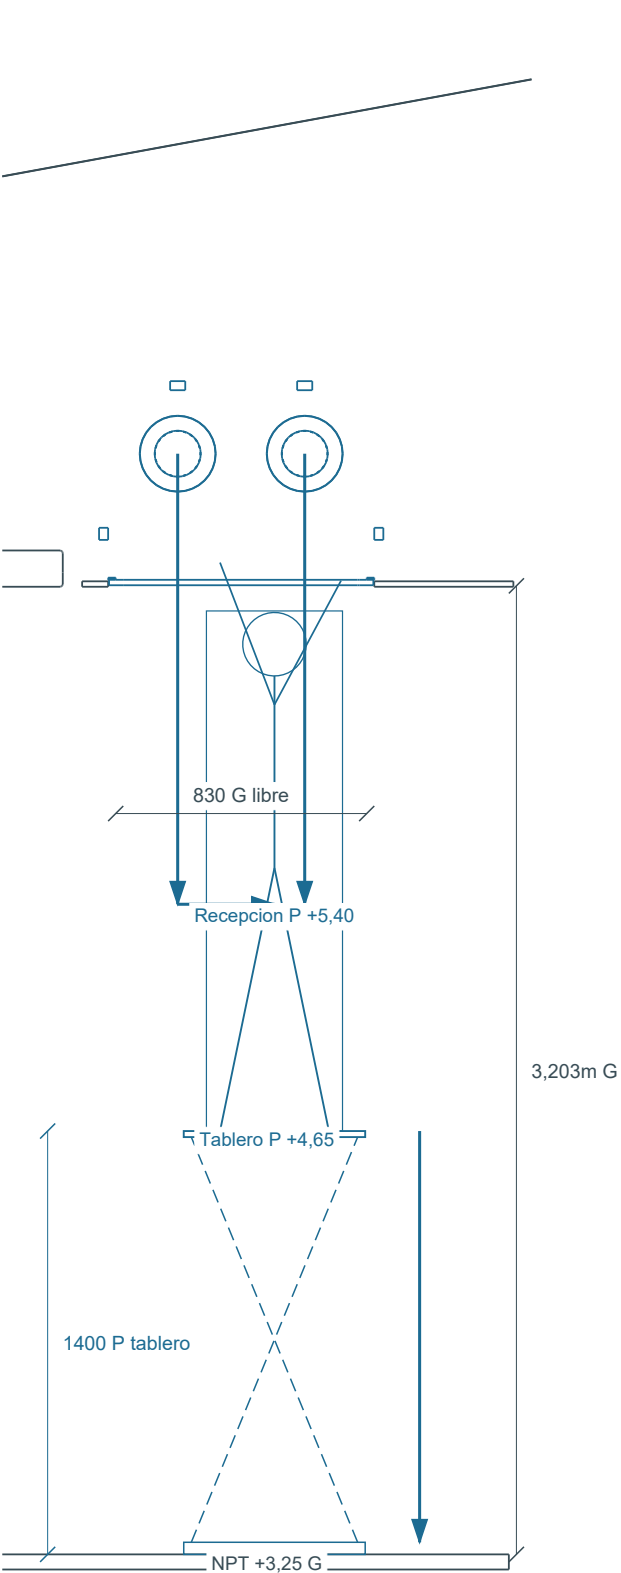


17 Axonometria de montaje / sin escala

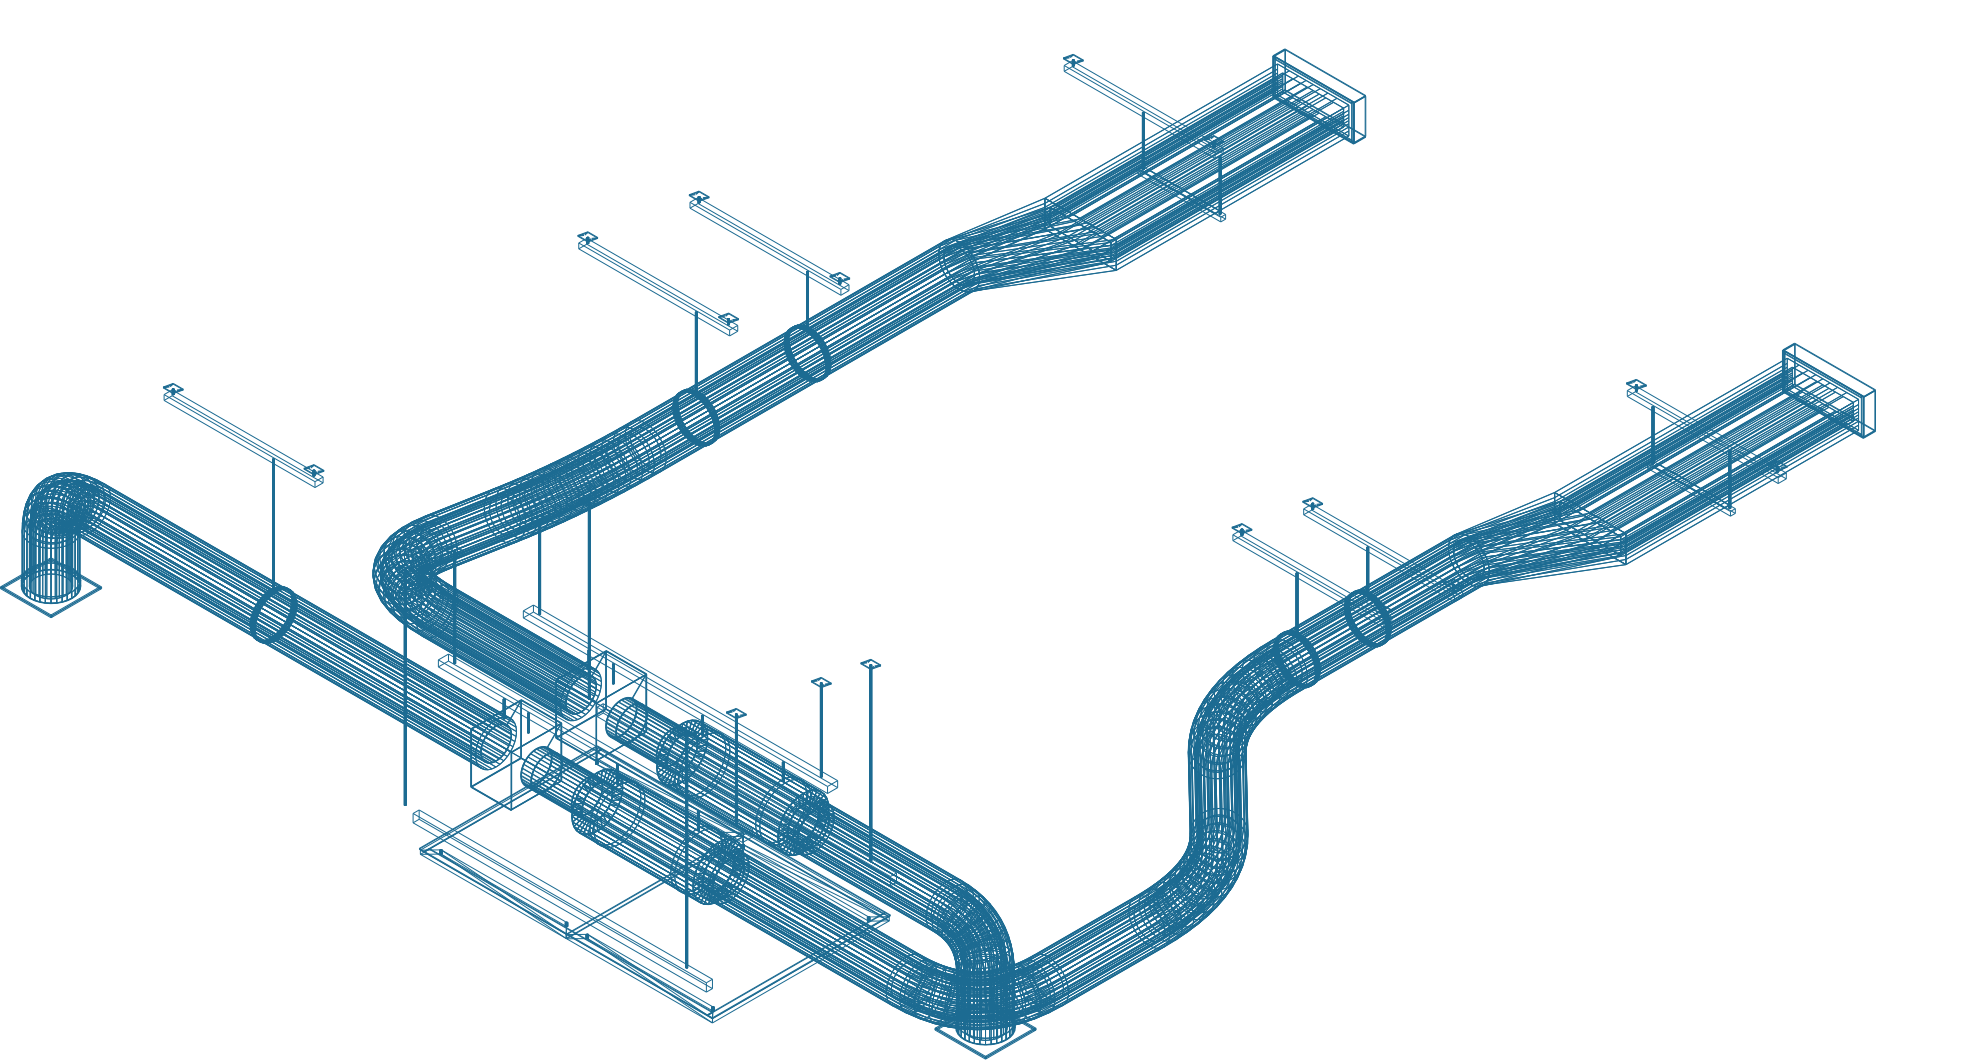

P medio auxiliar no modelado: plataforma elevadora 1200x600, tablero +4,65; cuerpo 450x1720, cabeza +6,37. Apartar mueble apoyo y 4 patas. Retirar a +5,40; trasladar sobre tablero y descender al piso. Operario cambia X segun modulo; seleccionar equipo, alcance, herramienta y capacidad.

20 Frente / corte X17,64 | 1:20

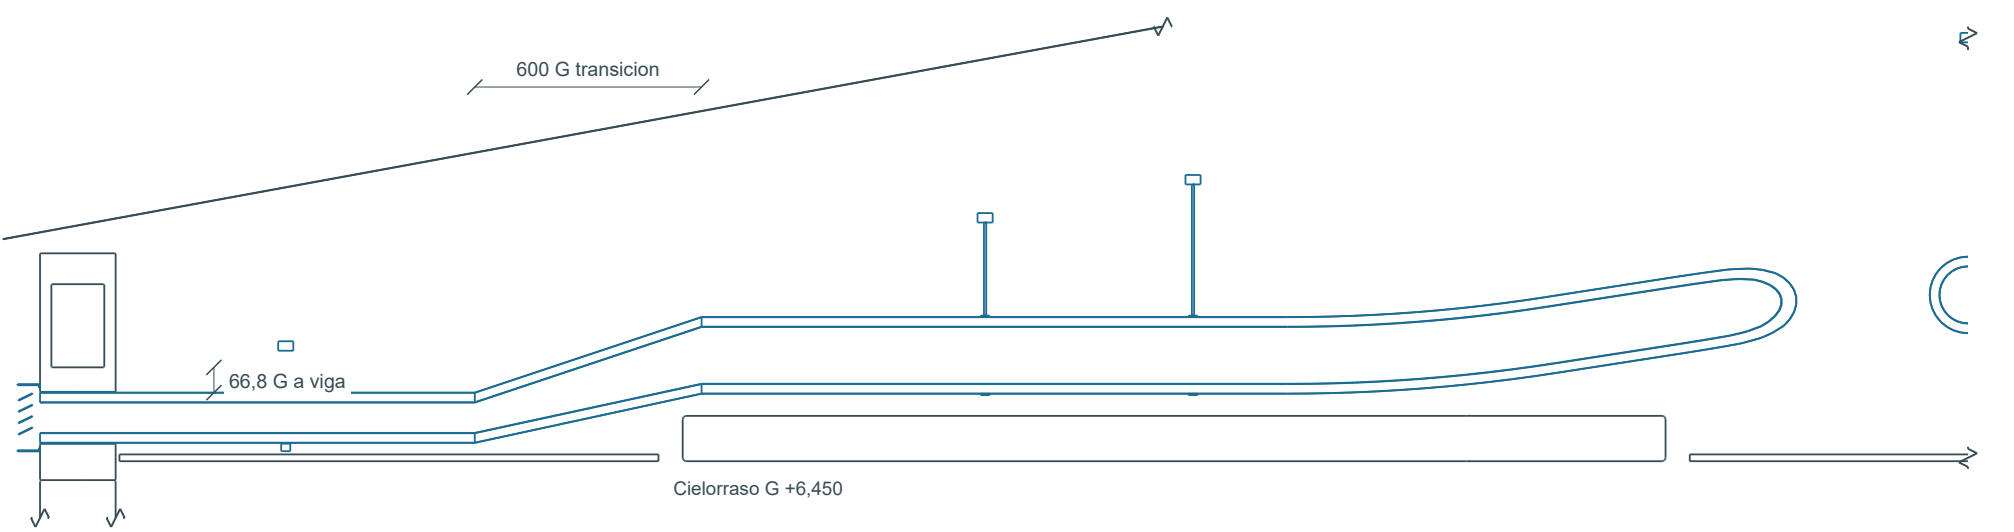


G seccion rectangular 300x80; area 0,024m2. Chapa 1 + aislacion 25 + camisa 0,5; exterior 353x133. P seleccion, caudal, ruido, condensacion y fijaciones pendientes de proyecto.

G = medido / gris

P = propuesta dimensional / azu

Todas las cotas en mm salvo niveles en m

18 Transición humedo-seco / geometría G | 1:5

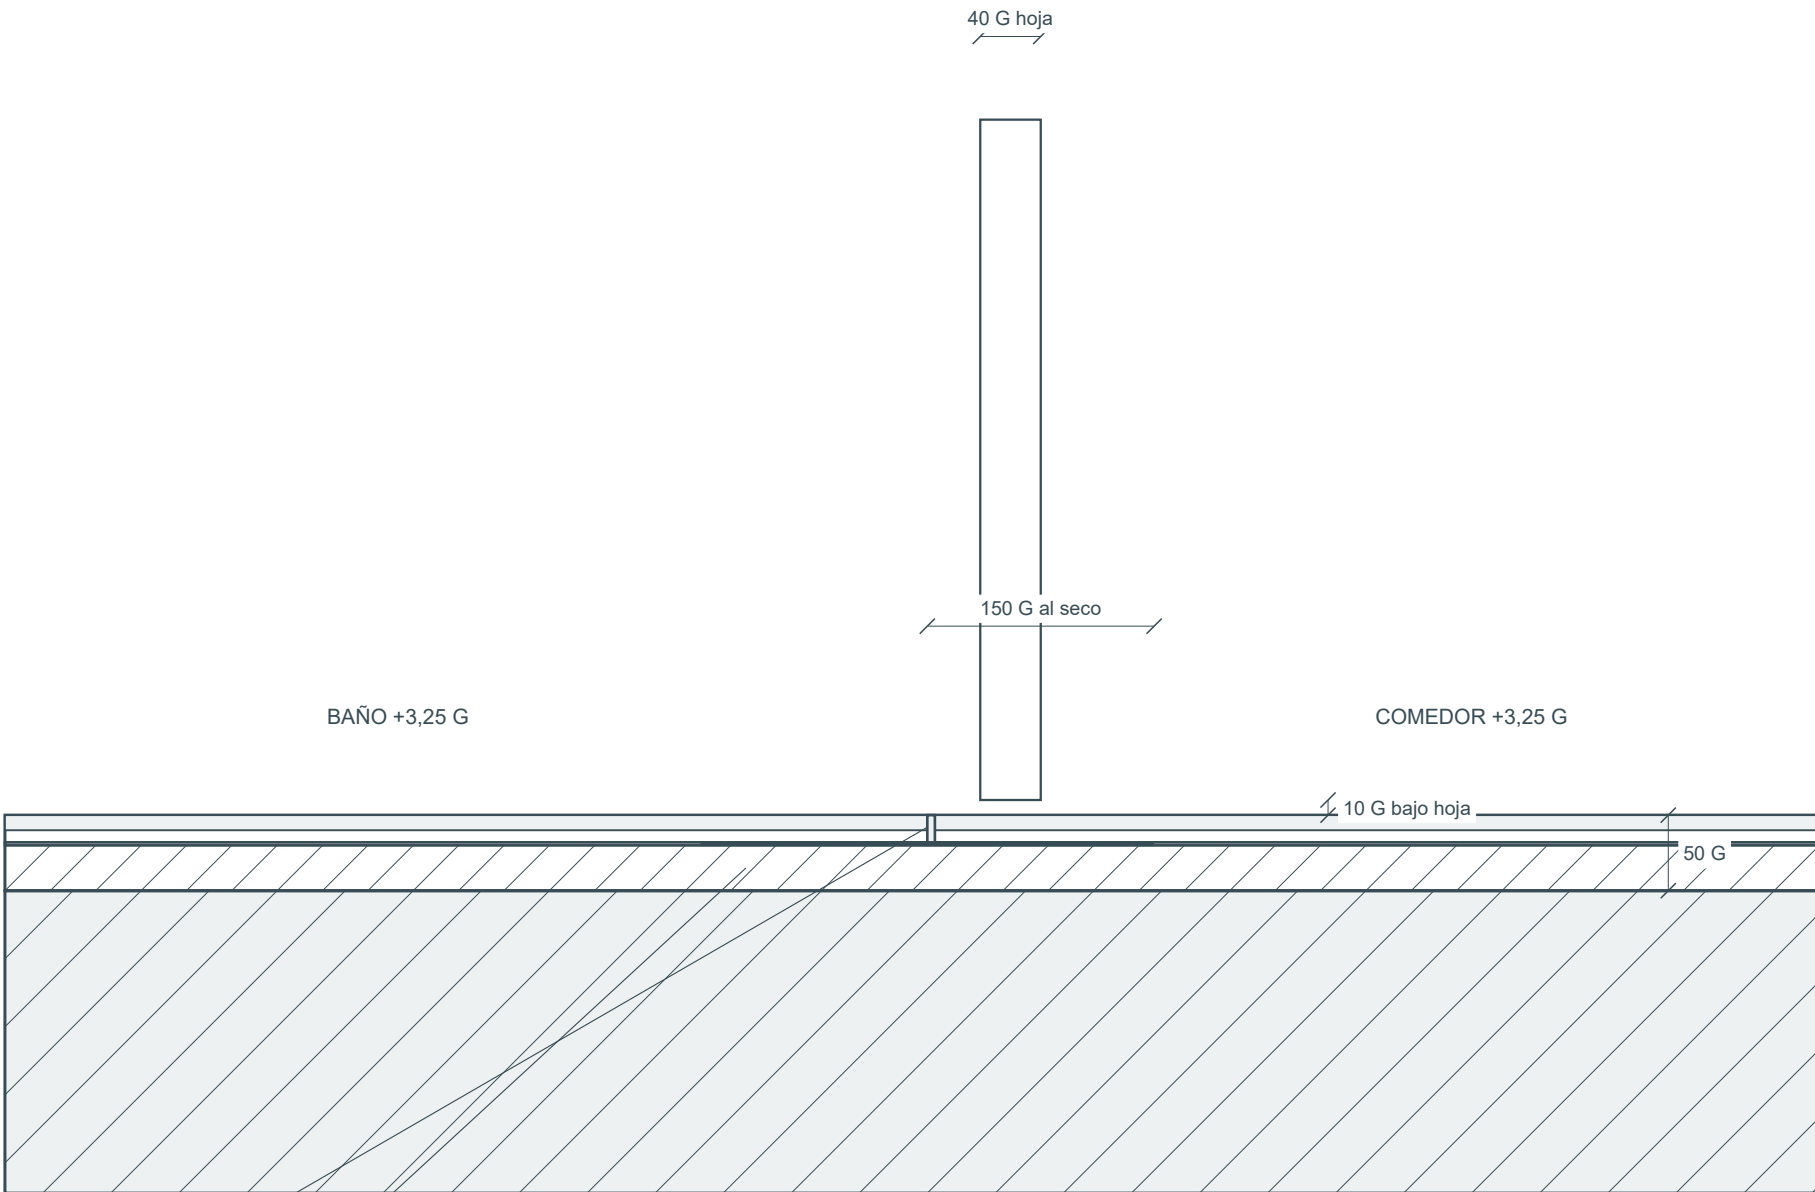


- G junta elastica5 en terminacion; banda flexible bajo baldosa, prolongacion150 al lado seco y retorno en jambas. El paso queda sin resalto


- G composicion dentro de50: mortero30 + membrana2 + adhesivo8 + baldosa10. Verificar espesores del sistema elegido y soporte: no duplicar piso general bajo la zona humeda

R5 | Hilti: Base plates - design considerations:

19 Corredera modelada / vista parcial G | 1:10

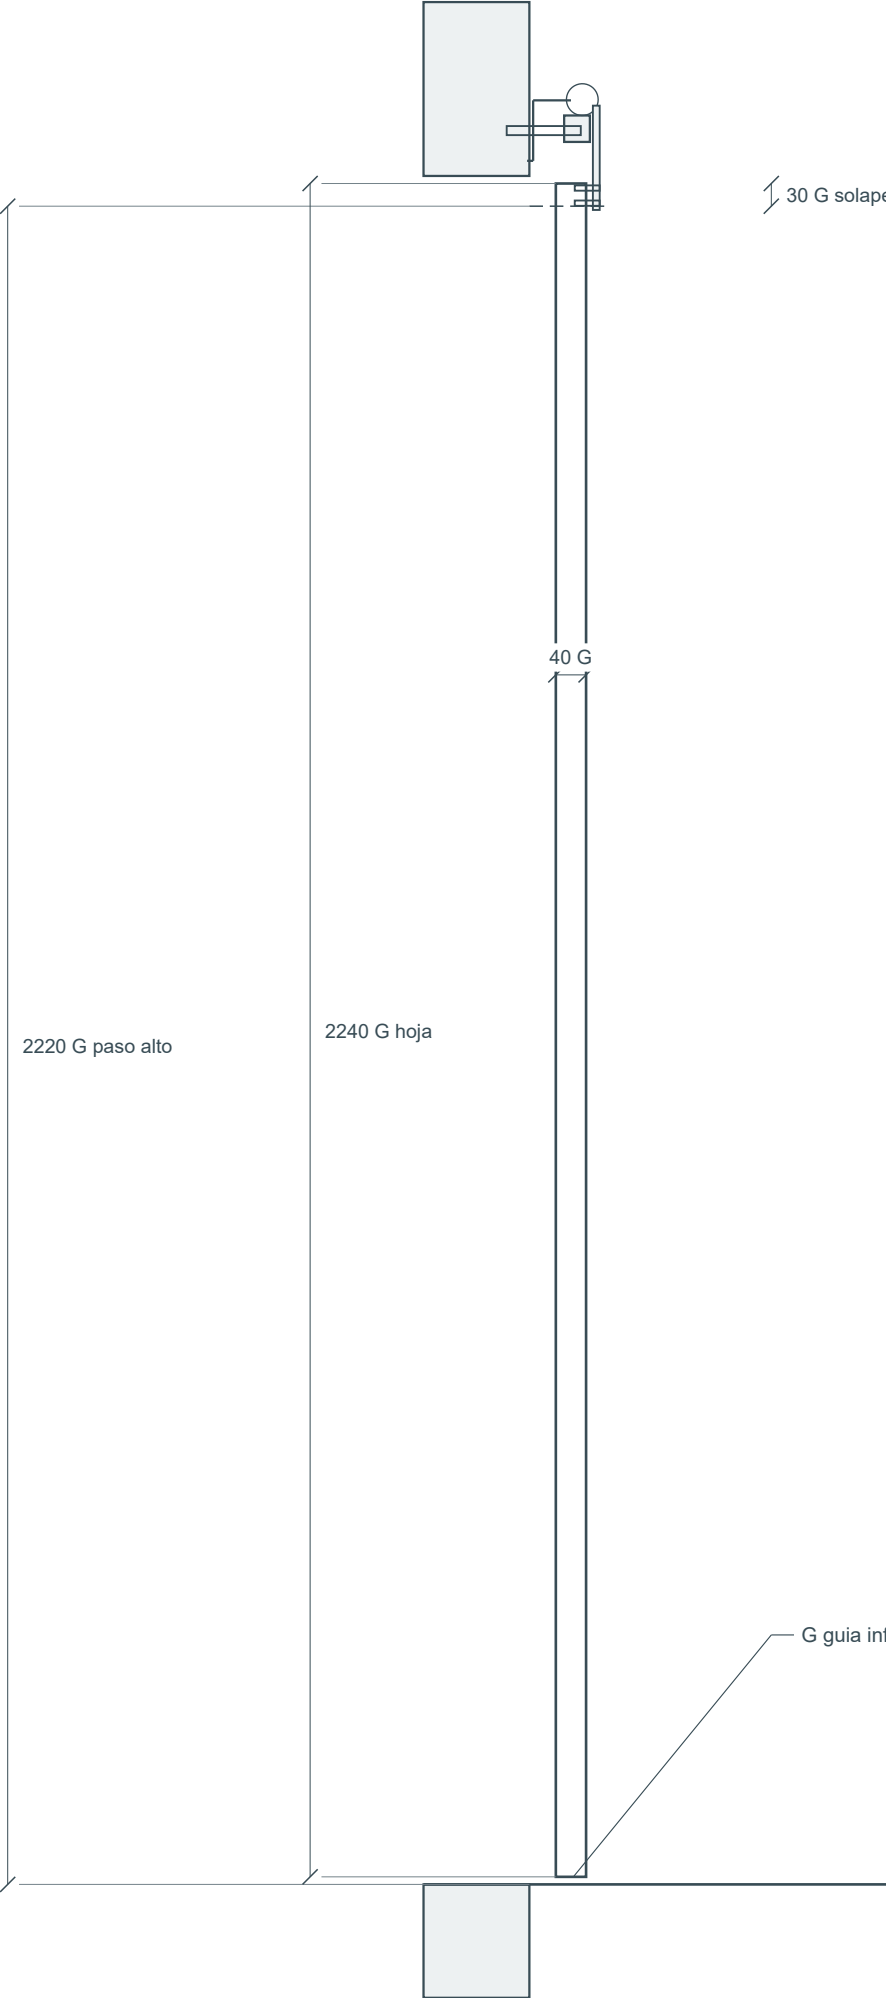

Herraje ampliado G | 1:2

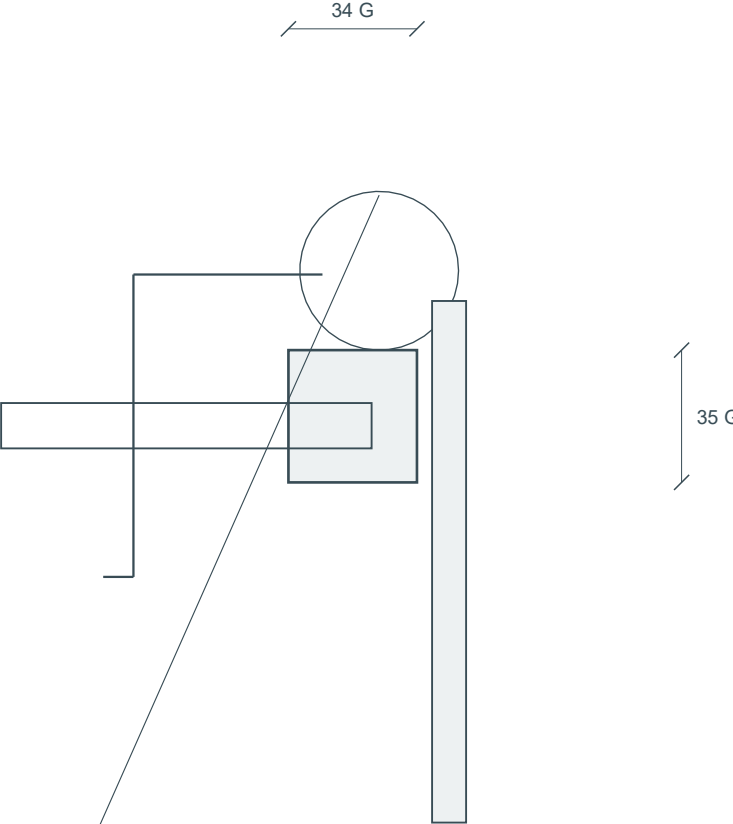

G2 ruedas Ø42 apoyan en cara superior +5.590. Pletinas 9 y pernos Ø7 vinculan carros con hoja

G guía inferior lateral fuera del paso. Tiradores embutidos en ambas caras, junto al extremo de mesada

G hoja superior+5,50; cabezal+5,47; riel+5,555..+5,590. Geometria propuesta incorporada: dimensiones no equivalen a capacidad del herraje ni certificacion de impermeabilidad

EN REVISION - PROPUESTAS DE COORDINACION, SIN CALCULO DE CAPACIDAD

Base G: Casa_de_Campo_99_R7D.blend / 9cf1a0e2f1b1a606


G acredita geometria, no capacidad. P identifica propuestas; su presencia3D no valida prestaciones

A2 / imprimir al 100 %

10 / 10-09-2026


G = medido / gris P = propuesta dimensional / azul Todas las cotas en mm salvo niveles en m

20 Rodadura / corte exacto de la geometria | 1:2

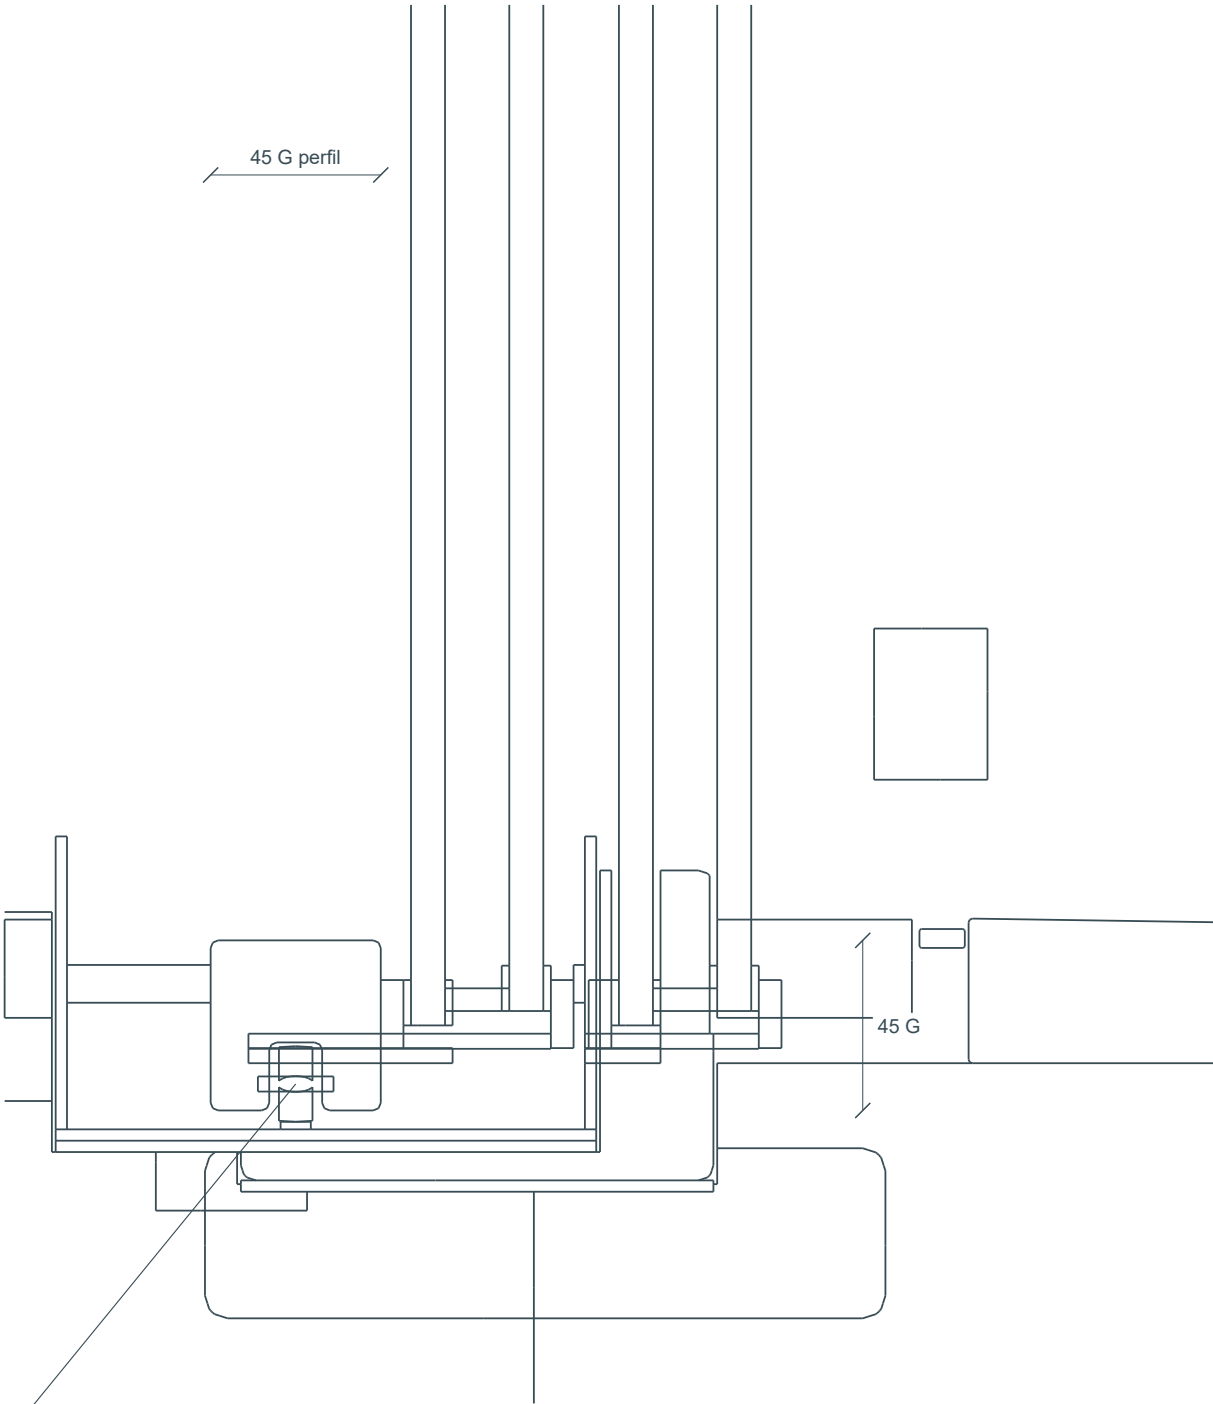


G rodilloØ20 / ejeØ4; carril8x2; bandeja3; lecho3. Alojamiento26x14x19 en perfil original. Carga, desgaste y seleccion del herraje requieren dimensionamiento.

21 Acristalamiento / corte por tacos | 1:2

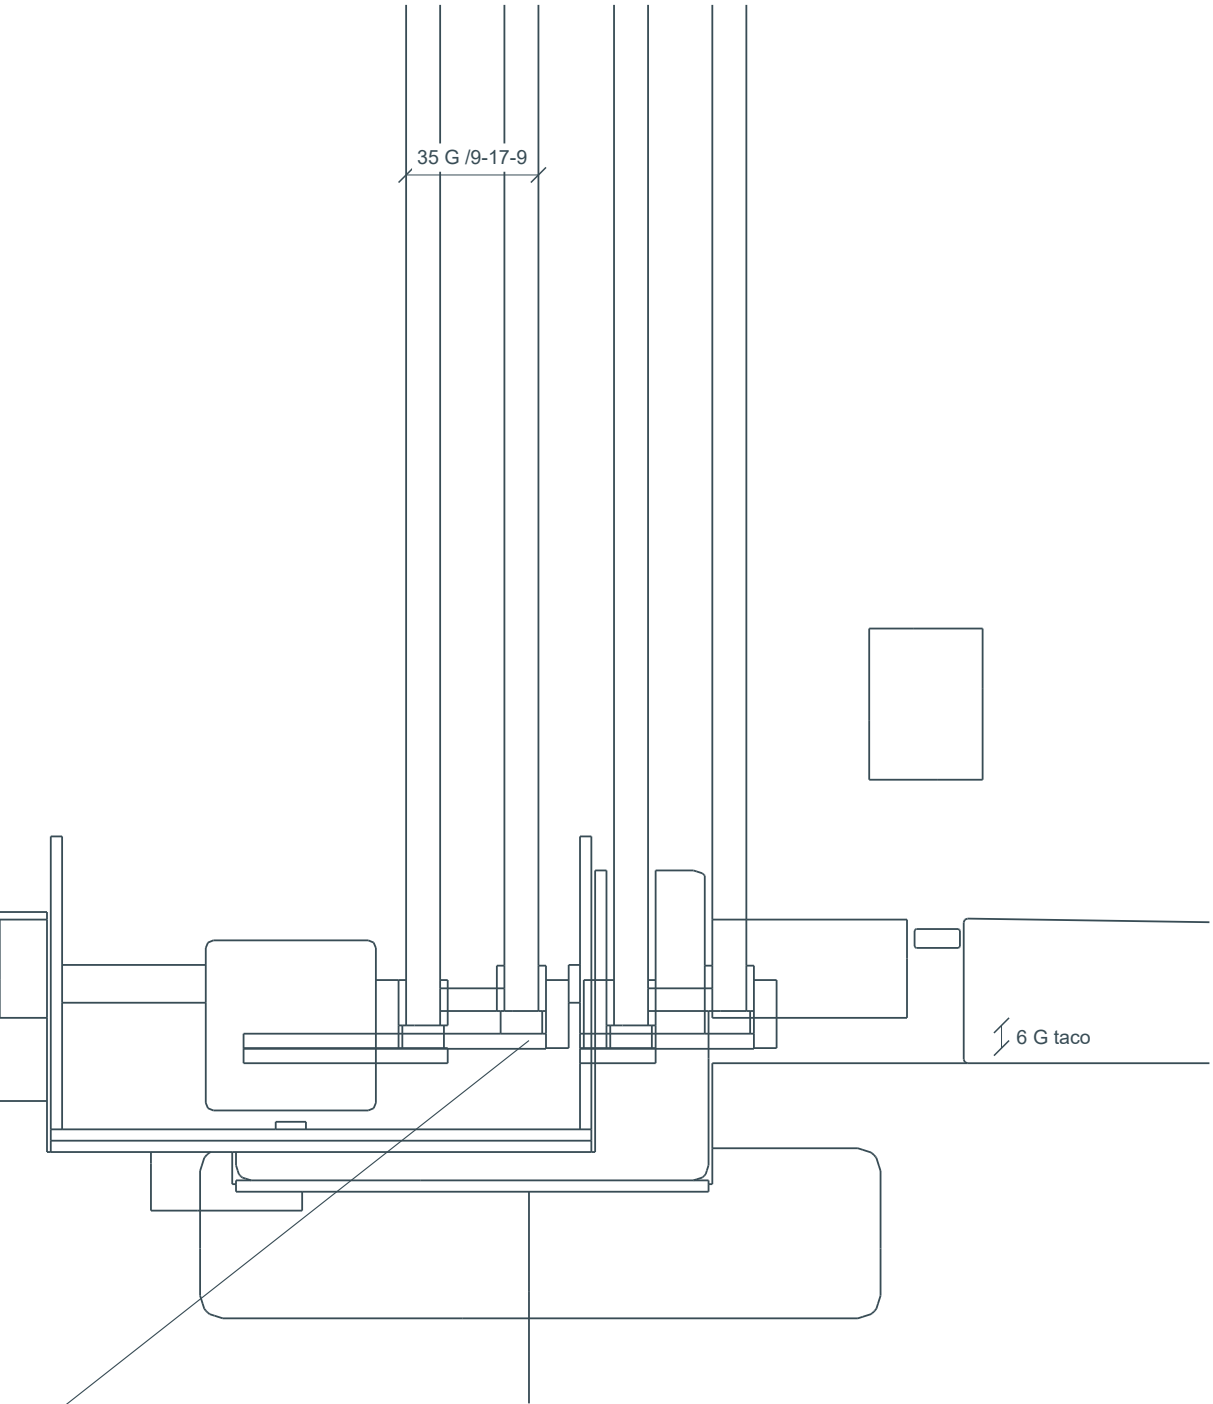


G tacos100mm en cuartos de luz;6mm de altura bajo cada vidrio. Puentes metalicos y junquillos conectan vidrio y perfiles; el vidrio interior conserva su retiro vertical3,81mm.

22 Guía superior / corte G | 1:2

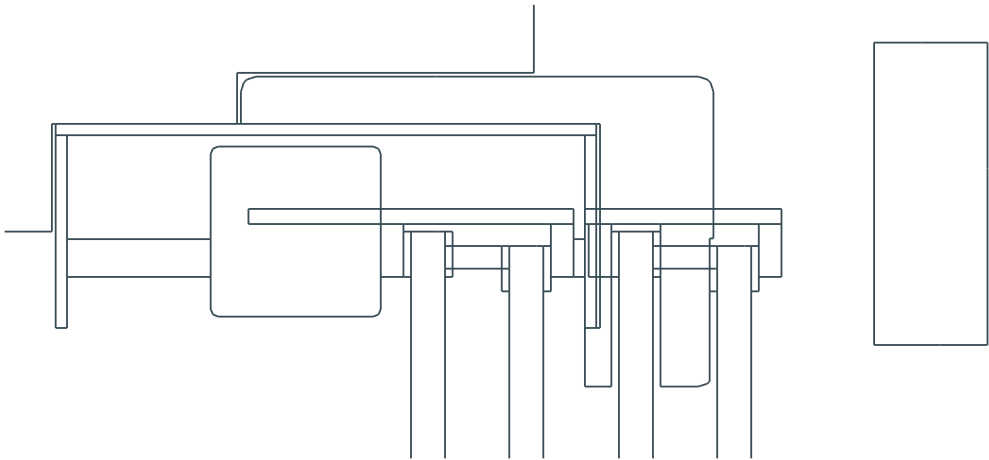

23 Drenaje al borde / corte G | 1:10

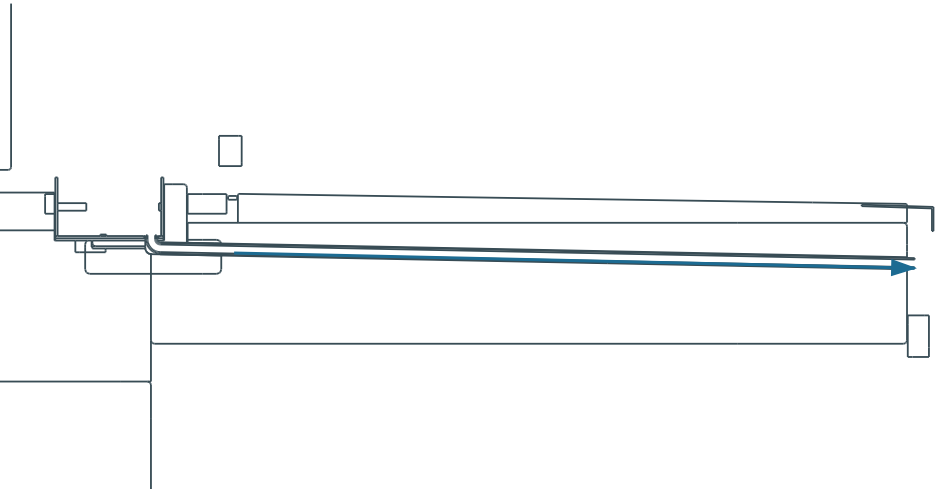

GEOMETRIA / LIMITES

G conserva13 rigs, carrera y dimensiones de vidrios. Se vaciaron galces y perfiles; no se movieron los vanos.

Holgura nominal3mm al contorno movil terminado;2mm en galce de vidrio. Felpas y EPDM son geometria propuesta, sin ensayo de estanqueidad.

Rodillos y tacos son una propuesta de montaje. No hay capacidad, durabilidad ni especificacion de producto validada.


Rebajes de losas y dinteles, y perforacionesØ16 para tubosØ14, requieren coordinacion con armado y calculo. No se declara aptitud resistente.

G = medido / gris

P = propuesta dimensional / azul


Todas las cotas en mm salvo niveles en m

24 Ducha PB / planta | 1:10

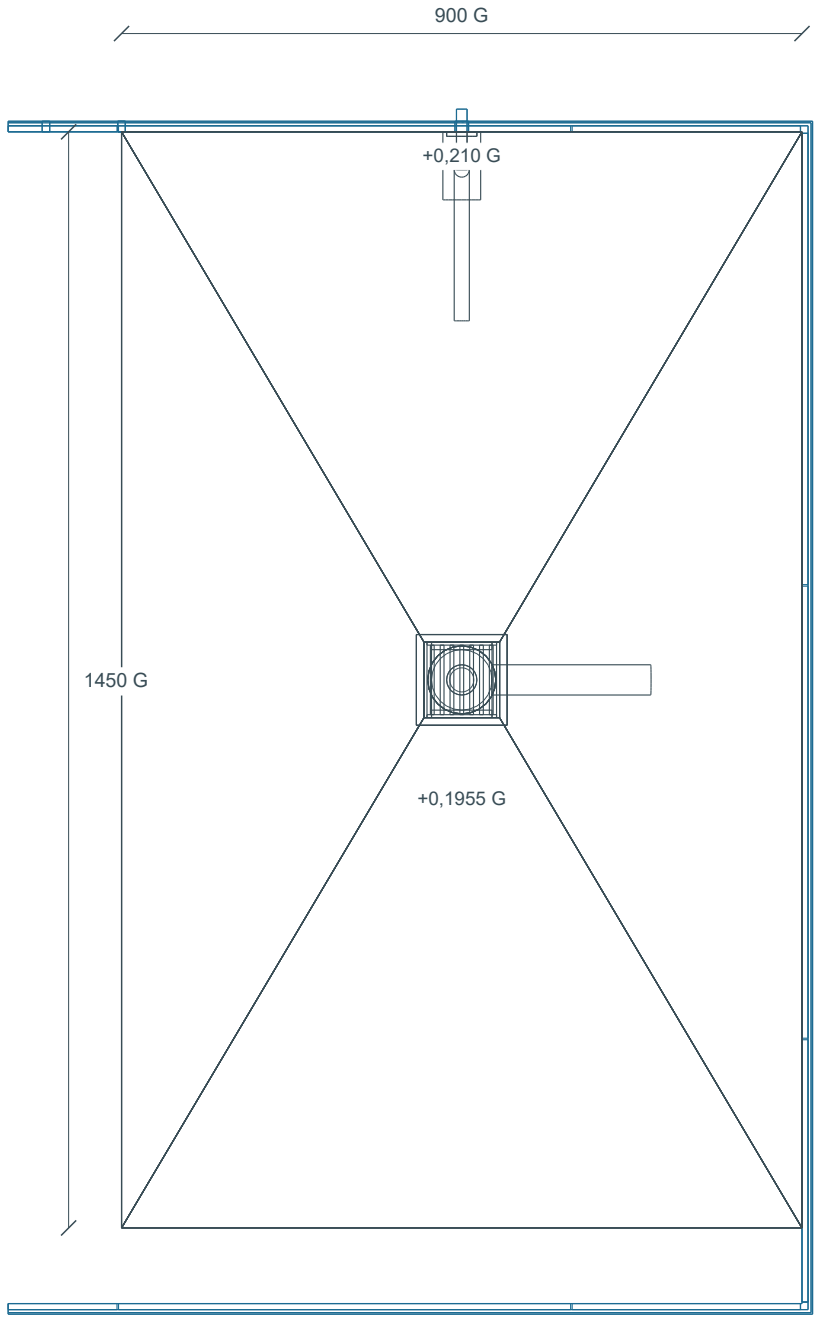


G ducha a piso: rejilla100x100 y caída14,5mm; pendientes2,15% /3,63% hasta el borde del desagüe.

24a Junta pasante / X21,35 | 1:1

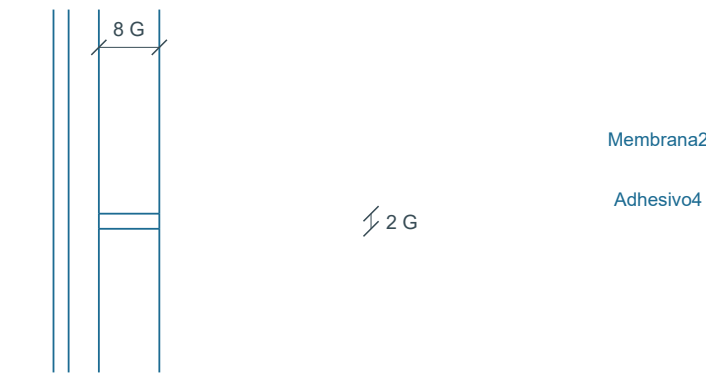


P modulo600x300; juntas2x8 y esquinas2. Compatibilidad y ensayo de estanqueidad pendientes.

25 Ducha PB / X21,35 | 1:10

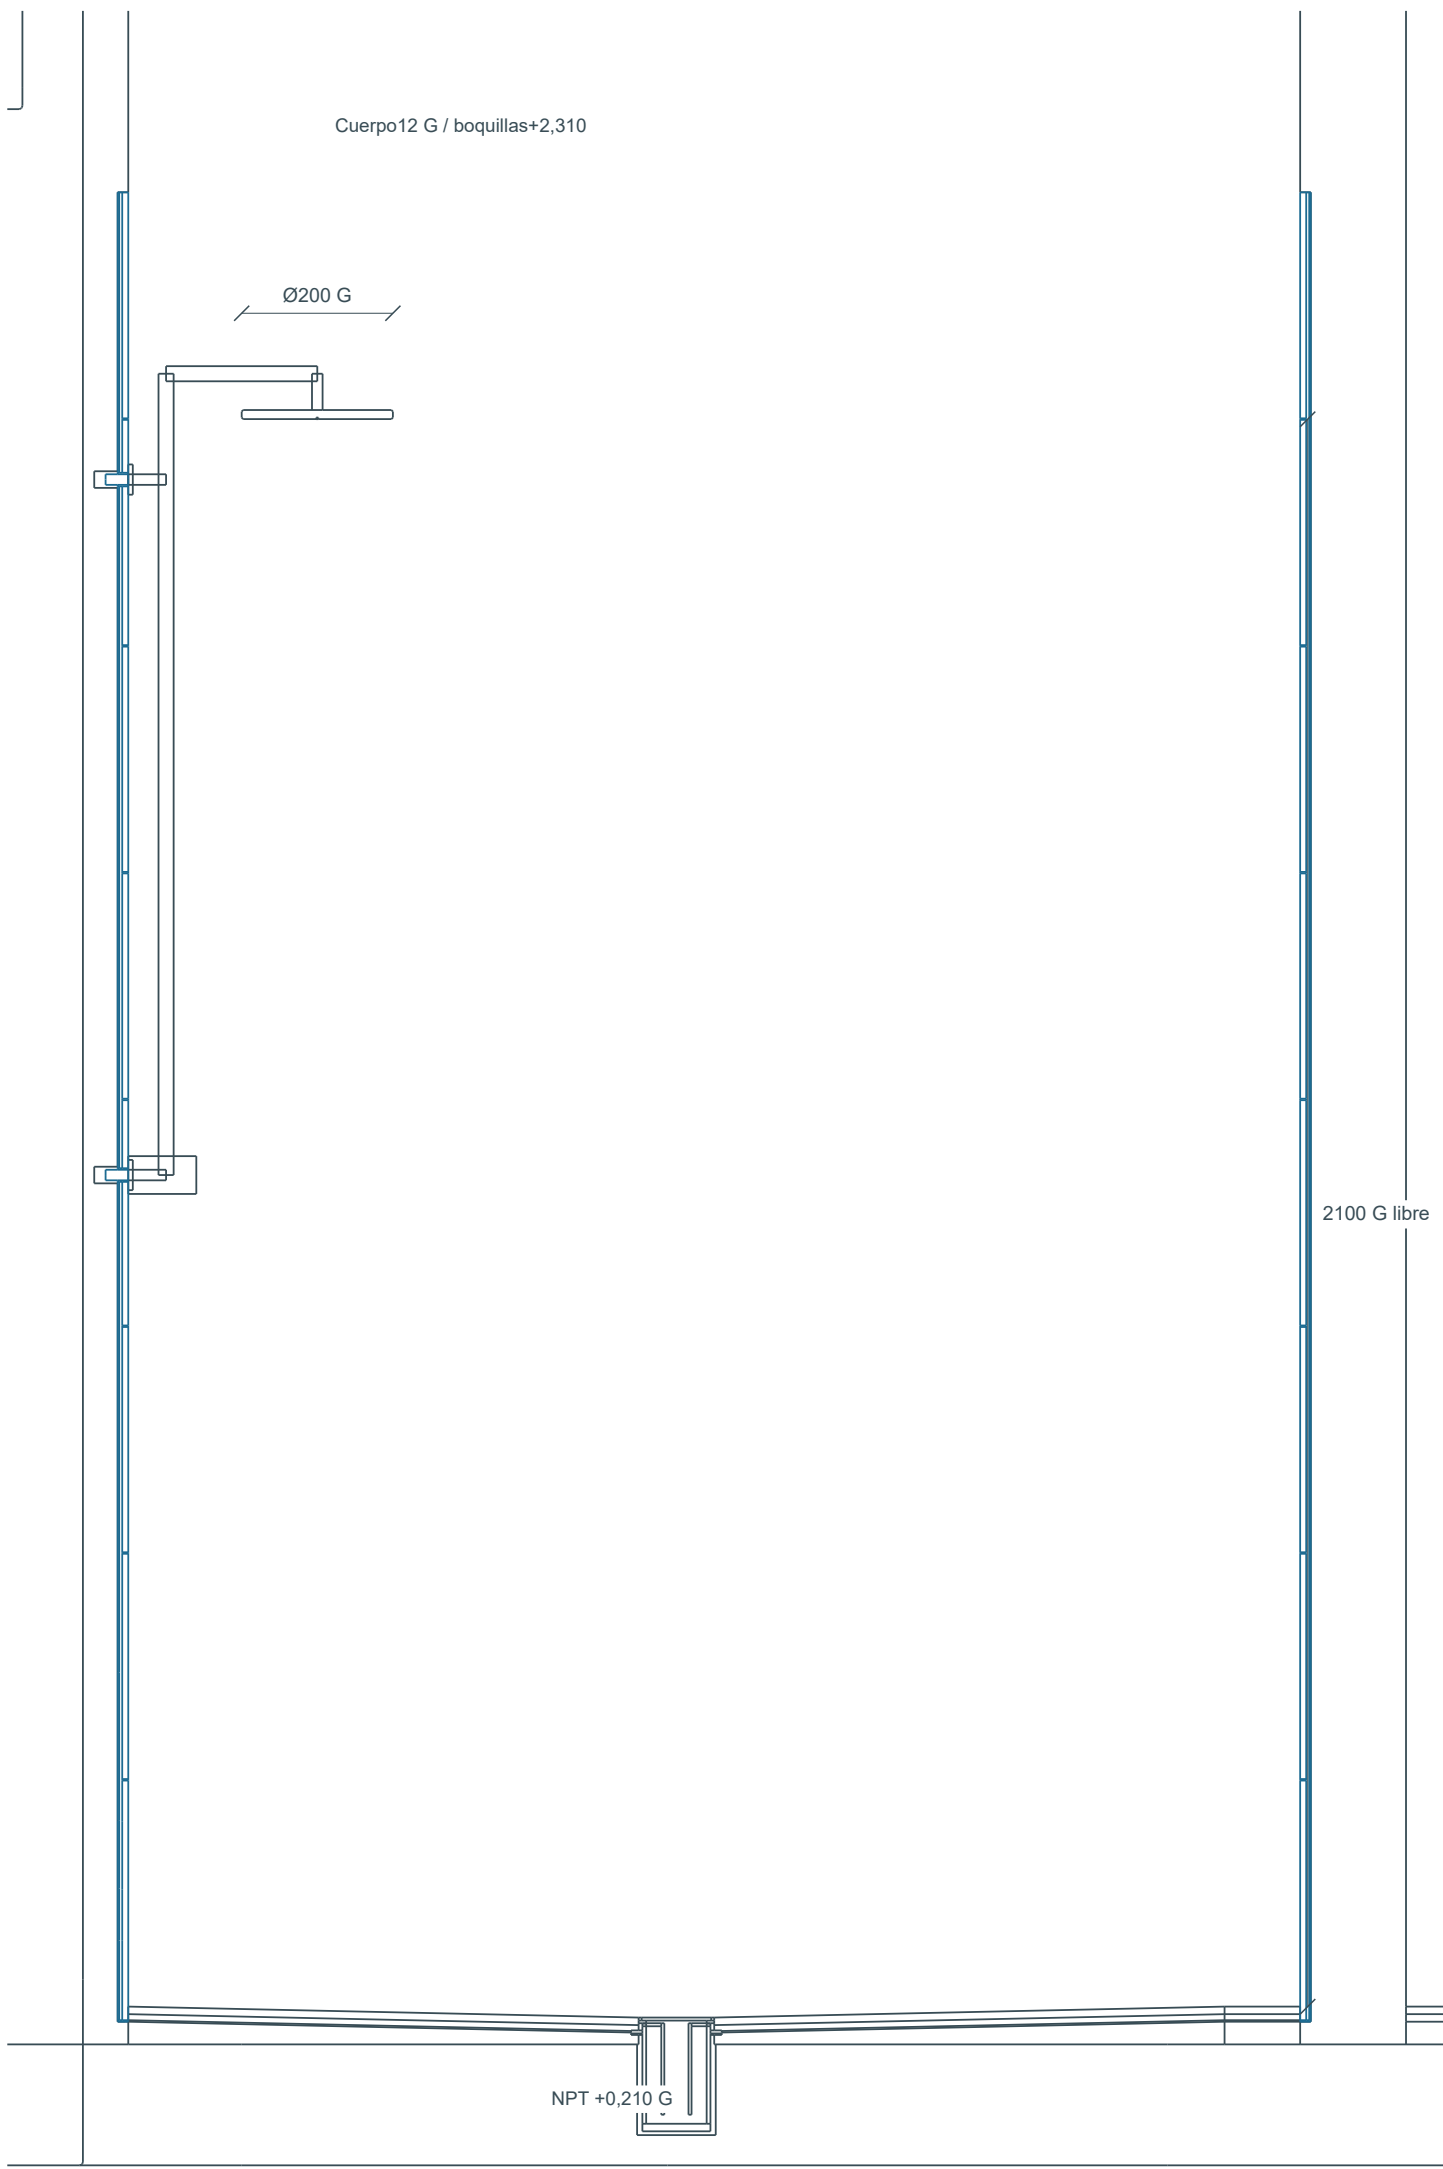


26 Griferia PA / X21,10 | 1:2

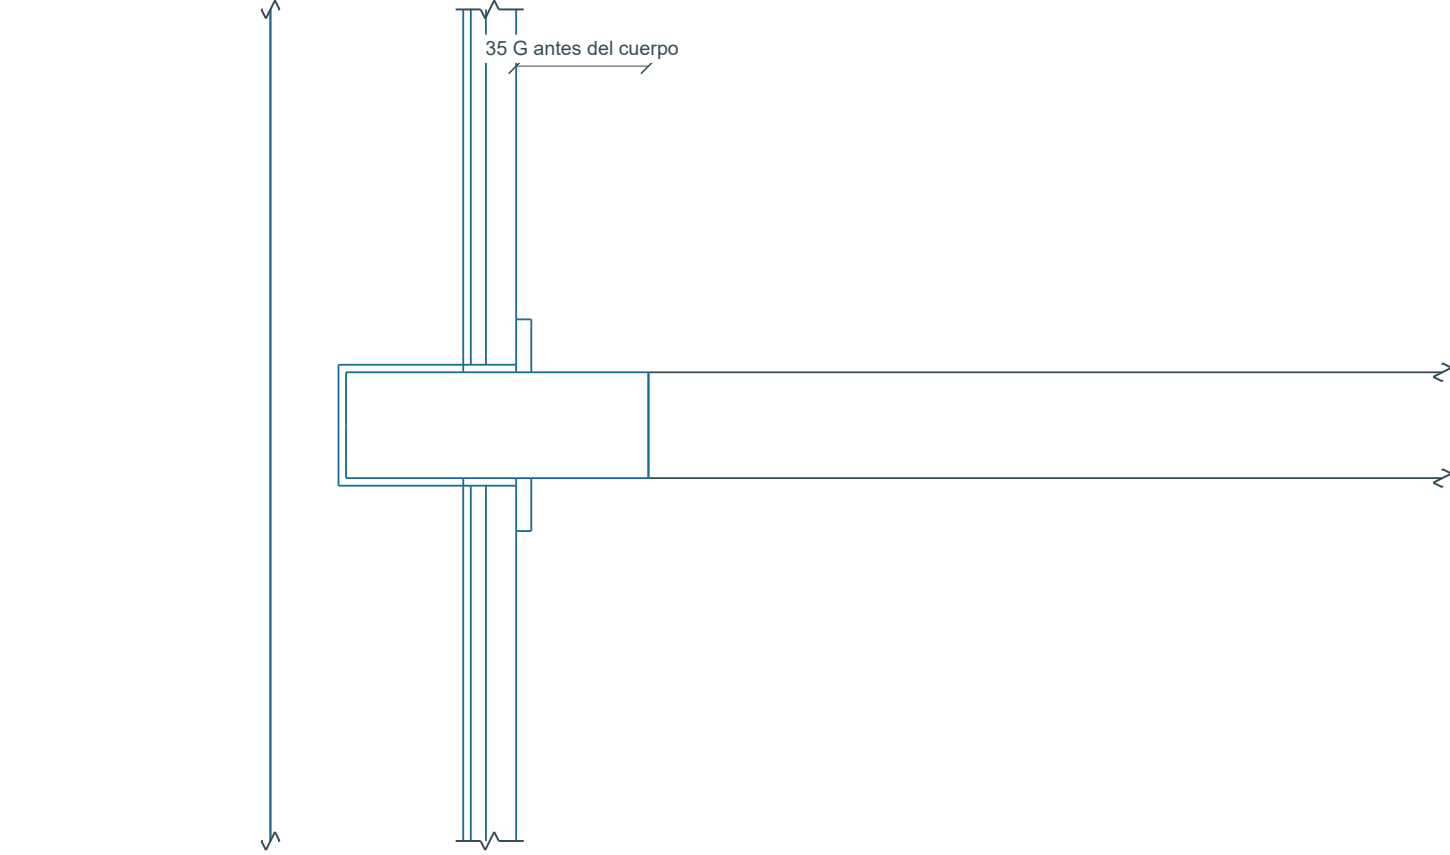

P vástago metálico hasta cuerpo empotrado, collar impermeable y roseta en cara terminada Z6,165; grifería conserva posición. Se conecta al sustrato, sin tubo flotante.

27 Piso-muro PB / Z1,40 | 1:2

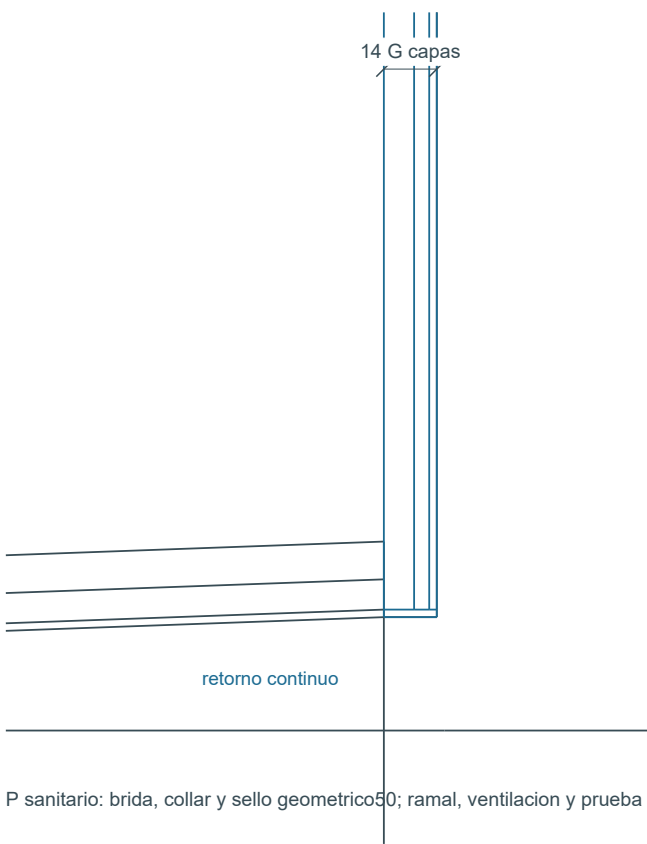

P sanitario: brida, collar y sello geométrico80; ramal, ventilación y prueba pendientes.

28 Sumidero PB / Z0,985 | 1:5

